

SUPERHELIX

Spis zmian nieistotnych według prawa budowlanego w stosunku do projektu architektoniczno-budowlanego objętego decyzją nr 171/6740.1/2023 z dnia 13 lutego 2023 r. Zmienionego decyzją nr 919/6740.1/2024 z dnia 07.10.2024 r oznaczono kolorem zielonym.

nazwa elementu projektu budowlanego **PROJEKT ARCHITEKTONICZNO-BUDOWLANY
ZAMIENNY**

tom **1 z 2**

nazwa zamierzenia budowlanego **28 BUDYNKÓW MIESZKALNYCH JEDNORODZINNYCH W
ZABUDOWIE BLIŹNIACZEJ Z 14 GARAŻAMI
ZAMKNIĘTYMI, WBUDOWANYMI ORAZ 14 GARAŻY
ZAMKNIĘTYCH, WOLNOSTOJĄCYCH, Z
ZAGOSPODAROWANIEM TERENU, SCHODAMI
ZEWNĘTRZNYMI, MURAMI OPOROWYMI,
ZEWNĘTRZNYMI STANOWISKAMI POSTOJOWYMI,
DOJŚCIEM I DOJAZDEM.**

adres obiektu budowlanego **KRAKÓW, UL. WŁADYSŁAWA ŁOKIETKA**

kategoria obiektu budowlanego **I – BUDYNKI MIESZKALNE JEDNORODZINNE
III – INNE NIEWIELKIE BUDYNKI: GARAŻE
VIII – INNE BUDOWLE: MURY OPOROWE I
SCHODY ZEWNĘTRZNE**

nazwa jednostki ewidencyjnej,
nazwa i numer obrębu ewidencyjnego,
numery działek ewidencyjnych,
na których obiekt jest usytuowany **KRAKÓW 126102_9, OBR. KROWODRZA 0033,
773, 774, 775**

imię i nazwisko lub nazwa inwestora **HAMMAK ŁOKIETKA SP. Z O. O.**

adres inwestora **UL. ARMII KRAJOWEJ 25, 30-150 KRAKÓW**

autor projektu		data opracowania SIERPIEŃ 2024	podpis
imię i nazwisko	BARTŁOMIEJ DRABIK		
specjalność	ARCHITEKTONICZNA DO PROJEKTOWANIA BEZ OGRAŃCZEŃ		
numer uprawnień	MPOIA/077/2013		
zakres opracowania	ARCHITEKTURA		
funkcja	PROJEKTANT		

SPIS TREŚCI

I. DOKUMENTY DOŁĄCZONE DO PROJEKTU.....	4
1. Kopia decyzji o nadaniu projektantowi uprawnień budowlanych w odpowiedniej specjalności.....	4
2. Kopia zaświadczenia o wpisie na listę członków właściwej izby samorządu zawodowego.....	5
3. Oświadczenie projektanta o sporządzeniu projektu zgodnie z obowiązującymi przepisami i zasadami wiedzy technicznej.....	6
II. CZĘŚĆ OPISOWA.....	7
1. Rodzaj i kategoria obiektu budowlanego będącego przedmiotem zamierzenia budowlanego.....	7
2. Zamierzony sposób użytkowania oraz program użytkowy obiektu budowlanego.....	10
3. Układ przestrzenny oraz forma architektoniczna obiektu budowlanego, w tym jego wygląd zewnętrzny, uwzględniając charakterystyczne wyroby wykończeniowe i kolorystykę elewacji, a także sposób jego dostosowania do warunków wynikających z wymaganych przepisów i szczególnymi pozwoleniami, uzgodnień lub opinii innych organów.....	10
4. Charakterystyczne parametry obiektu budowlanego.....	11
a. Kubatura:.....	11
b. Zestawienie powierzchni:.....	13
c. Wysokość, długość, szerokość, średnica.....	16
d. Liczba kondygnacji.....	16
e. Inne dane niezbędne do stwierdzenia zgodności usytuowania obiektu z wymaganiami ochrony przeciwpożarowej.....	17
5. Opinia geotechniczna oraz informację o sposobie posadowienia obiektu budowlanego.....	17
6. Liczba lokali mieszkalnych i użytkowych.....	17
7. Liczba lokali mieszkalnych dostępnych dla osób niepełnosprawnych.....	17
8. Opis zapewnienia niezbędnych warunków do korzystania z obiektów użyteczności publicznej i mieszkaniowego budownictwa wielorodzinnego przez osoby niepełnosprawne.....	17
9. Parametry techniczne obiektu budowlanego charakteryzujące wpływ obiektu budowlanego na środowisko i jego wykorzystywanie oraz na zdrowie ludzi i obiekty sąsiednie.....	17
a. Zapotrzebowanie i jakości wody oraz ilości, jakości i sposobu odprowadzania ścieków oraz wód opadowych.....	17
b. Emisja zanieczyszczeń gazowych, w tym zapachów, pyłowych i płynnych, z podaniem ich rodzaju, ilości i zasięgu rozprzestrzeniania się.....	18
c. Rodzaju i ilości wytwarzanych odpadów.....	18
d. Właściwości akustyczne oraz emisja drgań, a także promieniowania, w szczególności jonizującego, pola elektromagnetycznego i innych zakłóceń, z podaniem odpowiednich parametrów tych czynników i zasięgu ich rozprzestrzeniania się.....	18
e. Wpływ obiektu budowlanego na istniejący drzewostan, powierzchnię ziemi, w tym glebę, wody powierzchniowe i podziemne.....	18
10. Analiza technicznych, środowiskowych i ekonomicznych możliwości realizacji wysoce wydajnych systemów alternatywnych zaopatrzenia w energię i ciepło.....	19
a. Oszacowanie rocznego zapotrzebowania na energię użytkową do ogrzewania, wentylacji, przygotowania ciepłej wody użytkowej.....	19
b. Dostępne nośniki energii.....	19
c. Wybór dwóch systemów zaopatrzenia w energię do analizy porównawczej.....	19
d. Obliczenia optymalizacyjno-porównawcze dla wybranych systemów zaopatrzenia w energię.....	19
e. Wyniki analizy porównawczej i wybór systemu zaopatrzenia w energię.....	19
11. Analiza technicznych i ekonomicznych możliwości wykorzystania urządzeń, które automatycznie regulują temperaturę oddzielnie w poszczególnych pomieszczeniach lub w wyznaczonej strefie ogrzewanej.....	20
12. Informacje o zasadniczych elementach wyposażenia budowlano-instalacyjnego, zapewniających	

użytkowanie obiektu budowlanego zgodnie z przeznaczeniem.	20
13. Dane dotyczące warunków ochrony przeciwpożarowej, stosownie do zakresu projektu.	20
14. Zestawienie warstw przegród budowlanych.	21
15. Opis technologii systemu tarasu i stropodachu zielonego (biologicznie czynnego)	28

III.CZĘŚĆ RYSUNKOWA

NR RYSUNKU A.01-14

1. Rzuty budynków A1, A2	A.01
2. Rzuty budynków A3, A4	A.02
3. Rzuty budynków A5, A6	A.03
4. Rzuty budynków A7, A8	A.04
5. Rzuty budynków A9, A10	A.05
6. Rzuty budynków A11, A12	A.06
7. Rzuty budynków A13, A14	A.07
8. Rzuty budynków B1, C1, B2, C2	A.08
9. Rzuty budynków B3, C3, B4, C4	A.09
10. Rzuty budynków B5, C5, B6, C6	A.10
11. Rzuty budynków B7, C7, B8, C8	A.11
12. Rzuty budynków B9, C9, B10, C10	A.12
13. Rzuty budynków B11, C11, B12, C12	A.13
14. Rzuty budynków B13, C13, B14, C14	A.14

Dalszy ciąg rysunków o numerach A.15-42 umieszczono w tomie nr 2.

I. DOKUMENTY DOŁĄCZONE DO PROJEKTU.

1. Kopia decyzji o nadaniu projektantowi uprawnień budowlanych w odpowiedniej specjalności.



Kraków, dnia 30.12.2013 r.
Znak sprawy: OKK/Upb/123/13/MP

DECYZJA nr MPOIA/077/2013

Na podstawie art. 12 ust. 1 pkt 1, ust. 2 i 3, art. 13 ust. pkt 1 i ust. 4 ustawy z dnia 7 lipca 1994 r. - Prawo budowlane (tekst jednolity z 2010 r. Dz.U. Nr 243, poz. 1623 z późn. zm.), art. 11 i 24 ust. 1 pkt 2 ustawy z dnia 15 grudnia 2000 r. o samorządach zawodowych architektów, inżynierów budownictwa oraz urbanistów (Dz.U. z 2001 r. Nr 5, poz. 42 z późn. zm.), § 11 ust. 1 pkt 1 rozporządzenia Ministra Transportu i Budownictwa z dnia 28 kwietnia 2006 r. w sprawie samodzielnych funkcji technicznych w budownictwie (Dz.U. z 2006 r. Nr 83, poz. 578 z późn. zm.) oraz art. 104 i 107 § 1 i 4 ustawy z dnia 14 czerwca 1960 r. - Kodeks postępowania administracyjnego (tekst jednolity: Dz.U. z 2013 r. Nr 267)

stwierdza się, że

Pan

mgr inż. arch. Bartłomiej Drabik
urodzony w dniu 28 września 1985 r., w Krakowie

posiada odpowiednie wykształcenie techniczne i praktykę zawodową
i po zdaniu egzaminu z wynikiem pozytywnym otrzymuje

UPRAWNIENIA BUDOWLANE

w specjalności architektonicznej do projektowania bez ograniczeń

Decyzja niniejsza jako uwzględniająca w całości żądanie strony nie wymaga uzasadnienia.

Od decyzji przysługuje Panu odwołanie do Krajowej Komisji Kwalifikacyjnej Izby Architektów RP. Odwołanie wnosi się za pośrednictwem organu, który wydał decyzję tj. Okręgowej Komisji Kwalifikacyjnej Małopolskiej Okręgowej Izby Architektów RP, w terminie 14 dni od dnia doręczenia decyzji.


mgr inż. arch. Witold Szorc, Przewodniczący OKK

mgr inż. arch. Maria Kowalczyk, V-ce Przewodnicząca OKK

mgr inż. arch. Maria Janik, Sekretarz OKK

mgr inż. arch. Jerzy Głodkiewicz, Członek OKK

mgr inż. arch. Jan Skąpski, Członek OKK

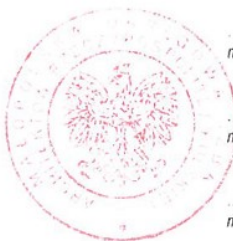

mgr inż. arch. Ryszard Piotr Szymański, Członek OKK

mgr inż. arch. Marek Tarko, Członek OKK

mgr inż. arch. Artur Trzępka, Członek OKK

mgr inż. arch. Jolanta Wąsik, Członek OKK

Otrzymują:

1. Bartłomiej Drabik, zam. ul. Szafrana 4/28, 30-401 Kraków
2. Gdy decyzja stanie się ostateczna:
 - 1) Główny Inspektor Nadzoru Budowlanego - w celu wpisania do centralnego rejestru osób posiadających uprawnienia budowlane,
 - 2) Małopolska Okręgowa Izba Architektów RP.
3. a/a



IZBA ARCHITEKTÓW
RZECZYPOSPOLITEJ POLSKIEJ

Małopolska Okręgowa Rada Izby Architektów RP

ZAŚWIADCZENIE - ORYGINAŁ

(wypis z listy architektów)

Małopolska Okręgowa Rada Izby Architektów RP zaświadcza, że:

mgr inż. arch. BARTŁOMIEJ DRABIK

posiadający kwalifikacje zawodowe do pełnienia samodzielnych funkcji technicznych w budownictwie w specjalności architektonicznej i w zakresie posiadanych uprawnień nr **MPOIA/077/2013**, jest wpisany na listę członków Małopolskiej Okręgowej Izby Architektów RP pod numerem: **MP-2012**.

Członek czynny od: 29-10-2014 r.

Data i miejsce wygenerowania zaświadczenia: 19-03-2024 r. Kraków.

Zaświadczenie jest ważne do dnia: **30-06-2025 r.**

Podpisano elektronicznie w systemie informatycznym Izby Architektów RP przez:
Grzegorz Lechowicz, Sekretarz Okręgowej Rady Izby Architektów RP.

Nr weryfikacyjny zaświadczenia:

MP-2012-BAD6-33Y5-33FE-A997

Dane zawarte w niniejszym zaświadczeniu można sprawdzić podając nr weryfikacyjny zaświadczenia w publicznym serwisie internetowym Izby Architektów: www.izbaarchitektow.pl lub kontaktując się bezpośrednio z właściwą Okręgową Izbą Architektów RP.

3. Oświadczenie projektanta o sporządzeniu projektu zgodnie z obowiązującymi przepisami i zasadami wiedzy technicznej.

Oświadczam, że projekt architektoniczno-budowlany zamienny dla inwestycji pod nazwą:

„28 budynków mieszkalnych jednorodzinnych w zabudowie bliźniaczej z 14 garażami zamkniętymi, wbudowanymi oraz 14 garaży zamkniętych, wolnostojących, z zagospodarowaniem terenu, schodami zewnętrznymi, murami oporowymi, zewnętrznymi stanowiskami postojowymi, dojściem i dojazdem na dz. Nr 773, 774 i 775 obr. 0033 Krowodrza w Krakowie”

został sporządzony zgodnie z obowiązującymi przepisami i zasadami wiedzy technicznej.

autor projektu architektoniczno-budowlanego	
imię i nazwisko	BARTŁOMIEJ DRABIK
numer uprawnień	MP0IA/077/2013

Bartłomiej Drabik

II. CZĘŚĆ OPISOWA.

Projekt ten jest projektem zamiennym w stosunku do projektu pierwotnego objętego decyzją Prezydenta Miasta Krakowa o numerze 171/6740.1/2023 z dnia 13 lutego 2023.

1. Rodzaj i kategoria obiektu budowlanego będącego przedmiotem zamierzenia budowlanego.

Rodzaj i kategoria obiektu budowlanego nie uległa zmianie względem projektu pierwotnego objętego decyzją Prezydenta Miasta Krakowa o numerze 171/6740.1/2023 z dnia 13 lutego 2023. Dla uczynienia zmian nanoszonych w projekcie wszystkie zmiany zostały oznaczone kolorem zależnym od kategorii tej zmiany:

- Kolorem fioletowym zostały oznaczone zmiany zakwalifikowane jako istotne w rozumieniu przepisów prawa budowlanego:

W budynkach A.1-A.14:

- Ist.1. Zmiana zamierzonego sposobu użytkowania części stropodachu budynku - przesunięcie barierki na dachu budynku skutkujące zwiększeniem powierzchni tarasu.
- Ist.2. Wydzielenie pomieszczenia i zmiana antresoli na II. kondygnację budynku, skutkująca także zwiększeniem powierzchni całkowitej, bez zmian gabarytu zewnętrznego budynku.

W budynkach B.1-B.6, B9, B10, B13, B14:

- Ist.1. Zmiana zamierzonego sposobu użytkowania części stropodachu budynku - przesunięcie barierki na dachu budynku skutkujące zwiększeniem powierzchni tarasu.
- Ist.2. Wydzielenie pomieszczenia i zmiana antresoli na III. kondygnację budynku, skutkująca także zwiększeniem powierzchni całkowitej, bez zmian gabarytu zewnętrznego budynku.
- Ist.3. Likwidacja otworu w stropie (związana ze zmianą antresoli na III. kondygnację).

W budynkach B7, B.8, B11, B12, C1-C14:

- Ist.1. Zmiana zamierzonego sposobu użytkowania części dachu budynku - przesunięcie barierki na dachu budynku skutkujące zwiększeniem powierzchni tarasu.

Powyższe zmiany, zostały oznaczone na rysunkach, zgodnie z przedstawioną numeracją. W opisie technicznym, zmiany wynikające pośrednio i bezpośrednio z tych zmian (np. zmiana powierzchni, kubatury) także zostały oznaczone kolorem fioletowym.

- Kolorem niebieskim zostały oznaczone zmiany zakwalifikowane jako nieistotne w rozumieniu przepisów prawa budowlanego:

W budynkach A.1-A.14:

1. Zmiana grubości ściany w osi A.3. (skutkuje zmniejszeniem powierzchni A.2.g, A.3.g).
2. Zmiana grubości ściany (skutkuje zmianą powierzchni A.2.1, A.2.5, A.2.8, A.2.9, A.2.10, A.2.12, A.1.1, A.1.6).
3. Zmiana wielkości otworu w ścianie.
4. Przesunięcie otworu.
5. Zmiana warstw przegrody (usunięcie tynku wew.).
6. Zmiana spadku posadzki garażu i struktury warstwowej.
7. Zmiana wielkości słupa (skutkuje zmianą powierzchni A.2.3).
8. Dodatkowy słup (skutkuje zmianą powierzchni A.1.5).
9. Przesunięcie przebiecia.
10. Zmiana wysokości osi przebiecia.
11. Zmiana grubości konstrukcji stropu.
12. Obniżenie nadproża.

13. Przesunięcie bramy garażowej.
14. Zmiana dojścia/dojazdu.
15. Zmiana warstw przegrody.
16. Zmiany fundamentów zgodnie z projektem technicznym konstrukcji.
17. Usunięcie okna przy drzwiach.
18. Okno stałe zamiast przesuwne.
19. Zmiana aranżacji pom. technicznego.
20. Zmiany w przebicjach lub dodatkowe przebiccia.
21. Przewód wentylacji.
22. Zmiana tynku ryflowanego na gładki.
23. Zmiana ościeży okiennych z blachy na tynkowane.
24. Zwiększenie szerokości bramy garażowej.
25. Zmniejszenie wysokości drzwi z 215 na 200 cm.
26. Zwiększenie obudowy pionu.

Zmiany w okładzinach i detalach elewacyjnych:

- blacha aluminiowa Prefa w kolorze p.10 zielona patyna, rąbek stojący, układ pionowy, podział na nieregularne pasy i wyrównany do okien,
- obróbka z blachy aluminiowej Prefa w kolorze p.10 zielona patyna,
- blacha aluminiowa Prefa w kolorze ciemnoszarym nr 23 (RAL 7022),
- obróbka ościeży z blachy aluminiowej Prefa w kolorze ciemnoszarym nr 23 (RAL 7022),
- tynk gładki, kolor szary,
- obróbka z blachy powlekanej, kolor szary – dopasowany do okładziny elewacyjnej, matowy,
- oścież tynkowana.

W budynkach B.1-B.14 i C.1-C.14:

1. Zmiana grubości ściany (skutkuje zmianą powierzchni C.1.g, C.2.g).
2. Zmiana wielkości słupa.
3. Przesunięcie bramy garażowej.
4. Zmiana kierunku spadku.
5. Zmiana warstw przegrody.
6. Zmiana spadku posadzki garażu i struktury warstwowej.
7. Zmiana wysokości osi przebiccia.
8. Obniżenie nadproża.
9. Przesunięcie przebiccia.
10. Zmiana grubości konstrukcji stropu.
11. Zmiana grubości i przesunięcie ściany oporowej.
12. Przesunięcie osi.
13. Zmiana dojścia/dojazdu.
14. Zmiana warstw przegrody.

15. Zmiany fundamentów zgodnie z projektem technicznym konstrukcji.
16. Zmiana aranżacji pom. Technicznego.
17. Dodatkowa wywiewka.
18. Zmiany w przebiciach lub dodatkowe przebiccia.
19. Przewód wentylacji.
20. Zmiana tynku ryflowanego na gładki.
21. Zmiana ościeży okiennych z blachy na tynkowane.
22. Zwiększenie szerokości bramy garażowej.
23. Zmniejszenie wysokości drzwi z 215 na 200 cm.
24. Zmiana lokalizacji drabinki.
25. Zmiana wielkości obudowy pionu.

Zmiany w okładzinach i detalach elewacyjnych:

- blacha aluminiowa Prefa w kolorze p.10 zielona patyna, rąbek stojący, układ pionowy, podział na nieregularne pasy i wyrównany do okien,
- obróbka z blachy aluminiowej Prefa w kolorze p.10 zielona patyna,
- blacha aluminiowa Prefa w kolorze ciemnoszarym nr 23 (RAL 7022),
- obróbka ościeży z blachy aluminiowej Prefa w kolorze ciemnoszarym nr 23 (RAL 7022),
- tynk gładki, kolor szary,
- obróbka z blachy powlekanej, kolor szary – dopasowany do okładziny elewacyjnej, matowy,
- oścież tynkowana.

Powyższe zmiany zostały oznaczone na rysunkach, zgodnie z przedstawioną numeracją. W niniejszym opisie, zmiany wynikające pośrednio i bezpośrednio z tych zmian (np. zmiana powierzchni) także została oznaczona kolorem niebieskim.

Przedmiotem zamierzenia budowlanego jest dwadzieścia osiem budynków mieszkalnych jednorodzinnych w zabudowie bliźniaczej oraz czternaście garaży wolnostojących zamkniętych. Dodatkowo przewiduje się realizację schodów zewnętrznych, murów oporowych, dojść, dojazdu oraz zewnętrznych stanowisk postojowych.

Budynki mieszkalne jednorodzinne zaliczają się do I kategorii obiektu budowlanego. Obiekty te zostały podzielone na typy A i B numerowane kolejno od 1 do 14. Budynki A i B zostały połączone w pary lustrzane - AA i BB, tworząc zabudowę bliźniaczą.

Budynki garażowe zaliczają się do III kategorii obiektu budowlanego. Obiekty te zostały oznaczone literą C i są numerowane kolejno od 1 do 14. Budynki garażowe stanowią niezależną konstrukcję - są wolnostojące, zamknięte, nie są połączone z budynkami mieszkalnymi.

Przestrzeń pomiędzy garażami a budynkami mieszkalnymi będzie zasypana ziemią, tak aby stworzyć powierzchnię zewnętrzną na jednym poziomie z wnętrzem budynku i dostępną z mieszkań zlokalizowanych na pierwszym piętrze budynku typu B. Mury oporowe stanowią zabezpieczenie zasypu i zaliczane są do VIII kategorii obiektu budowlanego.

Schody zewnętrzne umożliwiają dostęp do mieszkań zlokalizowanych na pierwszym piętrze budynków typu B. Budynki typu A posiadają wewnętrzne klatki schodowe. Schody zewnętrzne zaliczane są do VIII kategorii obiektu budowlanego.

Do każdego budynku zostało doprowadzone dojście oraz dojazd, dodatkowo przewidziano 14 zewnętrznych stanowisk postojowych.

2. Zamierzony sposób użytkowania oraz program użytkowy obiektu budowlanego.

Budynki typu A i B o numerach od 1-14 będą użytkowane jako mieszkalne jednorodzinne. Program użytkowy typowy dla tej funkcji budynku. Budynki typu A posiadają w swojej bryle garaż wbudowany. Budynki typu B, nie posiadają garażu wbudowanego, a ich mieszkańcy będą korzystać z wolnostojących budynków garażowych, zamkniętych oznaczonych literą C o numerach od 1 do 14.

Budynki typu A mają trzy kondygnacje nadziemne. W pierwszym lokalu, dostępnym z poziomu terenu, antresola została zmieniona na drugą kondygnację. Drugi lokal mieszkalny zajmuje pierwsze oraz drugie piętro budynku.

Budynki B.1-B.6, B9, B10, B13, B14 mają trzy kondygnacje nadziemne. Na parterze umieszczony jest lokal mieszkalny parterowy. Drugi lokal mieszkalny zajmuje pierwsze oraz drugie piętro budynku.

Budynki typu B7, B8, B.11, B.12 bez zmian względem projektu pierwotnego posiadają dwie kondygnacje nadziemne, ostatni poziom stanowi antresola pomieszczenia. Na parterze umieszczony jest lokal mieszkalny parterowy. Drugi lokal mieszkalny zajmuje pierwsze piętro oraz antresolę nad jednym pomieszczeniem – pokojem dziennym z kuchnią.

Budynki typu C posiadają jedną kondygnację nadziemną.

Szczegółowy układ funkcjonalny wnętrza oraz powiązań pomiędzy pomieszczeniami został przedstawiony w części rysunkowej projektu.

3. Układ przestrzenny oraz forma architektoniczna obiektu budowlanego, w tym jego wygląd zewnętrzny, uwzględniając charakterystyczne wyroby wykończeniowe i kolorystykę elewacji, a także sposób jego dostosowania do warunków wynikających z wymaganych przepisami szczególnymi pozwoleń, uzgodnień lub opinii innych organów.

Projekt powstał w oparciu o uchwałę XCII/2413/18 Rady Miasta Krakowa z dnia 10 stycznia 2018 r. w sprawie uchwalenia miejscowego planu zagospodarowania przestrzennego obszaru „Tonie – Zachód”.

Budynki zaprojektowano na rzutach złożonych z prostokątów. Poszczególne części mają różne wysokości a okna mieszkań zostały umieszczone w ścianach zewnętrznych tak aby zapewnić maksymalną prywatność przyszłym mieszkańcom. Bryły są skromne, kryte dachem płaskim, stropodachem zielonym oraz tarasami do chodzenia. Do wykończenia budynków zostanie użyty szary tynk gładki oraz blacha aluminiowa w kolorze zielonej patyny.

Ograniczenia i zakazy w obszarze opracowania projektu zgodnie z obowiązującym miejscowym planem zagospodarowania przestrzennego dotyczące planowanej inwestycji i terenu:	Sposób spełnienia wymagań w projekcie:
zakaz stosowania ogrodzeń pełnych	projekt nie przewiduje realizacji ogrodzenia.
zakaz lokalizacji wolnostojących budynków gospodarczych i wiat śmietnikowych od strony ul. Władysława Łokietka.	w projekcie nie występują wolnostojące budynki gospodarcze i wiaty śmietnikowe od strony ul. Władysława Łokietka
zakaz lokalizacji przydomowych oczyszczalni ścieków	budynki będą podłączone do miejskiej sieci kanalizacji sanitarnej
zakaz stosowania paliw stałych w obiektach budowlanych	w zakresie zaopatrzenia w ciepło planowane jest wykorzystanie powietrznych pomp ciepła
nakaz realizacji zabudowy jednorodzinnej w układzie wolnostojącym lub bliźniaczym	budynki mieszkalne jednorodzinne zaprojektowane zostały w układzie bliźniaczym, garaże zamknięte są wolnostojące
minimum 60% powierzchni biologicznie czynnej w terenach MN/U.12 i MN.17 oraz minimum 70% w terenie MN.6	projektowane zagospodarowanie terenu zapewnia wymaganą powierzchnię biologicznie czynną we wszystkich wymienionych terenach (szczegółowe zestawienie w pkt 4. opisu technicznego projektu zagospodarowania terenu)

Maksymalny wskaźnik powierzchni zabudowy dla terenów MN/U.12, MN.17 i MN.6 - 30%	projektowana powierzchnia zabudowy nie przekracza dopuszczalnego wskaźnika (szczegółowe zestawienie w pkt 4. opisu technicznego projektu zagospodarowania terenu)
wskaźnik intensywności zabudowy: 0,15 - 0,6 dla terenów MN.17 i MN.6 oraz 0,15 - 0,9	Intensywność projektowanej zabudowy mieści się w wymaganym przedziale (szczegółowe zestawienie w pkt 4. opisu technicznego projektu zagospodarowania terenu)
maksymalna wysokość zabudowy jednorodzinnej dla terenów MN/U.12, MN.17 i MN.6 wynosi 11m	projektowane budynki mieszkalne jednorodzinne nie przekraczają wysokości 11m, mierzonej zgodnie z określoną definicją, szczegółowe wymiary zostały określone na przekrojach w części rysunkowej projektu architektoniczno-budowlanego oraz w pkt 4. poniżej
maksymalna wysokość zabudowy gospodarczej i garaży dla terenów MN/U.12, MN.17 i MN.6 wynosi 6m	projektowane budynki garażowe nie przekraczają wysokości 6m, mierzonej zgodnie z określoną definicją, szczegółowe wymiary zostały określone na przekrojach w części rysunkowej projektu architektoniczno-budowlanego oraz w pkt 4. poniżej
dopuszczenie stosowania dachów płaskich jako stropodachów z nawierzchnią roślinną ekstensywną lub intensywną lub jako tarasów do chodzenia	projektowane budynki będą przekryte dachami płaskimi z nawierzchnią roślinną ekstensywną oraz częściowo będą tarasami do chodzenia
określa się minimalną liczbę miejsc parkingowych, wliczając miejsca w garażach, odniesioną odpowiednio do funkcji obiektów lub do funkcji ich części - budynki w zabudowie jednorodzinnej - 2 miejsca na 1 dom	wymagane jest 56 stanowisk postojowych - przewidziano łącznie 70 stanowisk postojowych, 14 zewnętrznych oraz 56 w garażach.

Projektowane budynki spełniają wymagania w zakresie przepisów dotyczących przestaniania oraz następcznienia. §13, 60 rozporządzenia ministra infrastruktury z dnia 12 kwietnia 2002 r. w sprawie warunków technicznych, jakim powinny odpowiadać budynki i ich usytuowanie.

Obowiązujący miejscowy plan zagospodarowania przestrzennego nie posiada definicji powierzchni biologicznie czynnej. Kalkulacja została dokonana na podstawie definicji występującej w przepisach odrębnych. Jest to teren o nawierzchni urządzonej w sposób zapewniający naturalną vegetację roślin i retencję wód opadowych, a także 50% powierzchni tarasów i stropodachów z taką nawierzchnią o powierzchni nie mniejszej niż 10 m². Opis planowane technologii wykonania tarasów i stropodachów zamieszczono w punkcie 15. Jest to typowe i powszechnie stosowane rozwiązanie systemowe zapewniające naturalną vegetację roślin i retencję wód opadowych. Tarasy będą pełniły swoją typową funkcję, tożsamą z terenem otaczającym budynek - ogrodem.

Wszystkie, bardziej szczegółowe informacje w zakresie formy oraz wyglądu zewnętrznego zawarto w części rysunkowej projektu.

4. Charakterystyczne parametry obiektu budowlanego.

a. Kubatura:

Wyjaśnienie oznaczenia zmian w poniższej tabeli:

Wielkość budynków (wysokość, szerokość, długość) nie uległa zmianie. Zmiana kubatury wynika z przesunięcia barierki na dachu budynku (zmiana istotna „Ist.1”), a przez to zwiększenia powierzchni tarasu. Zgodnie z obowiązującymi przepisami kubaturę budynku powiększa się o tarasy i balkony do wysokości barierki.

budynek	kubatura brutto (m³)
A1	1425,99
A2	1425,99
A3	1425,99
A4	1425,99
A5	1425,99
A6	1425,99
A7	1425,99
A8	1425,99
A9	1425,99
A10	1425,99
A11	1425,99
A12	1425,99
A13	1425,99
A14	1425,99
B1	1024,43
B2	1024,43
B3	1024,43
B4	1024,43
B5	1024,43
B6	1024,43
B7	1024,43
B8	1024,43
B9	1024,43
B10	1024,43
B11	1024,43
B12	1024,43
B13	1024,43
B14	1024,43
C1	198,63
C2	198,63
C3	198,63
C4	198,63
C5	198,63
C6	198,63
C7	198,63
C8	198,63
C9	198,63
C10	198,63
C11	198,63
C12	198,63
C13	198,63
C14	198,63

b. Zestawienie powierzchni:

Istotne zmiany w projekcie wpłynęły na zestawienie powierzchni całkowitej i użytkowej, zgodnie z poniższą tabelą.

Nieistotne zmiany w projekcie także wpłynęły na zestawienie powierzchni użytkowej mieszkań i powierzchni ruchu (garaż) zgodnie z poniższą tabelą.

budynek	powierzchnia zabudowy (m²)	powierzchnia całkowita (m²)	powierzchnia użytkowa (m²)	powierzchnia ruchu (garaż) (m²)
A1	179,81	377,51	256,75	41,06
A2	179,81	377,51	256,75	41,06
A3	179,81	377,51	256,75	41,06
A4	179,81	377,51	256,75	41,06
A5	179,81	377,51	256,75	41,06
A6	179,81	377,51	256,75	41,06
A7	179,81	377,51	256,75	41,06
A8	179,81	377,51	256,75	41,06
A9	179,81	377,51	256,75	41,06
A10	179,81	377,51	256,75	41,06
A11	179,81	377,51	256,75	41,06
A12	179,81	377,51	256,75	41,06
A13	179,81	377,51	256,75	41,06
A14	179,81	377,51	256,75	41,06
B1	108,75	289,10	234,19	-
B2	108,75	289,10	234,19	-
B3	108,75	289,10	234,19	-
B4	108,75	289,10	234,19	-
B5	108,75	289,10	234,19	-
B6	108,75	289,10	234,19	-
B7	108,75	217,51	226,69	-
B8	108,75	217,51	226,69	-
B9	108,75	289,10	234,19	-
B10	108,75	289,10	234,19	-
B11	108,75	217,51	226,69	-
B12	108,75	217,51	226,69	-
B13	108,75	289,10	234,19	-
B14	108,75	289,10	234,19	-
C1	47,79	47,79	-	41,2
C2	47,79	47,79	-	41,2
C3	47,79	47,79	-	41,2
C4	47,79	47,79	-	41,2
C5	47,79	47,79	-	41,2
C6	47,79	47,79	-	41,2
C7	47,79	47,79	-	41,2
C8	47,79	47,79	-	41,2
C9	47,79	47,79	-	41,2
C10	47,79	47,79	-	41,2
C11	47,79	47,79	-	41,2
C12	47,79	47,79	-	41,2
C13	47,79	47,79	-	41,2
C14	47,79	47,79	-	41,2
SUMA	4708,95	9715,20	6843,16	1151,64

Poszczególne powierzchnie całkowite przedstawiają się w następujący sposób:

budynek	powierzchnia całkowita pierwszej kondygnacji (m²)	powierzchnia całkowita drugiej kondygnacji (m²)	powierzchnia całkowita trzeciej kondygnacji (m²)	powierzchnia całkowita budynku (m²)
A1	169,77	119,82	87,92	377,51
A2	169,77	119,82	87,92	377,51
A3	169,77	119,82	87,92	377,51
A4	169,77	119,82	87,92	377,51
A5	169,77	119,82	87,92	377,51
A6	169,77	119,82	87,92	377,51
A7	169,77	119,82	87,92	377,51
A8	169,77	119,82	87,92	377,51
A9	169,77	119,82	87,92	377,51
A10	169,77	119,82	87,92	377,51
A11	169,77	119,82	87,92	377,51
A12	169,77	119,82	87,92	377,51
A13	169,77	119,82	87,92	377,51
A14	169,77	119,82	87,92	377,51
B1	108,75	108,75	71,59	289,10
B2	108,75	108,75	71,59	289,10
B3	108,75	108,75	71,59	289,10
B4	108,75	108,75	71,59	289,10
B5	108,75	108,75	71,59	289,10
B6	108,75	108,75	71,59	289,10
B7	108,75	108,75	0 – budynek 2-kondygnacyjny	217,51
B8	108,75	108,75	0 – budynek 2-kondygnacyjny	217,51
B9	108,75	108,75	71,59	289,10
B10	108,75	108,75	71,59	289,10
B11	108,75	108,75	0 – budynek 2-kondygnacyjny	217,51
B12	108,75	108,75	0 – budynek 2-kondygnacyjny	217,51
B13	108,75	108,75	71,59	289,10
B14	108,75	108,75	71,59	289,10
C1	47,79	0 – budynek 1-kondygnacyjny	0 – budynek 1-kondygnacyjny	47,79
C2	47,79	0 – budynek 1-kondygnacyjny	0 – budynek 1-kondygnacyjny	47,79
C3	47,79	0 – budynek 1-kondygnacyjny	0 – budynek 1-kondygnacyjny	47,79
C4	47,79	0 – budynek 1-kondygnacyjny	0 – budynek 1-kondygnacyjny	47,79
C5	47,79	0 – budynek 1-kondygnacyjny	0 – budynek 1-kondygnacyjny	47,79
C6	47,79	0 – budynek 1-kondygnacyjny	0 – budynek 1-kondygnacyjny	47,79
C7	47,79	0 – budynek 1-kondygnacyjny	0 – budynek 1-kondygnacyjny	47,79
C8	47,79	0 – budynek 1-kondygnacyjny	0 – budynek 1-kondygnacyjny	47,79
C9	47,79	0 – budynek 1-kondygnacyjny	0 – budynek 1-kondygnacyjny	47,79
C10	47,79	0 – budynek 1-kondygnacyjny	0 – budynek 1-kondygnacyjny	47,79
C11	47,79	0 – budynek 1-kondygnacyjny	0 – budynek 1-kondygnacyjny	47,79
C12	47,79	0 – budynek 1-kondygnacyjny	0 – budynek 1-kondygnacyjny	47,79
C13	47,79	0 – budynek 1-kondygnacyjny	0 – budynek 1-kondygnacyjny	47,79
C14	47,79	0 – budynek 1-kondygnacyjny	0 – budynek 1-kondygnacyjny	47,79
SUMA	4568,37	3200,05	1946,78	9715,20

Obliczeń dokonano na podstawie definicji określonych w obowiązującym miejscowym planie zagospodarowania terenu, zgodnie z którym:

- powierzchnia zabudowy – należy przez to rozumieć powierzchnię terenu zajęłą przez budynek w stanie wykończonym (wyznaczoną przez rzut wymiarów zewnętrznych budynku na powierzchnię terenu), do której nie zalicza się: a) powierzchni elementów budynku ani ich części nie wystających ponad powierzchnię terenu, b) powierzchni elementów drugorzędnych budynku np. schodów zewnętrznych, ramp zewnętrznych, pochylni zewnętrznych, daszków, markiz, okapów dachowych, oświetlenia zewnętrznego, c) zewnętrznych obiektów pomocniczych np. szklarni i przybudówek.
- powierzchnia całkowitej budynku – należy przez to rozumieć sumę powierzchni całkowitych wszystkich kondygnacji nadziemnych budynku,
- powierzchnia całkowitej zabudowy – należy przez to rozumieć sumę powierzchni całkowitych budynków w obrębie działki budowlanej objętej projektem zagospodarowania terenu do decyzji administracyjnej albo zgłoszeniem,
- wskaźniku intensywności zabudowy – należy przez to rozumieć parametr, wyrażony jako udział powierzchni całkowitej zabudowy w powierzchni terenu działki budowlanej objętej projektem zagospodarowania terenu do administracyjnej albo zgłoszeniem.

Zgodnie z § 3 pkt 16) Rozporządzenia Ministra Infrastruktury z dnia 12 kwietnia 2002 r. w sprawie warunków technicznych, jakim powinny odpowiadać budynki i ich usytuowanie przez pojęcie kondygnacji - należy rozumieć poziomą część budynku, zawartą pomiędzy powierzchnią posadzki na stropie lub najwyższej położonej warstwy podłogowej na gruncie, a powierzchnią posadzki na stropie lub warstwy osłaniającej izolację cieplną stropu, znajdującego się nad tą częścią budynku, przy czym za kondygnację uważa się także poddasze z pomieszczeniami przeznaczonymi na pobyt ludzi oraz poziomą część budynku stanowiącą przestrzeń na urządzenia techniczne, mającą średnią wysokość w świetle większą niż 2 m. Za kondygnację nie uznaje się nadbudówek ponad dachem, takich jak maszynownia dźwigu, centrala wentylacyjna, centrala klimatyzacyjna, obudowa wyjścia z klatki schodowej, kotłownia lub inne pomieszczenia techniczne.

Zgodnie z powyższymi definicjami do powierzchni całkowitej budynku wliczono powierzchnię wszystkich kondygnacji nadziemnych budynku liczoną w zewnętrznym obrysie wykończonych ścian. Do powierzchni całkowitej nie wliczono powierzchni tarasów i antresol, ponieważ zgodnie z definicją zawartą z Rozporządzeniu Ministra Infrastruktury nie są to kondygnacje. **Dodatkowo zgodnie ze zmianą rozporządzenia w sprawie zakresu i formy projektu budowlanego, które weszło w życie 1 kwietnia 2024 roku do powierzchni całkowitej nie wlicza się powierzchni tarasów, balkonów i logii (§ 20 w ust. 1 w pkt 4 w lit. B, tiret piąte).** Miejskowy plan zagospodarowania przestrzennego także nie nakazuje wliczania powierzchni tarasów i antresol do powierzchni całkowitej kondygnacji i budynku.

Zestawienie powierzchni poszczególnych pomieszczeń znajduje się w części rysunkowej projektu.

c. Wysokość, długość, szerokość, średnica.

budynek	wysokość mierzona zgodnie z MPZP (m)*	wysokość mierzona zgodnie z WT (m)**	długość budynku (m)	szerokość budynku (m²)
A1	10,265	10,47	18,46	13,285
A2	10,335	10,47	18,46	13,285
A3	10,3	10,47	18,46	13,285
A4	10,665	10,47	18,46	13,285
A5	10,835	10,47	18,46	13,285
A6	10,835	10,47	18,46	13,285
A7	10,6	10,47	18,46	13,285
A8	10,63	10,47	18,46	13,285
A9	10,455	10,47	18,46	13,285
A10	10,695	10,47	18,46	13,285
A11	10,67	10,47	18,46	13,285
A12	10,865	10,47	18,46	13,285
A13	10,65	10,47	18,46	13,285
A14	10,8	10,47	18,46	13,285
B1	10,335	10,47	12,855	8,46
B2	10,46	10,47	12,855	8,46
B3	10,695	10,47	12,855	8,46
B4	10,965	10,47	12,855	8,46
B5	10,96	10,47	12,855	8,46
B6	10,97	10,47	12,855	8,46
B7	10,76	10,47	12,855	8,46
B8	10,76	10,47	12,855	8,46
B9	10,705	10,47	12,855	8,46
B10	10,755	10,47	12,855	8,46
B11	10,81	10,47	12,855	8,46
B12	10,96	10,47	12,855	8,46
B13	10,925	10,47	12,855	8,46
B14	10,88	10,47	12,855	8,46
C1	2,985	3,295	7,55	6,33
C2	3,02	3,295	7,55	6,33
C3	3,49	3,295	7,55	6,33
C4	3,57	3,295	7,55	6,33
C5	3,755	3,295	7,55	6,33
C6	3,76	3,295	7,55	6,33
C7	3,475	3,295	7,55	6,33
C8	3,495	3,295	7,55	6,33
C9	3,085	3,295	7,55	6,33
C10	3,005	3,295	7,55	6,33
C11	3,315	3,295	7,55	6,33
C12	3,205	3,295	7,55	6,33
C13	3,46	3,295	7,55	6,33
C14	3,43	3,295	7,55	6,33

Zmiana wysokości garażu, mierzonej zgodnie z definicją rozporządzenia w sprawie warunków technicznych jakim powinny odpowiadać budynki i ich usytuowania, wynika ze zwiększenia spadku podłogi garażu, a przez to obniżenia poziomu terenu przy bramie garażowej o 5 cm z -10 do -15 cm, względem poziomu +- 0.00 budynku. 5 cm zmiany stanowi mniej niż 2% wysokości budynku. Wysokość garaży, mierzona metodą określoną w obowiązującym miejscowym planie zagospodarowania przestrzennego, nie ulega zmianie.

*Wysokość mierzona zgodnie z definicją obowiązującego planu zagospodarowania przestrzennego

**Wysokość mierzona zgodnie z definicją rozporządzenia w sprawie warunków technicznych jakim powinny odpowiadać budynki i ich usytuowania

d. Liczba kondygnacji.

Budynki typu A mają trzy kondygnacje nadziemne. Budynki B1-B6, B9, B10, B13, B14 mają trzy kondygnacje

nadziemne. Budynki B7, B8, B11, B12, bez zmian, posiadają dwie kondygnacje nadziemne. Budynki typu C mają jedną kondygnację nadziemną.

e. Inne dane niezbędne do stwierdzenia zgodności usytuowania obiektu z wymaganiami ochrony przeciwpożarowej.

Budynki zachowują wymagane odległości usytuowania od granic działek budowlanych oraz innych obiektów. Elewacje oraz pokrycie dachu zostaną wykonane z materiałów nierozprzestrzeniających ognia. Drewniane elementy podkonstrukcji okładzin elewacyjnych zostaną zabezpieczone przez impregnację do NRO.

5. Opinia geotechniczna oraz informację o sposobie posadowienia obiektu budowlanego.

Na potrzeby planowanej inwestycji zostały przeprowadzane badania gruntu, a dokumentacja badań podłoża gruntowego wraz z opinią geotechniczną została dołączona do odrębnego elementu projektu budowlanego (opinie, uzgodnienia, pozwolenia i inne dokumenty).

Warunki gruntowe: proste, pod warunkiem spełnienia wytycznych określonych w opinii geotechnicznej. Grunty występujące w podłożu projektowanych obiektów nadają się do ich posadowienia z uwzględnieniem zaleceń zawartych w dokumentacji badań podłoża gruntowego.

Kategoria geotechniczna obiektów: II.

Zgodnie z przeprowadzonymi badaniami oraz głębokością posadowienia fundamentów wymaganą ze względu na przemarzanie gruntu, zwierciadło wody gruntowej znajduje się poniżej poziomu posadowienia fundamentów.

Budynki będą posadowione na żelbetowych ławach fundamentowych. Szczegółowe rozwiązanie w zakresie posadowienia zostanie dobrane przez projektanta konstrukcji na etapie wykonywania projektu technicznego i wykonawczego.

6. Liczba lokali mieszkalnych i użytkowych.

Każdy z budynków mieszkalnych jednorodzinnych będzie posiadał dwa lokale mieszkalne. W sumie w całym zamierzeniu jest 56 lokali mieszkalnych.

7. Liczba lokali mieszkalnych dostępnych dla osób niepełnosprawnych.

Nie dotyczy. Planowana zabudowa obejmuje budynki mieszkalne jednorodzinne, dla których nie istnieje obowiązek realizacji lokali mieszkalnych dla osób niepełnosprawnych.

8. Opis zapewnienia niezbędnych warunków do korzystania z obiektów użyteczności publicznej i mieszkaniowego budownictwa wielorodzinnego przez osoby niepełnosprawne.

Nie dotyczy. Planowana zabudowa obejmuje jedynie budynki mieszkalne jednorodzinne.

9. Parametry techniczne obiektu budowlanego charakteryzujące wpływ obiektu budowlanego na środowisko i jego wykorzystywanie oraz na zdrowie ludzi i obiekty sąsiednie.

a. Zapotrzebowanie i jakości wody oraz ilości, jakości i sposobu odprowadzania ścieków oraz wód opadowych.

Dobowe zapotrzebowanie na wodę szacowane jest na poziomie pomiędzy 80-120 l/osobę. Dla jednego budynku będzie to ok. 0,8m³/dobę.

Ilość ścieków będzie równa zużyciu wody, a ich jakość będzie typowa dla funkcji mieszkaniowej. Ścieki będą odprowadzane do gminnej sieci kanalizacyjnej za pomocą przyłączy realizowanych na podstawie odrębnej procedury administracyjnej. Woda opadowa z dachów oraz części terenów utwardzonych będzie odprowadzana do szczelnych zbiorników i wykorzystywana do podlewania ogrodów. Nadmiar wody będzie wywożony. Woda opadowa z ostatnich odcinków dojdzie do wejść do budynków mieszkalnych będzie odprowadzana na teren nieutwardzony. Od budynków należy ukształtować spadek zapewniający

odpowiedni odpływ wody opadowej (min 1%).

Dokładne informacje w powyższym zakresie zostaną przedstawione w projekcie technicznym.

b. Emisja zanieczyszczeń gazowych, w tym zapachów, pyłowych i płynnych, z podaniem ich rodzaju, ilości i zasięgu rozprzestrzeniania się.

Emisja zanieczyszczeń gazowych i zapachów typowa dla funkcji mieszkalnej jednorodzinnej i zgodna z obowiązującymi przepisami.

c. Rodzaju i ilości wytwarzanych odpadów.

Rodzaj i ilość wytwarzanych odpadów typowa dla funkcji mieszkalnej jednorodzinnej. Odpady będą segregowane i przechowywane w wyznaczonych do tego miejscach do czasu odbioru przez służby komunalne.

d. Właściwości akustyczne oraz emisja drgań, a także promieniowania, w szczególności jonizującego, pola elektromagnetycznego i innych zakłóceń, z podaniem odpowiednich parametrów tych czynników i zasięgu ich rozprzestrzeniania się.

Budynki i urządzenia techniczne związane z ich funkcjonowaniem nie będą generowały hałasu ani wibracji wykraczających ponad obowiązujące standardy w tym zakresie. Nie będzie występowała emisja promieniowania jonizującego związana z realizacją inwestycji. Nie będzie generowane pole elektromagnetyczne inne niż związane z instalacją elektryczną i urządzeniami gospodarstwa domowego.

Przegrody budowlane należy wykonać w zgodności z obowiązującymi przepisami w szczególności w kwestii przegród wewnętrznych zachowując izolacyjność akustyczną:

Dla ścian oddzielających lokale mieszkalne – $R'_{A,1} \geq 50\text{dB}$

Dla ścian bez drzwi oddzielających pokój od pomieszczenia sanitarnego $R_{A,1,R} \geq 38\text{dB}$

Dla ścian bez drzwi oddzielające poszczególne pomieszczenia w mieszkaniu $R_{A,1,R} \geq 35\text{dB}$

Dla stropów w mieszkaniu wielopoziomowym $R_{A,1,R} \geq 45\text{dB}$

Dla ścian między budynkami bliźniaczymi $R'_{A,1,R} \geq 52\text{dB}$

Dla stropów izolacyjność od dźwięków uderzeniowych (wraz z podłogą) $L_{n,w,R} \leq 58\text{dB}$

e. Wpływ obiektu budowlanego na istniejący drzewostan, powierzchnię ziemi, w tym glebę, wody powierzchniowe i podziemne.

Obiekty budowlane nie mają wpływu na istniejący drzewostan – obszar inwestycji jest wolny od drzew.

Ze względu na spadek terenu przewiduje się prace związane z odpowiednim kształtowaniem terenu wokół budynków. Powierzchnia ziemi zostanie zagospodarowana zgodnie z oznaczeniami przedstawionymi w części rysunkowej projektu. Uzyskane w trakcie prac budowlanych masy ziemi zostaną wykorzystane do ukształtowania terenu i częściowo zutylizowane, zgodnie z obowiązującymi przepisami.

Projektowane ukształtowanie terenu nie zmienia naturalnego spływu wód opadowych występującego na tym terenie, tak aby wody opadowe były kierowane na sąsiednie nieruchomości.

Na terenie planowanej inwestycji nie występują wody powierzchniowe.

W trakcie wykonywania badań gruntu natrafiono na wody podziemne. Zgodnie z przeprowadzonymi badaniami oraz głębokością posadowienia fundamentów wymaganą ze względu na przemarzanie gruntu zwierciadło wody gruntowej znajduje się poniżej poziomu posadowienia fundamentów.

Na skutek zmian wynikających z projektu technicznego konstrukcji wystąpiły zmiany nieistotne polegające na zmianie głębokości posadowienia fundamentów zgodnie z poniższą tabelą.

numer otworu	rzędna terenu (m n.p.m.)	głębokość lustra wody (m)	rzędna lustra wody (m)	rzędna „0” najbliższego budynku (m n.p.m.)	głębokość fundamentu od „0” budynku (m)	wysokość fundamentu ponad lustrem wody (m)
1	223,32	1,1	222,22	223,5	1,25	0,03
2	223,06	0,8	222,26	223,6	1,25	0,09
3	223,42	1,1	222,32	223,6	1,25	0,03
4	223,2	1,1	222,1	223,7	1,25	0,35
5	223,9	1,7	222,2	224,1	1,25	0,65
6	223,7	1,6	222,1	224,1	1,25	0,75
7	224,38	2,3	222,08	224,2	1,25	0,87
8	224,2	2,3	221,9	224,3	1,25	1,15
9	224,3	2,4	221,9	224,4	1,25	1,25
10	224,2	2,3	221,9	224,5	1,25	1,35
11	224,1	2,3	221,8	224,6	1,25	1,55
12	224,2	2,8	221,4	224,7	1,25	2,05

10. Analiza technicznych, środowiskowych i ekonomicznych możliwości realizacji wysoce wydajnych systemów alternatywnych zaopatrzenia w energię i ciepło.

a. Oszacowanie rocznego zapotrzebowania na energię użytkową do ogrzewania, wentylacji, przygotowania ciepłej wody użytkowej.

Roczne zapotrzebowanie na energię użytkową do ogrzewania, wentylacji i przygotowywania c.w.u. szacuje się na około 60 kWh/m².

b. Dostępne nośniki energii.

Dostępne są nośniki energii nieodnawialnej takie gaz i energia elektryczna z sieci oraz nośniki energii odnawialnej takie jak energia elektryczna pozyskiwana z instalacji fotowoltaicznych. Ze względu na zapisy obowiązującego miejscowego planu zagospodarowania terenu nie dopuszczalne jest użycie paliw stałych.

c. Wybór dwóch systemów zaopatrzenia w energię do analizy porównawczej.

W celu przeprowadzenia analizy wybrano:

1. Zaopatrzenie w energię elektryczną pochodzącą z sieci do zasilania powietrznej pompy ciepła.
2. Zaopatrzenie w energię pochodzącą z spalania gazu.

d. Obliczenia optymalizacyjno-porównawcze dla wybranych systemów zaopatrzenia w energię.

Powierzchnia użytkowa i ogrzewana całego zamierzenia wynosi w zaokrągleniu 6 800 m².

Ilość nośnika dla pierwszego wariantu wyniesie około 113 350 kWh/rok przy sprawności systemu grzewczego na poziomie 3,6. Założeniem kosztu 1 kWh jest 0,73 zł przy wykorzystaniu energii jedynie z sieci.

Ilość nośnika dla drugiego wariantu wyniesie około 374 400 kWh/rok przy założeniu sprawności na poziomie 1,09. Założeniem kosztu 1 kWh jest 0,22 zł.

e. Wyniki analizy porównawczej i wybór systemu zaopatrzenia w energię.

Roczny koszt energii dla pierwszego wariantu wyniesie ok. 82 745 zł, natomiast dla drugiego ok. 82 368 zł.

Koszt energii dla obu analizowanych przypadków jest bardzo zbliżony. Ze względu na możliwość pozyskania energii elektrycznej ze źródeł odnawialnych oraz wysokie koszty doprowadzenia gazu do projektowych budynków wybrano system zaopatrzenia w energię elektryczną i powietrzną pompę ciepła.

11. Analiza technicznych i ekonomicznych możliwości wykorzystania urządzeń, które automatycznie regulują temperaturę oddzielnie w poszczególnych pomieszczeniach lub w wyznaczonej strefie ogrzewanej.

Instalacja ogrzewania będzie wyposażona w urządzenia automatycznie regulujące temperaturę oddzielnie w poszczególnych pomieszczeniach. Oszczędności zależnie od faktycznego przebywania użytkowników w ogrzewanych strefach oraz programowania mogą sięgać nawet 20% rocznie, co powinno zagwarantować zwrot z inwestycji już po pierwszych dwóch latach użytkowania.

12. Informacje o zasadniczych elementach wyposażenia budowlano-instalacyjnego, zapewniających użytkowanie obiektu budowlanego zgodnie z przeznaczeniem.

Każdy z budynków zaopatrzony będą w następujące instalacje:

- instalację elektryczną,
- instalację odgromową
- instalację wentylacji mechanicznej,
- instalację wodną i kanalizacji sanitarnej,
- instalację kanalizacji deszczowej,
- instalację c.o. opartą o powietrzne pompy ciepła,

Wszelkie informacje dotyczące rozwiązania elementów wyposażenia budowlano-instalacyjnego będą uwzględnione w projekcie technicznym opracowanym przez projektantów branżowych.

13. Dane dotyczące warunków ochrony przeciwpożarowej, stosownie do zakresu projektu.

Dla budynków jednorodzinnych, które posiadających do trzech kondygnacji nadziemnych łącznie oraz garaży wolnostojących o liczbie stanowisk postojowych nie większej niż 2 nie wymaga się określania klasy odporności pożarowej.

Wszystkie elementy drewniane zostaną zabezpieczone środkami do klasy nierozprzestrzeniania ognia i niezapalności. Ściany oraz dachy będą wykonane jako nierozprzestrzeniające ognia.

Budynki mieszkalne jednorodzinne należą do strefy pożarowej ZL IV. Garaże wolnostojące należą do strefy pożarowej PM o $Q < 500 \text{ MJ/m}^2$. Dopuszczalna wielość strefy pożarowej ZL IV dla budynków niskich wynosi 8 000 m². Dopuszczalna wielość strefy pożarowej PM o $Q < 500 \text{ MJ/m}^2$ dla budynków niskich wynosi 20 000 m².

Zespół budynków został podzielony na trzy strefy pożarowe obejmujące budynki o numerach:

- strefa pierwsza: A,B,C 1-4
- strefa druga A 5-10 oraz B i C 5-12
- strefa trzecia A 11-14 oraz B i C 13-14

Wszystkie budynki objęte niniejszym projektem położone są na jednej działce budowlanej. Powierzchnia wewnętrzna budynków w określonych trzech strefach nie przekracza najmniejszej dopuszczalnej powierzchni strefy pożarowej wymaganej dla każdego ze znajdujących się na tej działce rodzaju budynku, dlatego odległości między ścianami zewnętrznymi budynków nie ustala się.

W zabudowie jednorodzinnej nie określa się odległości od garaży zamkniętych o liczbie stanowisk postojowych nie większej niż 3.

Zachowano odległości od sąsiednich budynków i działek budowlanych wymagane przepisami, co szczegółowo oznaczono na rysunku projektu zagospodarowania terenu.

Dla projektowanych obiektów budowlanych woda do celów przeciwpożarowych do zewnętrznego gaszenia pożaru jest zapewniana w ramach ilości wody przewidzianej dla jednostek osadniczych i nie ma obowiązku zapewnienia dodatkowego zaopatrzenia w wodę.

Projektowana zabudowa nie wymaga doprowadzenia drogi pożarowej.

Należy zastosować przeciwpożarowy wyłącznik prądu dla każdej strefy pożarowej.

Stropy między lokalami mieszkalnymi posiadają odporność REI 30, natomiast ściana oddzielająca budynki

w zabudowie bliźniaczej posiada odporność REI 60. Odporność ogniowa przegród wewnętrznych oddzielających mieszkania lub samodzielne pomieszczenia mieszkalne od dróg komunikacji ogólnej oraz od innych mieszkań i samodzielnych pomieszczeń mieszkalnych i lokalu użytkowego wynosi min. EI30.

Dopuszcza się stosowanie przewodów wentylacyjnych o klasie reakcji na ogień co najmniej E pod warunkiem zainstalowania w miejscu przejścia przewodów wentylacyjnych przez przegrody wydzielające lokal mieszkalny zabezpieczenia ogniochronnego o klasie odporności ogniowej co najmniej E I 30.

14. Zestawienie warstw przegród budowlanych.

Na skutek zmian wynikających z projektu technicznego oraz zmian materiałów elewacyjnych wystąpiły zmiany nieistotne w warstwach przegród budowlanych. Zmiany wykazane w dokumentacji objętej zmiennym pozwoleniem na budowę, decyzja nr 919/6740.1/2024 z dnia 07.10.2024 r. Oznaczono kolorem niebieskim. Spis zmian nieistotnych według prawa budowlanego w stosunku do projektu architektoniczno-budowlanego objętego decyzją nr 171/6740.1/2023 z dnia 13 lutego 2023 r. Zmienionego decyzją nr 919/6740.1/2024 z dnia 07.10.2024 r oznaczono kolorem zielonym.

PRZEGRODA POZIOMA ZEWNĘTRZNA					
FUNKCJA	NAZWA	NR	WARSTWY	GR. (MM)	DODATKOWE PARAMETRY
podłoga na gruncie	PpZ 1	1	grunt rodzimy		
		2	zagęszczona podsypka piaskowa	300	Is min. 0,98, grubość podbudowy min. 300 mm + do głębokości usuniętego humusu
		3	chudy beton	100	
		4	hydroizolacja		2x papa termozgrzewalna
		5	termoizolacja	160	XPS lub EPS.100 λ 0,036 W/(m·K), układany w czterech warstwach 40 mm
		6	folia do ogrzewania podłogowego		
		7	wylewka betonowa	70	
		8	warstwa wykończeniowa	20	
podłoga na gruncie w garażu	PpZ 2	1	grunt rodzimy		
		2	zagęszczona podsypka piaskowa	300	Is min. 0,98, grubość podbudowy min. 300 mm + do głębokości usuniętego humusu
		3	chudy beton	100	
		4	hydroizolacja		2x papa termozgrzewalna
		5	termoizolacja	50-200	XPS 300 λ 0,036 W/(m·K), układany w spadku
		6	folia do ogrzewania podłogowego		
		7	posadzka betonowa	100	beton klasy min. C35/45, zbrojenie włóknem rozproszonym 25kg/m3
		8	warstwa wykończeniowa	0	farba poliuretanowa
podłoga na gruncie w garażu nieogrzewanym	PpZ 2a	1	grunt rodzimy		

	2	zagęszczona podsypka piaskowa	300	Is min. 0,98, grubość podbudowy min. 300 mm + do głębokości usuniętego humusu
	3	chudy beton	100	
	4	hydroizolacja		2x papa termozgrzewalna
	5	termoizolacja	0-150	XPS 300, układany w spadku
	6	folia PE		
	7	posadzka betonowa	100	beton klasy min. C35/45, zbrojenie włóknem rozproszonym 25kg/m3
	8	warstwa wykończeniowa	0	farba poliuretanowa

stropodach SOPREMA Dach zielony ekstensywny TUNDRA o tradycyjnym układzie warstw, izolacja wodochronna bitumiczna, dwuwarstwowa, samoprzylepna, na podłożu betonowym z termoizolacją EPS. Broof (t1)

PpZ 3

1 żelbet

150/180/200

Grubość zgodnie z projektem konstrukcji

	2	preparat gruntujący SOPRADERE		
	3	Papa paroizolacyjna MAMUT VAP		
	4	Klej poliuretanowy EFIFOAM		
	5	Termoizolacja SOPRADACH EPS 100	180	Λ 0,036 W/(m·K)
	6	Klej poliuretanowy EFIFOAM		
	7	Kliny spadkowe ze styropianu SOPRADACH EPS 100	20-140	w spadku min. 2%, λ 0,036 W/(m·K), nad parterem w budynkach „A” 20-110
	8	papa podkładowa samoprzylepna SOPRASTICK		
	9	Papa antykorzenna SOPRALENE FLAM JARDIN		
	10	Geowłóknina GEOTEXTILE 300		
	11	Mata drenażowa SOPRADRAIN PLAT F	20	
	12	Włóknina filtracyjna SOPRAFILTRE		
	13	Substrat dachowy SOPRAFLOR PI	100	Zachować maksymalnie 50 cm różnicy wysokości z poziomu wyjścia
	14	Marta wegetacyjna lub sadzonki Tundra		

stropodach SOPREMA Dach o tradycyjnym układzie warstw, izolacja wodochronna bitumiczna, dwuwarstwowa, samoprzylepna, na podłożu betonowym z termoizolacją EPS. Broof (t1)

PpZ 4

1 żelbet

150/180/200

Grubość zgodnie z projektem konstrukcji

	2	preparat gruntujący SOPRADERE		
	3	Papa paroizolacyjna MAMUT VAP		
	4	Klej poliuretanowy EFIFOAM		
	5	Termoizolacja SOPRADACH EPS 100	180	Λ 0,036 W/(m·K)

		6	Klej poliuretanowy EFIFOAM		
		7	Kliny spadkowe ze styropianu SOPRADACH EPS 100	20-140	w spadku min. 2%, λ 0,036 W/(m·K), nad parterem w budynkach „A” 20-110
		8	papa podkładowa samoprzylepna SOPRASTICK		
		9	Papa antykorzenna SOPRALENE FLAM JARDIN		
		10	Geowłóknina GEOTEXTILE 300		
		11	Mata drenażowa SOPRADRAIN PLAT F	20	
		12	Włóknina filtracyjna SOPRAFILTRE		
		13	Żwir płukany	60-200	do wyrównaniu spadku, nad parterem w budynkach „A” 60-110
		14	płyty betonowe	40	
nadwieszenie wykończone blachą	PpZ 5	1	blacha aluminiowa		Prefa nr 10, zielona patyna, na rąbek stojący
		2	deskowanie	20	impregnowane do NRO
		3	szczelina wentylacyjna	25	
		4	termoizolacja/podkonstrukcja	120	kooltherm K15 λ 0,021 W/(m·K), podkonstrukcja drewniana impregnowana NRO
		5	żelbet	180	
		6	styropian akustyczny	15	np. Austrotherm STK EPS T
		7	styropian		EPS.100 λ 0,036 W/(m·K)
		8	folia do ogrzewania podłogowego		
		9	wylewka anhydrytowa	60	
		10	wykończenie	20	
nadwieszenie wykończone tynkiem gładkim	PpZ 6	1	tynk gładki	10	kolor szary, matowy
		2	termoizolacja	180	styropian λ 0,031 W/(m·K)
		3	żelbet	180	
		4	styropian akustyczny	30	np. Austrotherm STK EPS T
		5	styropian	40	EPS.100 λ 0,036 W/(m·K)
		6	folia do ogrzewania podłogowego		
		7	wylewka betonowa	60	
		8	wykończenie	20	

stropodach SOPREMA Dach
zielony ekstensywny
TUNDRA o tradycyjnym
układzie warstw, izolacja
wodoszczelna bitumiczna,
dwuwarstwowa,
samoprzylepna, na podłożu
betonowym z termoizolacją
EPS. Broof (t1)

PpZ 7

1 żelbet

200

2 preparat gruntujący SOPRADERE

3 Papa paroizolacyjna MAMUT VAP

4 Klej poliuretanowy EFIFOAM

5 Termoizolacja SOPRADACH EPS 100 180 Λ 0,036 W/(m·K)

6 Klej poliuretanowy EFIFOAM

7 Klíny spadkowe ze styropianu SOPRADACH EPS 100 20-160 w spadku min. 1,5%, Λ 0,036 W/(m·K)

8 papa podkładowa samoprzylepna SOPRASTICK

9 Papa antykorzenna SOPRALENE FLAM JARDIN

10 Geowłóknina GEOTEXTILE 300

11 Mata drenażowa SOPRADRAIN PLAT F 20

12 Włóknina filtracyjna SOPRAFILTRE

13 Substrat dachowy SOPRAFLOR PI 100 Zachować maksymalnie 50 cm różnicy wysokości z poziomu wyjścia

14 Marta wegetacyjna lub sadzonki Tundra

stropodach SOPREMA Dach
zielony ekstensywny
TUNDRA o tradycyjnym
układzie warstw, izolacja
wodoszczelna bitumiczna,
dwuwarstwowa,
samoprzylepna, na podłożu
betonowym z termoizolacją
EPS. Broof (t1)

PpZ 8

1 żelbet

150

Grubość zgodnie z projektem konstrukcji

2 preparat gruntujący SOPRADERE

3 Papa paroizolacyjna MAMUT VAP

4 Klej poliuretanowy EFIFOAM

5 Klíny spadkowe ze styropianu SOPRADACH EPS 100 50-150 w spadku min. 2%

6 papa podkładowa samoprzylepna SOPRASTICK

7 Papa antykorzenna SOPRALENE FLAM JARDIN

8 Geowłóknina GEOTEXTILE 300

9 Mata drenażowa SOPRADRAIN PLAT F 20

10 Włóknina filtracyjna SOPRAFILTRE

11 Substrat dachowy SOPRAFLOR PI 230-330 do wyrównania spadku

12 Marta wegetacyjna lub sadzonki Tundra

dojście przy schodach zewnętrznych	PpZ 9	1	żelbet w spadku	180-230	Min. 2%
		2	wylewka betonowa w spadku	40-90	Min. 2%
		3	hydroizolacja		2x papa, antykorzenna
		4	XPS	20mm	
		5	Podbudowa w kruszywa	150-200	do wyrównaniu spadku
		6	Kostka brukowa	60	

PRZEGRODA POZIOMA WEWNĘTRZNA

FUNKCJA	NAZWA	NR	WARSTWY	GR. (MM)	DODATKOWE PARAMETRY
strop	PpW 1	1	tynk	10	
		2	żelbet	180/200	Grubość zgodnie z projektem konstrukcji
		3	styropian akustyczny	15	np. Austrotherm STK EPS T
		4	styropian		EPS.100 λ 0,036 W/(m·K)
		5	folia do ogrzewania podłogowego		
		6	wylewka betonowa	60	
		8	wykończenie	20	
schody betonowe	PpW 2	1	tynk	10	
		2	żelbet		Grubość zgodnie z projektem konstrukcji
		3	styropian akustyczny	20	np. Austrotherm STK EPS T
		4	wylewka wyrównawcza	40	
		5	wykończenie	20	

ŚCIANY ZEWNĘTRZNE


FUNKCJA	NAZWA	NR	WARSTWY	GR. (MM)	DODATKOWE PARAMETRY
ściana murowana lub żelbetowa, tynkowana	ŚcZ 1	1	tynk	10	
		2	błoczki silikatowe lub żelbet	180	
		3	termoizolacja	180	styropian λ 0,031 W/(m·K)
		4	tynk gładki	10	kolor szary, matowy
ściana murowana lub żelbetowa, tynkowana, gładka	ŚcZ 2	1	tynk	10	
		2	błoczki silikatowe lub żelbet	180	
		3	termoizolacja	180	styropian λ 0,031 W/(m·K)
		4	tynk	10	kolor szary, matowy

ściana murowana lub żelbetowa, podziemna	ŚcZ 3	1	tynk	10	
		2	błoczki silikatowe, betonowe lub żelbet	180	
		3	hydroizolacja		
		4	termoizolacja	160	XPS λ 0,031 W/(m·K)
		5	folia kubetkowa		
ściana murowana lub żelbetowa, garaż	ŚcZ 4	1	błoczki silikatowe, lub żelbet	180	
		2	termoizolacja	40	warstwa wyrównawcza
		3	tynk gładki	10	kolor szary, matowy
ściana oporowa	ŚcZ 5	1	hydroizolacja		
		2	żelbet	-	Grubość zgodnie z projektem konstrukcji
		3	tynk gładki	10	kolor szary, matowy
ściana murowana lub żelbetowa z okładziną z blachy	ŚcZ 6	1	tynk	10	
		2	błoczki silikatowe lub żelbet	180	
		3	termoizolacja/podkonstrukcja	140	kooltherm K15 λ 0,021 W/(m·K), podkonstrukcja drewniana impregnowana NRO
		4	szczelina wentylacyjna	30	
		5	deskowanie	20	impregnowane do NRO
		6	blacha aluminiowa		Prefa nr 10, zielona patyna, na rąbek stojący
ściana murowana lub żelbetowa, podziemna garażu	ŚcZ 7	1	błoczki silikatowe, betonowe lub żelbet	180	
		2	hydroizolacja		
		3	folia kubetkowa		
ściana fundamentowa	ŚcZ 8	1	hydroizolacja		
		2	błoczki betonowe lub żelbet	180	
		3	hydroizolacja		
		4	termoizolacja	160	XPS λ 0,031 W/(m·K)
		5	folia kubetkowa		
ściana fundamentowa	ŚcZ 9	1	hydroizolacja		





		2	błoczki betonowe lub żelbet	180	
		3	hydroizolacja		
ściana przy schodach	ŚCZ 10	1	tynk gładki	10	kolor szary, matowy
		2	termoizolacja	40	styropian
		3	błoczki silikatowe lub żelbet	180	
		4	termoizolacja	40	styropian
		5	tynk gładki	10	kolor szary, matowy
ściana murowana lub żelbetowa, tynkowana	ŚCZ 11	1	błoczki silikatowe lub żelbet	180	
		2	termoizolacja	180	styropian λ 0,031 W/(m·K)
		3	tynk gładki	10	kolor szary, matowy
ŚCIANY WEWNĘTRZNE					
FUNKCJA	NAZWA	NR	WARSTWY	GR. (MM)	DODATKOWE PARAMETRY
ściana nośna	ŚCW 1	1	tynk	10	
		2	błoczki silikatowe lub żelbet	180	
		3	tynk	10	
ściana działowa	ŚCW 2	1	tynk	10	
		2	błoczki silikatowe	80	
		3	tynk	10	
ściany bliźniacze	ŚCW 3	1	tynk	10	
		2	błoczki silikatowe	180	akustyczne np. Silka E18A
		3	termoizolacja	20	min. λ 0,031 W/(m·K)
		4	dylatacja	10	wypełnienie ze styropianu
		5	termoizolacja	20	min. λ 0,031 W/(m·K)
		6	błoczki silikatowe	180	akustyczne np. Silka E18A
		7	tynk	10	
ściana ocieplona	ŚCW 4	1	tynk	10	
		2	błoczki silikatowe lub żelbet	180	
		3	termoizolacja	60	wełna skalna λ 0,042 W/(m·K)
		4	tynk	10	
ściana nośna	ŚCW 5	1	błoczki silikatowe lub żelbet	180	

15. Opis technologii systemu tarasu i stropodachu zielonego (biologicznie czynnego)

Planuje się realizację stropodachów i tarasów zielonych w technologii firmy Soprema. System ten poza standardowymi warstwami izolacji termicznej i wodnej posiada maty drenażowe oraz włókniny filtracyjne, na które rozkładany jest substrat zapewniający retencję wody oraz naturalną roślinność. SOPREMA oferuje substraty SOPRAFLOR przeznaczone do zakładania zieleni na dachach. Można je stosować już od grubości ok. 5 cm. Ich struktura należy do bardzo stabilnych, o dużej zawartości części mineralnych. To przede wszystkim w substracie zachodzi retencja wody. Rośliny korzenią się w substracie. Jest to typowe i powszechnie stosowane rozwiązanie systemowe.

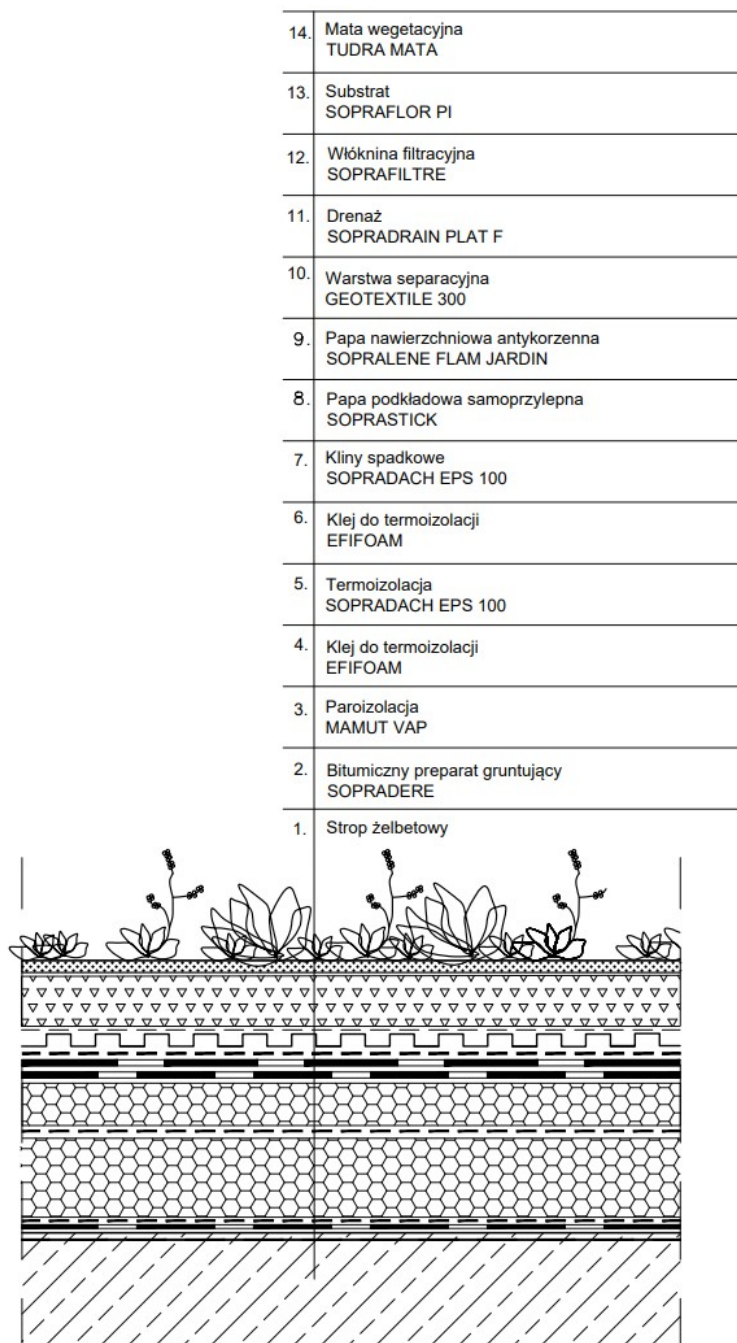

Rysunek przekroju systemu opracowano przez Soprema Polska.

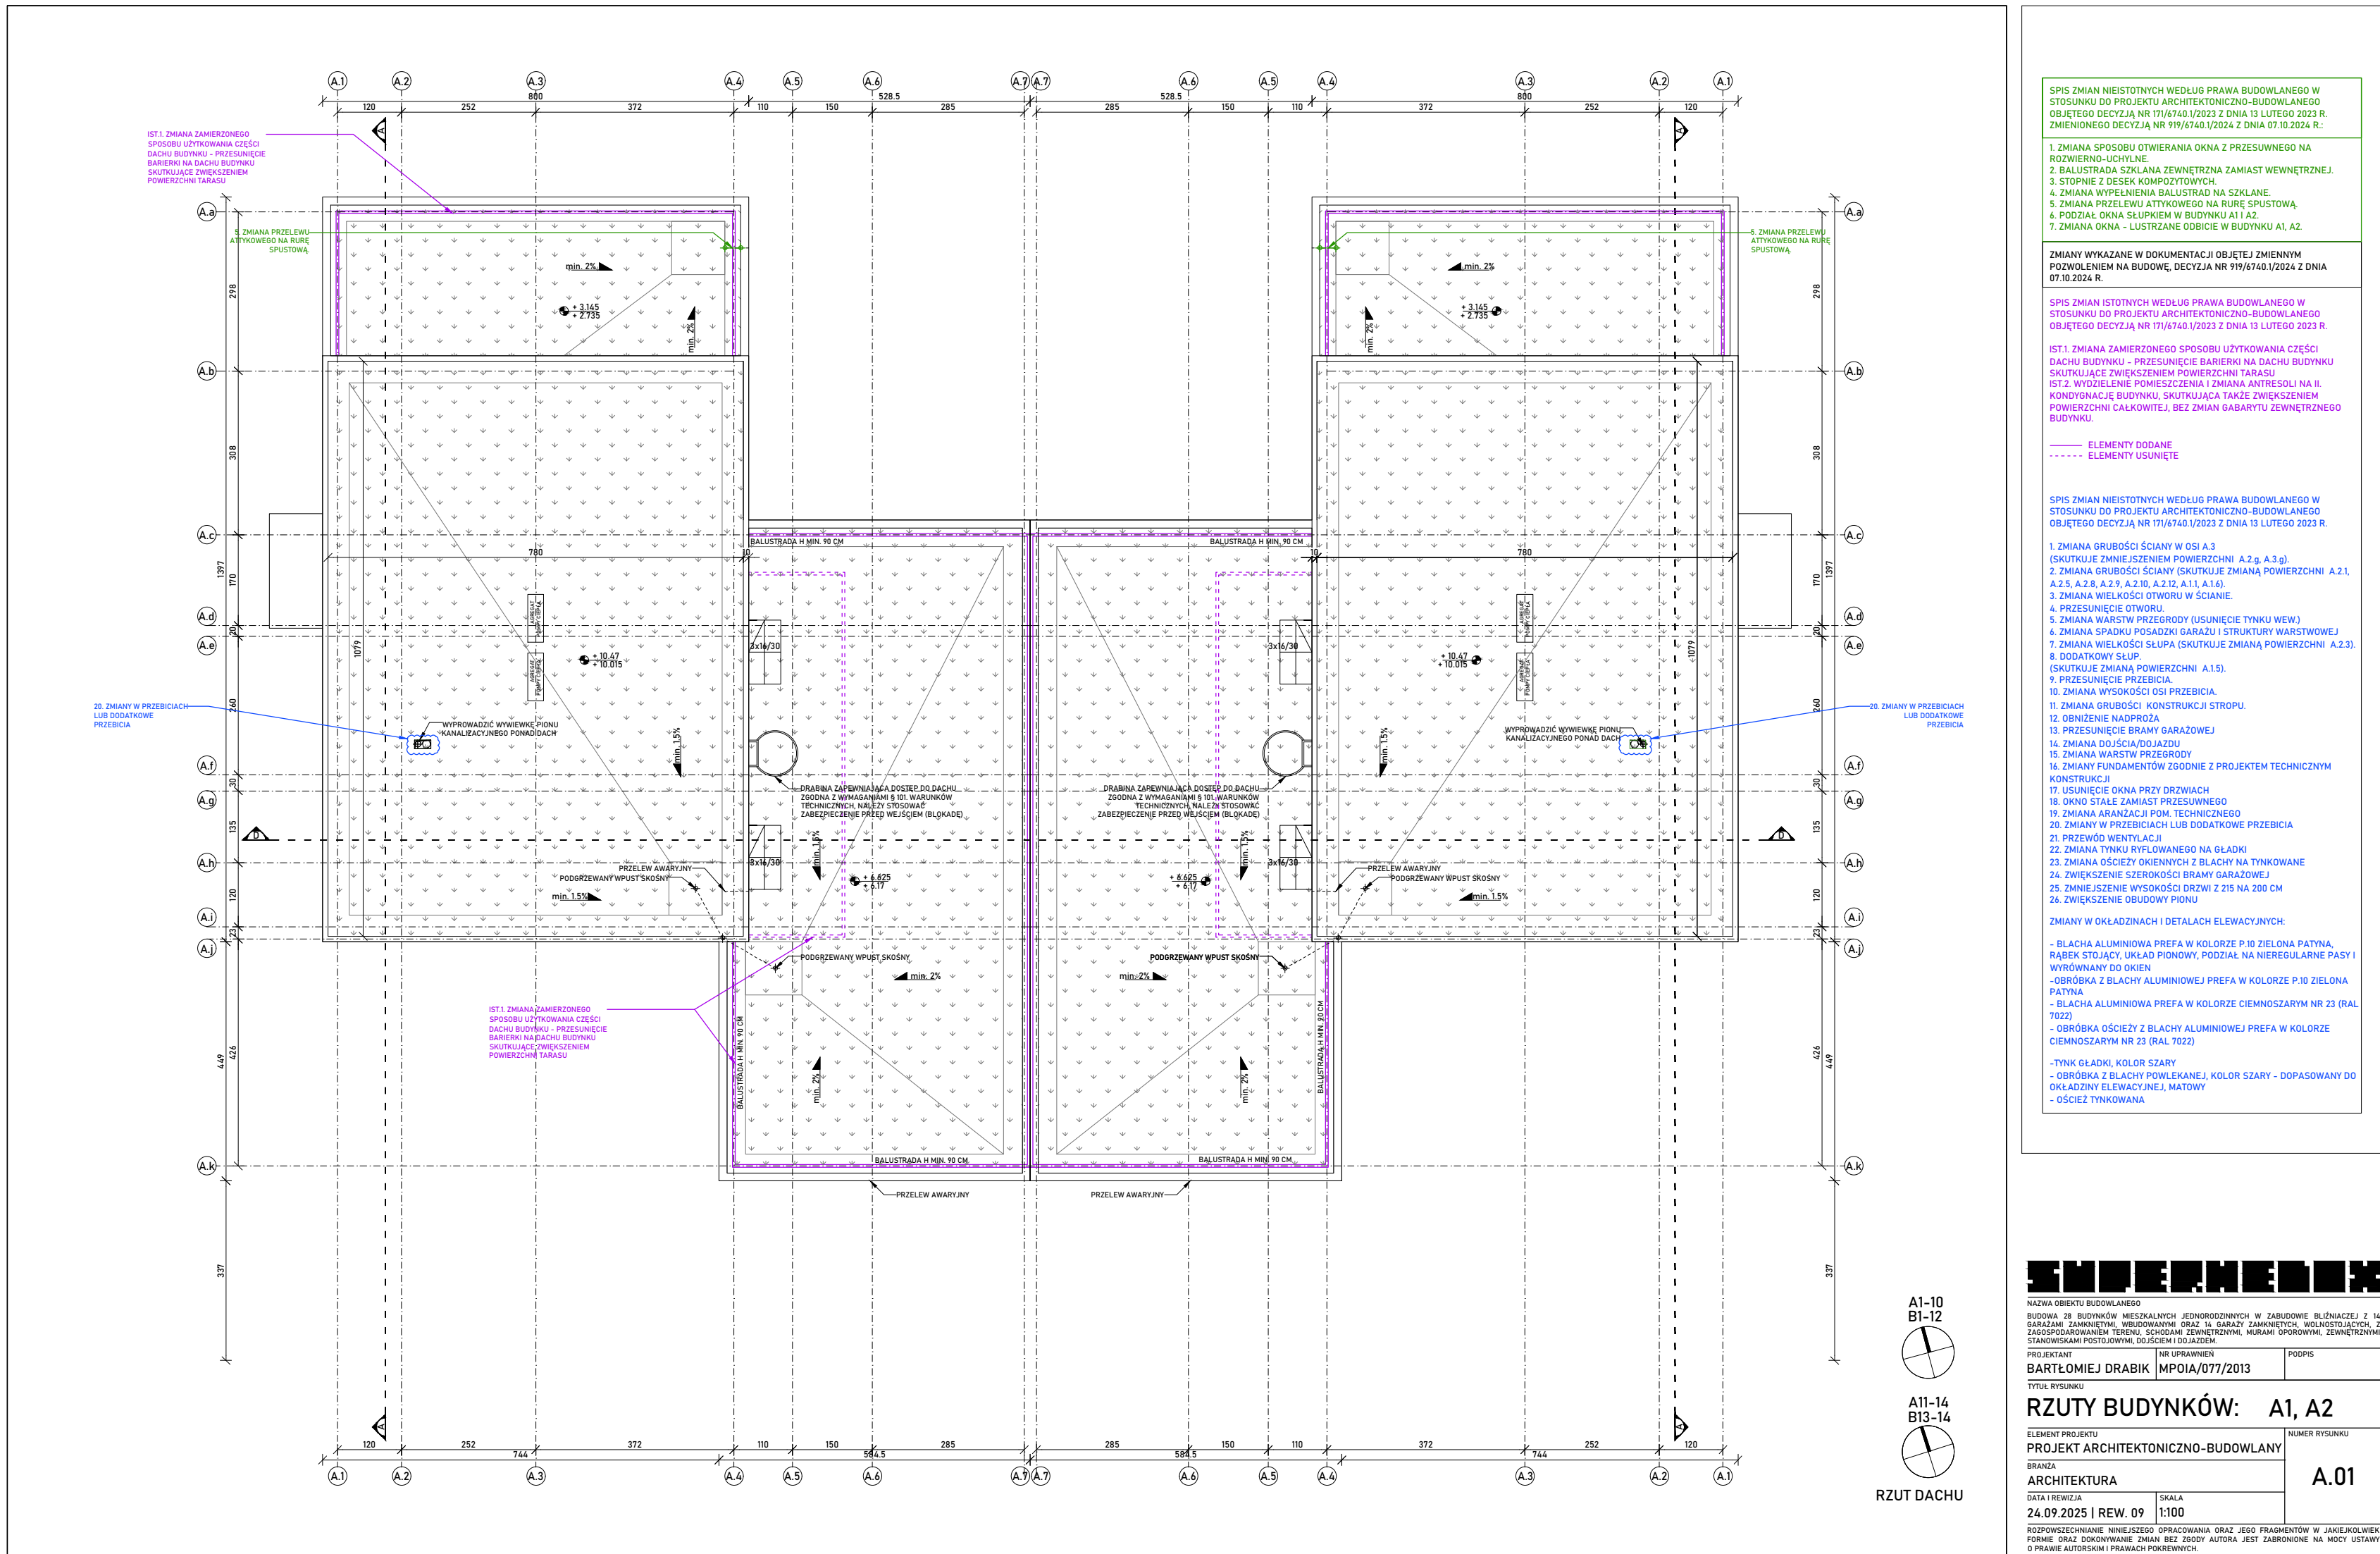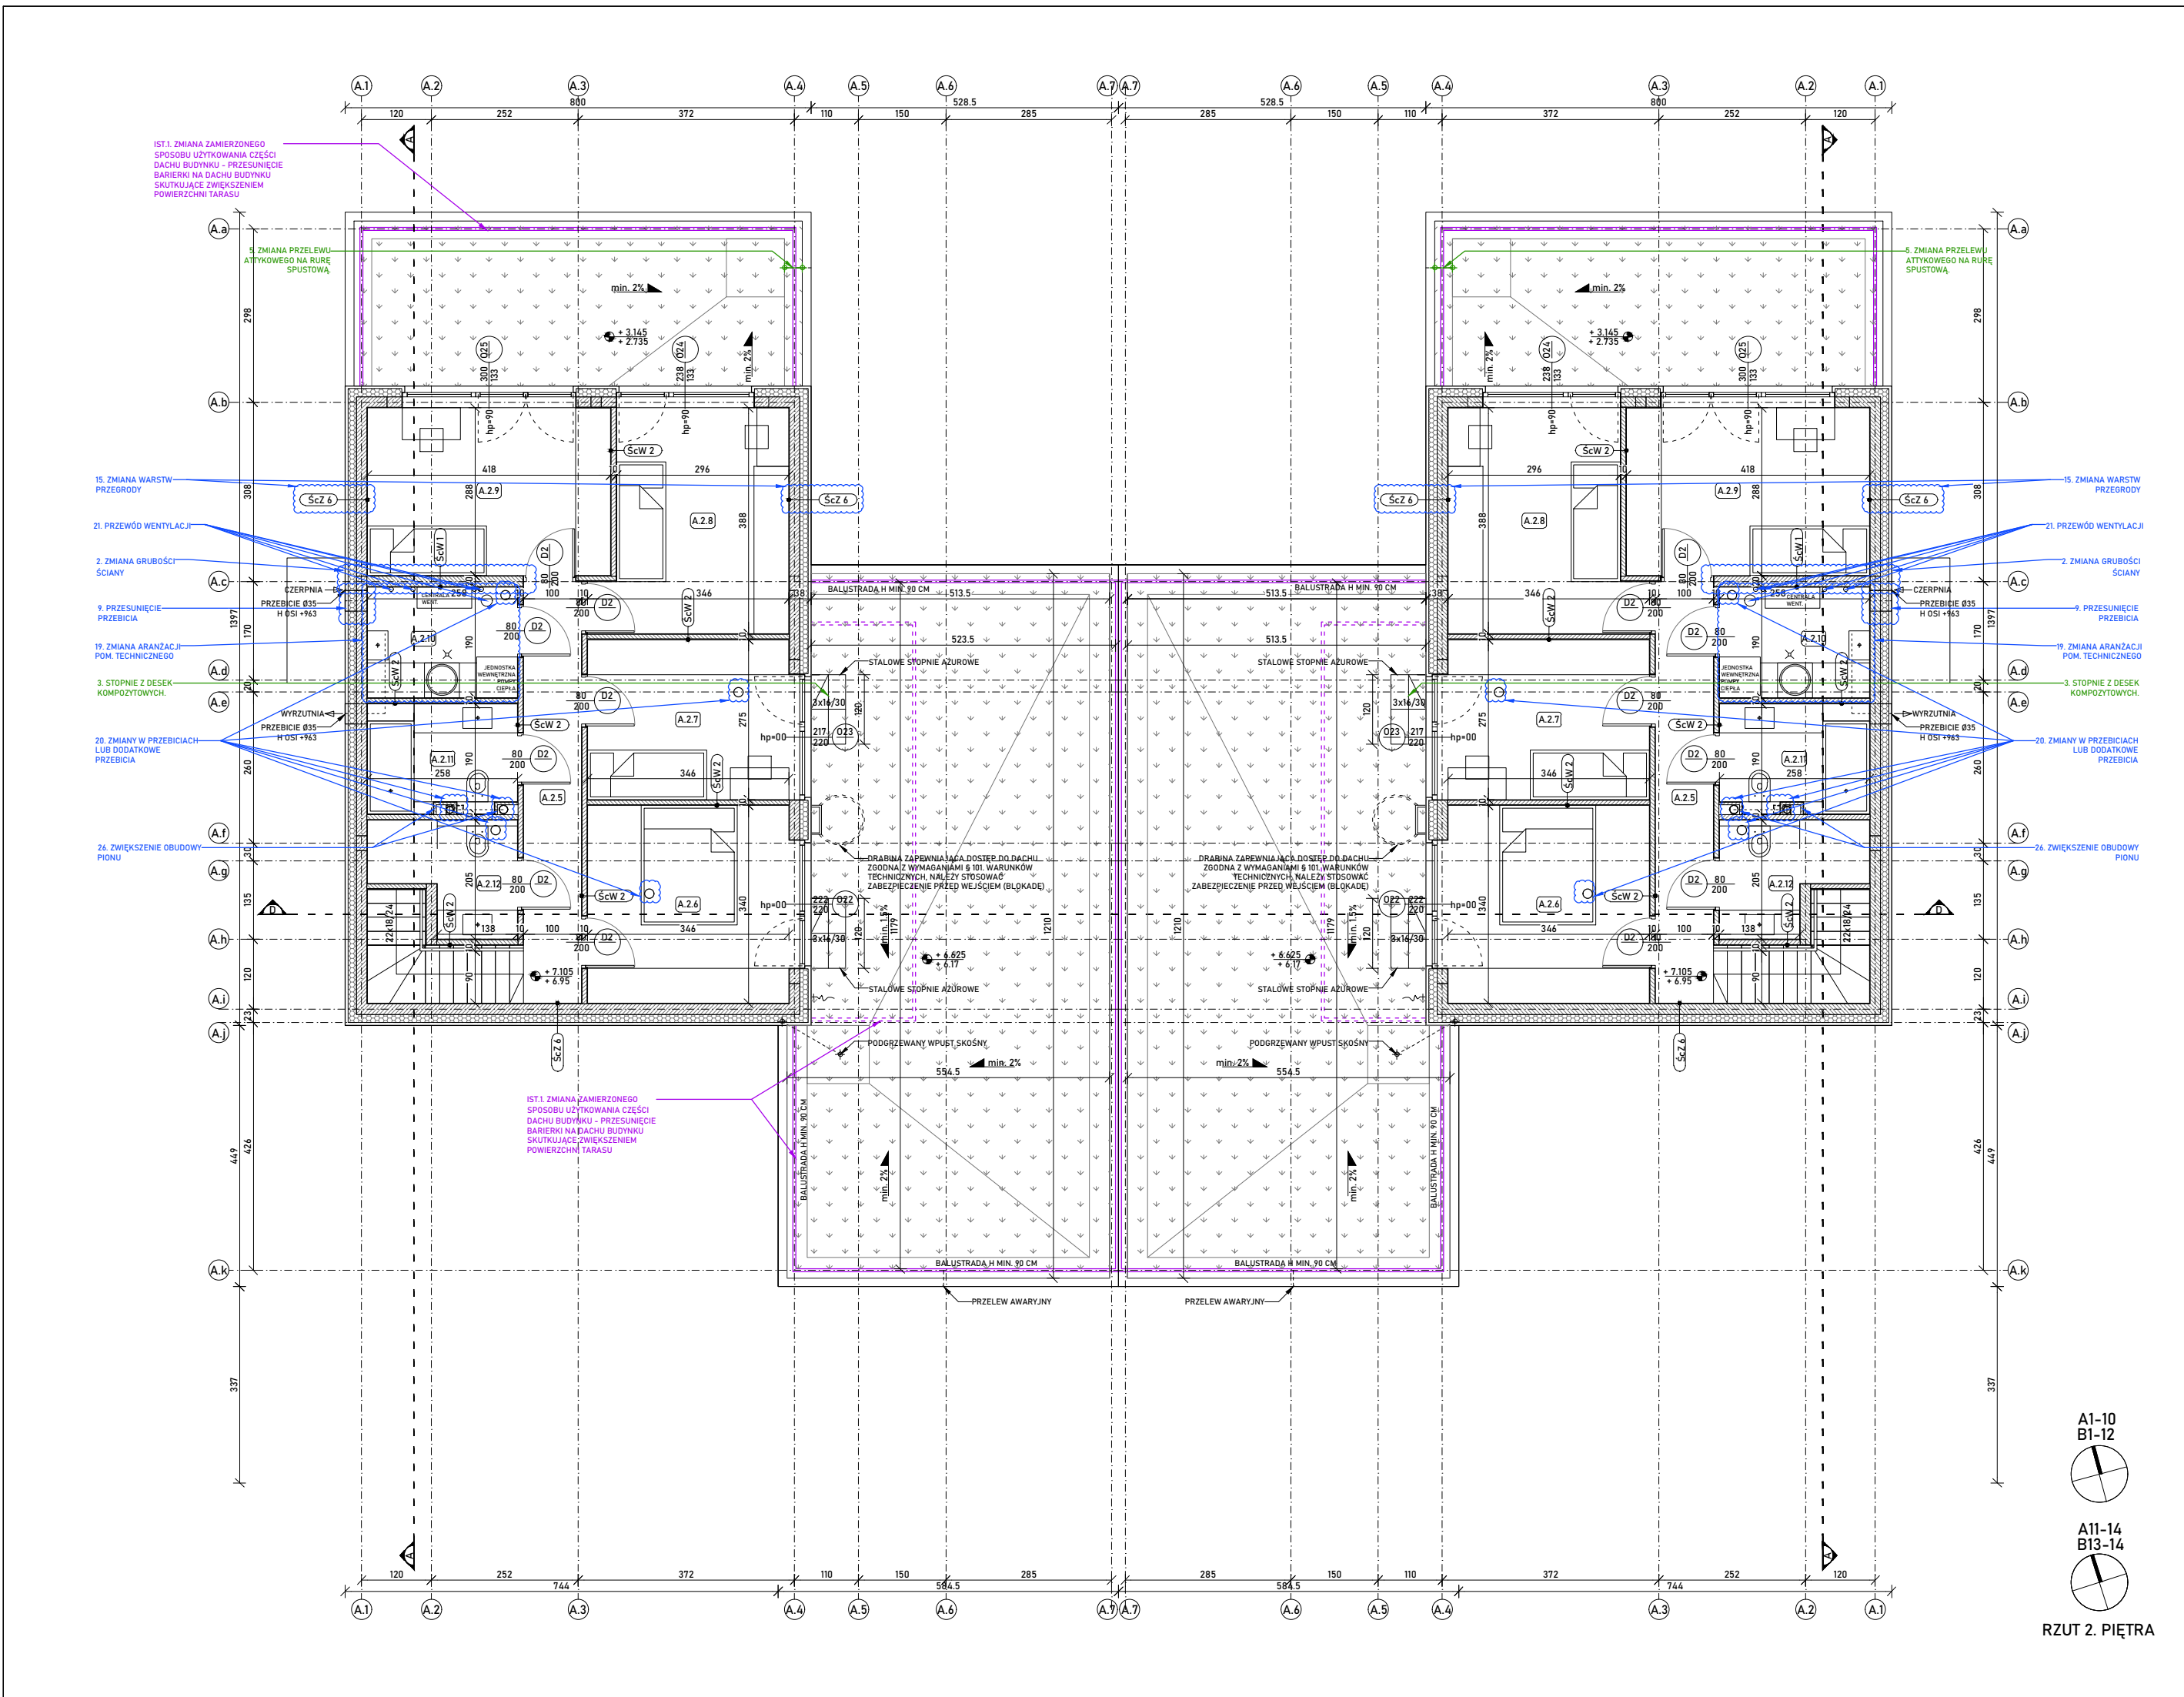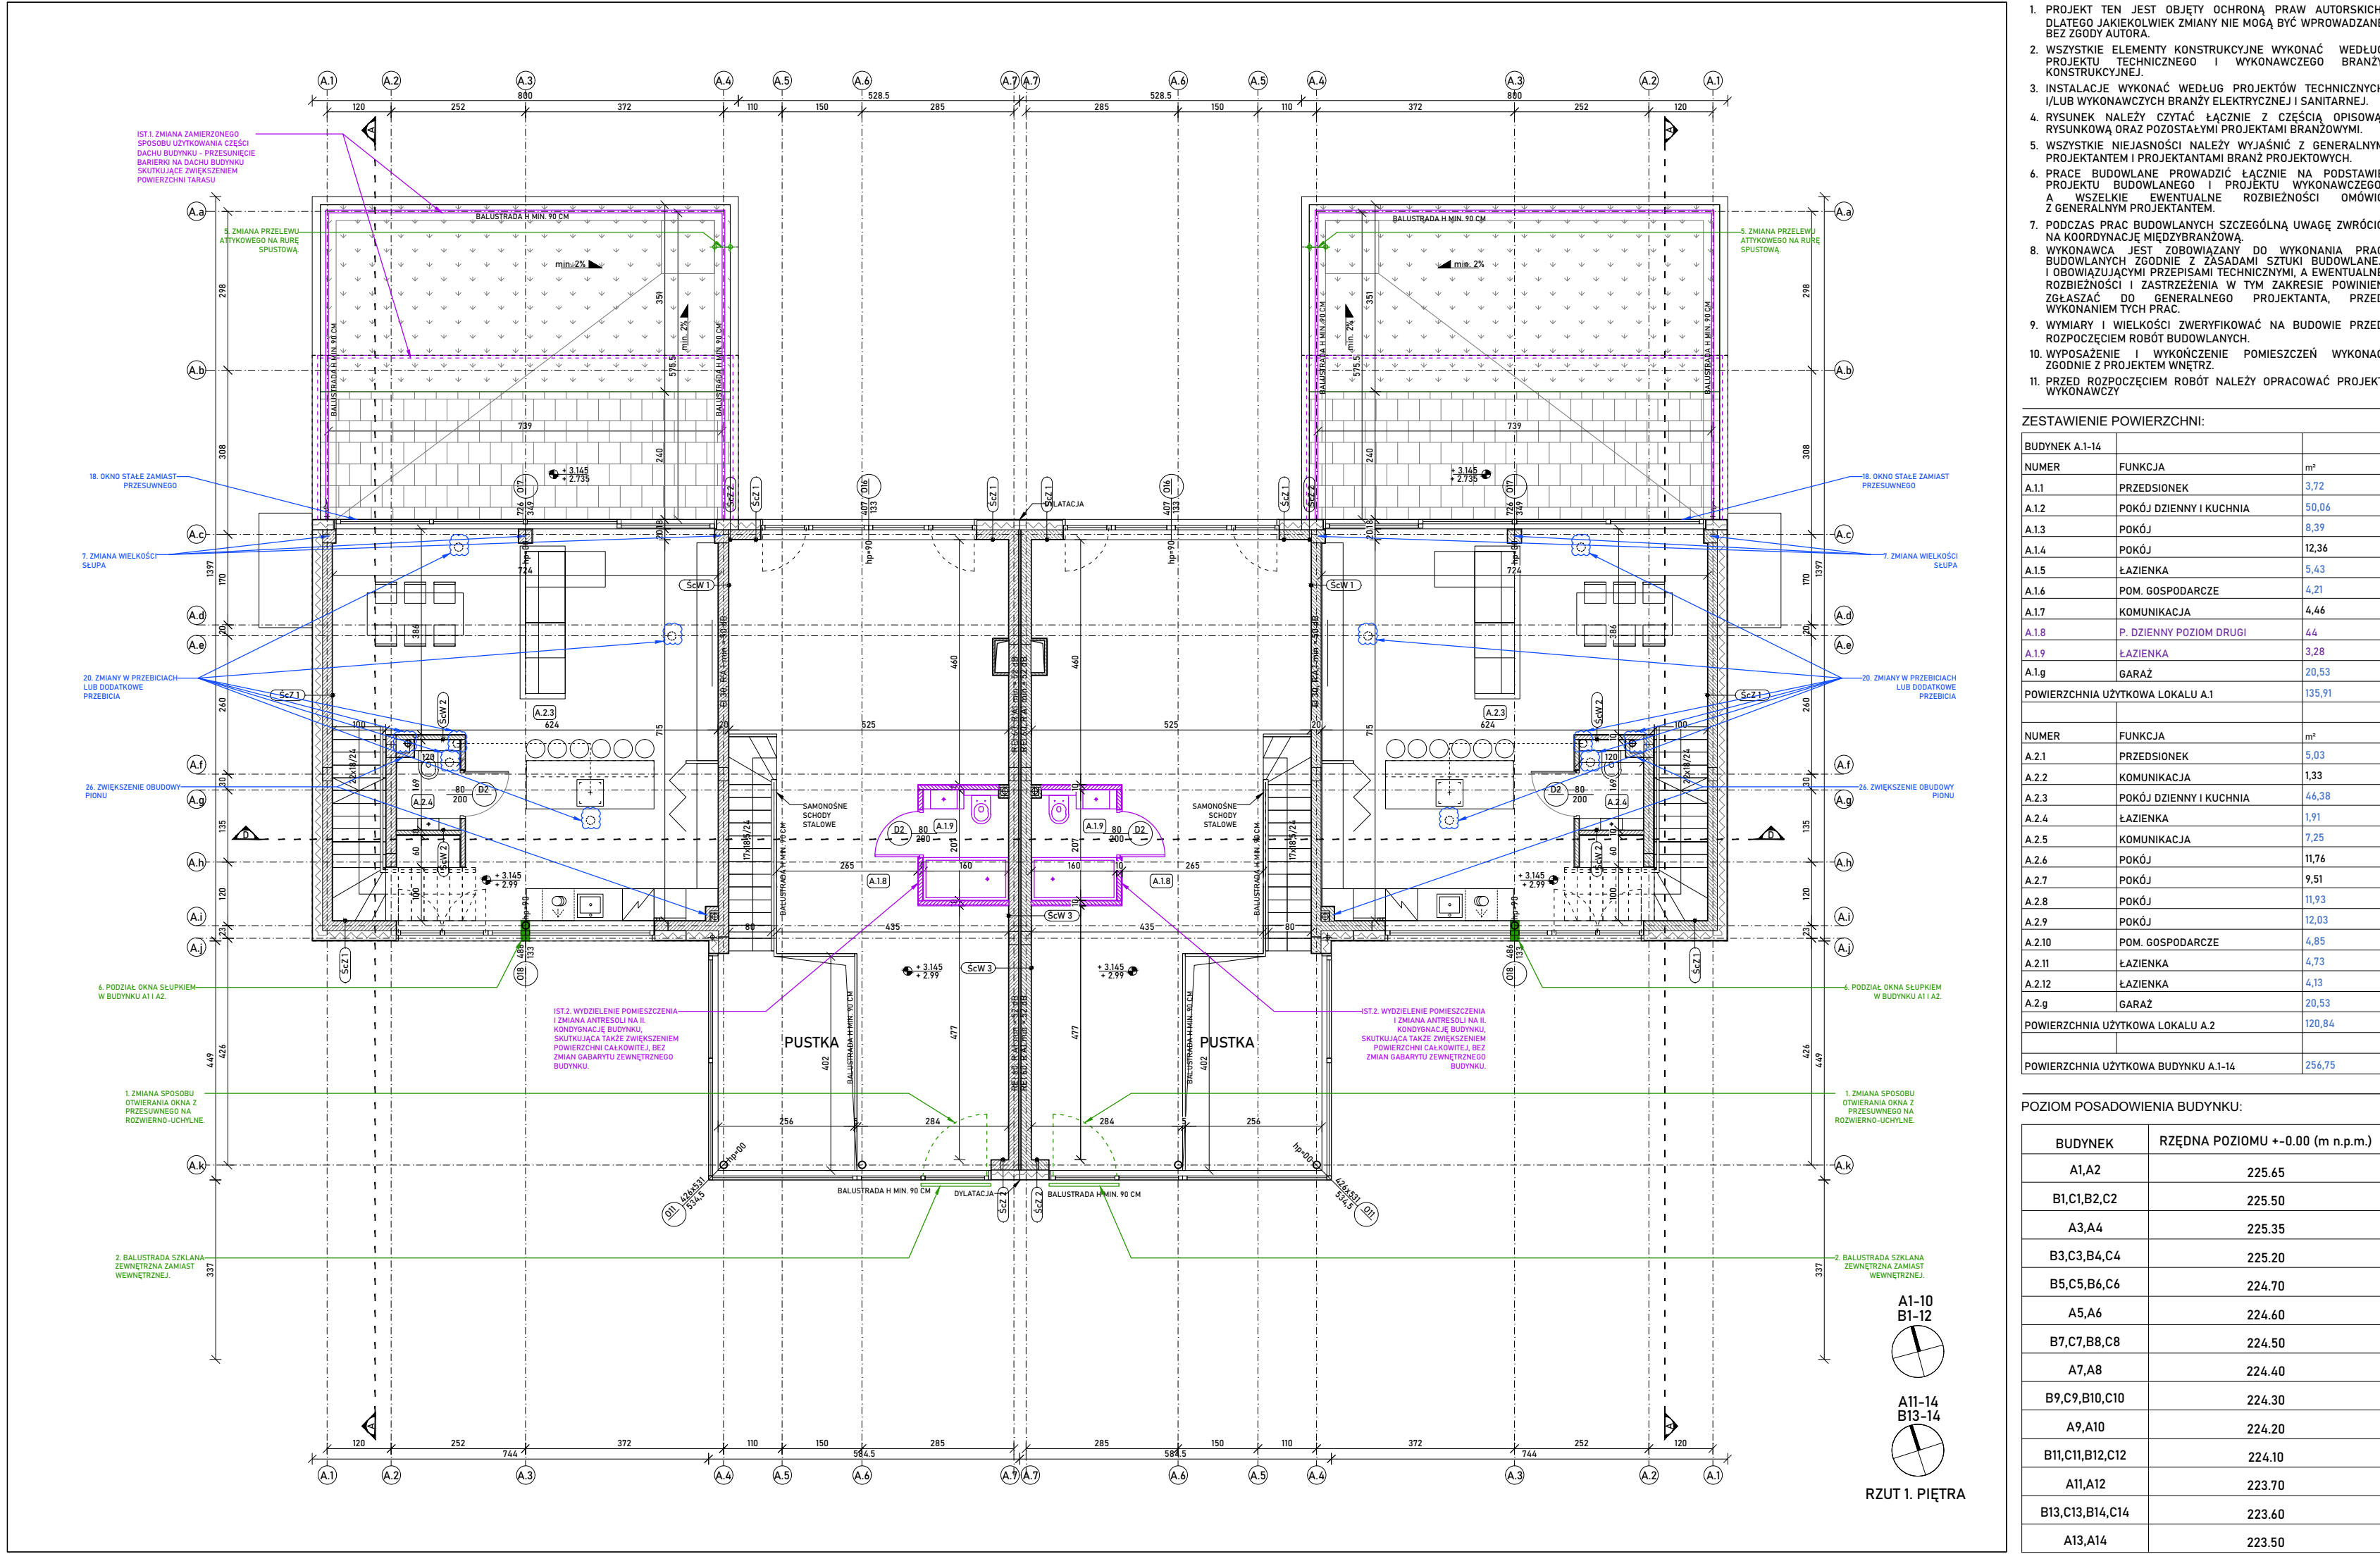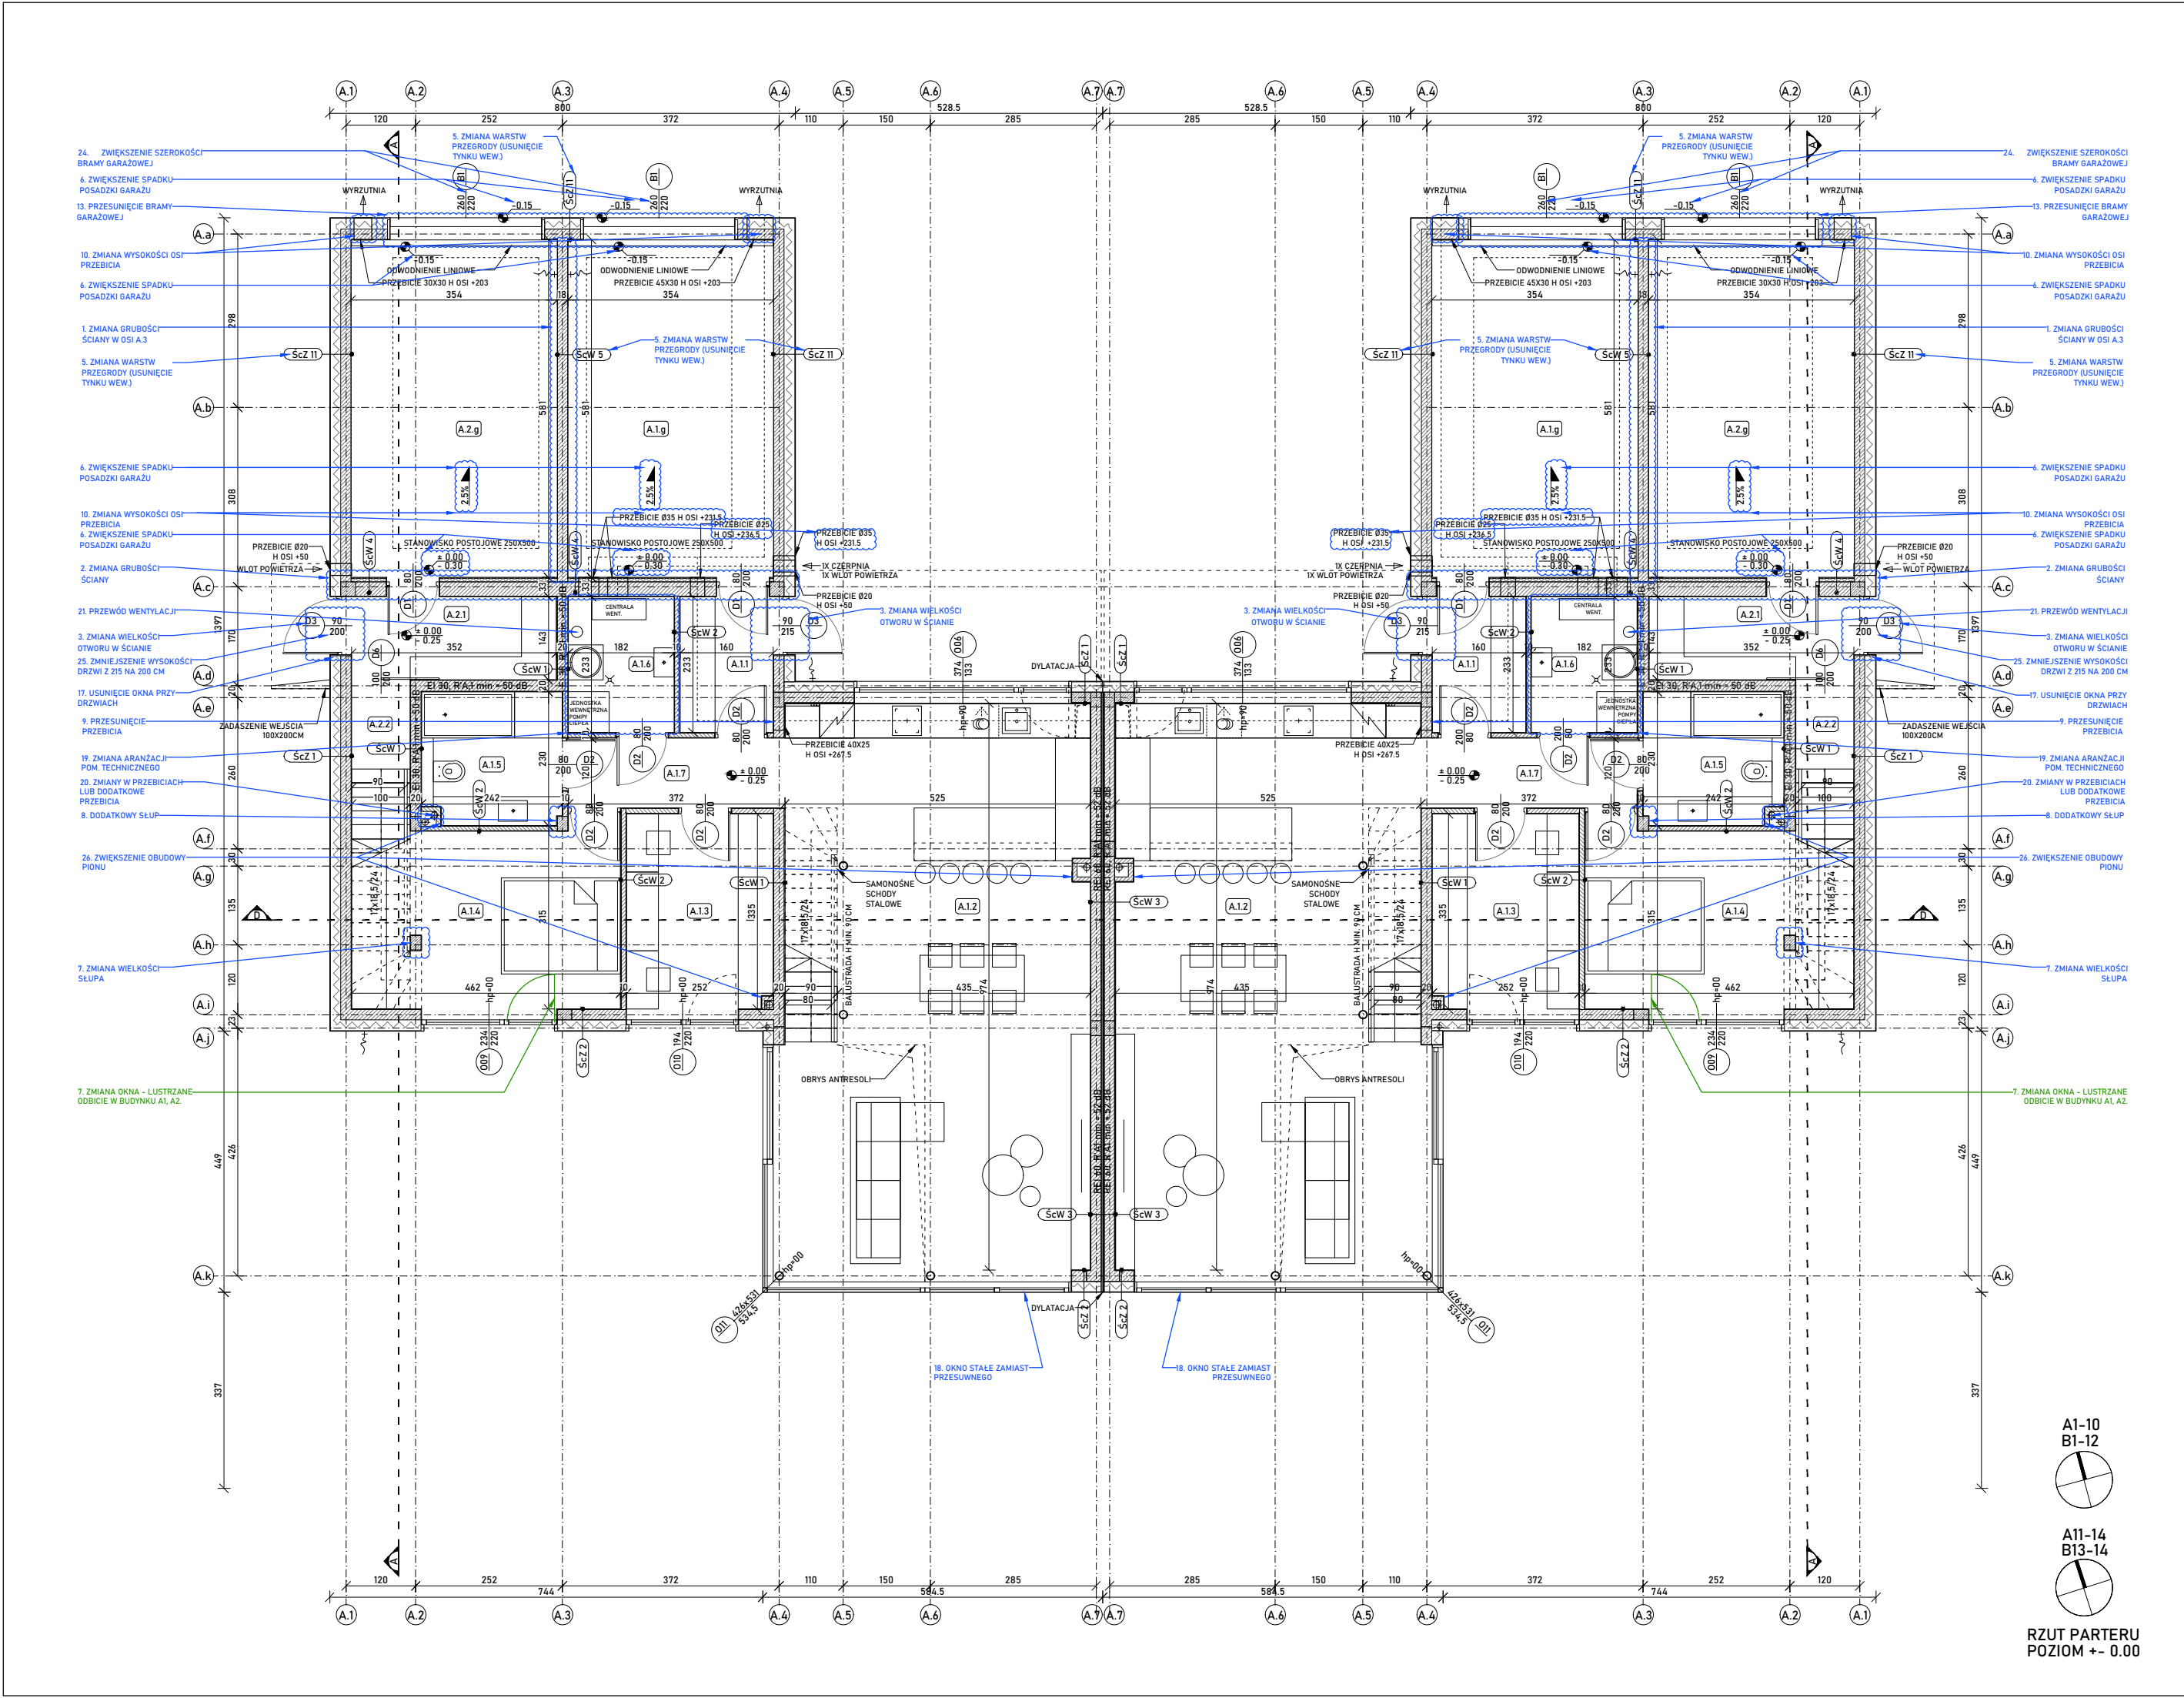

1. PROJEKT JEST OBJEKT OCHRONY, PRAW AUTORSKICH, BŁAGODZIEMNYCH, ZNANY NIE MOGA BYĆ WYKONYWANE BEZ ZGODY AUTORA.	
2. WSKAZANE ELEMENTY KONSTRUKCYJNE WYKONAĆ WEDŁUG PROJEKTU TECHNICZNEGO I WYKONAWCZEGO KONSTRUKCJI.	
3. INSTALACJE WYKONAĆ WEDŁUG PROJEKTU TECHNICZNEGO I LUB WYKONAWCZEGO BRANŻY ELEKTRYCZNEJ I SANITARNEJ.	
4. RYSUNEK NALEŻY CZYTAĆ ŁĄCZNIE Z CZĘŚCIĄ SPISOWĄ, RYSUNKOWĄ ORAZ PODZIAŁAMI PROJEKTAMI BRANŻOWYMI.	
5. WSKAZANE NIEJASNOŚCI NALEŻY WYJAŚNIĆ Z GENERALNYM PROJEKTEM I PROJEKTAMI BRANŻOWYMI.	
6. PRACE BUDOWLANE PRACOWNIKI NALEŻY WYKONYWAĆ W ZGODNIE Z PROJEKTEM I PROJEKTAMI BRANŻOWYMI.	
7. PODCZAS PRAC BUDOWLANICH SZCZEGÓLNĄ UWAGĘ ZWRÓCIĆ NA KONTROLĘ WYKONANIA PRAC.	
8. WYKONAWCA JEST ZOBOWIĄZANY DO WYKONANIA PRAC BUDOWLANICH ZGODNIE Z ZASADAMI SZTETNY BUDOWLANEJ I OBLADZAJĄCYMI PRZEPISAMI TECHNICZNYMI, A EWENTUALNE ROZBIEŻNOŚCI I ZASTĘPIENIA W TM ZAKREŚLENIU POWINNY ZŁAGASZCZĄĆ DO GENERALNEGO PROJEKTANTA, PRZED WYKONANIEM TYCH PRAC.	
9. WYMIARY I WIELKOŚCI ZWERYFIKOWAĆ NA BUDOWIE PRZED ROZPOCZĘCIEM ROBÓT BUDOWLANICH.	
10. WYPOSAŻENIE I WYKONANIE POMIESZCZENI WYKONAĆ ZGODNIE Z PROJEKTEM WNEŹ.	
11. PRZED ROZPOCZĘCIEM ROBÓT NALEŻY OPRAWIĆ PROJEKT WYKONAWCZY.	
ZESTAWIENIE POWIERZCHNI:	
BUDYNEK A1-14	
NUMER	FUNKCJA
A1.1	PRZEDSIÓDEK
A1.2	POM. DZIENNY KUCHNIA
A1.3	POM. DZIENNY KUCHNIA
A1.4	POM. DZIENNY KUCHNIA
A1.5	ŁAZIENKA
A1.6	POM. GOSPODARCZE
A1.7	KOMUNIKACJA
A1.8	P. DZIENNY POZIOM DRUGI
A1.9	ŁAZIENKA
A1.10	GARAŻ
POWIERZCHNIA UŻYTKOWA LOKALU A1	
NUMER	FUNKCJA
A2.1	PRZEDSIÓDEK
A2.2	KOMUNIKACJA
A2.3	POM. DZIENNY KUCHNIA
A2.4	ŁAZIENKA
A2.5	KOMUNIKACJA
A2.6	POM. DZIENNY KUCHNIA
A2.7	POM. DZIENNY KUCHNIA
A2.8	POM. DZIENNY KUCHNIA
A2.9	POM. DZIENNY KUCHNIA
A2.10	POM. GOSPODARCZE
A2.11	ŁAZIENKA
A2.12	ŁAZIENKA
A2.13	GARAŻ
POWIERZCHNIA UŻYTKOWA LOKALU A2	
NUMER	FUNKCJA
A3.1	PRZEDSIÓDEK
A3.2	KOMUNIKACJA
A3.3	POM. DZIENNY KUCHNIA
A3.4	ŁAZIENKA
A3.5	KOMUNIKACJA
A3.6	POM. DZIENNY KUCHNIA
A3.7	POM. DZIENNY KUCHNIA
A3.8	POM. DZIENNY KUCHNIA
A3.9	POM. DZIENNY KUCHNIA
A3.10	POM. GOSPODARCZE
A3.11	ŁAZIENKA
A3.12	ŁAZIENKA
A3.13	GARAŻ
POWIERZCHNIA UŻYTKOWA LOKALU A3	
NUMER	FUNKCJA
A4.1	PRZEDSIÓDEK
A4.2	KOMUNIKACJA
A4.3	POM. DZIENNY KUCHNIA
A4.4	ŁAZIENKA
A4.5	KOMUNIKACJA
A4.6	POM. DZIENNY KUCHNIA
A4.7	POM. DZIENNY KUCHNIA
A4.8	POM. DZIENNY KUCHNIA
A4.9	POM. DZIENNY KUCHNIA
A4.10	POM. GOSPODARCZE
A4.11	ŁAZIENKA
A4.12	ŁAZIENKA
A4.13	GARAŻ
POWIERZCHNIA UŻYTKOWA LOKALU A4	
NUMER	FUNKCJA
A5.1	PRZEDSIÓDEK
A5.2	KOMUNIKACJA
A5.3	POM. DZIENNY KUCHNIA
A5.4	ŁAZIENKA
A5.5	KOMUNIKACJA
A5.6	POM. DZIENNY KUCHNIA
A5.7	POM. DZIENNY KUCHNIA
A5.8	POM. DZIENNY KUCHNIA
A5.9	POM. DZIENNY KUCHNIA
A5.10	POM. GOSPODARCZE
A5.11	ŁAZIENKA
A5.12	ŁAZIENKA
A5.13	GARAŻ
POWIERZCHNIA UŻYTKOWA LOKALU A5	
NUMER	FUNKCJA
A6.1	PRZEDSIÓDEK
A6.2	KOMUNIKACJA
A6.3	POM. DZIENNY KUCHNIA
A6.4	ŁAZIENKA
A6.5	KOMUNIKACJA
A6.6	POM. DZIENNY KUCHNIA
A6.7	POM. DZIENNY KUCHNIA
A6.8	POM. DZIENNY KUCHNIA
A6.9	POM. DZIENNY KUCHNIA
A6.10	POM. GOSPODARCZE
A6.11	ŁAZIENKA
A6.12	ŁAZIENKA
A6.13	GARAŻ
POWIERZCHNIA UŻYTKOWA LOKALU A6	
NUMER	FUNKCJA
A7.1	PRZEDSIÓDEK
A7.2	KOMUNIKACJA
A7.3	POM. DZIENNY KUCHNIA
A7.4	ŁAZIENKA
A7.5	KOMUNIKACJA
A7.6	POM. DZIENNY KUCHNIA
A7.7	POM. DZIENNY KUCHNIA
A7.8	POM. DZIENNY KUCHNIA
A7.9	POM. DZIENNY KUCHNIA
A7.10	POM. GOSPODARCZE
A7.11	ŁAZIENKA
A7.12	ŁAZIENKA
A7.13	GARAŻ
POWIERZCHNIA UŻYTKOWA LOKALU A7	
NUMER	FUNKCJA
A8.1	PRZEDSIÓDEK
A8.2	KOMUNIKACJA
A8.3	POM. DZIENNY KUCHNIA
A8.4	ŁAZIENKA
A8.5	KOMUNIKACJA
A8.6	POM. DZIENNY KUCHNIA
A8.7	POM. DZIENNY KUCHNIA
A8.8	POM. DZIENNY KUCHNIA
A8.9	POM. DZIENNY KUCHNIA
A8.10	POM. GOSPODARCZE
A8.11	ŁAZIENKA
A8.12	ŁAZIENKA
A8.13	GARAŻ
POWIERZCHNIA UŻYTKOWA LOKALU A8	
NUMER	FUNKCJA
A9.1	PRZEDSIÓDEK
A9.2	KOMUNIKACJA
A9.3	POM. DZIENNY KUCHNIA
A9.4	ŁAZIENKA
A9.5	KOMUNIKACJA
A9.6	POM. DZIENNY KUCHNIA
A9.7	POM. DZIENNY KUCHNIA
A9.8	POM. DZIENNY KUCHNIA
A9.9	POM. DZIENNY KUCHNIA
A9.10	POM. GOSPODARCZE
A9.11	ŁAZIENKA
A9.12	ŁAZIENKA
A9.13	GARAŻ
POWIERZCHNIA UŻYTKOWA LOKALU A9	
NUMER	FUNKCJA
A10.1	PRZEDSIÓDEK
A10.2	KOMUNIKACJA
A10.3	POM. DZIENNY KUCHNIA
A10.4	ŁAZIENKA
A10.5	KOMUNIKACJA
A10.6	POM. DZIENNY KUCHNIA
A10.7	POM. DZIENNY KUCHNIA
A10.8	POM. DZIENNY KUCHNIA
A10.9	POM. DZIENNY KUCHNIA
A10.10	POM. GOSPODARCZE
A10.11	ŁAZIENKA
A10.12	ŁAZIENKA
A10.13	GARAŻ
POWIERZCHNIA UŻYTKOWA LOKALU A10	
NUMER	FUNKCJA
A11.1	PRZEDSIÓDEK
A11.2	KOMUNIKACJA
A11.3	POM. DZIENNY KUCHNIA
A11.4	ŁAZIENKA
A11.5	KOMUNIKACJA
A11.6	POM. DZIENNY KUCHNIA
A11.7	POM. DZIENNY KUCHNIA
A11.8	POM. DZIENNY KUCHNIA
A11.9	POM. DZIENNY KUCHNIA
A11.10	POM. GOSPODARCZE
A11.11	ŁAZIENKA
A11.12	ŁAZIENKA
A11.13	GARAŻ
POWIERZCHNIA UŻYTKOWA LOKALU A11	
NUMER	FUNKCJA
A12.1	PRZEDSIÓDEK
A12.2	KOMUNIKACJA
A12.3	POM. DZIENNY KUCHNIA
A12.4	ŁAZIENKA
A12.5	KOMUNIKACJA
A12.6	POM. DZIENNY KUCHNIA
A12.7	POM. DZIENNY KUCHNIA
A12.8	POM. DZIENNY KUCHNIA
A12.9	POM. DZIENNY KUCHNIA
A12.10	POM. GOSPODARCZE
A12.11	ŁAZIENKA
A12.12	ŁAZIENKA
A12.13	GARAŻ
POWIERZCHNIA UŻYTKOWA LOKALU A12	
NUMER	FUNKCJA
A13.1	PRZEDSIÓDEK
A13.2	KOMUNIKACJA
A13.3	POM. DZIENNY KUCHNIA
A13.4	ŁAZIENKA
A13.5	KOMUNIKACJA
A13.6	POM. DZIENNY KUCHNIA
A13.7	POM. DZIENNY KUCHNIA
A13.8	POM. DZIENNY KUCHNIA
A13.9	POM. DZIENNY KUCHNIA
A13.10	POM. GOSPODARCZE
A13.11	ŁAZIENKA
A13.12	ŁAZIENKA
A13.13	GARAŻ
POWIERZCHNIA UŻYTKOWA LOKALU A13	
NUMER	FUNKCJA
A14.1	PRZEDSIÓDEK
A14.2	KOMUNIKACJA
A14.3	POM. DZIENNY KUCHNIA
A14.4	ŁAZIENKA
A14.5	KOMUNIKACJA
A14.6	POM. DZIENNY KUCHNIA
A14.7	POM. DZIENNY KUCHNIA
A14.8	POM. DZIENNY KUCHNIA
A14.9	POM. DZIENNY KUCHNIA
A14.10	POM. GOSPODARCZE
A14.11	ŁAZIENKA
A14.12	ŁAZIENKA
A14.13	GARAŻ
POWIERZCHNIA UŻYTKOWA LOKALU A14	
NUMER	FUNKCJA
A15.1	PRZEDSIÓDEK
A15.2	KOMUNIKACJA
A15.3	POM. DZIENNY KUCHNIA
A15.4	ŁAZIENKA
A15.5	KOMUNIKACJA
A15.6	POM. DZIENNY KUCHNIA
A15.7	POM. DZIENNY KUCHNIA
A15.8	POM. DZIENNY KUCHNIA
A15.9	POM. DZIENNY KUCHNIA
A15.10	POM. GOSPODARCZE
A15.11	ŁAZIENKA
A15.12	ŁAZIENKA
A15.13	GARAŻ
POWIERZCHNIA UŻYTKOWA LOKALU A15	
NUMER	FUNKCJA
A16.1	PRZEDSIÓDEK
A16.2	KOMUNIKACJA
A16.3	POM. DZIENNY KUCHNIA
A16.4	ŁAZIENKA
A16.5	KOMUNIKACJA
A16.6	POM. DZIENNY KUCHNIA
A16.7	POM. DZIENNY KUCHNIA
A16.8	POM. DZIENNY KUCHNIA
A16.9	POM. DZIENNY KUCHNIA
A16.10	POM. GOSPODARCZE
A16.11	ŁAZIENKA
A16.12	ŁAZIENKA
A16.13	GARAŻ
POWIERZCHNIA UŻYTKOWA LOKALU A16	
NUMER	FUNKCJA
A17.1	PRZEDSIÓDEK
A17.2	KOMUNIKACJA
A17.3	POM. DZIENNY KUCHNIA
A17.4	ŁAZIENKA
A17.5	KOMUNIKACJA
A17.6	POM. DZIENNY KUCHNIA
A17.7	POM. DZIENNY KUCHNIA
A17.8	POM. DZIENNY KUCHNIA
A17.9	POM. DZIENNY KUCHNIA
A17.10	POM. GOSPODARCZE
A17.11	ŁAZIENKA
A17.12	ŁAZIENKA
A17.13	GARAŻ
POWIERZCHNIA UŻYTKOWA LOKALU A17	
NUMER	FUNKCJA
A18.1	PRZEDSIÓDEK
A18.2	KOMUNIKACJA
A18.3	POM. DZIENNY KUCHNIA
A18.4	ŁAZIENKA
A18.5	KOMUNIKACJA
A18.6	POM. DZIENNY KUCHNIA
A18.7	POM. DZIENNY KUCHNIA
A18.8	POM. DZIENNY KUCHNIA
A18.9	POM. DZIENNY KUCHNIA
A18.10	POM. GOSPODARCZE
A18.11	ŁAZIENKA
A18.12	ŁAZIENKA
A18.13	GARAŻ
POWIERZCHNIA UŻYTKOWA LOKALU A18	
NUMER	FUNKCJA
A19.1	PRZEDSIÓDEK
A19.2	KOMUNIKACJA
A19.3	POM. DZIENNY KUCHNIA
A19.4	ŁAZIENKA
A19.5	KOMUNIKACJA
A19.6	POM. DZIENNY KUCHNIA
A19.7	POM. DZIENNY KUCHNIA
A19.8	POM. DZIENNY KUCHNIA
A19.9	POM. DZIENNY KUCHNIA
A19.10	POM. GOSPODARCZE
A19.11	ŁAZIENKA
A19.12	ŁAZIENKA
A19.13	GARAŻ
POWIERZCHNIA UŻYTKOWA LOKALU A19	
NUMER	FUNKCJA
A20.1	PRZEDSIÓDEK
A20.2	KOMUNIKACJA
A20.3	POM. DZIENNY KUCHNIA
A20.4	ŁAZIENKA
A20.5	KOMUNIKACJA
A20.6	POM. DZIENNY KUCHNIA
A20.7	POM. DZIENNY KUCHNIA
A20.8	POM. DZIENNY KUCHNIA
A20.9	POM. DZIENNY KUCHNIA
A20.10	POM. GOSPODARCZE
A20.11	ŁAZIENKA
A20.12	ŁAZIENKA
A20.13	GARAŻ
POWIERZCHNIA UŻYTKOWA LOKALU A20	
NUMER	FUNKCJA
A21.1	PRZEDSIÓDEK
A21.2	KOMUNIKACJA
A21.3	POM. DZIENNY KUCHNIA
A21.4	ŁAZIENKA
A21.5	KOMUNIKACJA
A21.6	POM. DZIENNY KUCHNIA
A21.7	POM. DZIENNY KUCHNIA
A21.8	POM. DZIENNY KUCHNIA
A21.9	POM. DZIENNY KUCHNIA
A21.10	POM. GOSPODARCZE
A21.11	ŁAZIENKA
A21.12	ŁAZIENKA
A21.13	GARAŻ
POWIERZCHNIA UŻYTKOWA LOKALU A21	
NUMER	FUNKCJA
A22.1	PRZEDSIÓDEK
A22.2	KOMUNIKACJA
A22.3	POM. DZIENNY KUCHNIA
A22.4	ŁAZIENKA
A22.5	KOMUNIKACJA
A22.6	POM. DZIENNY KUCHNIA
A22.7	POM. DZIENNY KUCHNIA
A22.8	POM. DZIENNY KUCHNIA
A22.9	POM. DZIENNY KUCHNIA
A22.10	POM. GOSPODARCZE
A22.11	ŁAZIENKA
A22.12	ŁAZIENKA
A22.13	GARAŻ
POWIERZCHNIA UŻYTKOWA LOKALU A22	
NUMER	FUNKCJA
A23.1	PRZEDSIÓDEK
A23.2	KOMUNIKACJA
A23.3	POM. DZIENNY KUCHNIA
A23.4	ŁAZIENKA
A23.5	KOMUNIKACJA
A23.6	POM. DZIENNY KUCHNIA
A23.7	POM. DZIENNY KUCHNIA
A23.8	POM. DZIENNY KUCHNIA
A23.9	POM. DZIENNY KUCHNIA
A23.10	POM. GOSPODARCZE
A23.11	ŁAZIENKA
A23.12	ŁAZIENKA
A23.13	GARAŻ
POWIERZCHNIA UŻYTKOWA LOKALU A23	
NUMER	FUNKCJA
A24.1	PRZEDSIÓDEK
A24.2	KOMUNIKACJA
A24.3	POM. DZIENNY KUCHNIA
A24.4	ŁAZIENKA
A24.5	KOMUNIKACJA
A24.6	POM. DZIENNY KUCHNIA
A24.7	POM. DZIENNY KUCHNIA
A24.8	POM. DZIENNY KUCHNIA
A24.9	POM. DZIENNY KUCHNIA
A24.10	POM. GOSPODARCZE
A24.11	ŁAZIENKA
A24.12	ŁAZIENKA
A24.13	GARAŻ
POWIERZCHNIA UŻYTKOWA LOKALU A24	
NUMER	FUNKCJA
A25.1	PRZEDSIÓDEK
A25.2	KOMUNIKACJA
A25.3	POM. DZIENNY KUCHNIA
A25.4	ŁAZIENKA
A25.5	KOMUNIKACJA
A25.6	POM. DZIENNY KUCHNIA
A25.7	POM. DZIENNY KUCHNIA
A25.8	POM. DZIENNY KUCHNIA
A25.9	POM. DZIENNY KUCHNIA
A25.10	POM. GOSPODARCZE
A25.11	ŁAZIENKA
A25.12	ŁAZIENKA
A25.13	GARAŻ
POWIERZCHNIA UŻYTKOWA LOKALU A25	
NUMER	FUNKCJA
A26.1	PRZEDSIÓDEK
A26.2	KOMUNIKACJA
A26.3	POM. DZIENNY KUCHNIA
A26.4	ŁAZIENKA
A26.5	KOMUNIKACJA
A26.6	POM. DZIENNY KUCHNIA
A26.7	POM. DZIENNY KUCHNIA
A26.8	POM. DZIENNY KUCHNIA
A26.9	POM. DZIENNY KUCHNIA
A26.10	POM. GOSPODARCZE
A26.11	ŁAZIENKA
A26.12	ŁAZIENKA
A26.13	GARAŻ
POWIERZCHNIA UŻYTKOWA LOKALU A26	
NUMER	FUNKCJA
A27.1	PRZEDSIÓDEK
A27.2	KOMUNIKACJA
A27.3	POM. DZIENNY KUCHNIA
A27.4	ŁAZIENKA
A27.5	KOMUNIKACJA
A27.6	POM. DZIENNY KUCHNIA
A27.7	POM. DZIENNY KUCHNIA
A27.8	POM. DZIENNY KUCHNIA
A27.9	POM. DZIENNY KUCHNIA
A27.10	POM. GOSPODARCZE
A27.11	ŁAZIENKA
A27.12	ŁAZIENKA
A27.13	GARAŻ
POWIERZCHNIA UŻYTKOWA LOKALU A27	
NUMER	FUNKCJA
A28.1	PRZEDSIÓDEK
A28.2	KOMUNIKACJA
A28.3	POM. DZIENNY KUCHNIA
A28.4	ŁAZIENKA
A28.5	KOMUNIKACJA
A28.6	POM. DZIENNY KUCHNIA
A28.7	POM. DZIENNY KUCHNIA
A28.8	POM. DZIENNY KUCHNIA
A28.9	POM. DZIENNY KUCHNIA
A28.10	POM. GOSPODARCZE
A28.11	ŁAZIENKA
A28.12	ŁAZIENKA
A28.13	GARAŻ
POWIERZCHNIA UŻYTKOWA LOKALU A28	
NUMER	FUNKCJA
A29.1	PRZEDSIÓDEK
A29.2	KOMUNIKACJA
A29.3	POM. DZIENNY KUCHNIA

1. PROJEKT NIE JEST OBJEKT OCHRONY PRAW AUTORSKICH.
2. WSKAZANE ELEMENTY KONSTRUKCYJNE SĄ WYKONANE WEDŁUG
PROJEKTU TECHNICZNEGO I WYKONAWCZEGO KONSTRUKCJI.
3. INSTALACJE WYKONAĆ WEDŁUG PROJEKTU TECHNICZNEGO
I LUB WYKONAWCZEGO BRANŻY ELEKTRYCZNEJ I SANITARNEJ.
4. RYSUNEK NALEŻY CZYTAĆ ŁĄCZNIE Z CZĘŚCIĄ SPISOWĄ,
RYSUNKOWĄ ORAZ DOPOSIŁAJĄCYMI PROJEKTAMI BRANŻOWYMI.
5. WSKAZANE NIEJASNOŚCI NALEŻY WYJAŚNIĆ Z GENERALNYM
PROJEKTEM I PROJEKTANTEM BRANŻY PROJEKTOWYCH.
6. PRACE BUDOWLANE PRACOWNIKI ŁĄCZNIE NA PRZEDSTAWIE
PROJEKTU BUDOWLANEGO I PROJEKTU WYKONAWCZEGO
Z GENERALNYM PROJEKTEM I PROJEKTANTEM
7. PODCZAS PRAC BUDOWLANICH SZCZEGÓLNĄ UWAGĘ ZWRÓCIĆ
NA WYKONANIE WYKONAWCZEGO KONSTRUKCJI
8. WYKONAWCA JEST ZOBOWIĄZANY DO WYKONANIA PRAC
BUDOWLANICH ZGODNIE Z ZAKŁADANĄ STYMI I OBOWIĄZUJĄCYMI
PRZEPISAMI TECHNICZNYMI, A EWENTUALNE ROZBIEŻNOŚCI
I ZASTRZEŻENIA W TYM ZAKRESIE POWINIEN
WYKONAWCA PRAC WYKONAWCZYM PRACOWNIKI
9. WYMIARY I WŁASNOŚCI ZWIERZĄCE NA BUDOWIE PRZED
ZACZĄTKIEM PRAC BUDOWLANICH
10. WYPOSAŻENIE I WYKONANIE POMIESZCZENI WYKONAC
ZGODNIE Z PROJEKTEM WŁĘCZNYM
11. PRZED ROZPOCZĘCIEM ROBÓT NALEŻY OPRAWIĆ PROJEKT
WYKONAWCZY

ZESTAWIENIE POWIERZCHNI:


NUMER	FUNKCJA	m ²
A1.1	PRZEDSIÓDNEK	3,77
A1.2	POM. DZIENNY KUCHNIA	10,56
A1.3	POM. J	8,39
A1.4	POM. J	12,36
A1.5	ŁAZIENKA	5,43
A1.6	POM. GOSPODARCZE	6,21
A1.7	KOMUNIKACJA	4,46
A1.8	P. DZIENNY POZIOM DRUGI	4,46
A1.9	ŁAZIENKA	5,38
A1.10	GARAŻ	20,53
POWIERZCHNIA UŻYTKOWA LOKALU A1		135,91

NUMER	FUNKCJA	m ²
A2.1	PRZEDSIÓDNEK	5,03
A2.2	KOMUNIKACJA	1,23
A2.3	POM. DZIENNY KUCHNIA	44,58
A2.4	ŁAZIENKA	1,91
A2.5	KOMUNIKACJA	7,25
A2.6	POM. J	11,76
A2.7	POM. J	9,51
A2.8	POM. J	11,73
A2.9	POM. J	12,03
A2.10	POM. GOSPODARCZE	4,05
A2.11	ŁAZIENKA	6,73
A2.12	ŁAZIENKA	4,73
A2.13	GARAŻ	20,53
POWIERZCHNIA UŻYTKOWA LOKALU A2		120,84


POWIERZCHNIA UŻYTKOWA BUDYNKU A1-A2		256,75
-------------------------------------	--	--------

POZIOM POSADOWIENIA BUDYNKU:


BUDYNEK	RZĘDNA POZIOMU ±0.00 (m n.p.m.)
A1.2	225.65
B1,C1,B2,C2	225.50
A3.4	225.35
B3,C3,B4,C4	225.20
B5,C5,B6,C6	224.70
A5.6	224.60
B7,C7,B8,C8	224.50
A7.8	224.40
B9,C9,B10,C10	224.30
A9.10	224.20
B11,C11,B12,C12	224.10
A11.12	223.70
B13,C13,B14,C14	223.60
A13.14	223.50

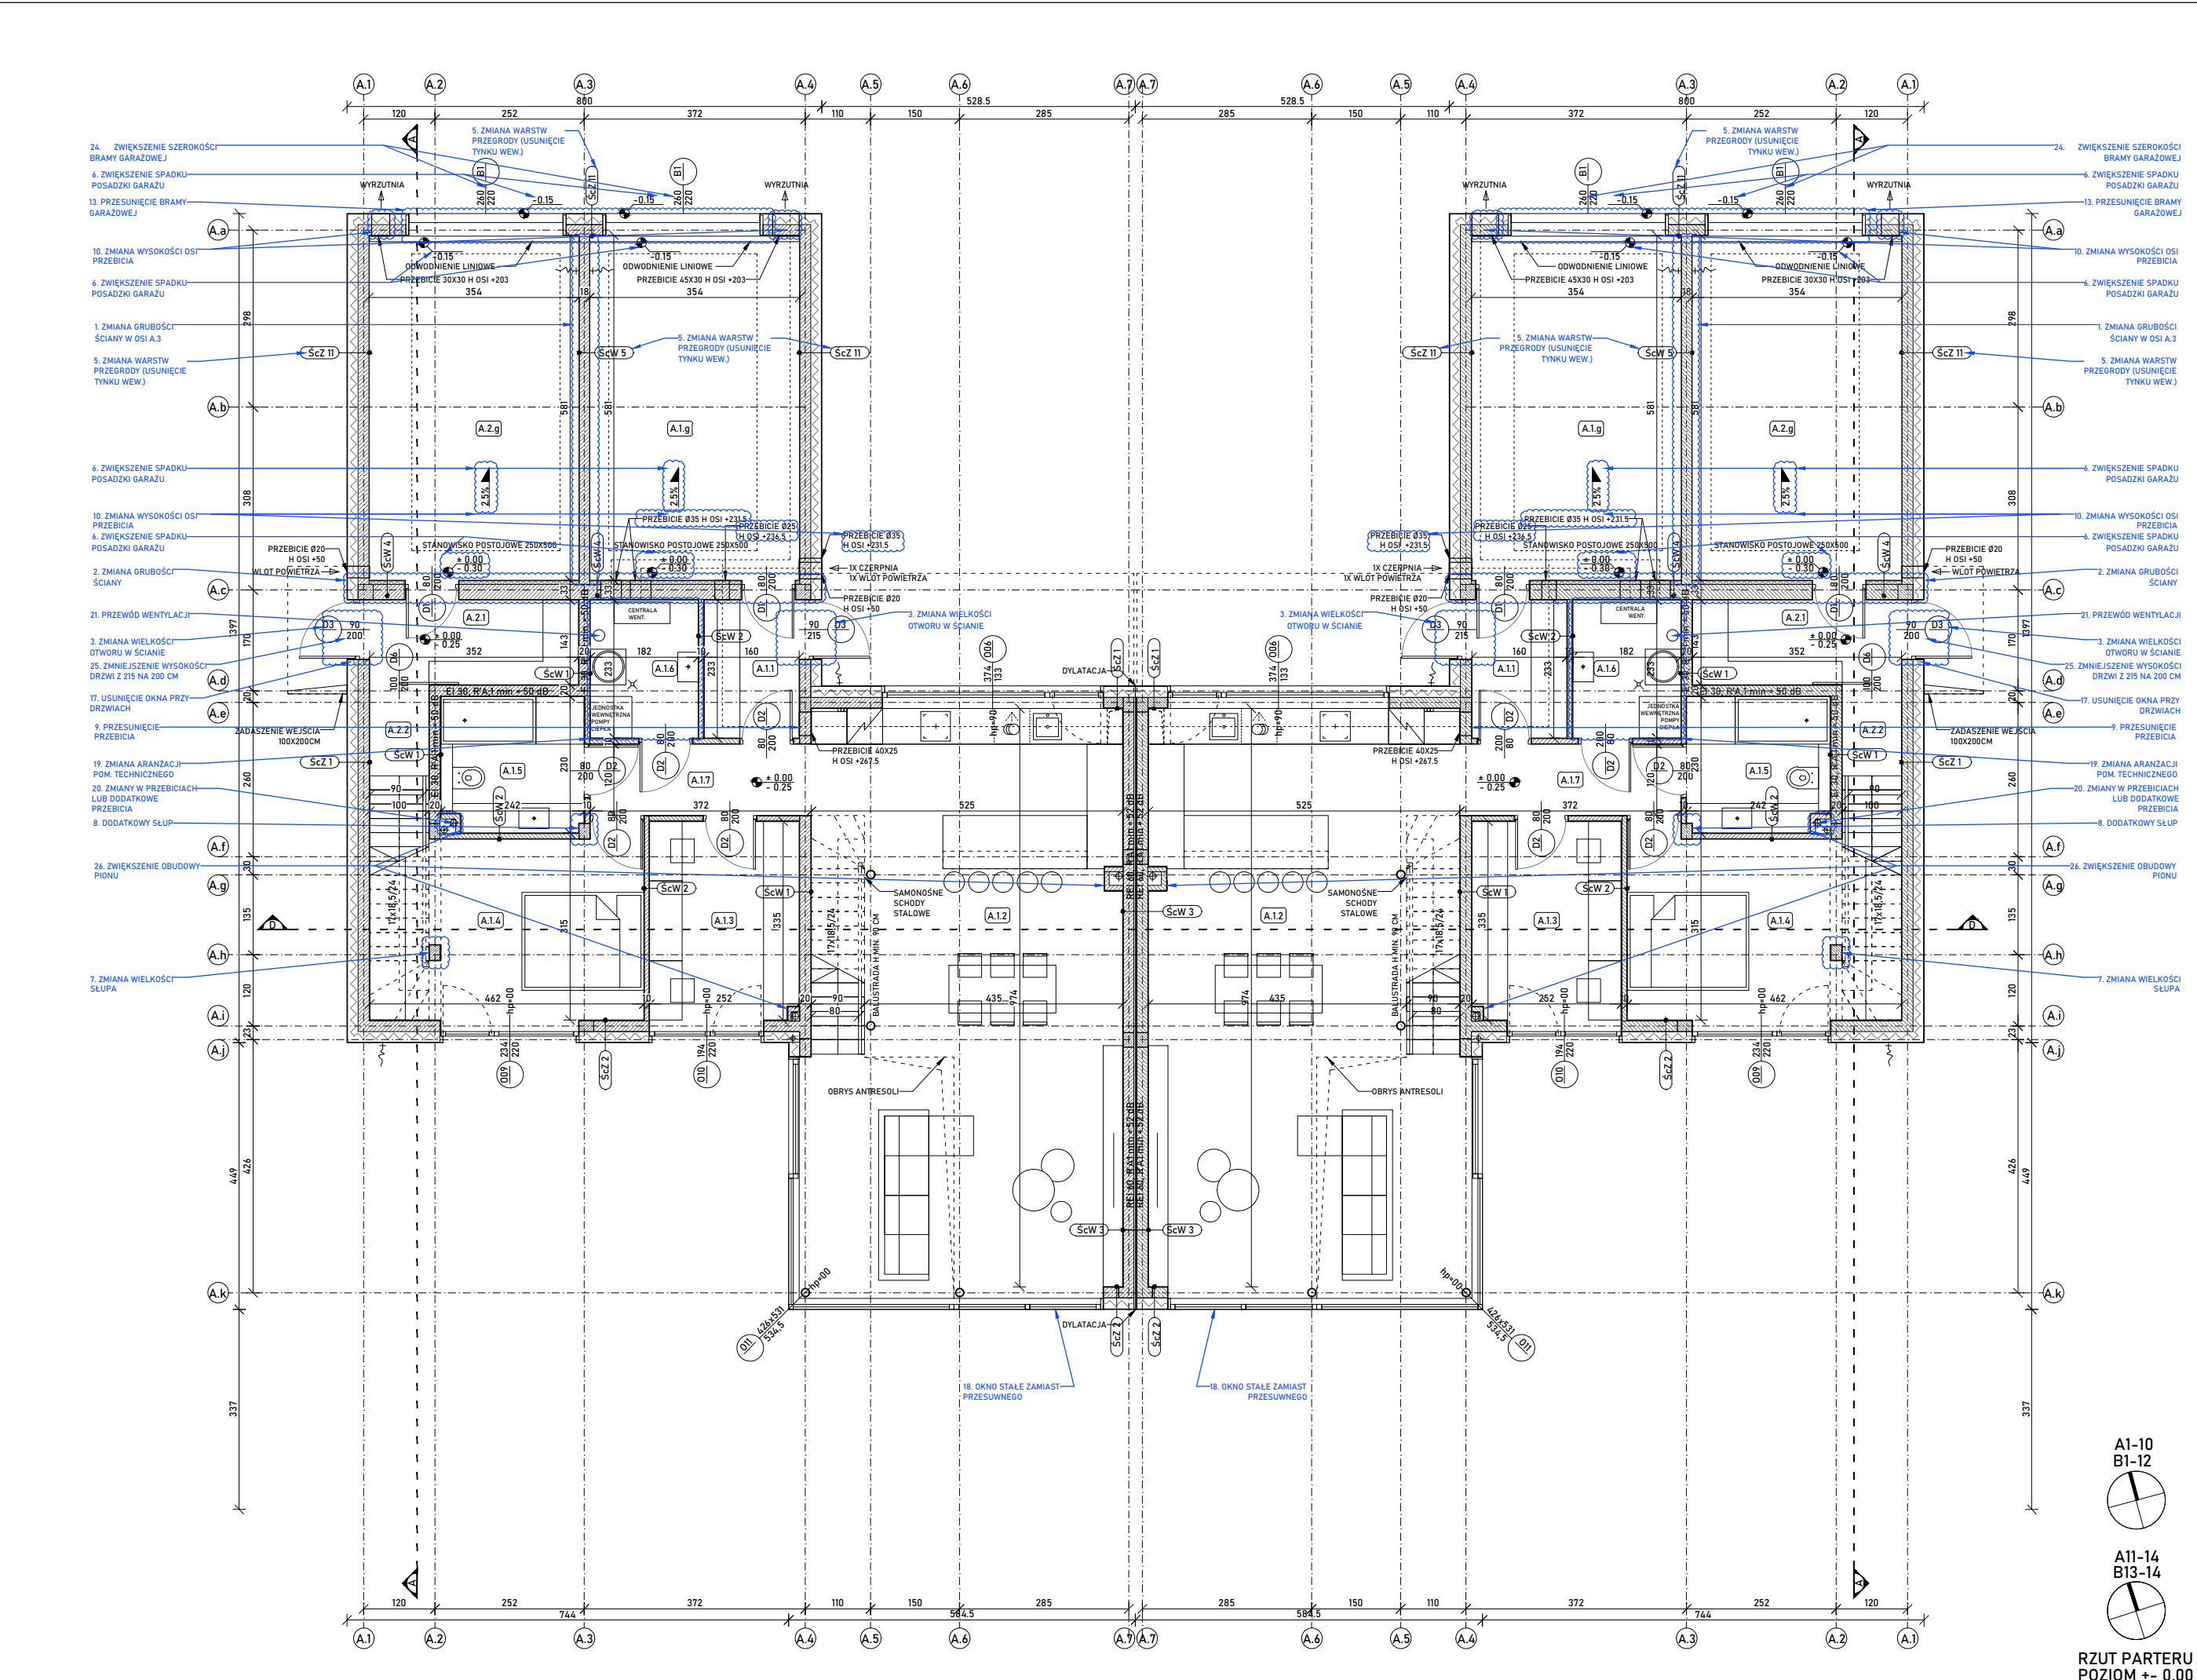


RZUT PARTERU
POZIOM ±0.00

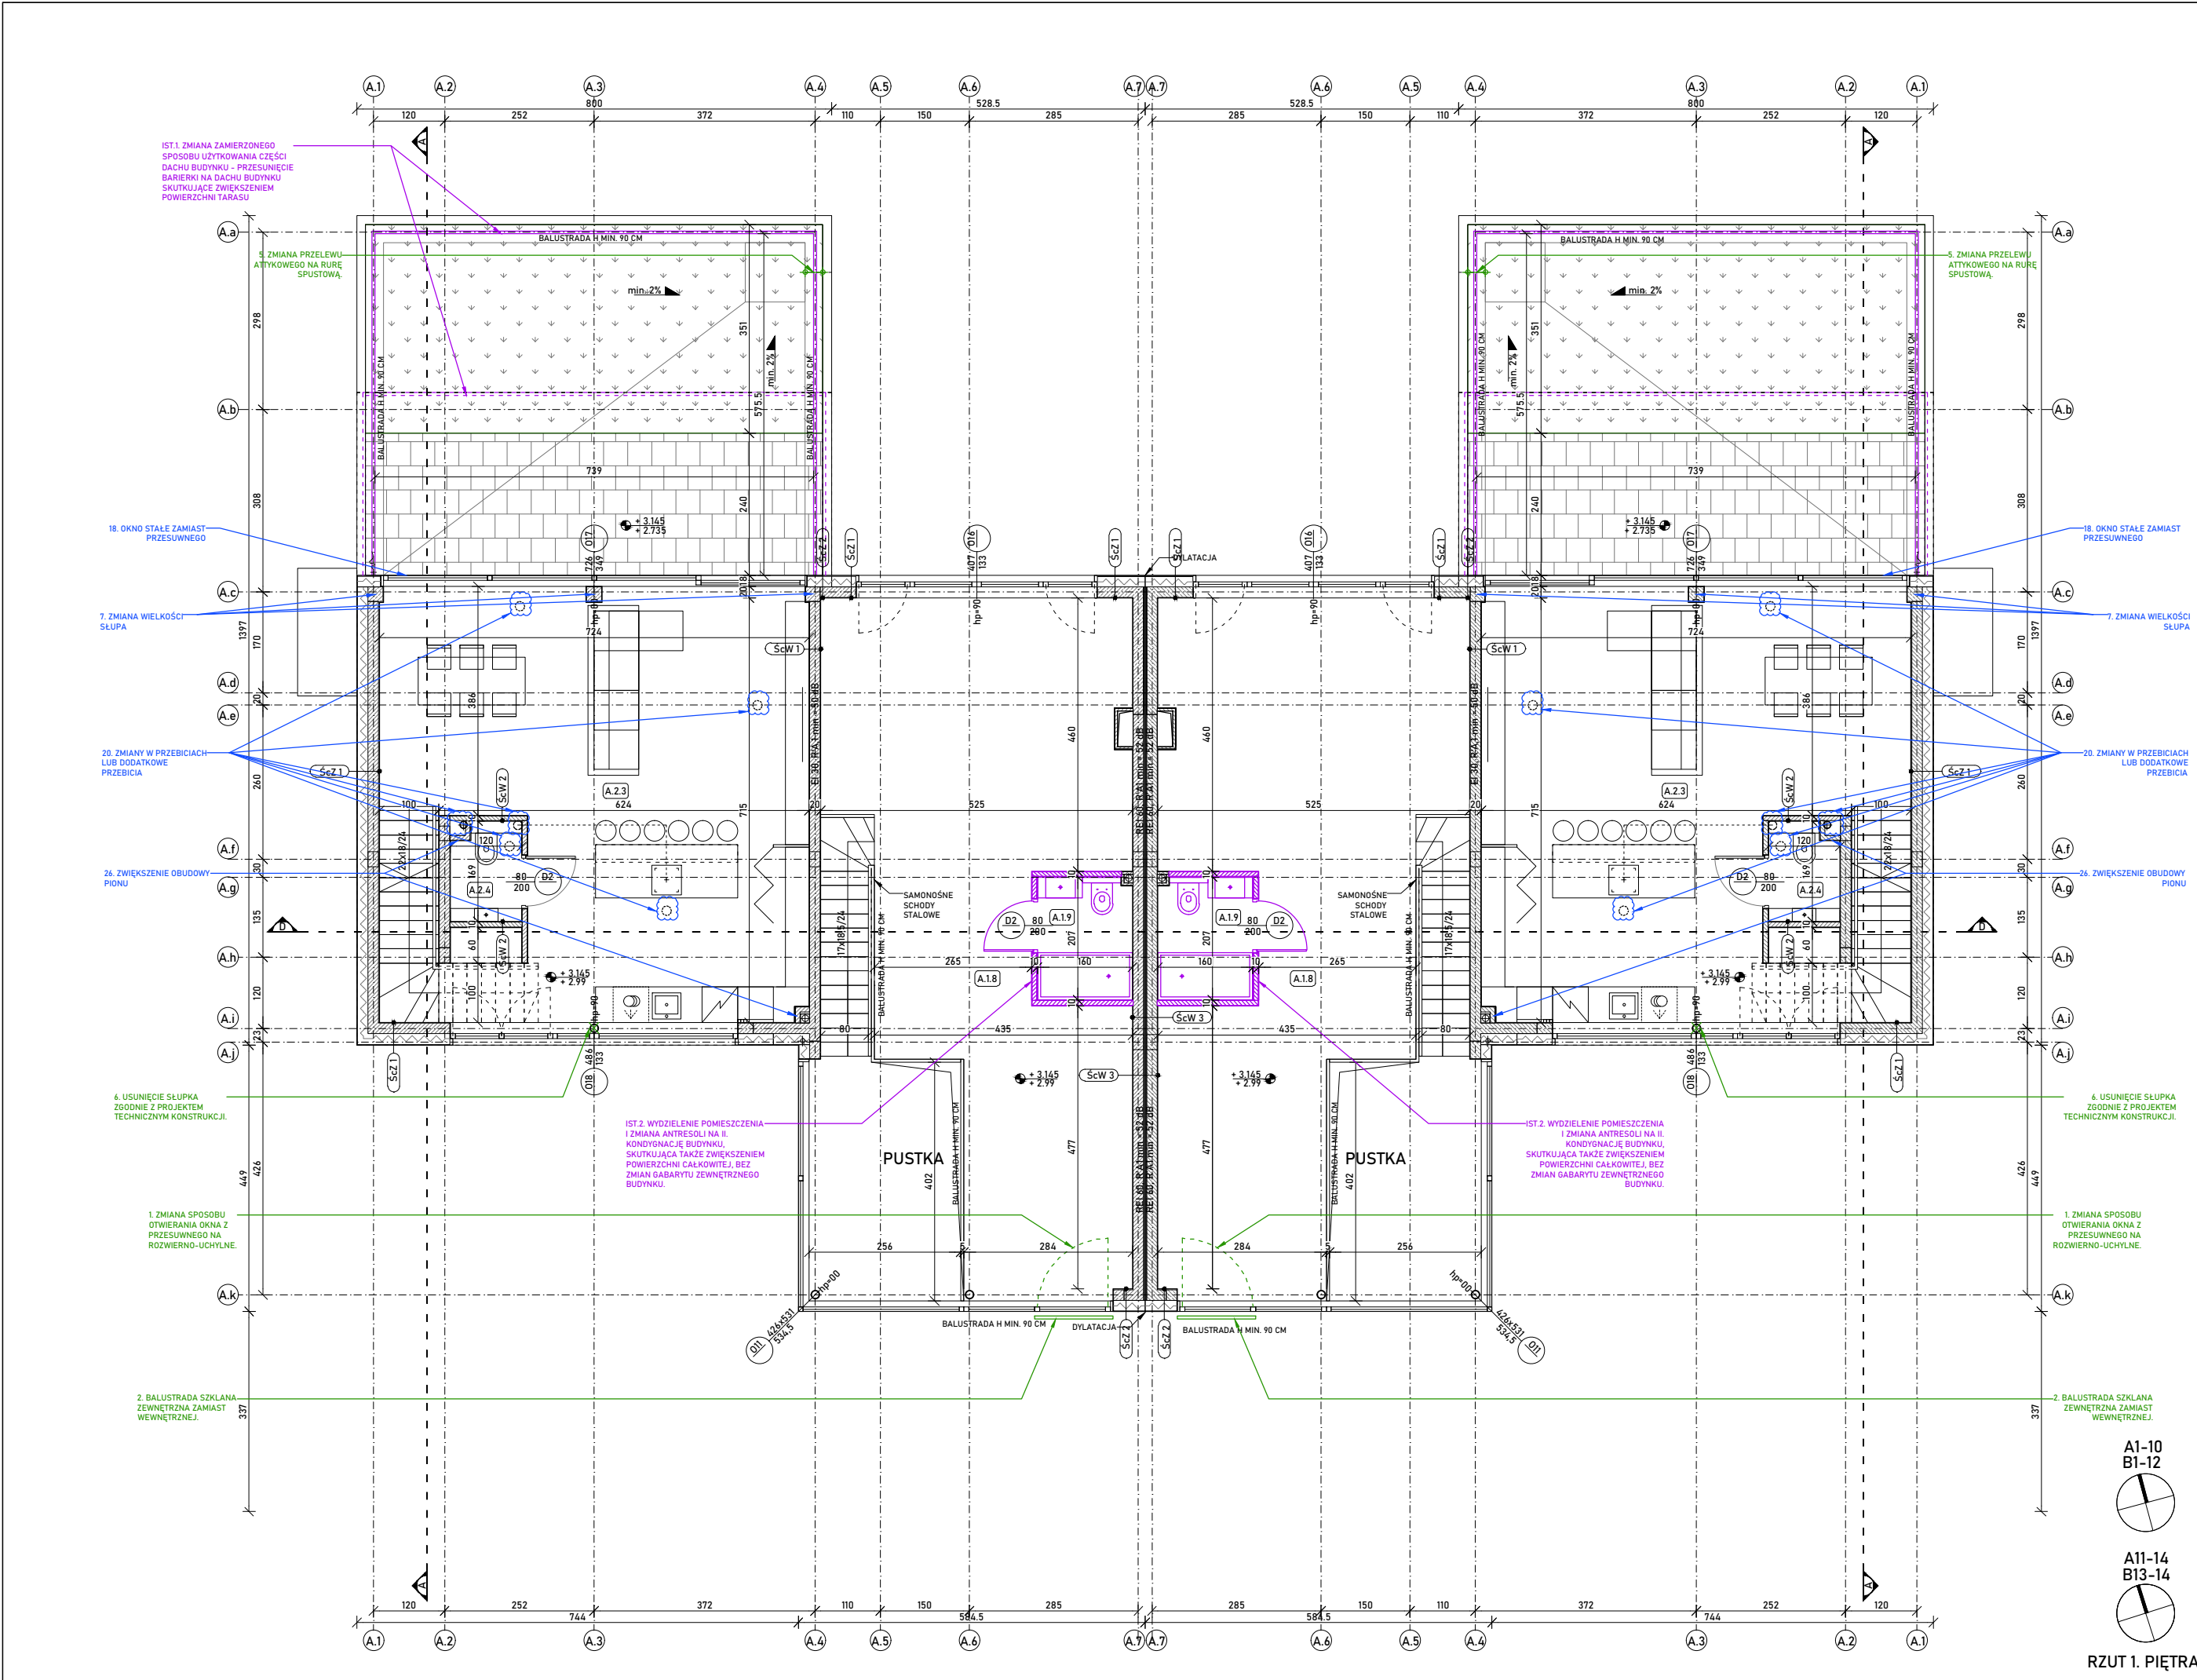

RZUT I. PIĘTRA

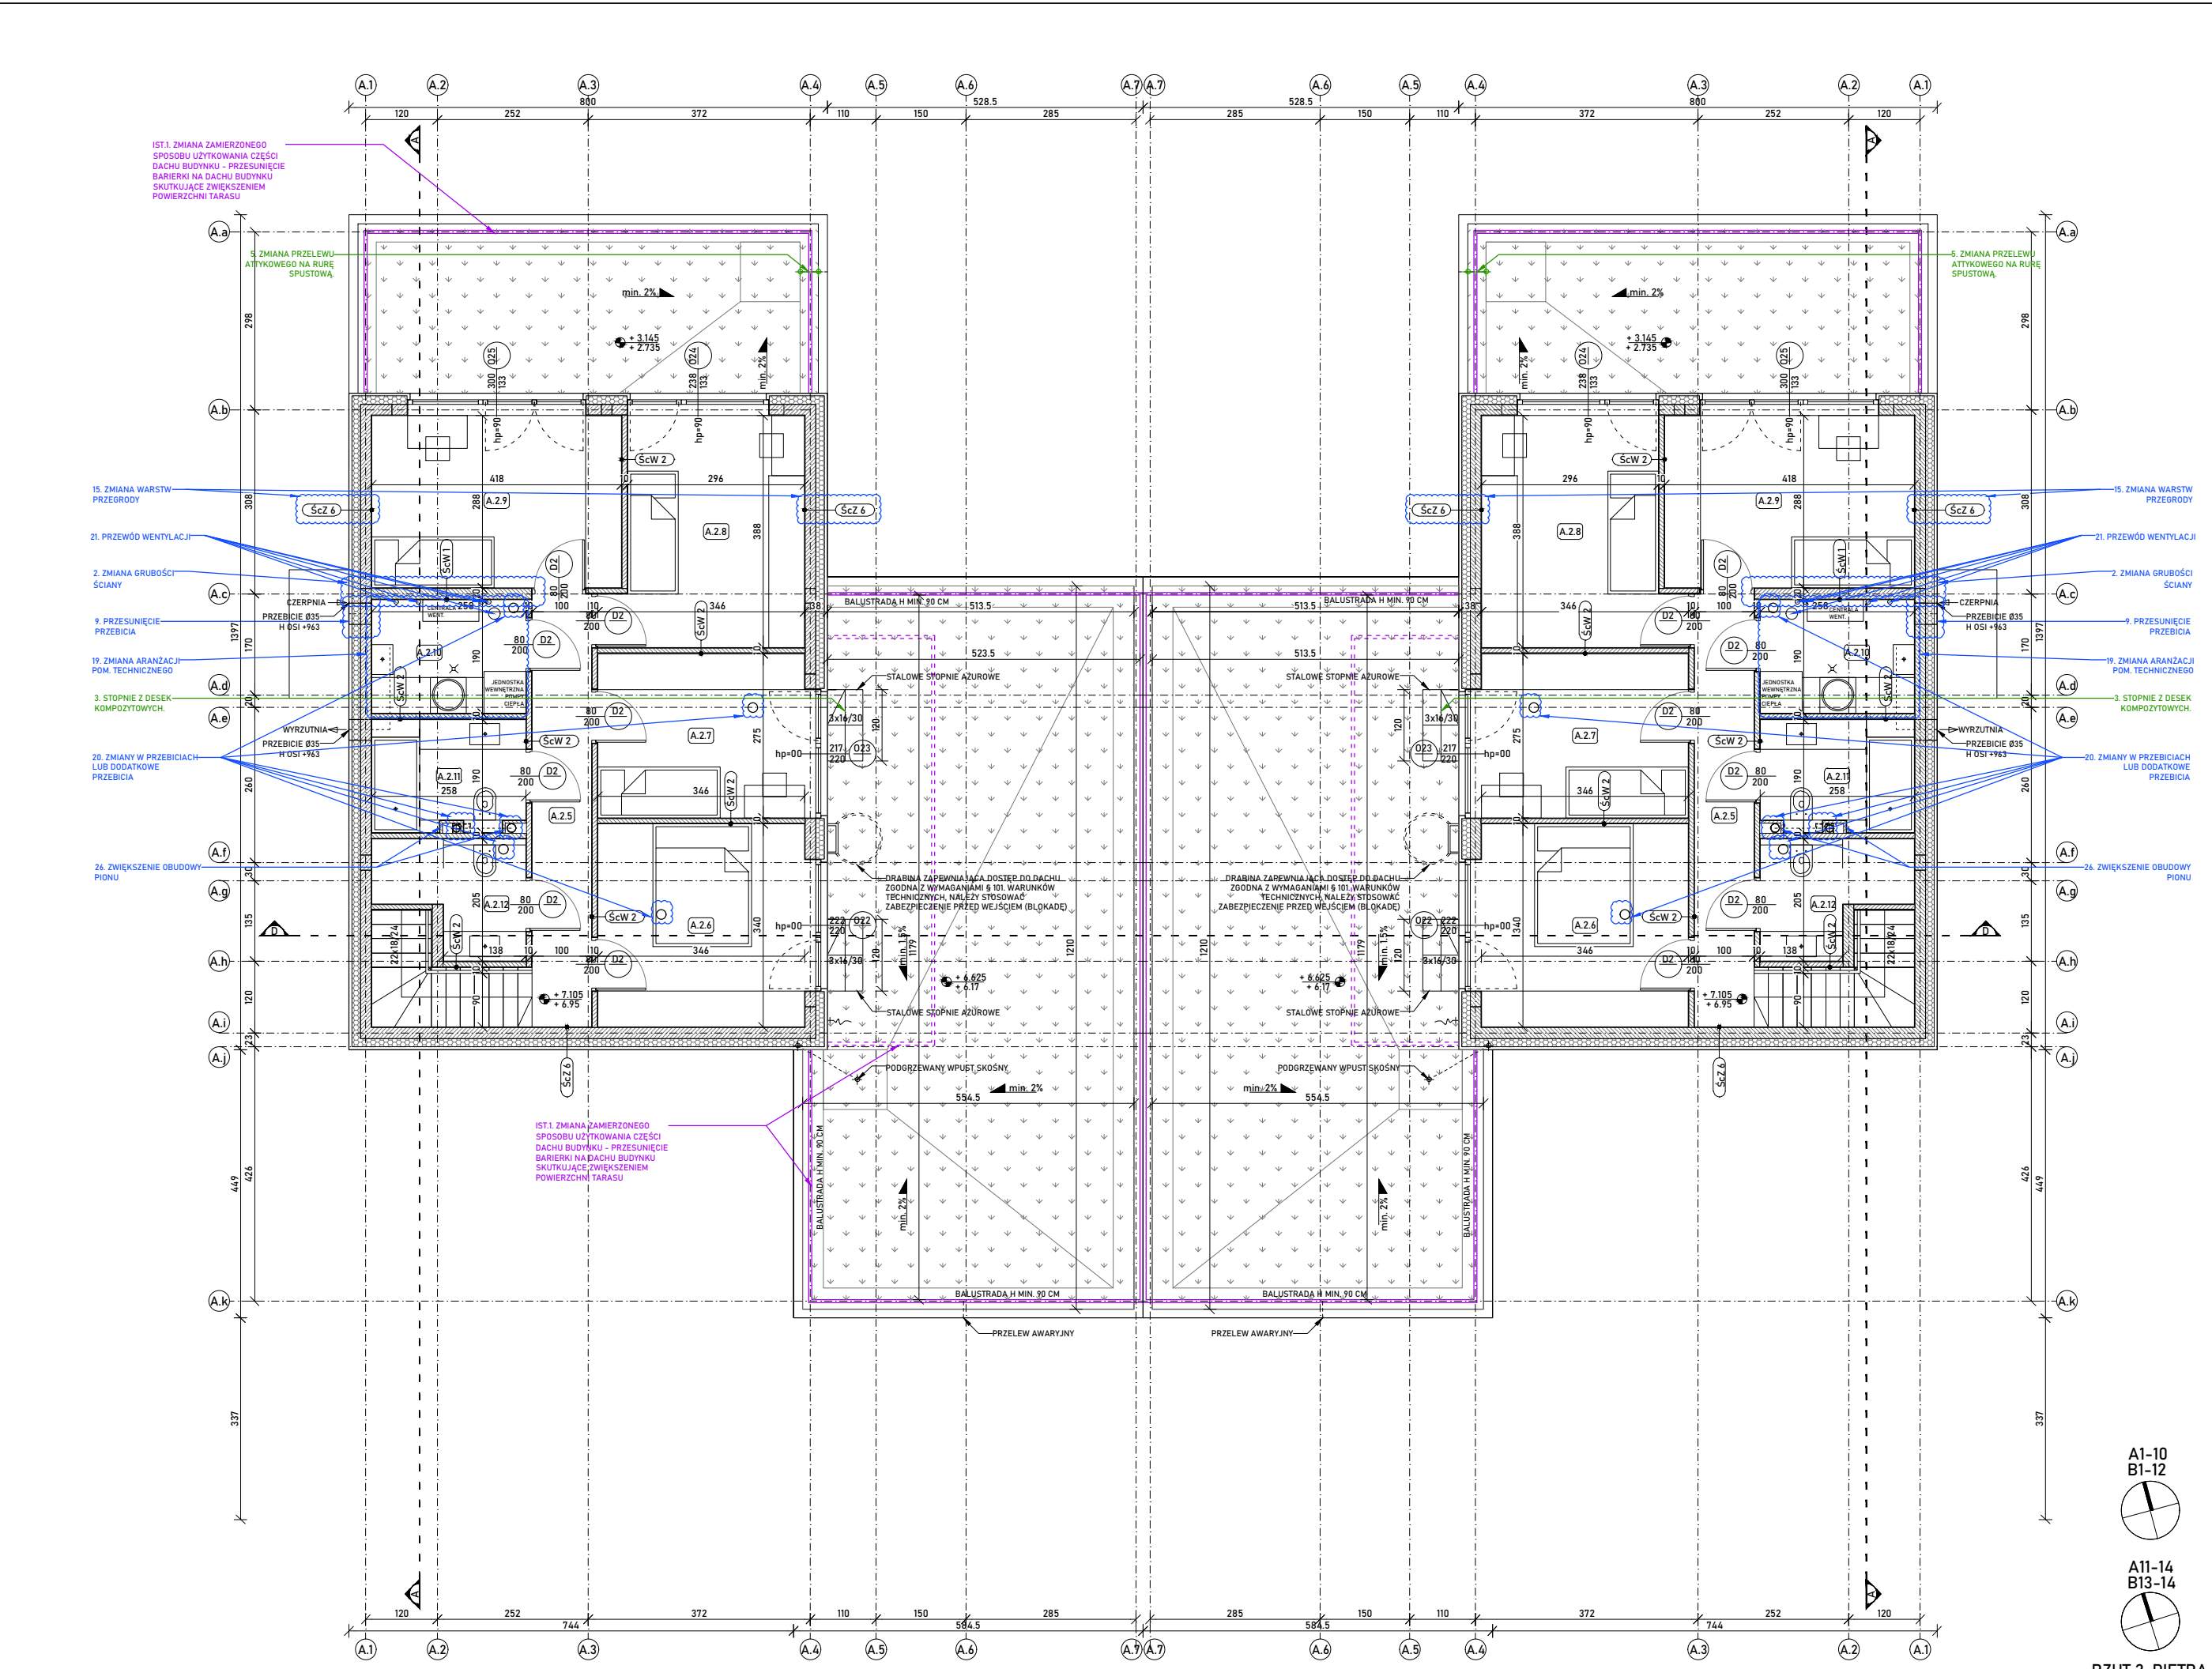

RZUT 2. PIĘTRA

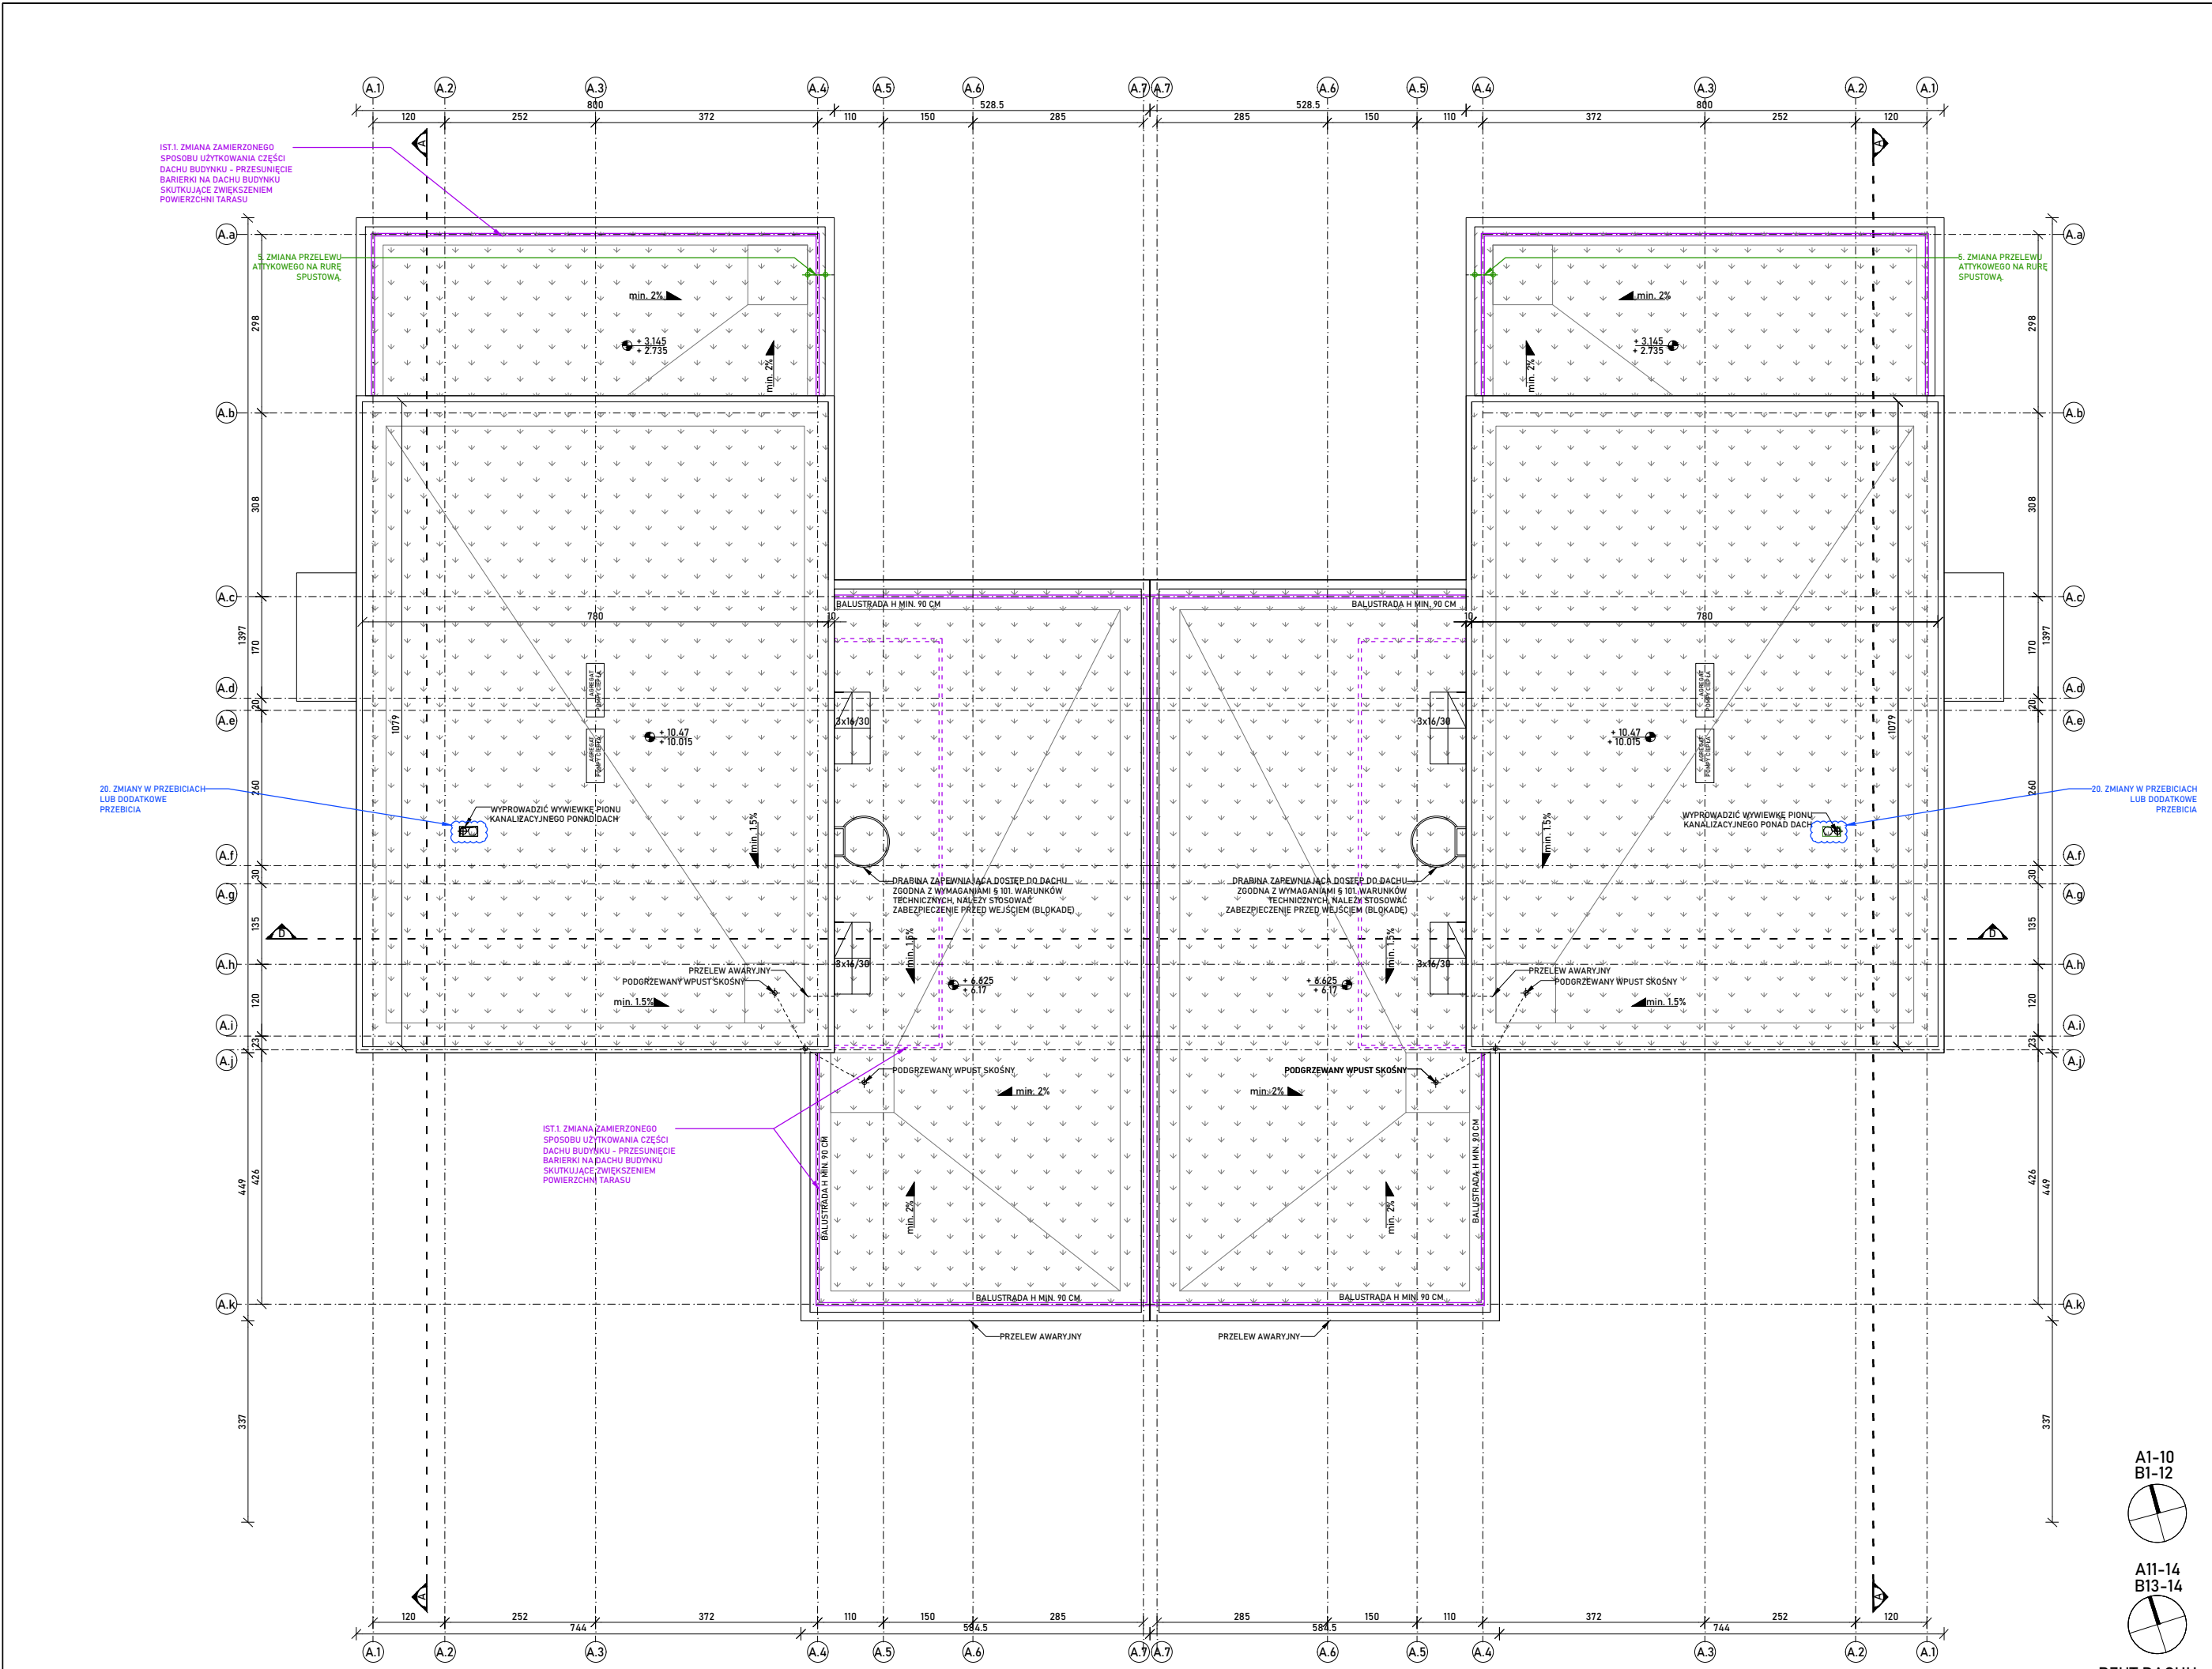

RZUT DACHU





SPIS ZMIAN NIEISTOTNYCH WEDŁUG PRAWA BUDOWLANEGO W STOSUNKU DO PROJEKTU ARCHYTEKTONICZNO-BUDOWLANEGO
OBJĘTOŚĆ BUDYNKU W PRZEDSIÓDNIU ZMIAN 13. LISTOPAD 2023 R.
ZMIENIONEGO DECYZJĄ NR WYK/14/2024 Z DNIA 07.10.2024 R.

1. ZMIANA SPOSOBU OŚWIETLENIA DACHU Z PRZESZKODZONYM NA ROZBIEŻNOŚCIACH
2. BALUSTRADE SZKLANA ZEWNĘTRZNA ZAMIAST WEWNĘTRZNEJ
3. STROPIE Z DŁUGIEM KONTAKTOWYM
4. ZMIANA WYPEŁNIENIA BALUSTRAD NA SZKLANO
5. ZMIANA PRZECIŁNIA ATTYKOWEGO NA KULISTO
6. LUSZKOWE SŁUPY ZŁOŻONE Z PROJEKTU TECHNICZNEGO
KONSTRUKCJI

ZMIANY WYKAZANE W DOKUMENTACJI OBJEKTU ZMIENIENIEM
POSIADANIE NA BUDOWIE, DECYZJĄ NR WYK/14/2024 Z DNIA 07.10.2024 R.

SPIS ZMIAN ISTOTNYCH WEDŁUG PRAWA BUDOWLANEGO W STOSUNKU DO PROJEKTU ARCHYTEKTONICZNO-BUDOWLANEGO
OBJĘTOŚĆ BUDYNKU W PRZEDSIÓDNIU ZMIAN 13. LISTOPAD 2023 R.
ZMIENIONEGO DECYZJĄ NR WYK/14/2024 Z DNIA 07.10.2024 R.

1. ZMIANA GRUBOŚCI ŚCIANY W OS. A.3
2. ZMIANA GRUBOŚCI ŚCIANY ŚCIANY ZMIAN WYKONAWCZYCH A.1.1, A.1.2, A.1.3, A.1.4, A.1.5, A.1.6, A.1.7, A.1.8, A.1.9, A.1.10, A.1.11, A.1.12,A.1.99, A.1.100, A.1.101, A.1.102,A.1.999, A.2000, A.2001, A.2002,A.2151, A

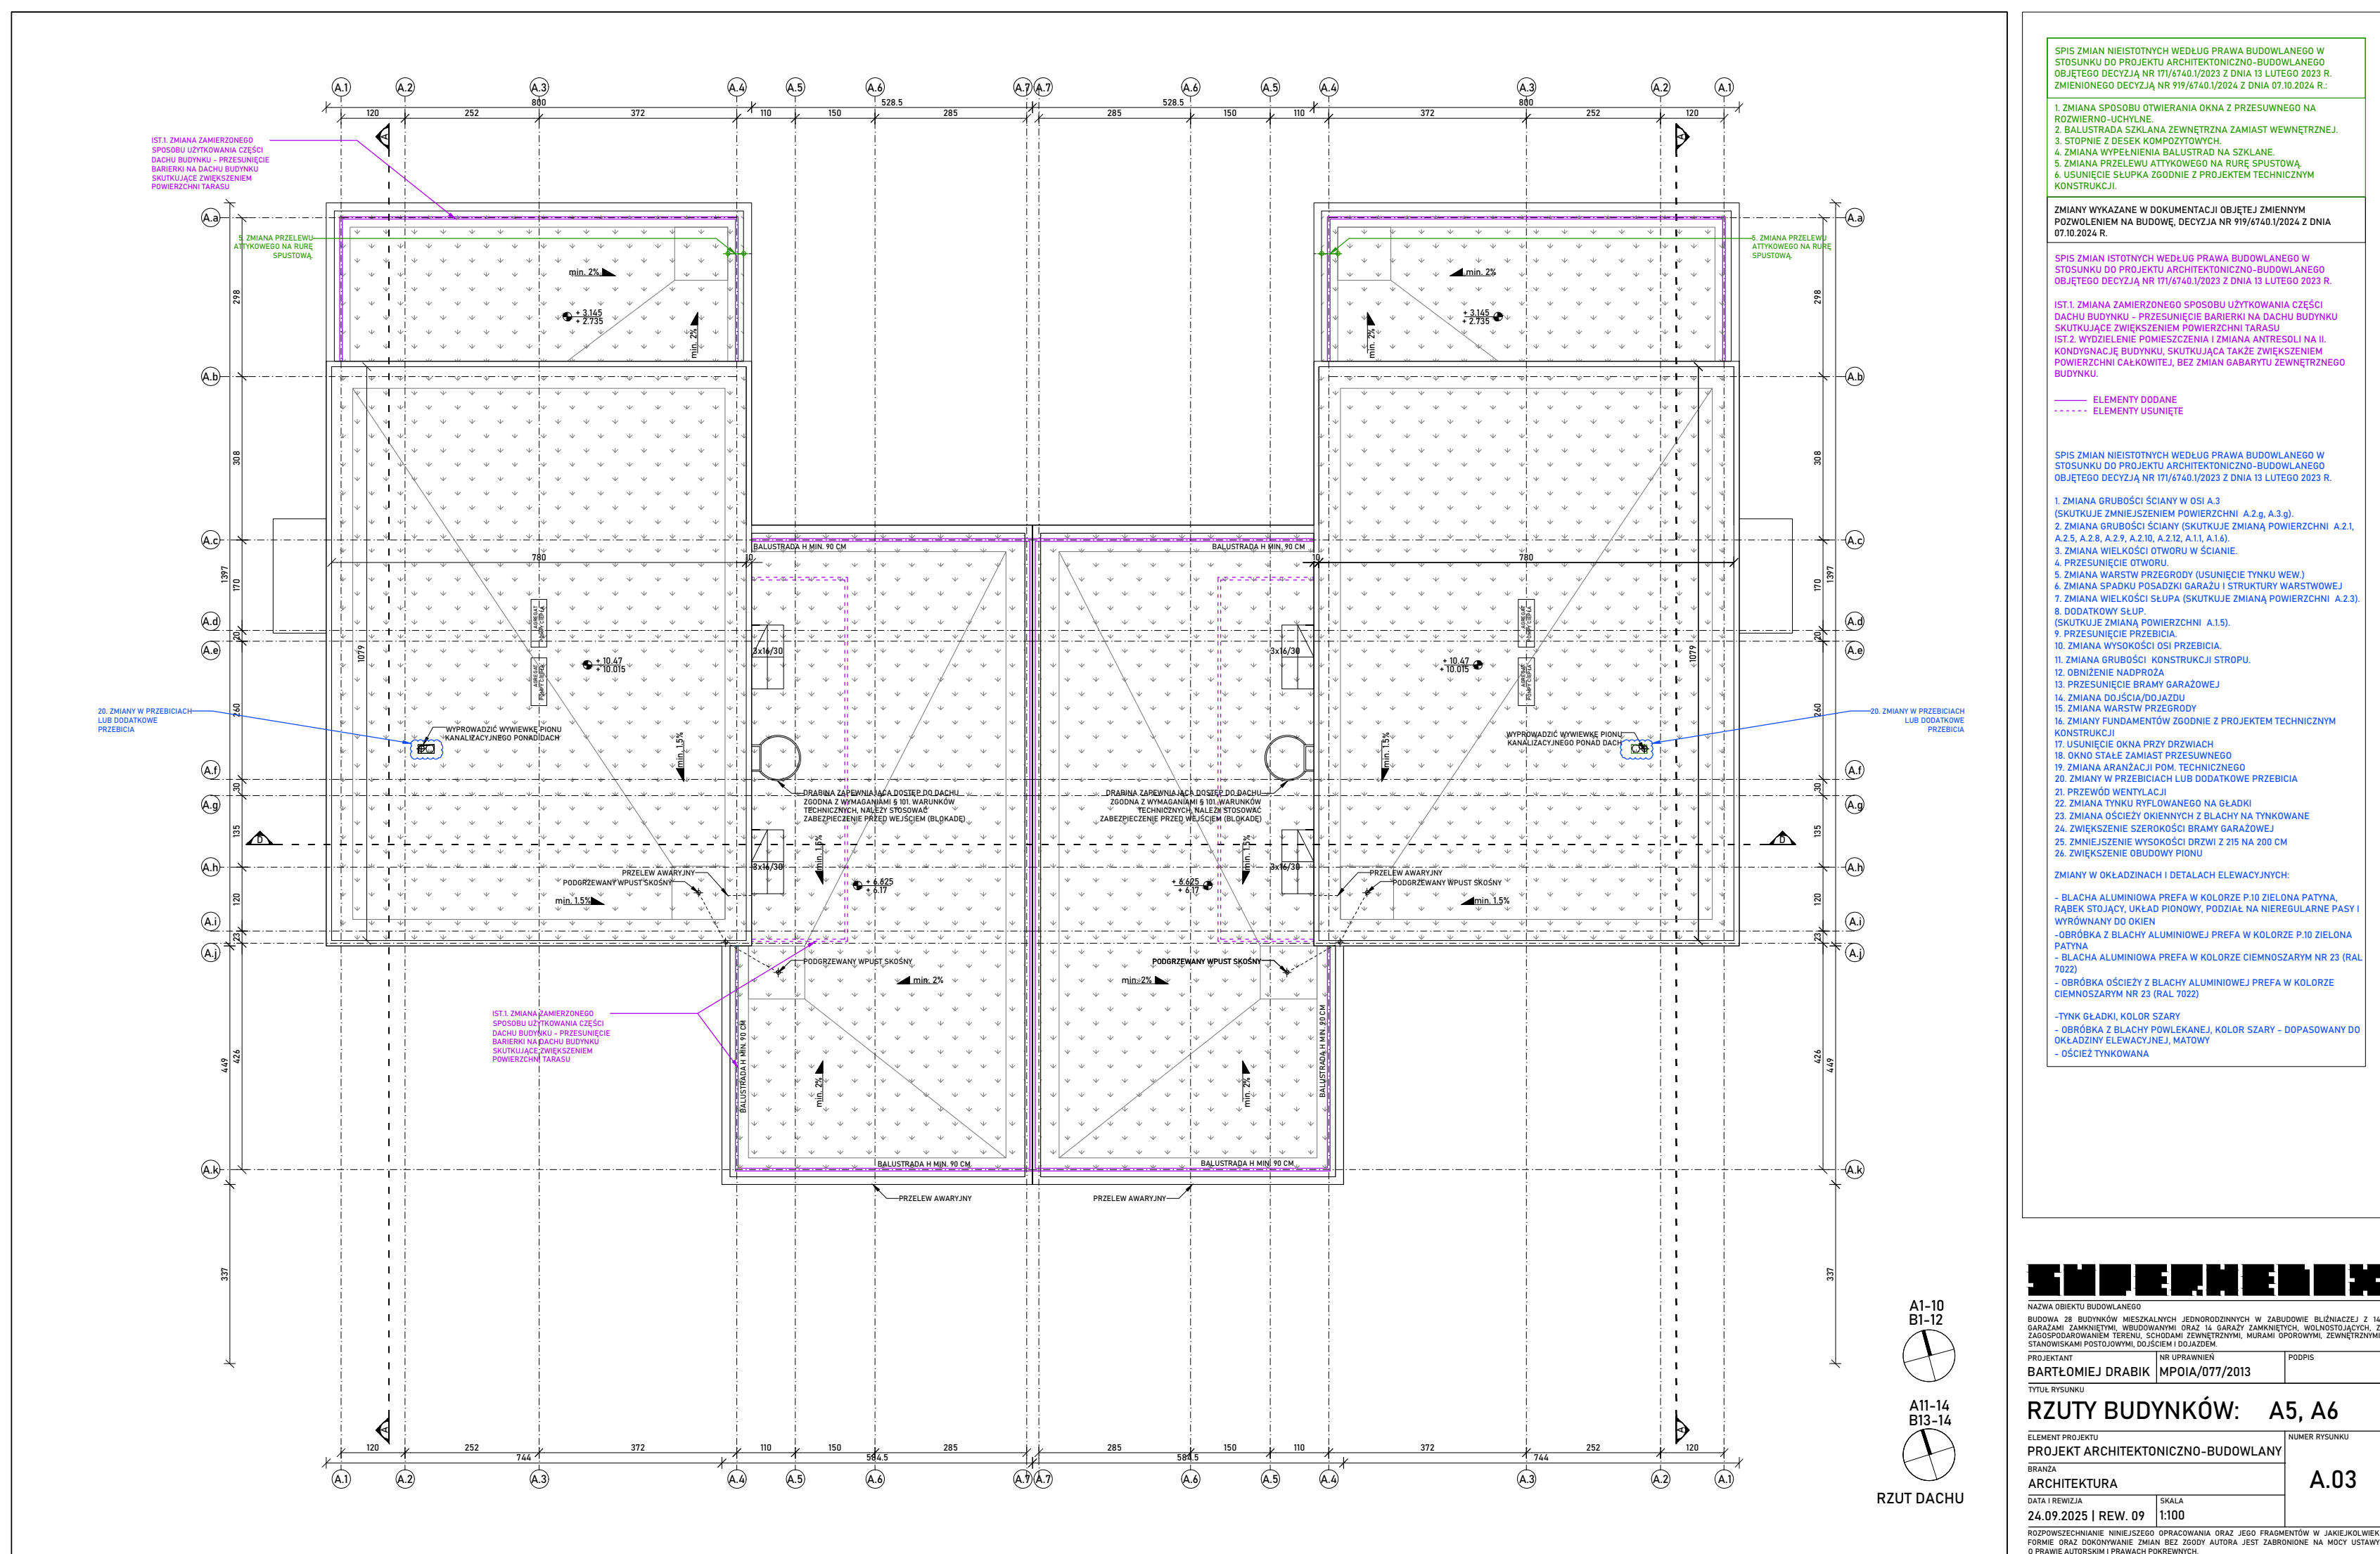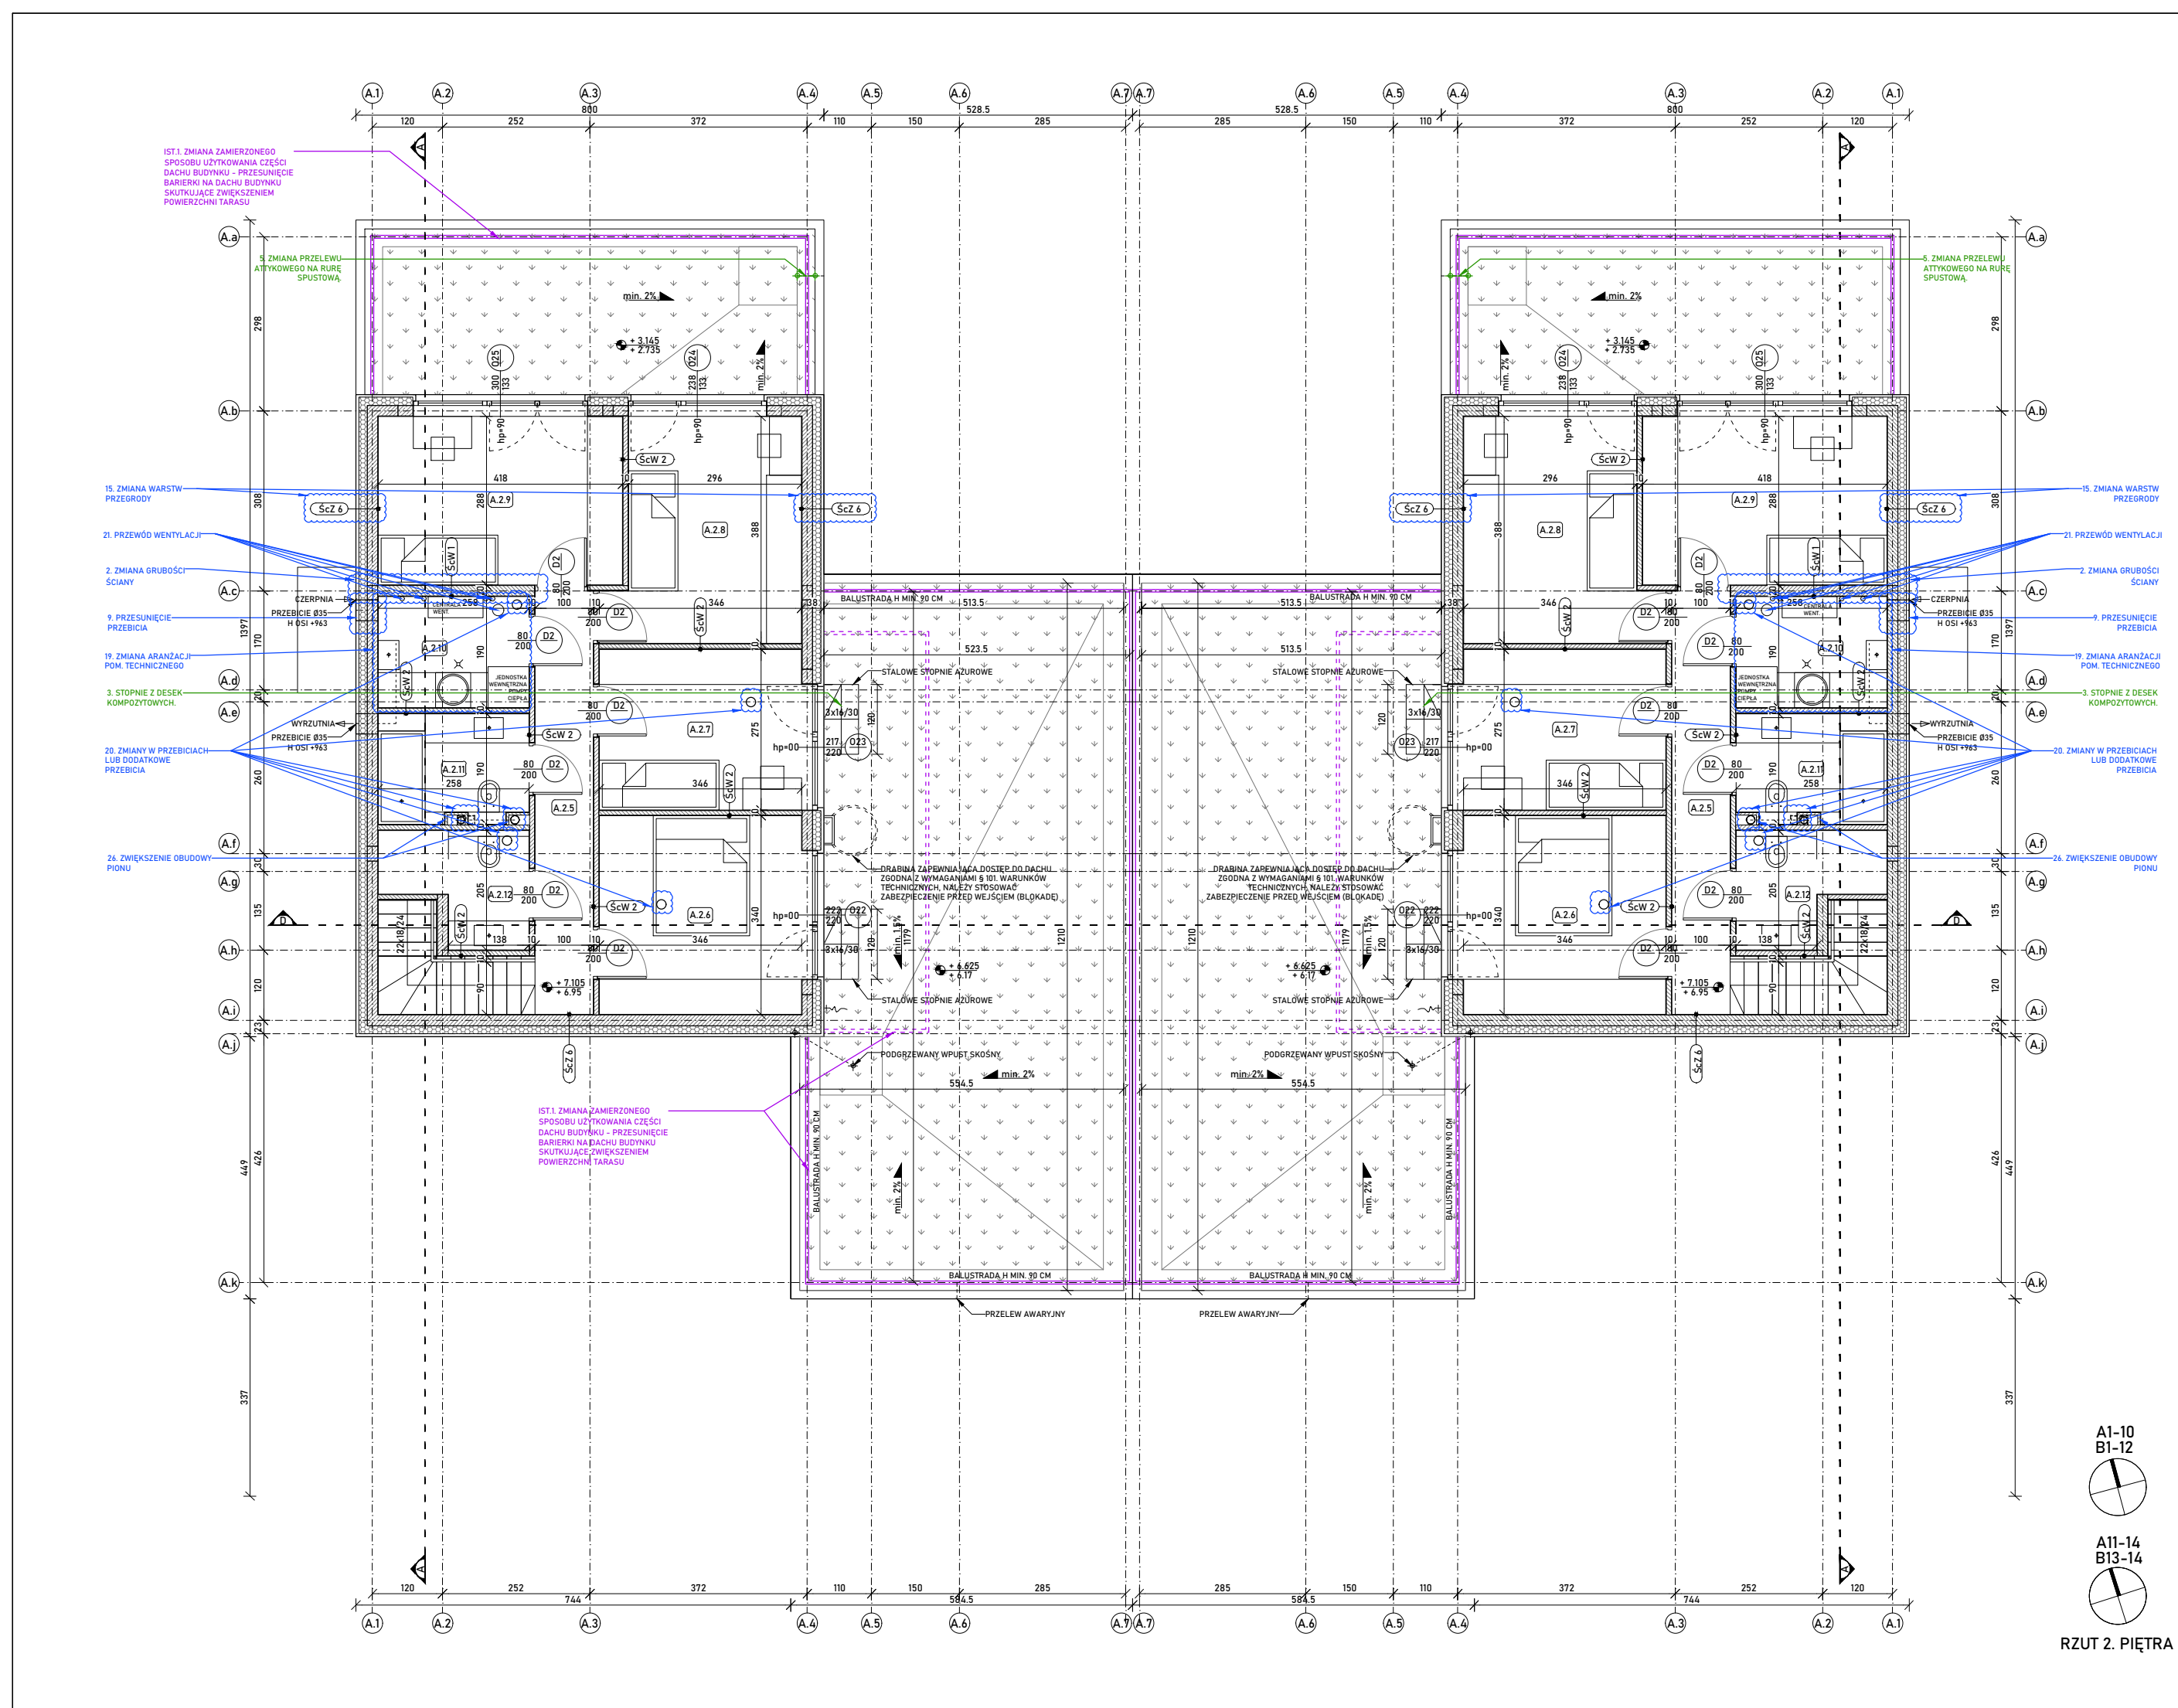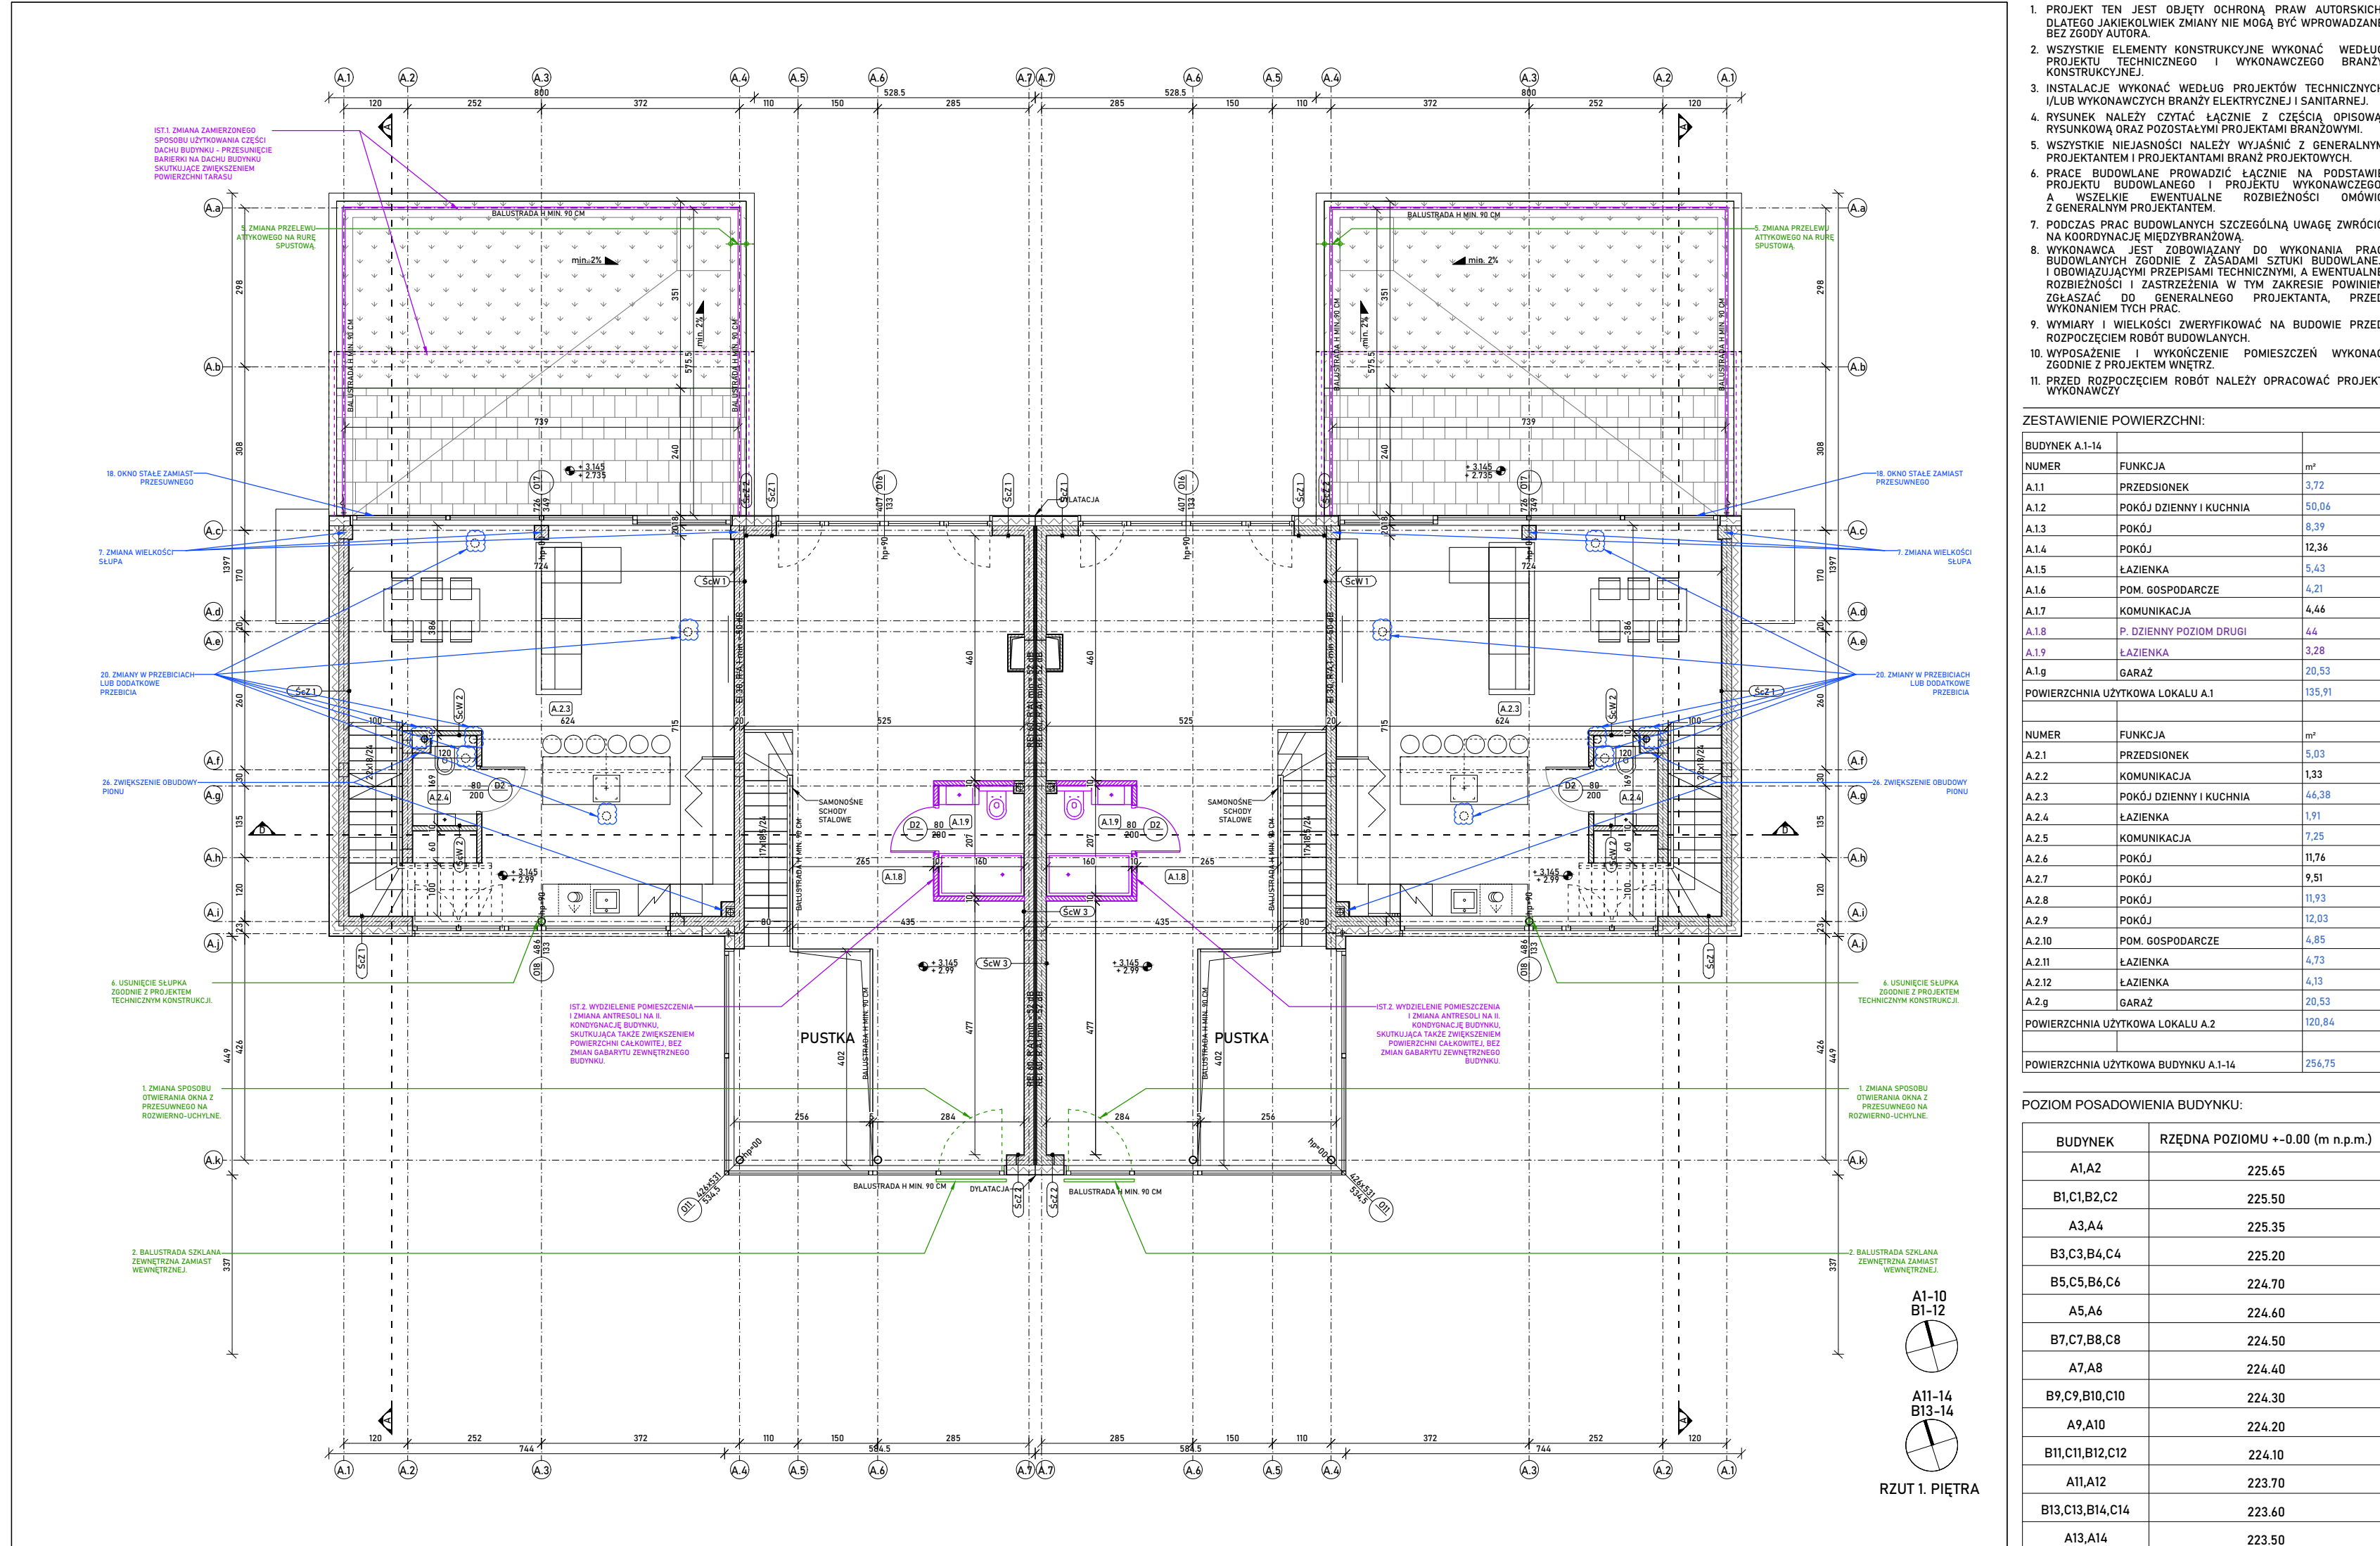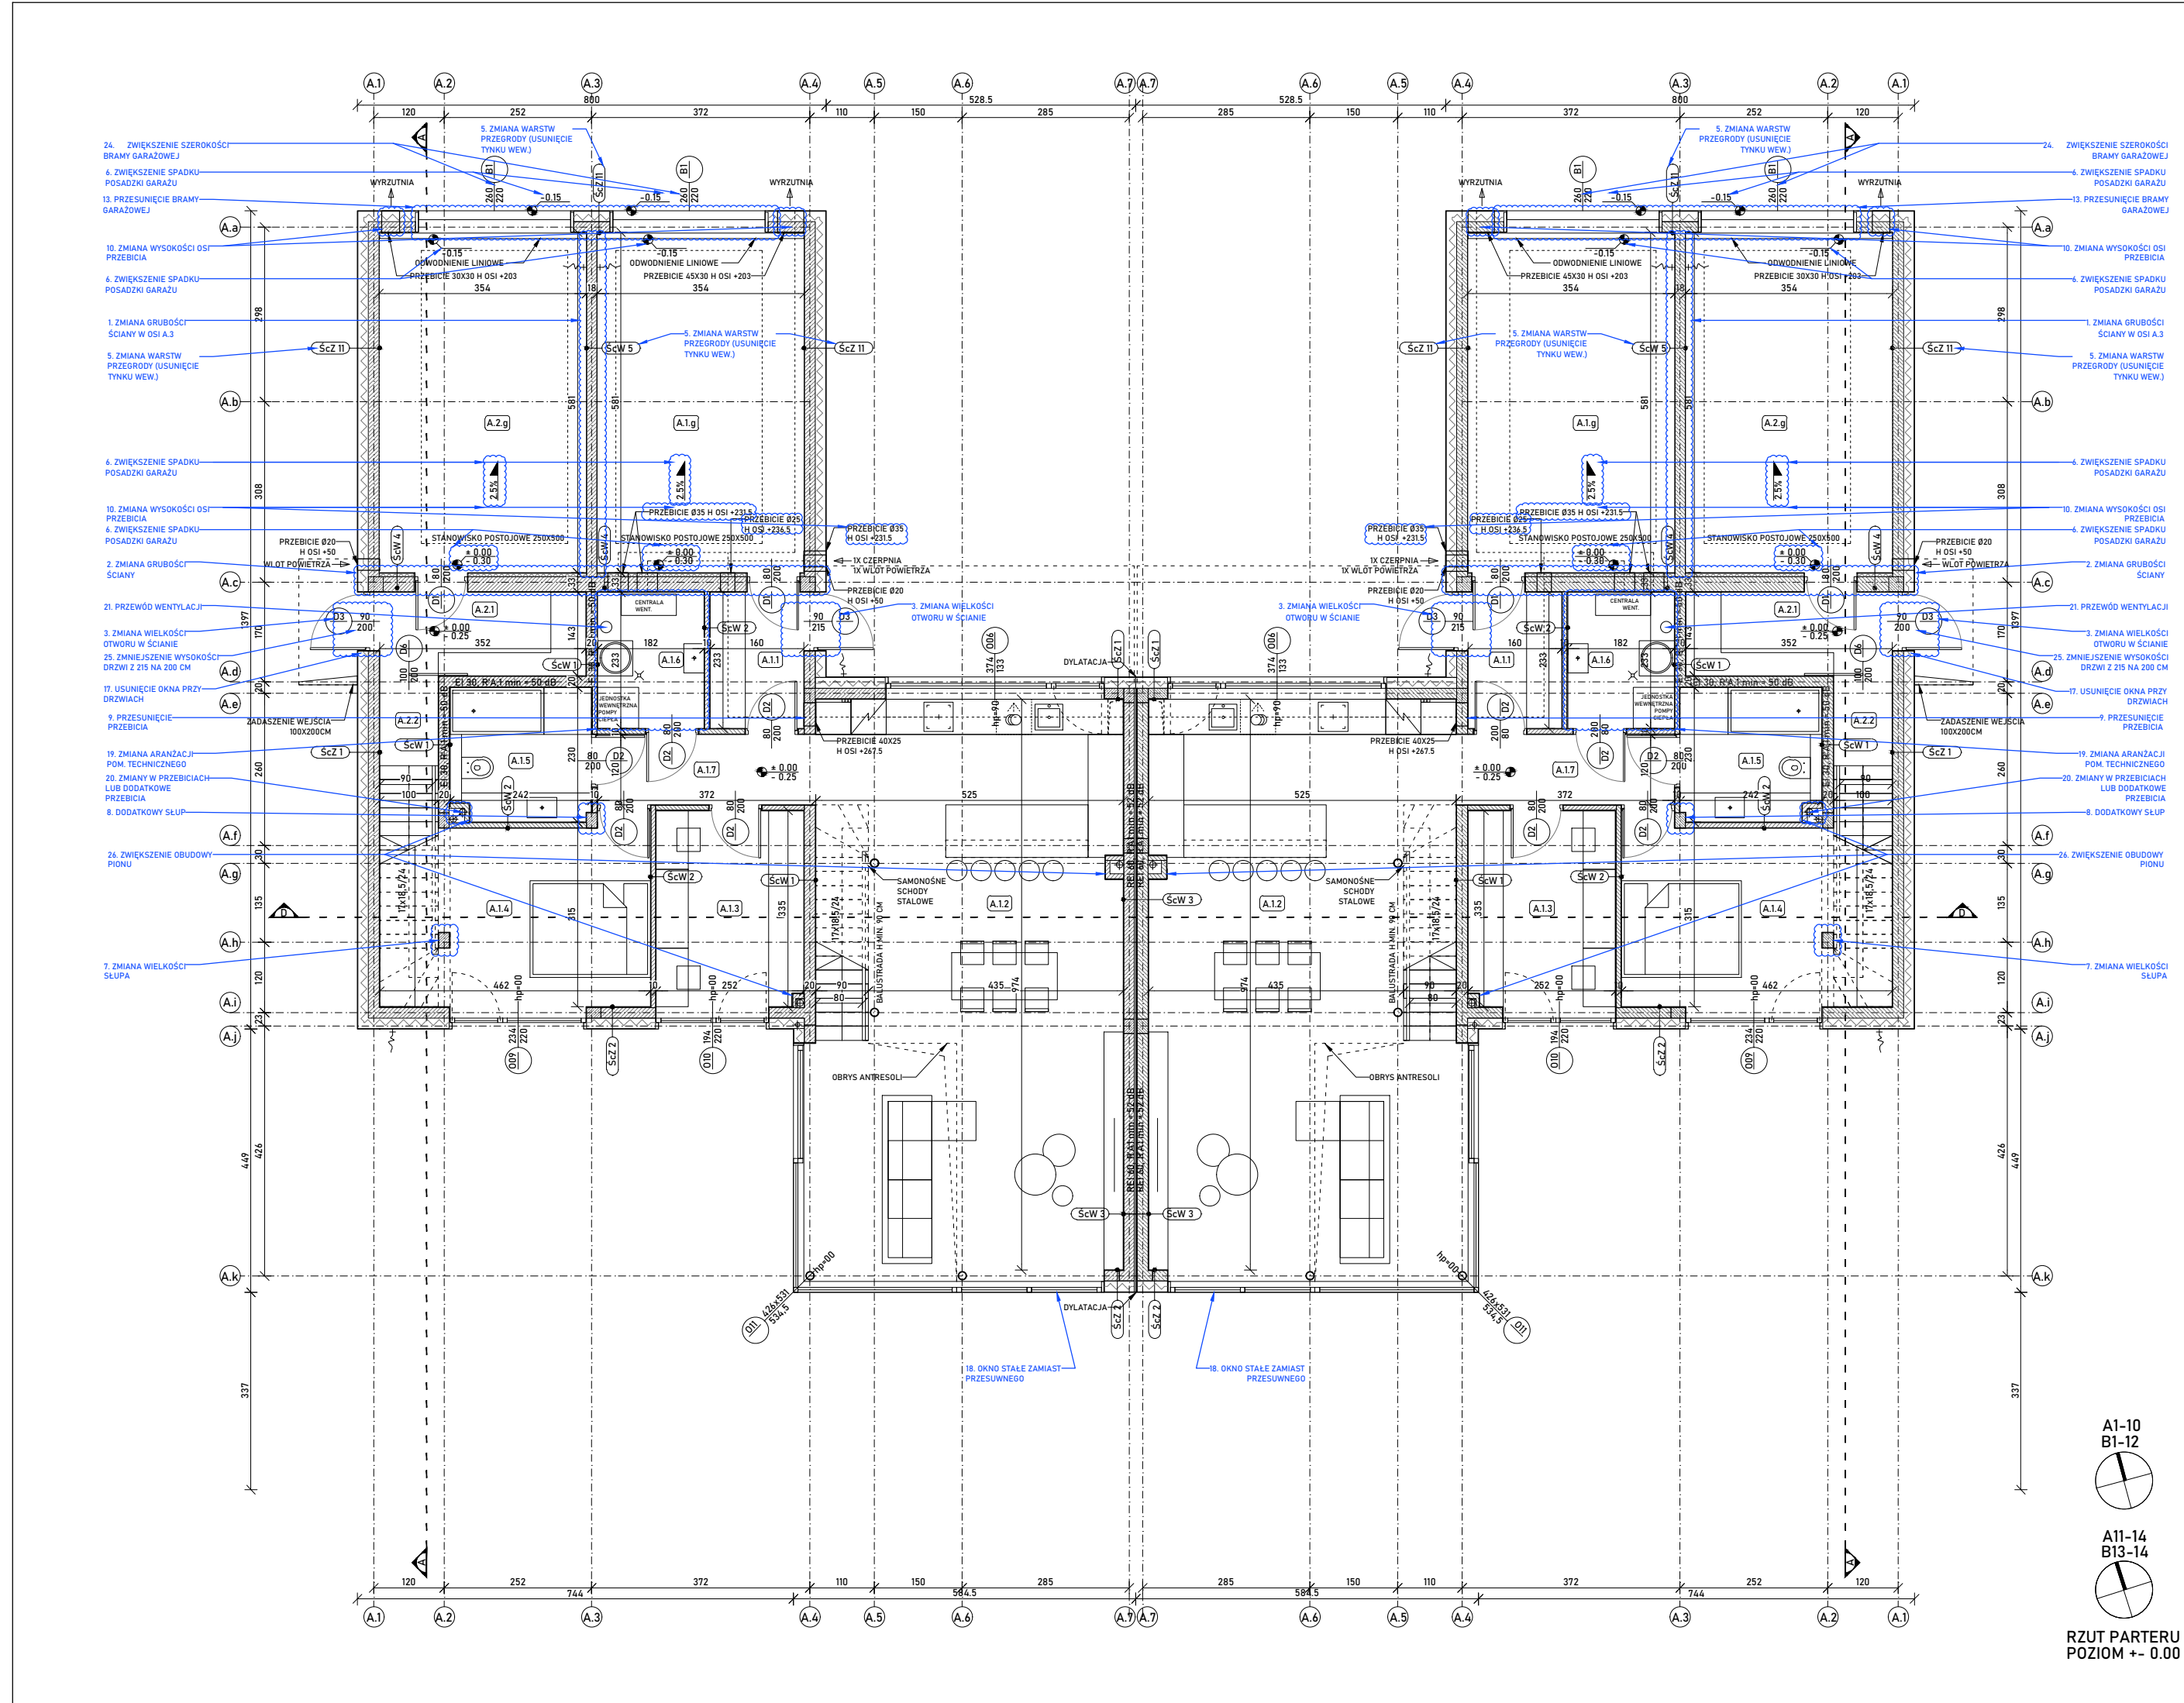

- [illegible]

ZESTAWIENIE POWIERZCHNI:		
BUDYNEK A.1-14		
NUMER	FUNKCJA	PRZ.
A.1.1	PRZEDSIĘBIO	3,72
A.1.2	POKÓJ: DZIENNY I KUCHNIA	30,08
A.1.3	POKÓJ	8,29
A.1.4	POKÓJ	12,36
A.1.5	ŁAZIENKA	5,43
A.1.6	POM. GOSPODARCZE	6,21
A.1.7	KOMUNIKACJA	4,46
A.1.8	P. DZIENNY POZIOM DRUGI	4,64
A.1.9	ŁAZIENKA	3,28
A.1.10	GABINET	20,53
POWIERZCHNIA UŻYTKOWA LOKALU A.1		195,91
BUDYNEK A.2-14		
NUMER	FUNKCJA	PRZ.
A.2.1	PRZEDSIĘBIO	5,03
A.2.2	KOMUNIKACJA	1,33
A.2.3	POKÓJ: DZIENNY I KUCHNIA	66,38
A.2.4	ŁAZIENKA	1,29
A.2.5	KOMUNIKACJA	1,75
A.2.6	POKÓJ	11,76
A.2.7	POKÓJ	9,51
A.2.8	POKÓJ	11,93
A.2.9	POKÓJ	12,03
A.2.10	POM. GOSPODARCZE	4,85
A.2.11	ŁAZIENKA	4,73
A.2.12	ŁAZIENKA	4,03
A.2.13	GABINET	20,53
POWIERZCHNIA UŻYTKOWA LOKALU A.2		120,84
BUDYNEK A.3-14		
NUMER	FUNKCJA	PRZ.
POWIERZCHNIA UŻYTKOWA BUDYNKU A.1-14		256,75

POZIOM POSADOWIENIA BUDYNKU:

BUDYNEK	RZĘDNA POZIOMU + 0.00 (m n.p.m.)
A1A2	225.65
B1,C1,B2,C2	225.50
A3A4	225.35
B3,C3,B4,C4	225.20
B5,C5,B6,C6	224.70
A5,A6	224.60
B7,C7,B8,C8	224.50
A7,A8	224.40
B9,C9,B10,C10	224.30
A9,A10	224.20
B11,C11,B12,C12	224.10
A11A12	223.70
B13,C13,B14,C14	223.60
A13,A14	223.50

SPIS ZMIAN NIEISTOTNYCH WEDŁUG PRAWA BUDOWLANEGO W STOSUNKU DO PROJEKTU ARCHITEKTONICZNO-BUDOWLANEGO OBJĘTEGO DECYZJĄ NR 171/6740.1/2023 Z DNIA 13 LUTEGO 2023 R. ZMIENIONEGO DECYZJĄ NR 919/6740.1/2024 Z DNIA 07.10.2024 R.:

1. ZMIANA SPOSOBU OTWIERANIA DRZWI Z PRZESUNIEM NA
2. ZMIANĄ KĄTA OTWIERANIA
3. BALKONOSTAJA SZKLANA ZEWNĘTRZNA ZMIANA WEWNĘTRZNEJ
5. STÓPKE Z DESEK KOMPOZYTOWYCH
4. ZMIANA WYPEŁNIENIA LUSTRA SZKLANE
6. ZMIANA PRZEWŁOKI ATYPOWEGO NA RURĘ SPOUSTOWĄ
i ŁUSKINIE SŁUPKA ZŁOCONE Z PROJEKTEM TECHNICZNYM
KONSTRUKCJI

TEMATY WYKAZANE W DOKUMENTACJE OBIEKTU ZMIENNY
PODZIAŁENIEM NA BUDOWE: DECYZJA NR 1919/24-1/2022 Z DNIA
07.09.2024 R.

SPIS DZIAŁ ISTOTNYCH WEDŁUG PLANU BUDOWLANEGO W
STOSUNKU DO PROJEKTU ARCHITEKTONICZNO-BUDOWLANO
OBIEKTU DECYZJA NR 1919/24-1/2022 Z DNIA 13 LUTEGO 2023 R.

1ST1 ZMIANA ZAMIERZONEGO SPOSOBU UŻYTKOWANIA CZĘŚCI
DACHU BUDYNKU - PRZESUNIĘCIE BARIERKI NA DACH BUDYNKU
KUCHNIA ZWIĘKSZENIECIEM POWIERZCHNI
1ST2 WYŻOŁCENIE POMIESZCZENIA I ZMIANA ANTRESOLI NA II
KONDYGNACJI, ZWIĘKSZENIE KUCHNIA TAKŻE ZWIĘKSZENIE
POWIERZCHNI CAŁKOWITEJ, ZMIANA SEGMENTU ZEWNĘTRZNEGO
BUDYNKU.

— ELEMENTY DODANE
 ELEMENTY USUNIĘTE

SPIS ZMIAN NIEISTOTNYCH WEDŁUG PRAWA BUDOWLANEGO W STOSUNKU DO PROJEKTU ARCHITEKTONICZNO-BUDOWLANOGO
OBJĘTOŚCI DECYZJA NR 17154/63 Z DNIA 13 LUTEGO 2023 R.

1. ZMIANA GRUBOŚCI ŚCIANY W GÓR A3

2. KONTAKTY DŁUGIE SIENIECH POWIERZCHNI A2.g A.3.g

3. ZMIANA GRUBOŚCI ŚCIANY (SKUTKOWIE ZMIANA POWIERZCHNI A2.1, A2.5 A.2.8, A2.9, A2.10, A2.11 A.1A)

4. ZMIANA WIELKOŚCI OTWORU W SCIANIE

5. PRZESUNĘCIE OTWORU

6. ZMIANA WARTOŚCI PRZEGRODY (USUNIĘCIE TYNKU WŁEW)

7. ZMIANA SPADKU PODŁOGI (GAZARU) I STROPIWY WARTOŚCI

8. ZMIANA WIELKOŚCI ŚLĄPA (KONTAKTY ZMIANA POWIERZCHNI A2.3)

9. RODKOWY SŁUP

10. ZMIANA DŁUGOŚCI POWIERZCHNI A.15)

11. PRZESUNĘCIE PRZEBIEGA

12. ZMIANA WYKOSYŚCI OSI PRZEBIEGA

13. ZMIANA GRUBOŚCI KONSTRUKCJA STROPU

14. OGRZEWANIE NADPŁAZU

15. PRZESUNĘCIE BRAMY GARAZOWEJ

16. ZMIANA DŁUGOŚCI DŁOŻYDU

16. ZMIANY FUNDAMENTÓW ZGODNIE Z PROJEKTEM TECHNICZNYM KONSTRUKCJI

[illegible]

= OŚCIEŻ TYNKOWANA

INFORMACJE

NACZA OKREŚLIŁ RUSZKOWSKI

BUDOWA 38 BUDYNÓW MIESZKALNYCH JEDNORODZINNYCH W ZABŁOUDIE (BŁDNACZCE) Z 14 GARAJAMI, ZAMKNIĘTĄ, WYŁOŻONYM STALĄ I 14 GARAJÓW ZAMKNIĘTĄ, WOLNOSTOJĄCĄ, ZŁOŻONYM WYŁOŻONYM TERENEM, SPOŁOŻĄ ZWIĘZNYCH, MARIAM UDROWY, ZWIĘZNYCH STANOWISKAMI POSTYJOWYMI, ODJĘCIEM I BUDOWĄ

POCZĄTKIEM

BRONOW

BARTŁOMIEJ DRABIK	MP01A/077/2013	
Tytuł (tytuły)		

ELEMENT PROJEKTU		NUMER RYSUNKU
PROJEKT ARCHITEKTONICZNO-BUDOWLANY		
BRANŻA		
ARCHITEKTURA		
DATA I WERSJA		A.03
24.09.2025 REV. 09		
SKALA		
1:100		

ROZPOWIESZANIE NIE WSKAZUJE ODDZIAŁYWAŃ ORAZ JEJ FRAGMENTÓW W JAKIEJKOLWIEK FORMIE ORAZ KOPLOWANIE TAKIĄ JEST DZIAŁA AUTORA JEST ZABRONIONE NA MIECY USTAWY O PRAWACH AUTORSKICH I PRAWACH PODROBICZNYCH


1. PROJEKT NIE JEST OBJEKT OCHRONY PRAW AUTORSKICH.
2. WSKAZANE ELEMENTY KONSTRUKCYJNE SĄ WYKONANE WEDŁUG PROJEKTU TECHNICZNEGO I WYKONAWCZEGO KONSTRUKCJI.
3. INSTALACJE WYKONANE WEDŁUG PROJEKTU TECHNICZNEGO (LUB WYKONAWCZEGO) BRANŻY ELEKTRYCZNEJ I SANITARNEJ.
4. RYSUNEK NALEŻY CZYTAĆ ŁĄCZNIE Z CZĘŚCIĄ SPISOWĄ, RYSUNKOWĄ ORAZ DOPOSIĄTAMI PROJEKTAMI BRANŻOWYMI.
5. WSKAZANE NIEJASNOŚCI NALEŻY WYJAŚNIĆ Z GENERALNYM PROJEKTANTEM I PROJEKTANTAMI BRANŻ PROJEKTOWYCH.
6. PRACE BUDOWLANE PRACOWNIKI ŁĄCZNIE NA PRZEDSTAWIENIE PROJEKTU BUDOWLANEGO I PROJEKTU WYKONAWCZEGO Z GENERALNYM PROJEKTANTEM.
7. PODCZAS PRAC BUDOWLANICH SZCZEGÓLNĄ UWAGĘ ZWROCIĆ NA WYKONANIE WIEDZĄCZĄCĄ.
8. WYKONANIE JEST ZOBOWIĄZANE DO WYKONANIA PRAC BUDOWLANICH ZODPOWIEDNIE Z JAKIŚMI SZTETNĄ I ODBYWAJĄCĄ PRZEPISAMI TECHNICZNYMI, A EWENTUALNE ROZBIEŻNOŚCI I ZASTRZEŻENIA W TYM ZAKRESIE POWINNI BYĆ WYKONANE PRZEZ PROJEKTANTA, PRZED WYKONANIEM TYCH PRAC.
9. WYMIARY I WŁASNOŚCI ZWIERZĄCĄCĄ NA BUDOWIE PRZED WYKONANIEM PRAC BUDOWLANICH.
10. WYPOSAŻENIE I WYKONANIE POMIESZCZENI WYKONANE ZODPOWIEDNIE Z PROJEKTEM WYKONAWCZYM.
11. PRZED ROZPOCZĘCIEM ROBÓT NALEŻY OPRAWIĆ PROJEKT WYKONAWCZY.

ZESTAWIENIE POWIERZCHNI:


NUMER	FUNKCJA	m ²
A1.1	PRZEDSIÓDNEK	3,77
A1.2	POM. DZIENNY KUCHNIA	10,56
A1.3	POM. J	8,39
A1.4	POM. J	12,36
A1.5	ŁAZIENKA	5,43
A1.6	POM. GOSPODARCZE	6,21
A1.7	KOMUNIKACJA	4,46
A1.8	P. DZIENNY POZIOM DRUGI	4,46
A1.9	ŁAZIENKA	5,38
A1.10	GARAŻ	20,53
POWIERZCHNIA UŻYTKOWA LOKALU A1		135,91
A2.1	PRZEDSIÓDNEK	5,03
A2.2	KOMUNIKACJA	1,23
A2.3	POM. DZIENNY KUCHNIA	44,58
A2.4	ŁAZIENKA	1,91
A2.5	KOMUNIKACJA	7,25
A2.6	POM. J	11,76
A2.7	POM. J	9,51
A2.8	POM. J	11,73
A2.9	POM. J	12,03
A2.10	POM. GOSPODARCZE	4,05
A2.11	ŁAZIENKA	6,73
A2.12	ŁAZIENKA	4,13
A2.13	GARAŻ	20,53
POWIERZCHNIA UŻYTKOWA LOKALU A2		120,84
POWIERZCHNIA UŻYTKOWA BUDYNKU A1-A2		256,75

POZIOM POSADOWIENIA BUDYNKU:


BUDYNEK	RZĘDNA POZIOMU ±0.00 (m n.p.m.)
A1.2	225.65
B1.C1.B2.C2	225.50
A3.A4	225.35
B3.C3.B4.C4	225.20
B5.C5.B6.C6	224.70
A5.A6	224.60
B7.C7.B8.C8	224.50
A7.A8	224.40
B9.C9.B10.C10	224.30
A9.A10	224.20
B11.C11.B12.C12	224.10
A11.A12	223.70
B13.C13.B14.C14	223.60
A13.A14	223.50

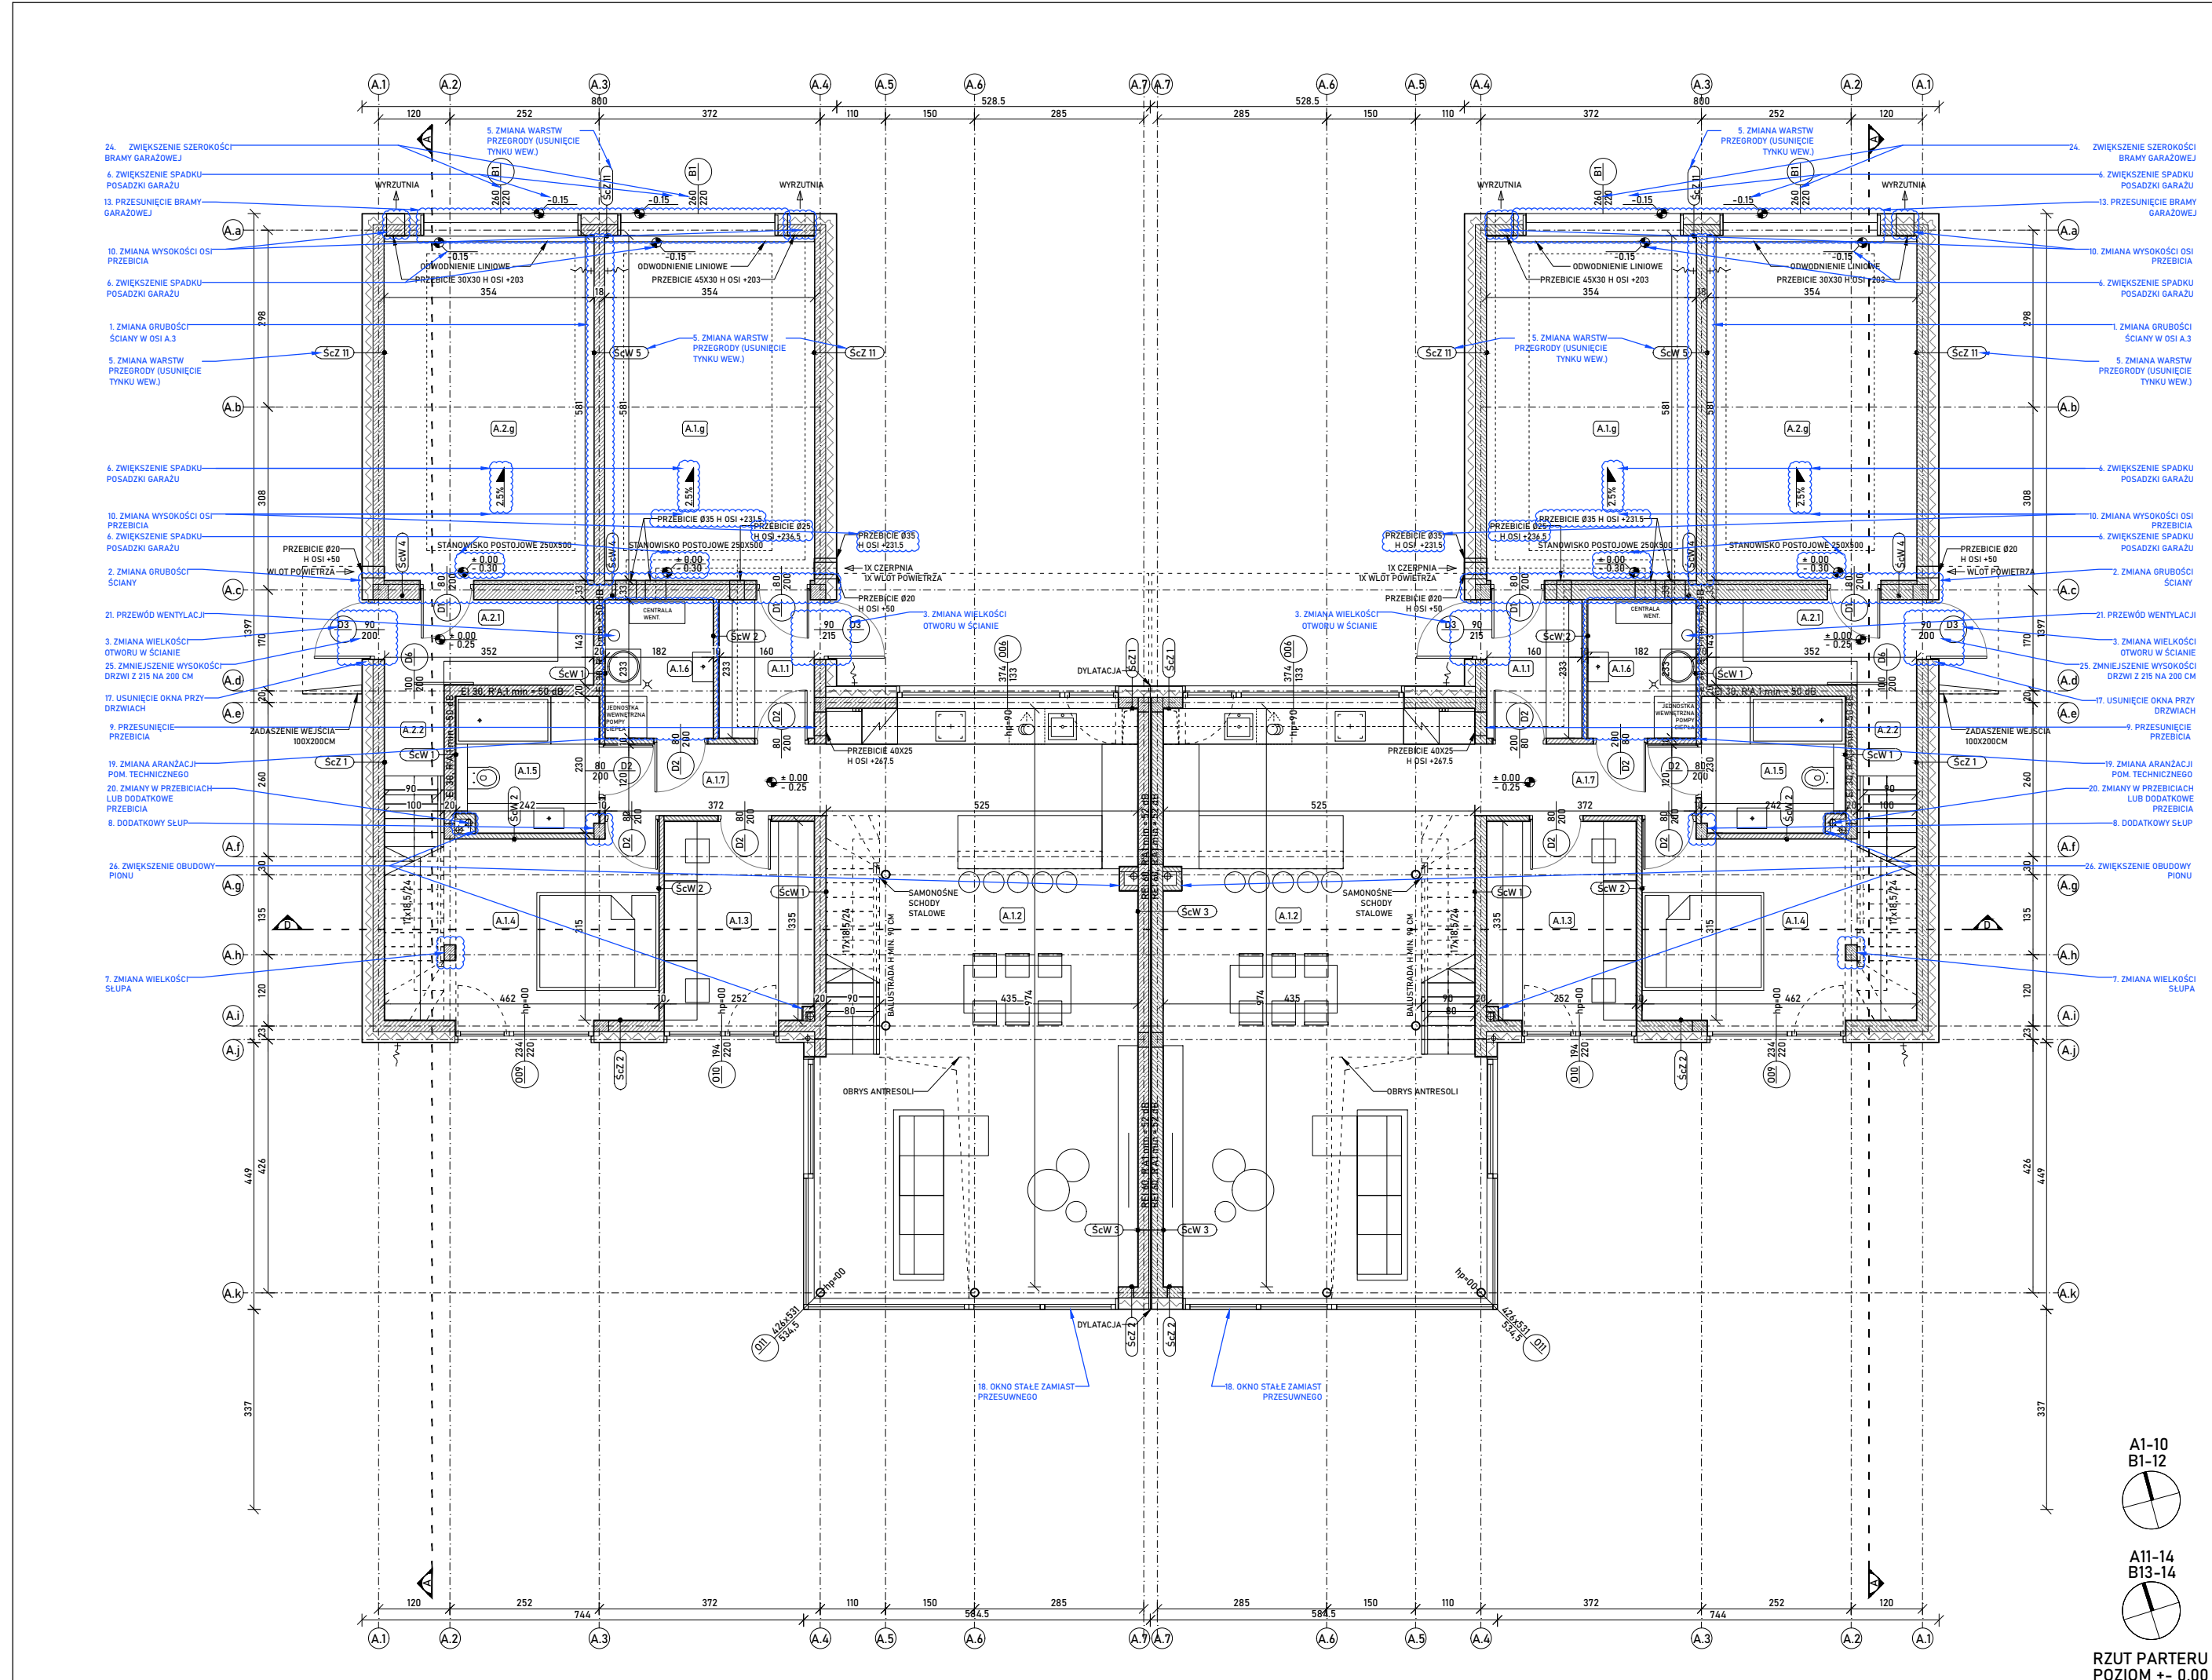


RZUT PARTERU
POZIOM ±0.00

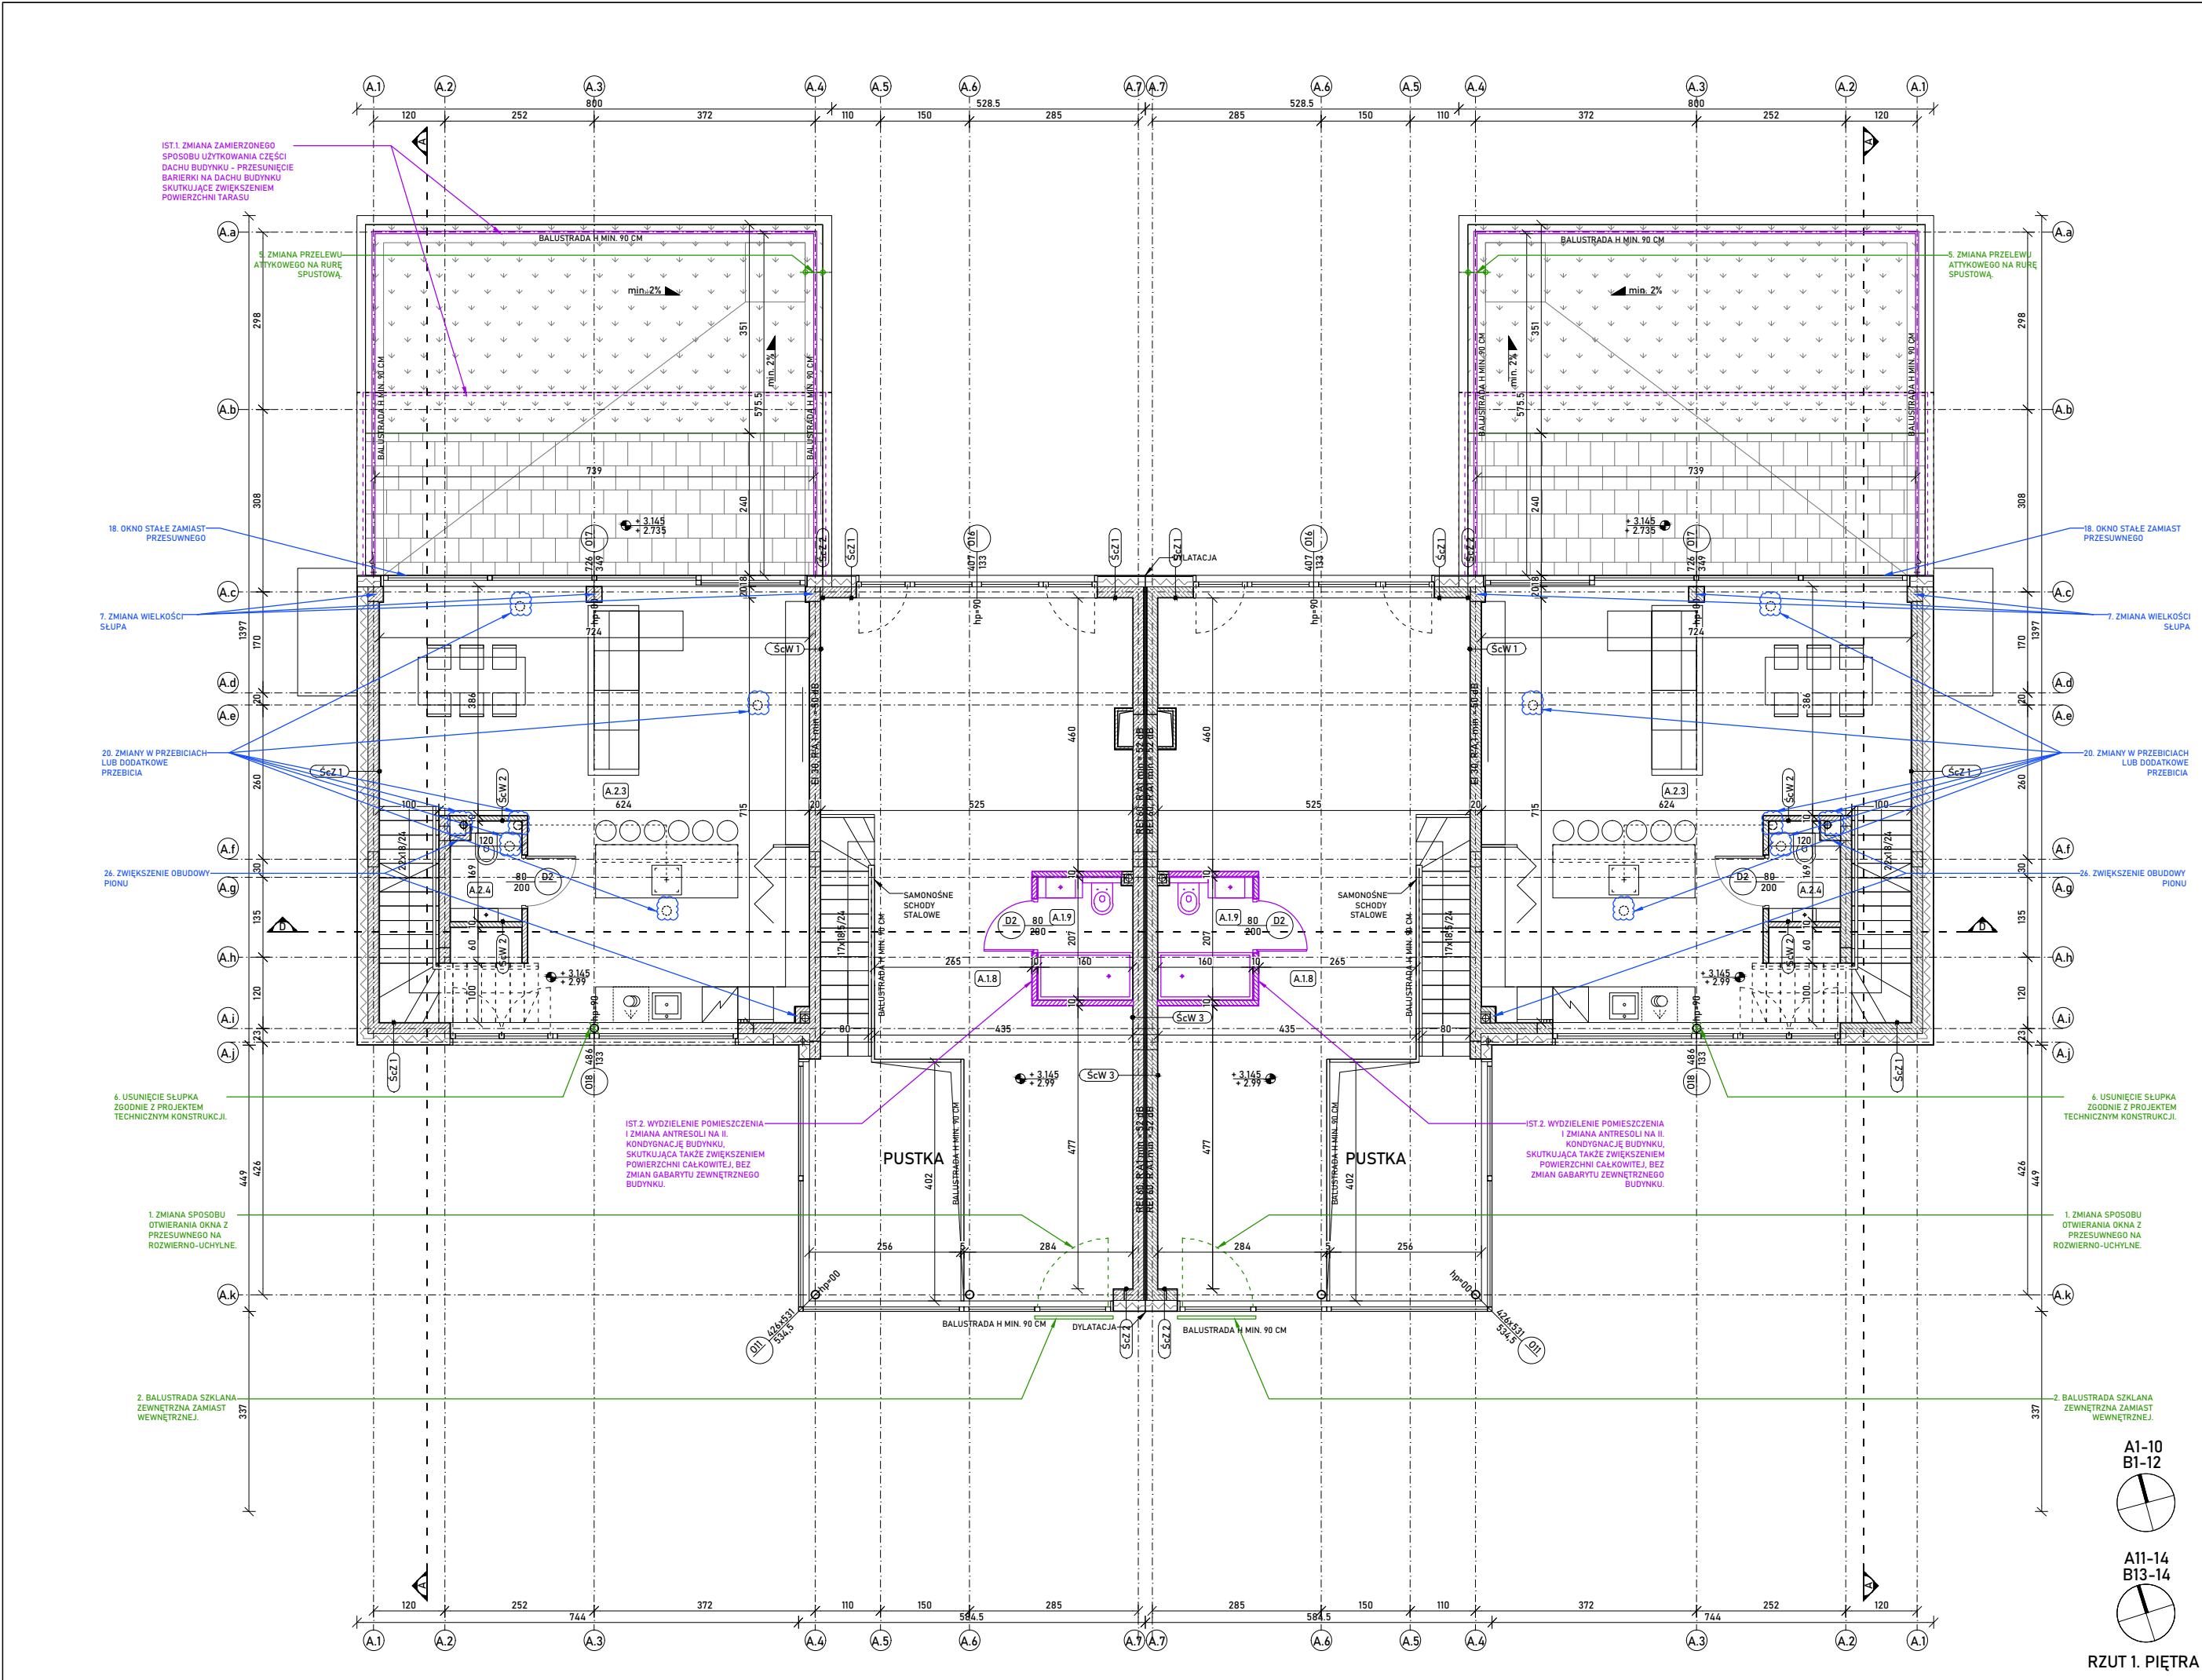

RZUT I. PIĘTRA


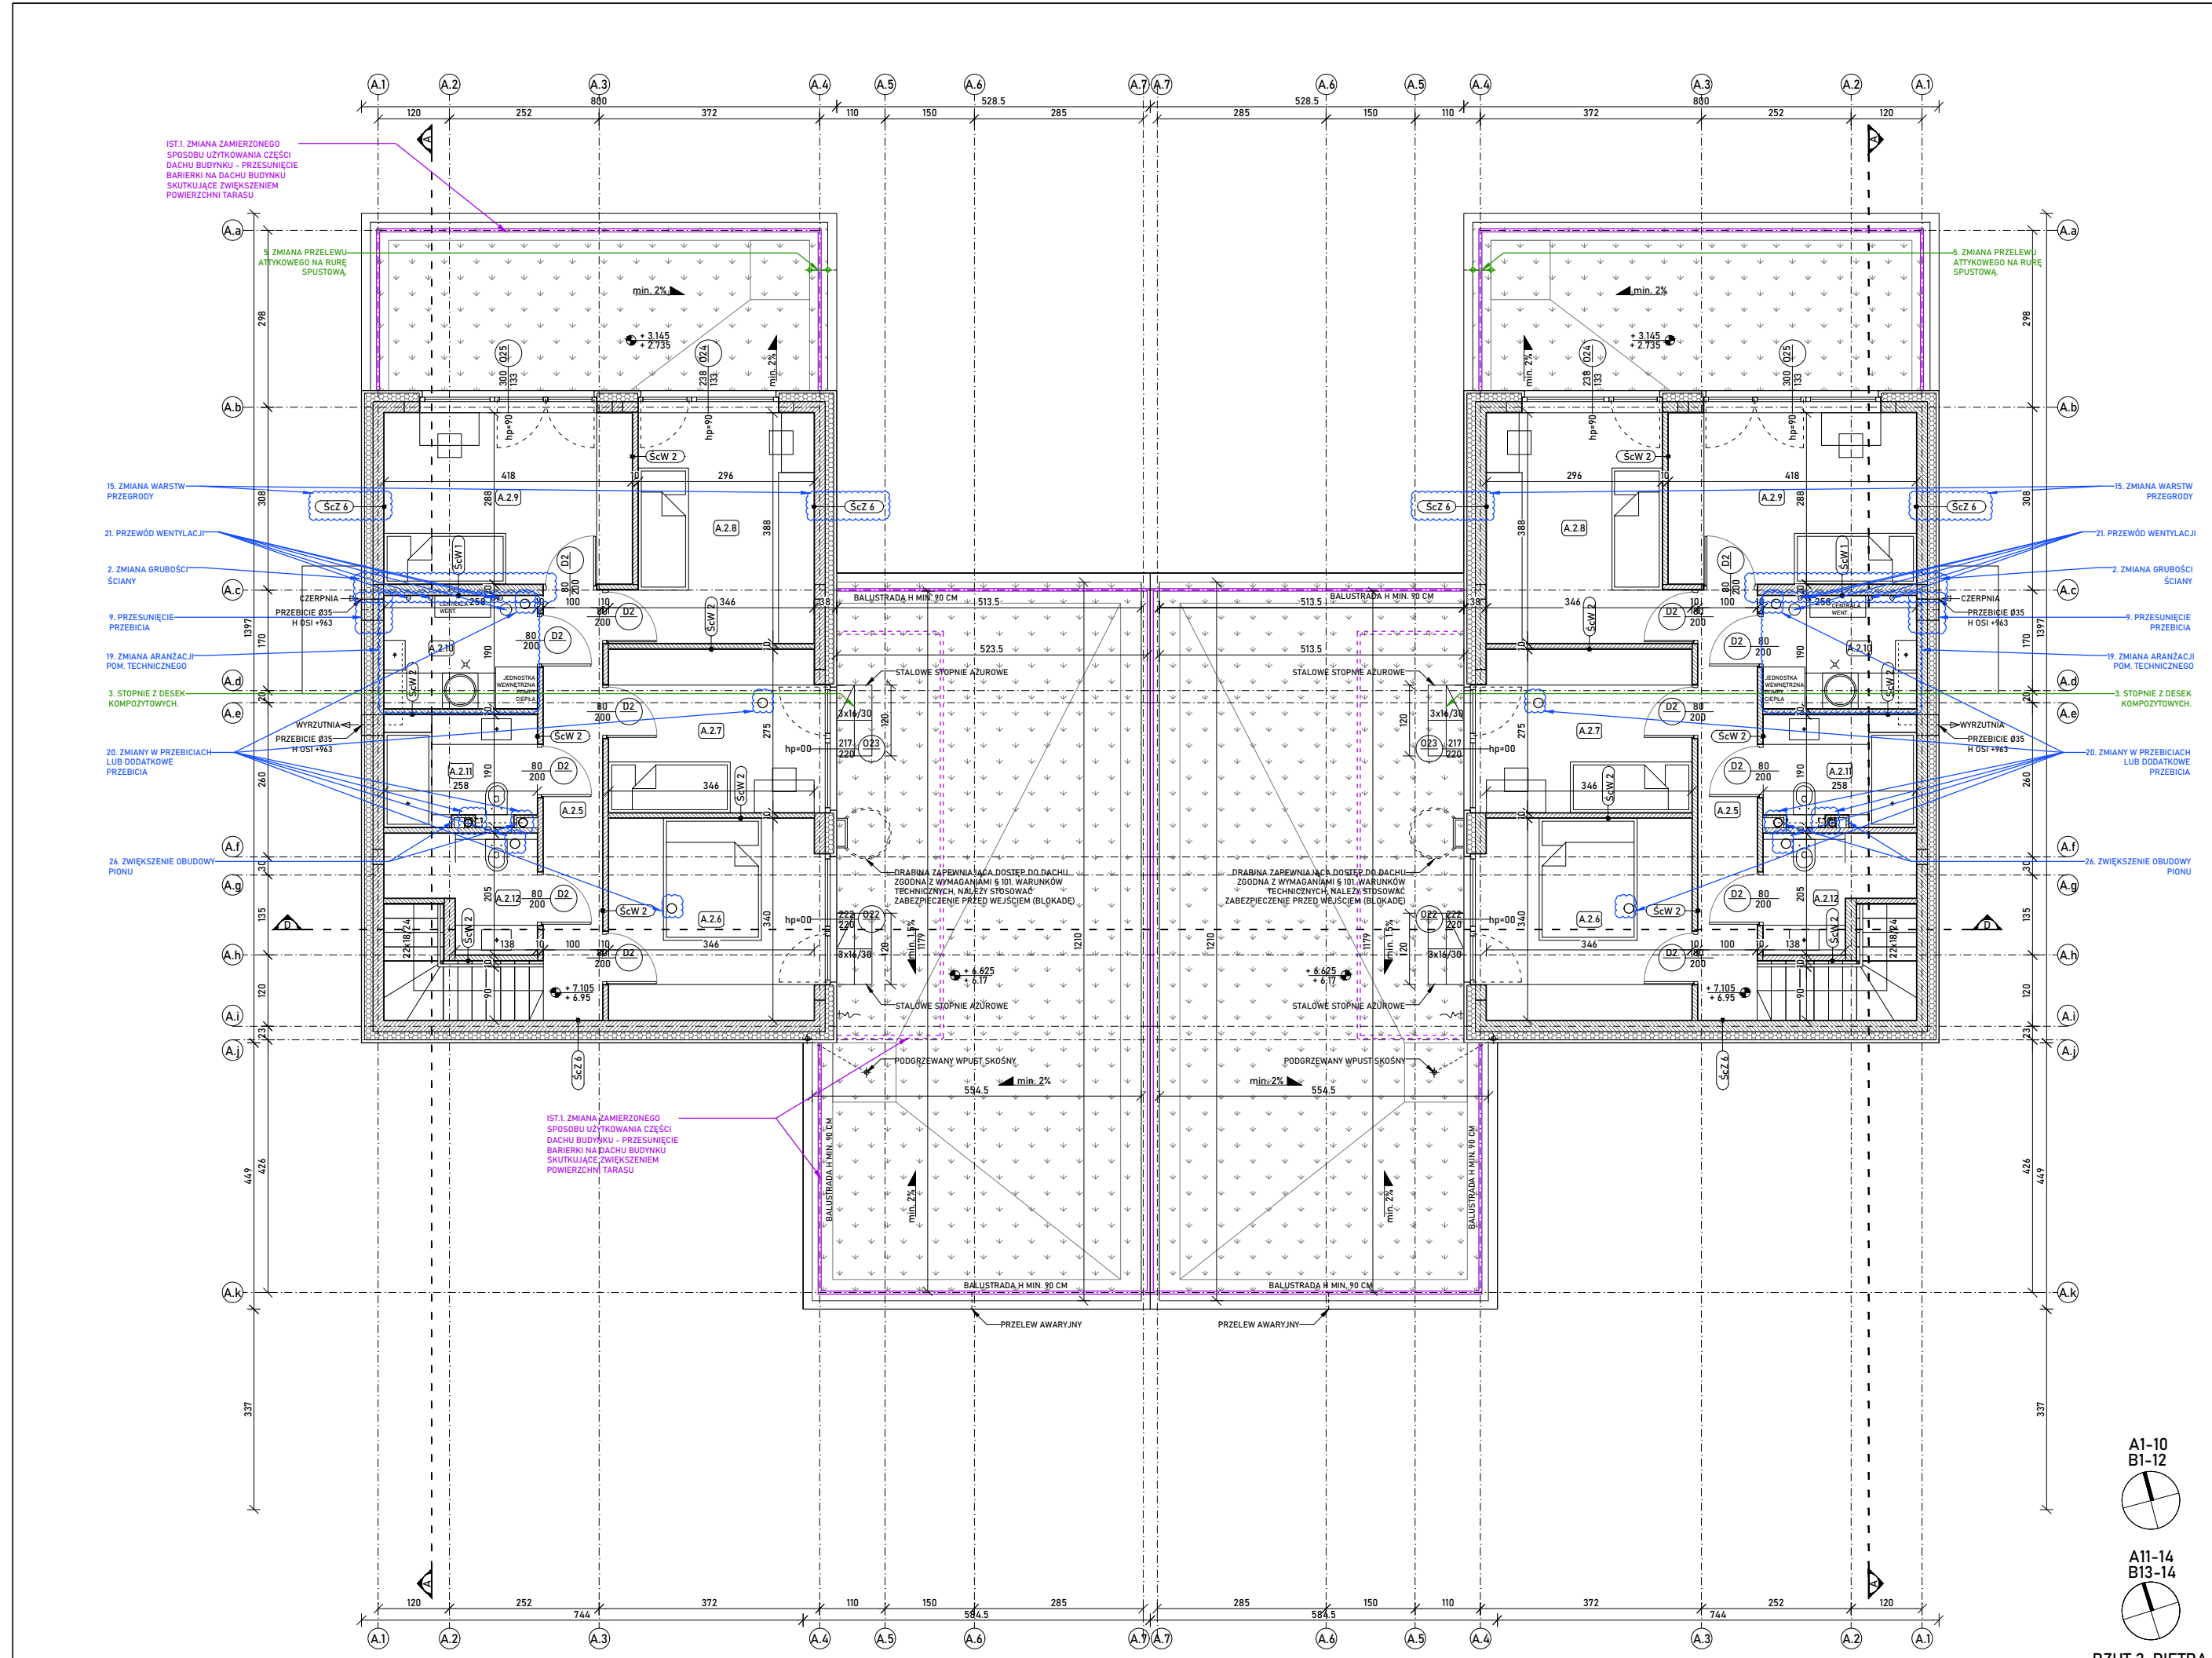


RZUT 2. PIĘTRA

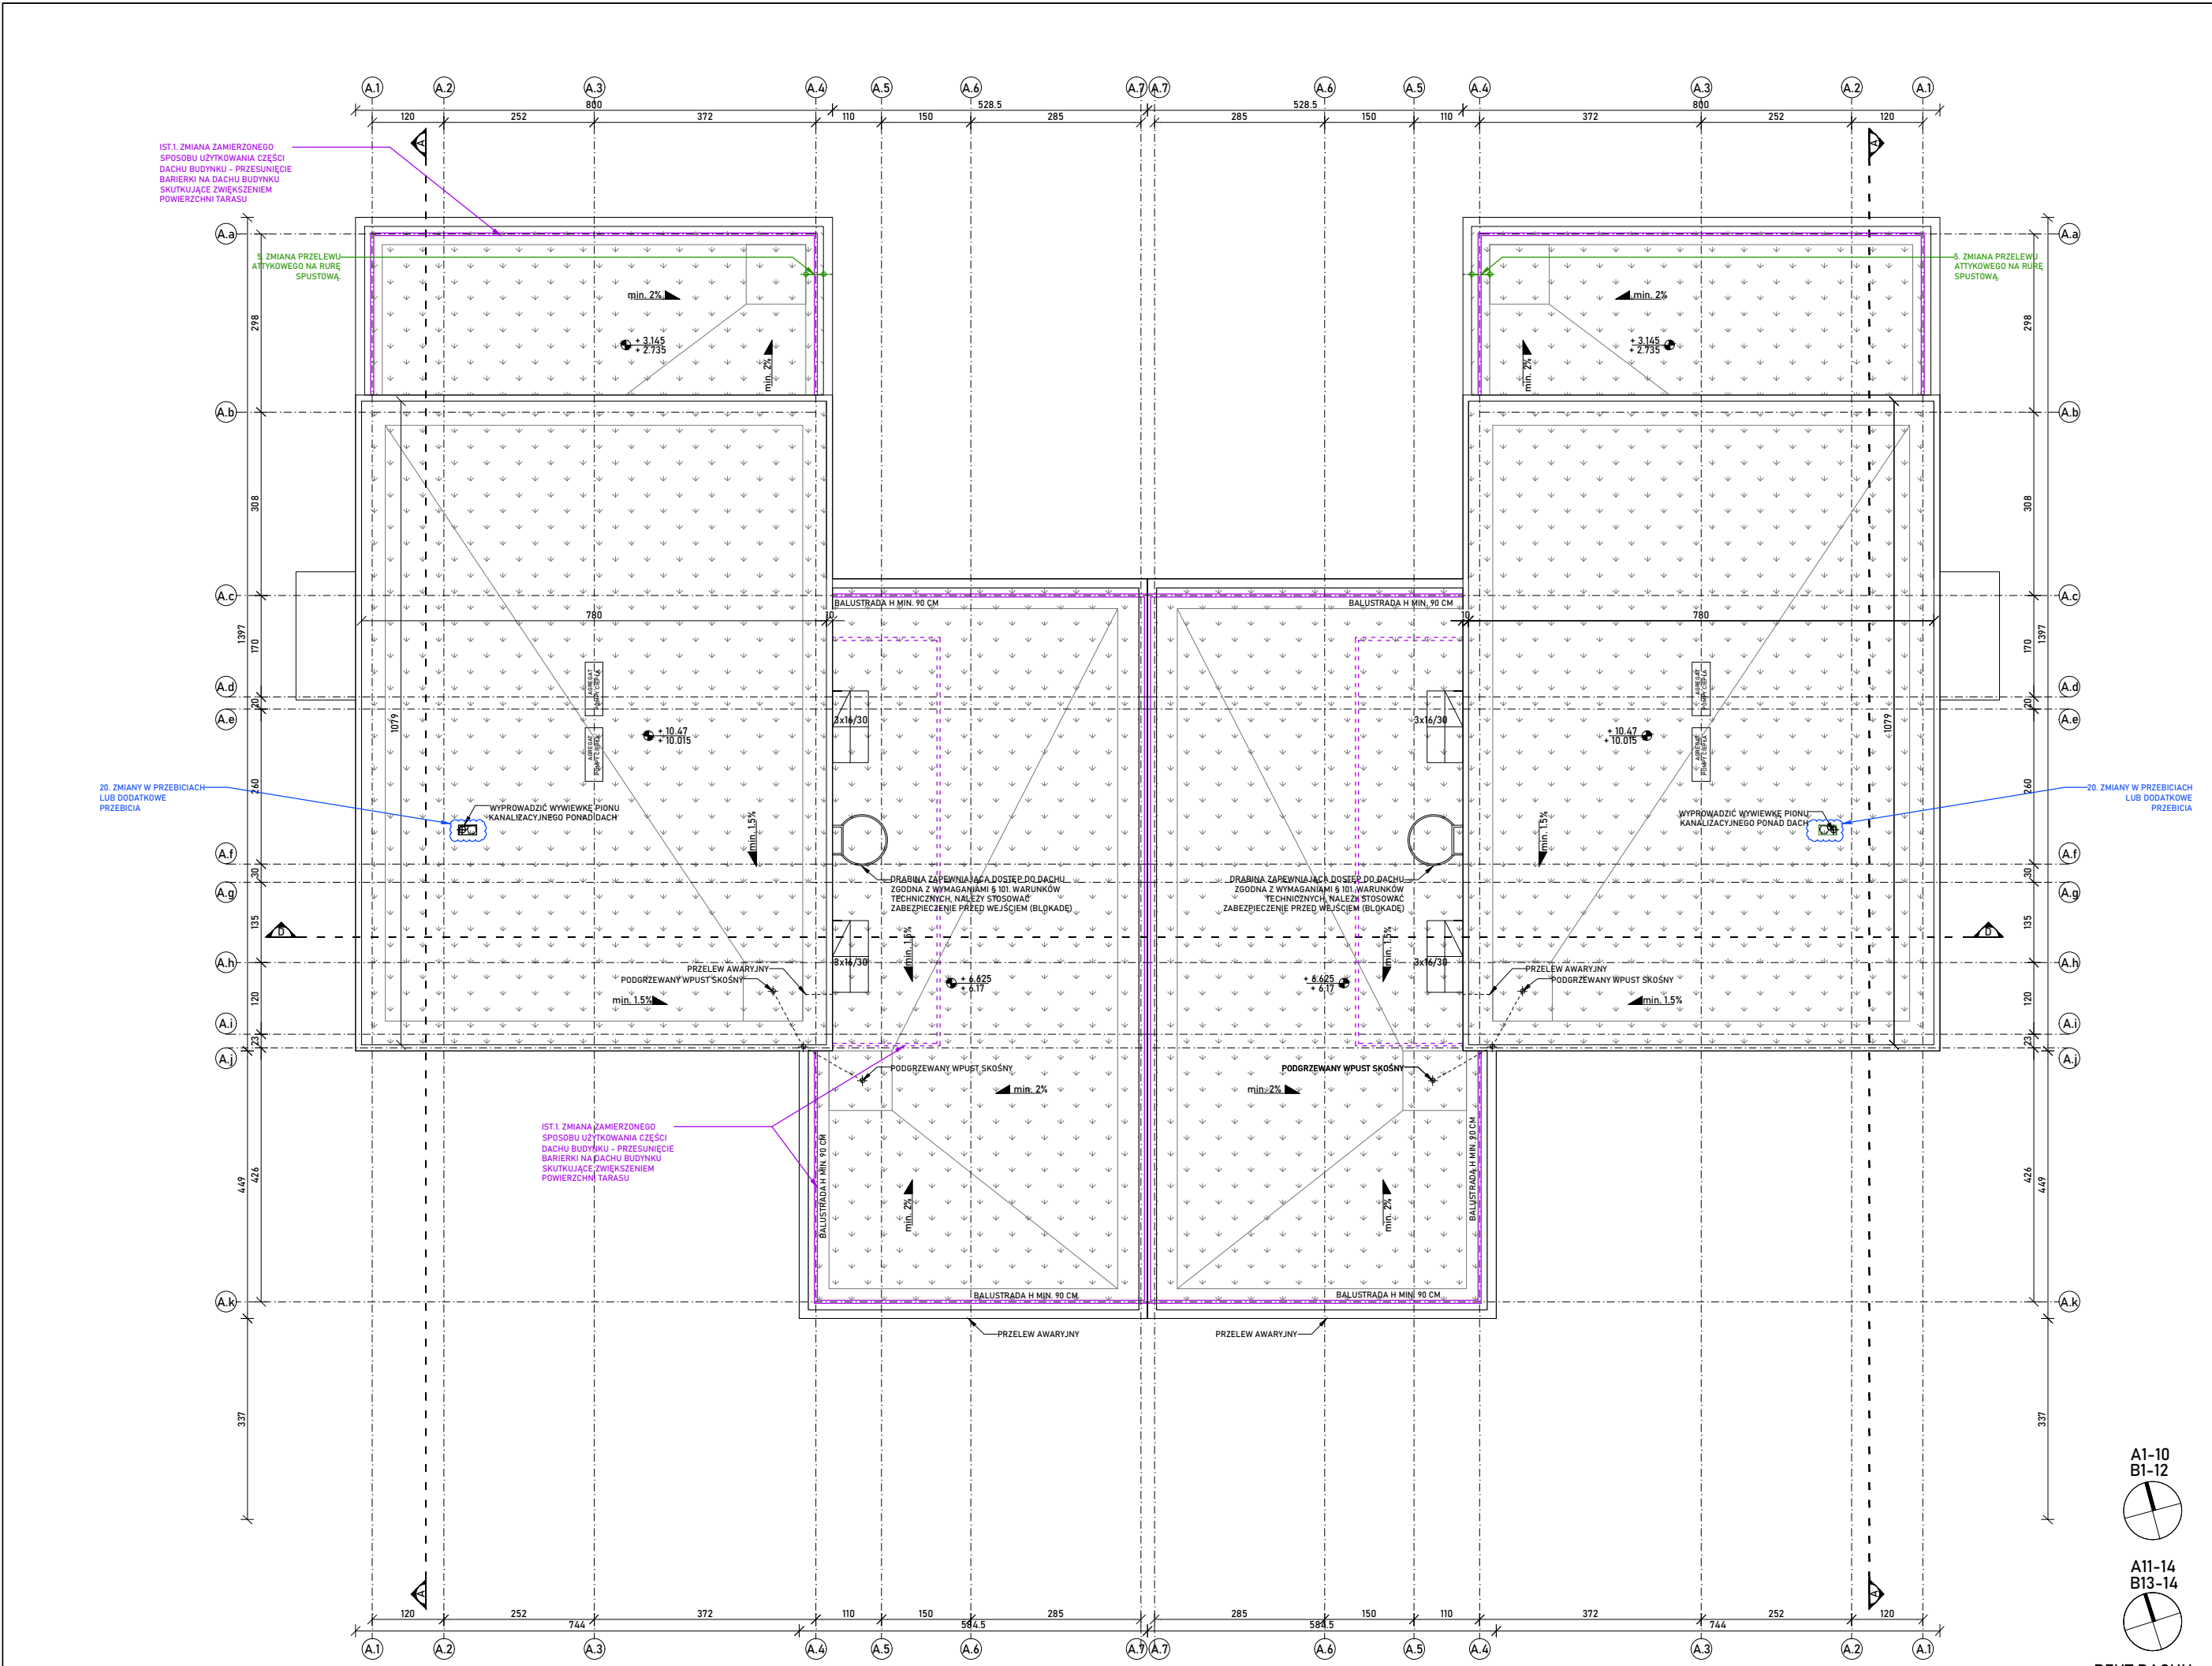

RZUT DACHU

- SPIS ZMIAN NIEISTOTNYCH WEDŁUG PRAWA BUDOWLANEGO W STOSUNKU DO PROJEKTU ARCHYTEKTONICZNO-BUDOWLANEGO ORAZ DO DECYZJI NR PRY.14/1024 Z DNIA 13.11.2023 R. ZMIENIONEGO DECYZJĄ NR PRY.14/1024 Z DNIA 07.10.2024 R.
1. ZMIANA SPOSOBU OTWIERANIA OKNA Z PRZESZKONEM NA ROZBIEŻNOŚCIACH.
 2. BALUSTRADE SZKLANA ZEWNĘTRZNA ZAMIAST WEWNĘTRZNEJ.
 3. STROPIE Z DZIEK KOMPOZYCYJNYCH.
 4. ZMIANA WYPEŁNIENIA BALUSTRAD NA SZKLANO.
 5. ZMIANA PRZELĘWY ATTROFOWA NA KURSE SPOTYKOWA.
 6. LUSZKOWE SŁUPY ZODPOWIEDNIE Z PROJEKTEM TECHNICZNYM KONSTRUKCJI.
- ZMIANY WYKAZANE W DOKUMENTACJI OBJEKTU ZMIENIENIEM POSADOWIENIA NA BUDOWIE, DECYZJĄ NR PRY.14/1024 Z DNIA 07.10.2024 R.
- SPIS ZMIAN ISTOTNYCH WEDŁUG PRAWA BUDOWLANEGO W STOSUNKU DO PROJEKTU ARCHYTEKTONICZNO-BUDOWLANEGO ORAZ DO DECYZJI NR PRY.14/1024 Z DNIA 13.11.2023 R. ZMIENIONEGO DECYZJĄ NR PRY.14/1024 Z DNIA 07.10.2024 R.
- IST. ZMIANA ZAMIERZENEJ SPOSOBU UŻYTKOWANIA CZĘŚCI DACHU BUDYNKU - PRZESZKONIE BARIERY NA DACHU BUDYNKU.
- IST. ZMIANA WYPEŁNIENIA BALUSTRAD NA SZKLANO.
- IST. WYPEŁNIENIE PRZESZKONIA NA II KONDYCYJACH BUDYNKU, WYPEŁNIENIE TAKŻE ZMIENIENIE POWIERZCHNI CAŁOKWISTE, BEZ ZMIAN BARIIER ZEWNĘTRZNEJ BUDYNKU.
- ELEMENTY DODANE
--- ELEMENTY USUNIĘTE
- SPIS ZMIAN NIEISTOTNYCH WEDŁUG PRAWA BUDOWLANEGO W STOSUNKU DO PROJEKTU ARCHYTEKTONICZNO-BUDOWLANEGO ORAZ DO DECYZJI NR PRY.14/1024 Z DNIA 13.11.2023 R. ZMIENIONEGO DECYZJĄ NR PRY.14/1024 Z DNIA 07.10.2024 R.
1. ZMIANA GRUBOŚCI ŚCIANY W OS. A.3.
 2. ZMIANA GRUBOŚCI ŚCIANY ŚCIANY ZMIANA POWIERZCHNI A.2.1, A.2.2, A.2.3, A.2.4, A.2.5, A.2.6, A.2.7, A.2.8, A.2.9, A.2.10, A.2.11, A.2.12,A.2.99, A.2.100, A.2.101, A.2.102,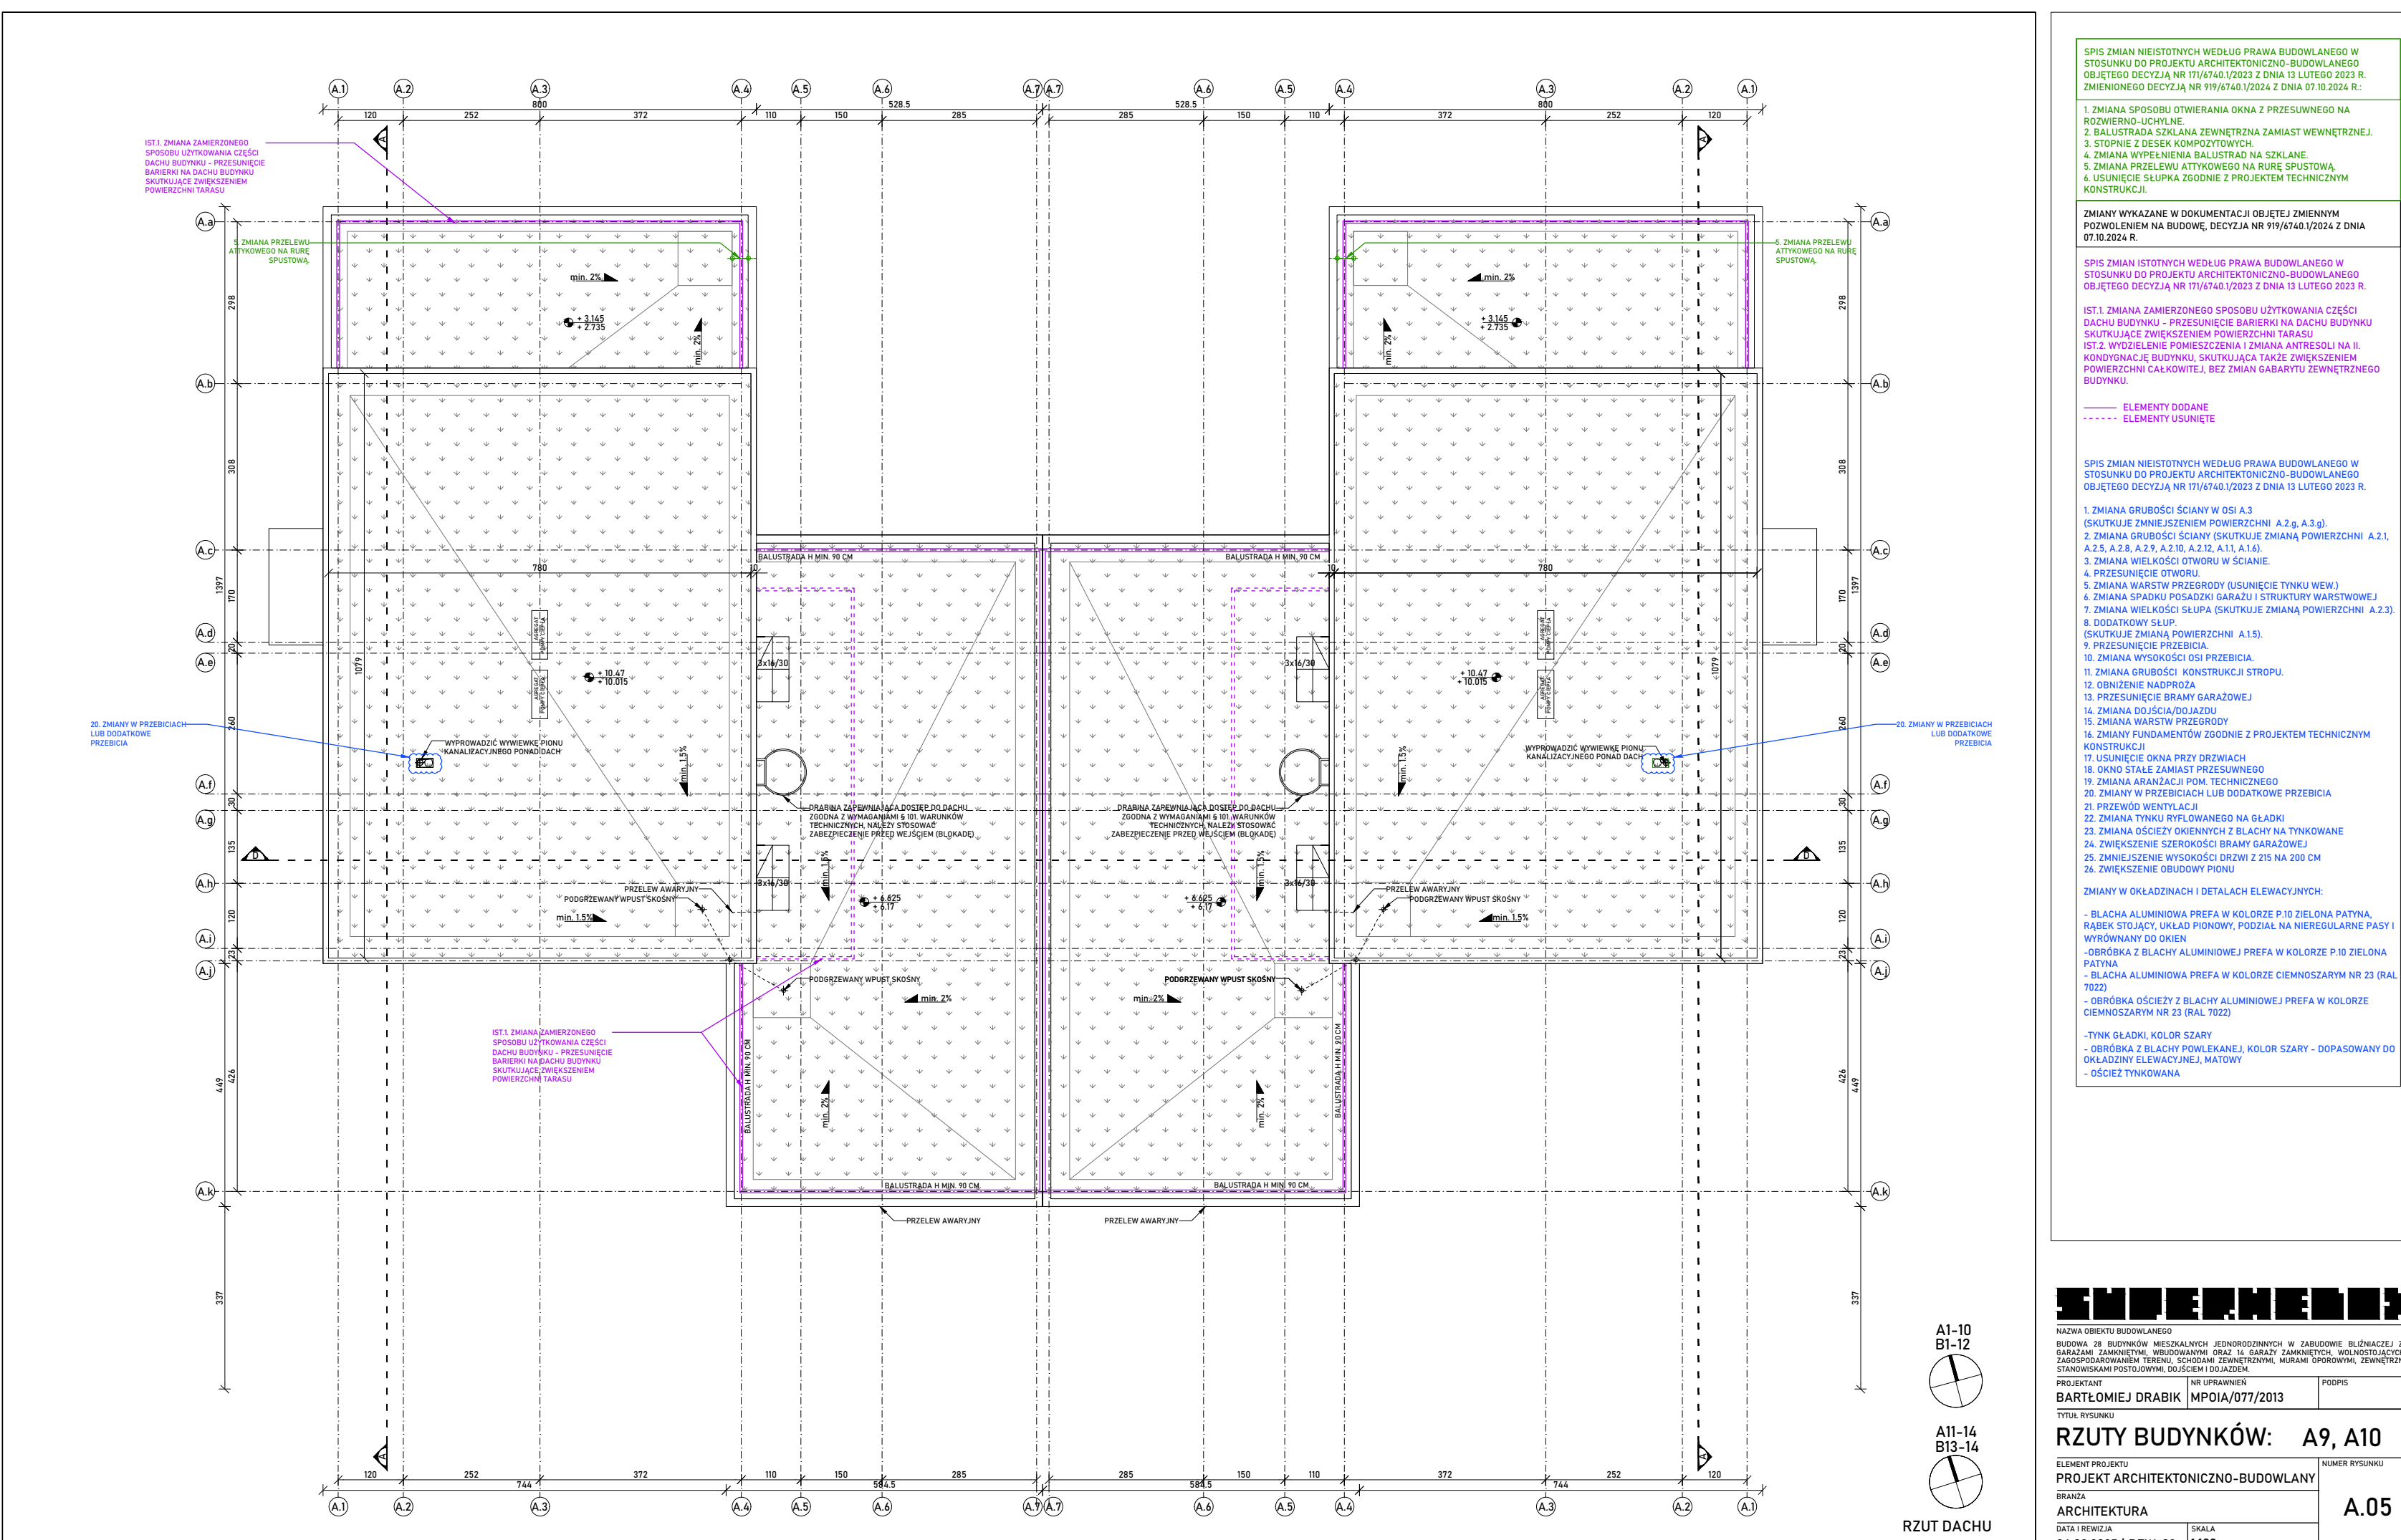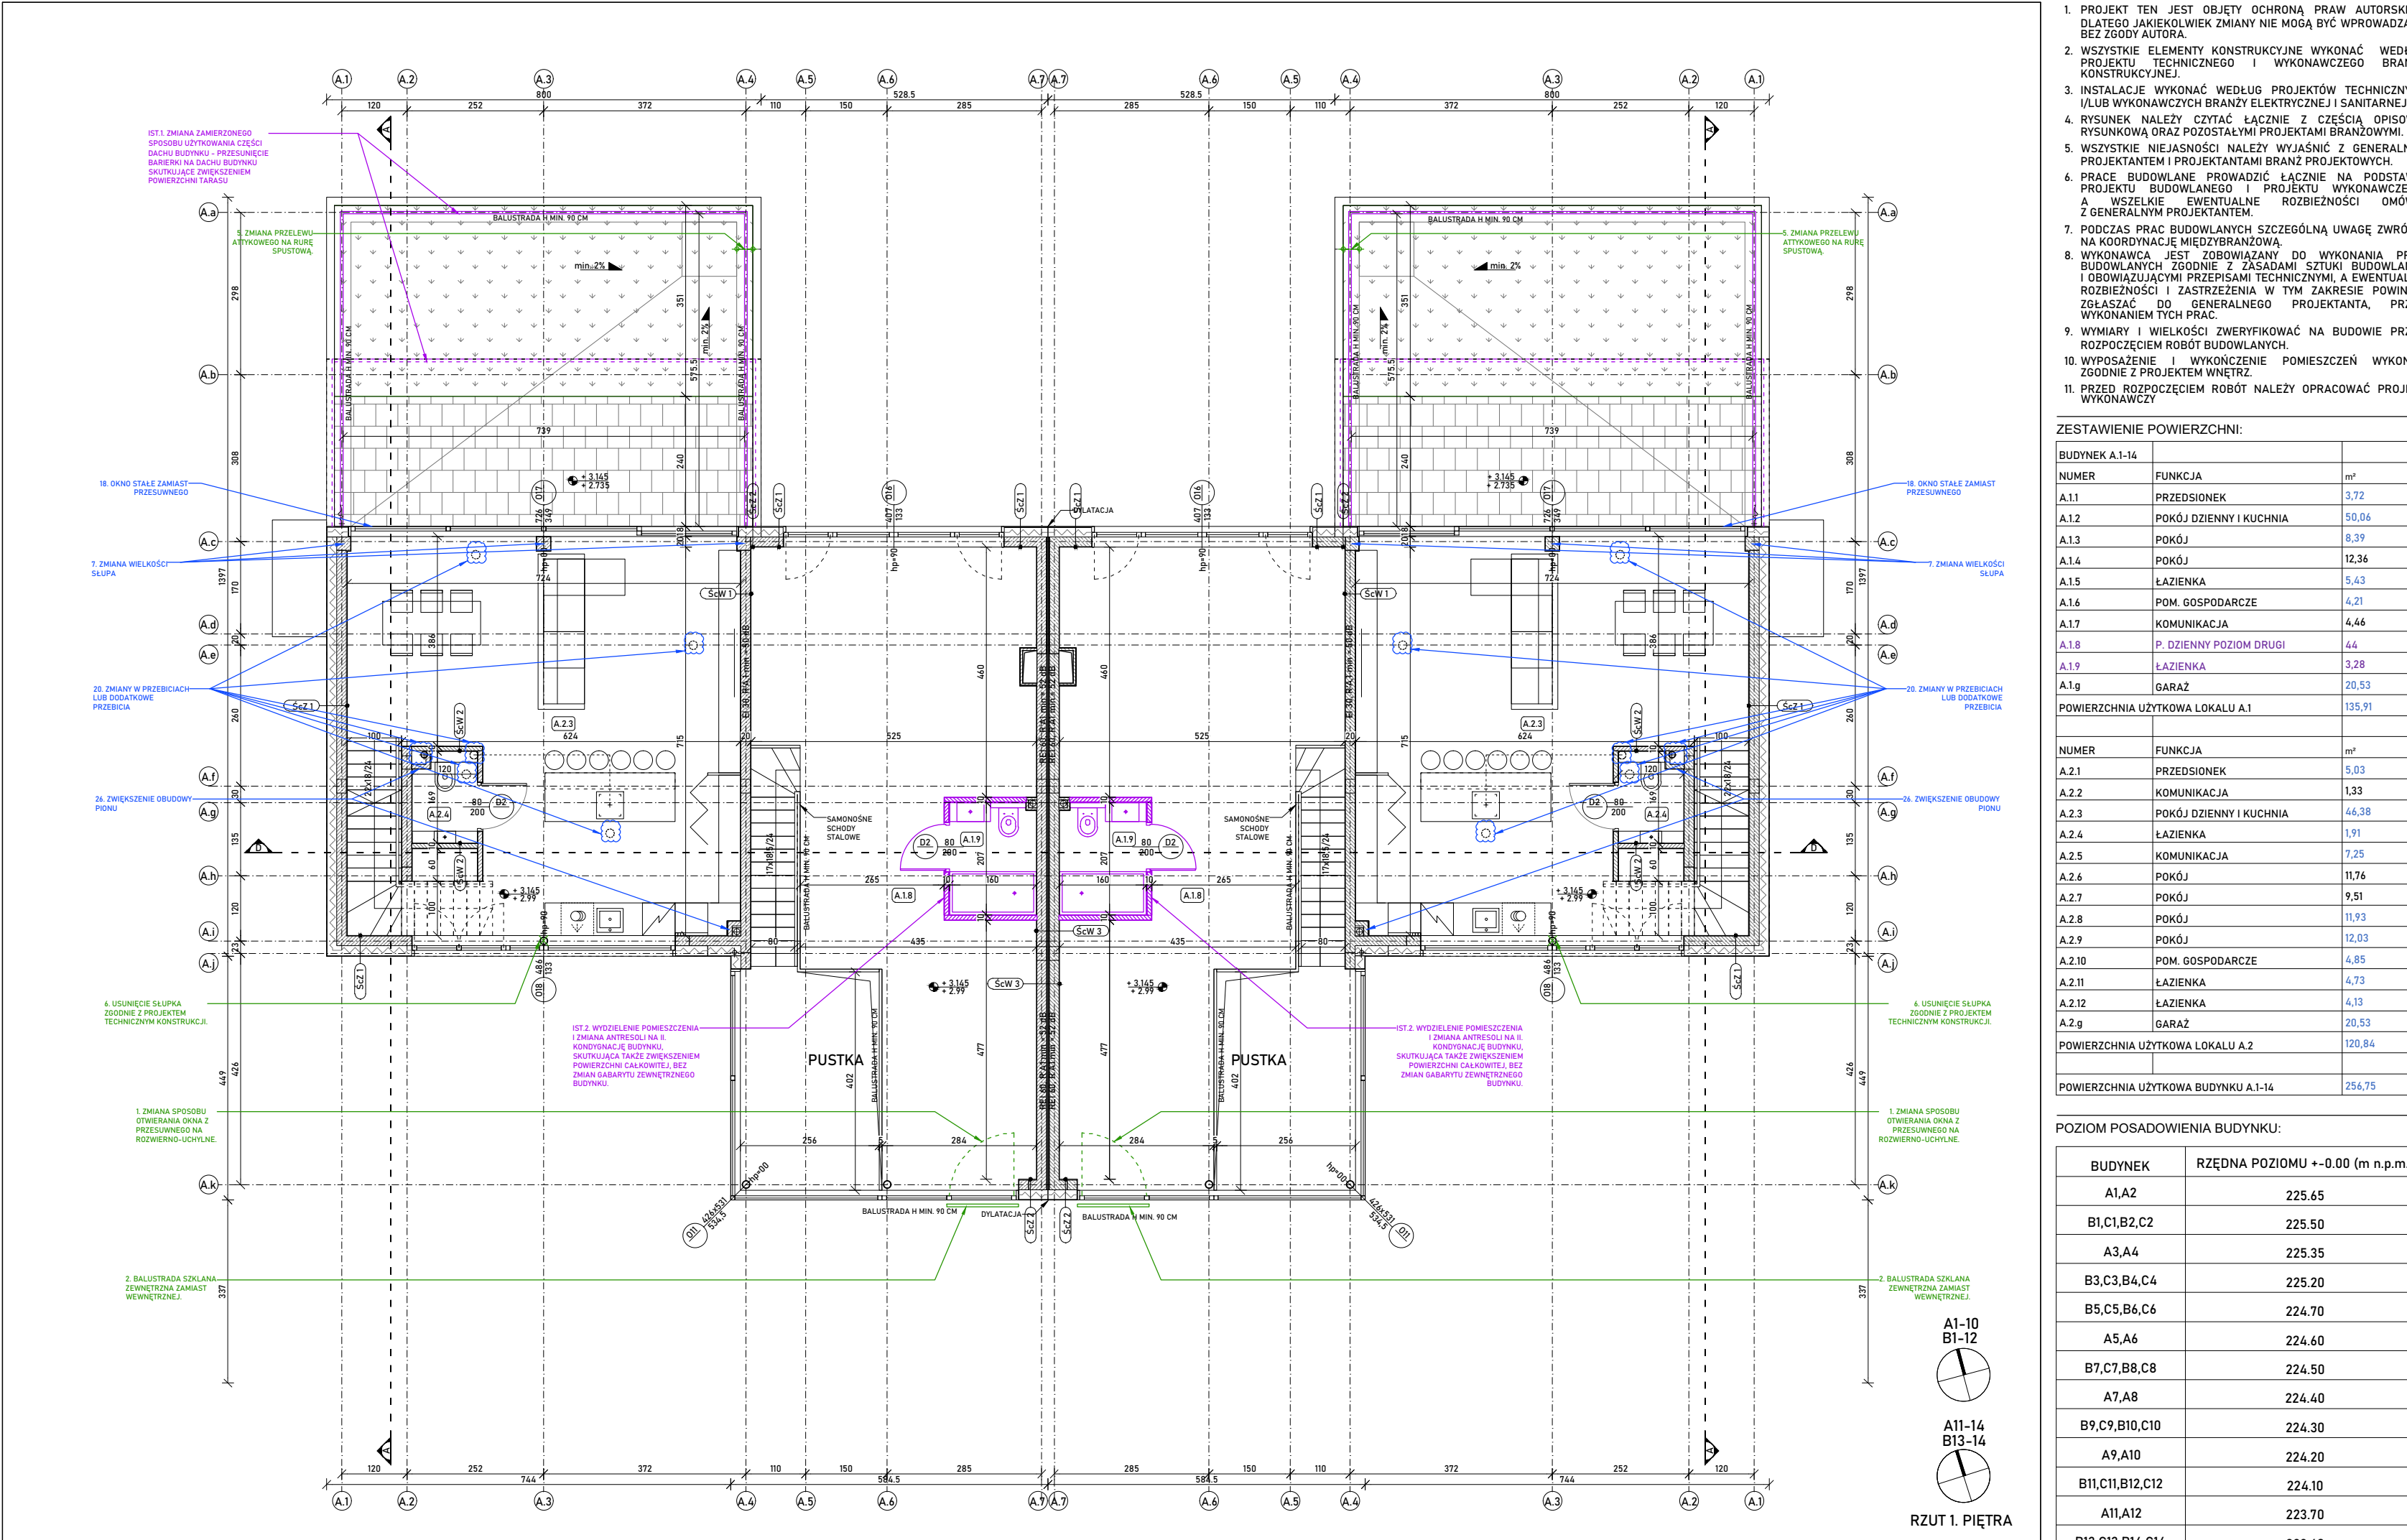[illegible]

ZESTAWIENIE POWIERZCHNI:		
BUDYNK A.1-14		
NUMER	FUNKCJA	m ²
A.1.1	PRZEDSIĘBIE	5,72
A.1.2	POKÓJ DZIENNY I KUCHNIA	90,06
A.1.3	POKÓJ	12,39
A.1.4	POKÓJ	5,33
A.1.5	ŁAZIENKA	6,21
A.1.6	POM. GOSPODARCZE	6,46
A.1.7	KOMUNIKACJA	4,4
A.1.8	P. DZIENNY PODŁÓŻY DRUGI	44
A.1.9	ŁAZIENKA	3,28
A.1.10	GARAŻ	20,53
A.1.11	GARAŻ	135,9
POWIERZCHNIA UŻYTKOWA LOKALU A.1		
NUMER	FUNKCJA	m ²
A.2.1	PRZEDSIĘBIE	5,03
A.2.2	KOMUNIKACJA	1,33
A.2.3	POKÓJ DZIENNY I KUCHNIA	46,18
A.2.4	ŁAZIENKA	1,1
A.2.5	KOMUNIKACJA	7,25
A.2.6	POKÓJ	11,76
A.2.7	POKÓJ	9,51
A.2.8	POKÓJ	11,73
A.2.9	POKÓJ	12,03
A.2.10	POM. GOSPODARCZE	4,85
A.2.11	ŁAZIENKA	4,75
A.2.12	ŁAZIENKA	4,33
A.2.13	GARAŻ	20,53
A.2.14	GARAŻ	135,9
POWIERZCHNIA UŻYTKOWA BUDYNKU A.1-14		
		256,19

POZIOM POSADOWIENIA BUDYNKU:	
BUDYNEK	RZĘDNA POZIOMU +0.00 (m n.p.m.)
A1,A2	225.65
B1,C1,B2,C2	225.50
A3,A4	225.35
B3,C3,B4,C4	225.20
B5,C5,B6,C6	224.70
A5,A6	224.60
B7,C7,B8,C8	224.50
A7,A8	224.40
B9,C9,B10,C10	224.30
A9,A10	224.20
B11,C11,B12,C12	224.10
A11,A12	223.70
B13,C13,B14,C14	223.60
A13,A14	223.50

SPIS ZMIAN NIEISTOTNYCH WEDŁUG PRAWA BUDOWLANEGO W STOSUNKU DO PROJEKTU ARCHITEKTONICZNO-BUDOWLANEGO OBJĘTEGO DECYZJĄ NR 171/6740.1/2023 Z DNIA 13 LUTEGO 2023 R. ZMIENIONEGO DECYZJĄ NR 919/6740.1/2024 Z DNIA 07.10.2024 R.:

1. ZMIANA SPOSOBU OTWIERANIA OKNA Z PRZESUWNEGO NA ROZWIERNO-UCHYLNIE.
2. BALUSTRADA SZKLANA ZEWNĘTRZNA ZAMIAST WEWNĘTRZNEJ.
3. STOPNIE Z DESEK KOMPOZYTYWYCH.
4. ZMIANA WYPEŁNIENIA BALUSTRAD NA SZKLANE.
5. ZMIANA PRZELEWU ATTYKOWEGO NA RURĘ SPUSTOWĄ.
6. USUNIĘCIE SŁUPKA ZGODNIE Z PROJEKTEM TECHNICZNYM KONSTRUKCJI.

ZMIANY WYKAZANE W DOKUMENTACJI OBJĘTEJ ZMIENNĄ
POZWOLENIEM NA BUDOWĘ, DECYZJA NR 999/6740.1/2024 Z DNIA
07.10.2024 R.

SPIS ZMIAN ISTOTNYCH WIEDZ PRAWA BUDOWLANEGO W
POSTANOWIENIACH PROJEKTU ARCHYTEKTONICZNO-BUDOWLANEGO
OBJĘTEGO DECYZJĄ NR 171/6740/V/2023 Z DNIA 13 LUTEGO 2023 R.

— ELEMENTY DODANE
..... ELEMENTY USUNIĘTE

SPIS ZMIAN NIEISTOTNYCH WEDŁUG PRAWA BUDOWLANEGO W

STOSUNKU DO PROJEKTU ARCHITEKTONICZNO-BUDOWLANEGO
OBJĘTEGO DECYZJĄ NR 171/6740.3/2023 Z DNIA 13 LUTEGO 2023 R.

2. ZMIANA GRUBOŚCI ŚCIANY (SKUTKUJE ZMIANĄ POWIERZCHNI A.2, A.2.5, A.2.8, A.2.9, A.2.10, A.2.12, A.1.1, A.1.6).

3. ZMIANA WIELKOŚCI OTWORU W ŚCIANIE.
4. PRZESUNIĘCIE OTWORU.
5. ZMIANA WARSZT PRZEGRODY (USUNIĘCIE TYNKU WEW.)

8. DODATKOWY SŁUP.
(SKUTKUJE ZMIANĄ POWIERZCHNI, A.1.5)

10. ZMIANA WYSOKOŚCI OSI PRZEBIECIA.
11. ZMIANA GRUBOŚCI KONSTRUKCJI STROPU.

12. OBNIZENIE NADPROŻA
13. PRZESUNIĘCIE BRAMY GARAŻOWEJ
14. ZMIANA DOJŚCIA/DOJAZDU
15. ZAKAZAŁA WYKONANIE PRAC

17. USUNIĘCIE OKNA PRZY DRZWIACH

18. OKNO STAŁE ZAMIĄST PRZESUWNEGO
19. ZMIANA ARANŻACJI POM. TECHNICZNEGO
20. ZMIANY W PRZEBIĘCIACH LUB DODATKOWE PRZEBIECIA
21. PRZEBIECIA LUB WYMIARY, J.C.

23. ZMIANA OŚCIEŻY OKIENNYCH Z BLACHY NA TYNKOWANIE

26. ZWIĘKSZENIE OBUŁOWY PIONU

- BLACHA ALUMINIOWA PREFABRYKOWANA W KOLORZE P.10 ZIELONA PATYNA, RALIEK STĄJĄCY, UKŁAD PIONOWY, PODZIAŁ NA NIEREGULARNE PASY I

WYRÓWNY DO OKIEN
-OBRÓBKA Z BLACHY ALUMINIOWEJ PREFAB W KOLORZE P.10 ZIELONA
PATYNA

- BLACHA ALUMINIOWA PREFA W KOLORZE CIEMNOSZARYM NR 23 (RAL 7022)
- OBRÓBKA DŚCIEŻY Z BLACHY ALUMINIOWEJ PREFA W KOLORZE CIEMNOSZARYM NR 23 (RAL 7022)

- TYNK GŁADKI, KOLOR SZARY
- OBRÓBKA Z BLACHY POWLEKANEJ, KOLOR SZARY - DOPASOWANY DO

OKŁADZINY ELEWACYJNEJ, MATOWY
- OŚCIEŻ TYNKOWANA

REFERENCES

NAZWA OBIEKTU BUDOWLANEGO
BUDOWA 28 BUDYNKÓW MIESZKALNYCH JEDNORODZINNYCH W ZABUDOWIE BLIŹNACZEJ

GARAŻAMI ZAMKNIĘTYMI, WŁĘDZANYMI ORAZ 14 GARAŻY ZAMKNIĘTYCH, WOLNOSTOJĄCYCH ZAGOSZCZANIEM TERENU, SCHODAMI ZIEMNymi, MURAMI OPOROWYMI, ZEWNĘTRZNYMI STANOWISKAMI POSTOJOWYMI, ODJAZDEM I DOJAZDEM.		
PROJEKTANT	NR UPRAWNIEN	PODPIS





BARTŁOMIEJ DRABIK	MPOIA/077/2013	
Tytuł: RYSUNKI		
REZERWACJA	10	110

RZUTY BUDYNKÓW: A9, A10	
ELEMENT PROJEKTU	NUMER RYSUNKU

PROJEKT ARCHITEKTONICZNO-BUDOWLANY	A.05
BRANŻA	
ARCHITEKTURA	

DATA I WYKONANIE	SKALA
24.09.2025 REW. 09	1:100

ROZPOWIECZANIE NIEJESZEGO OPRACOWANIA ORAZ JEJ FRAGMENTÓW W JAKIEJKOLWIEK FORMIE ORAZ DOKONYWANIE ZMIAN BEZ ZGODY AUTORA JEST ZABRONIONE NA MOCY UST. O PRAWIE AUTORSKIM I PRAWACH POWIĘKNYCH.

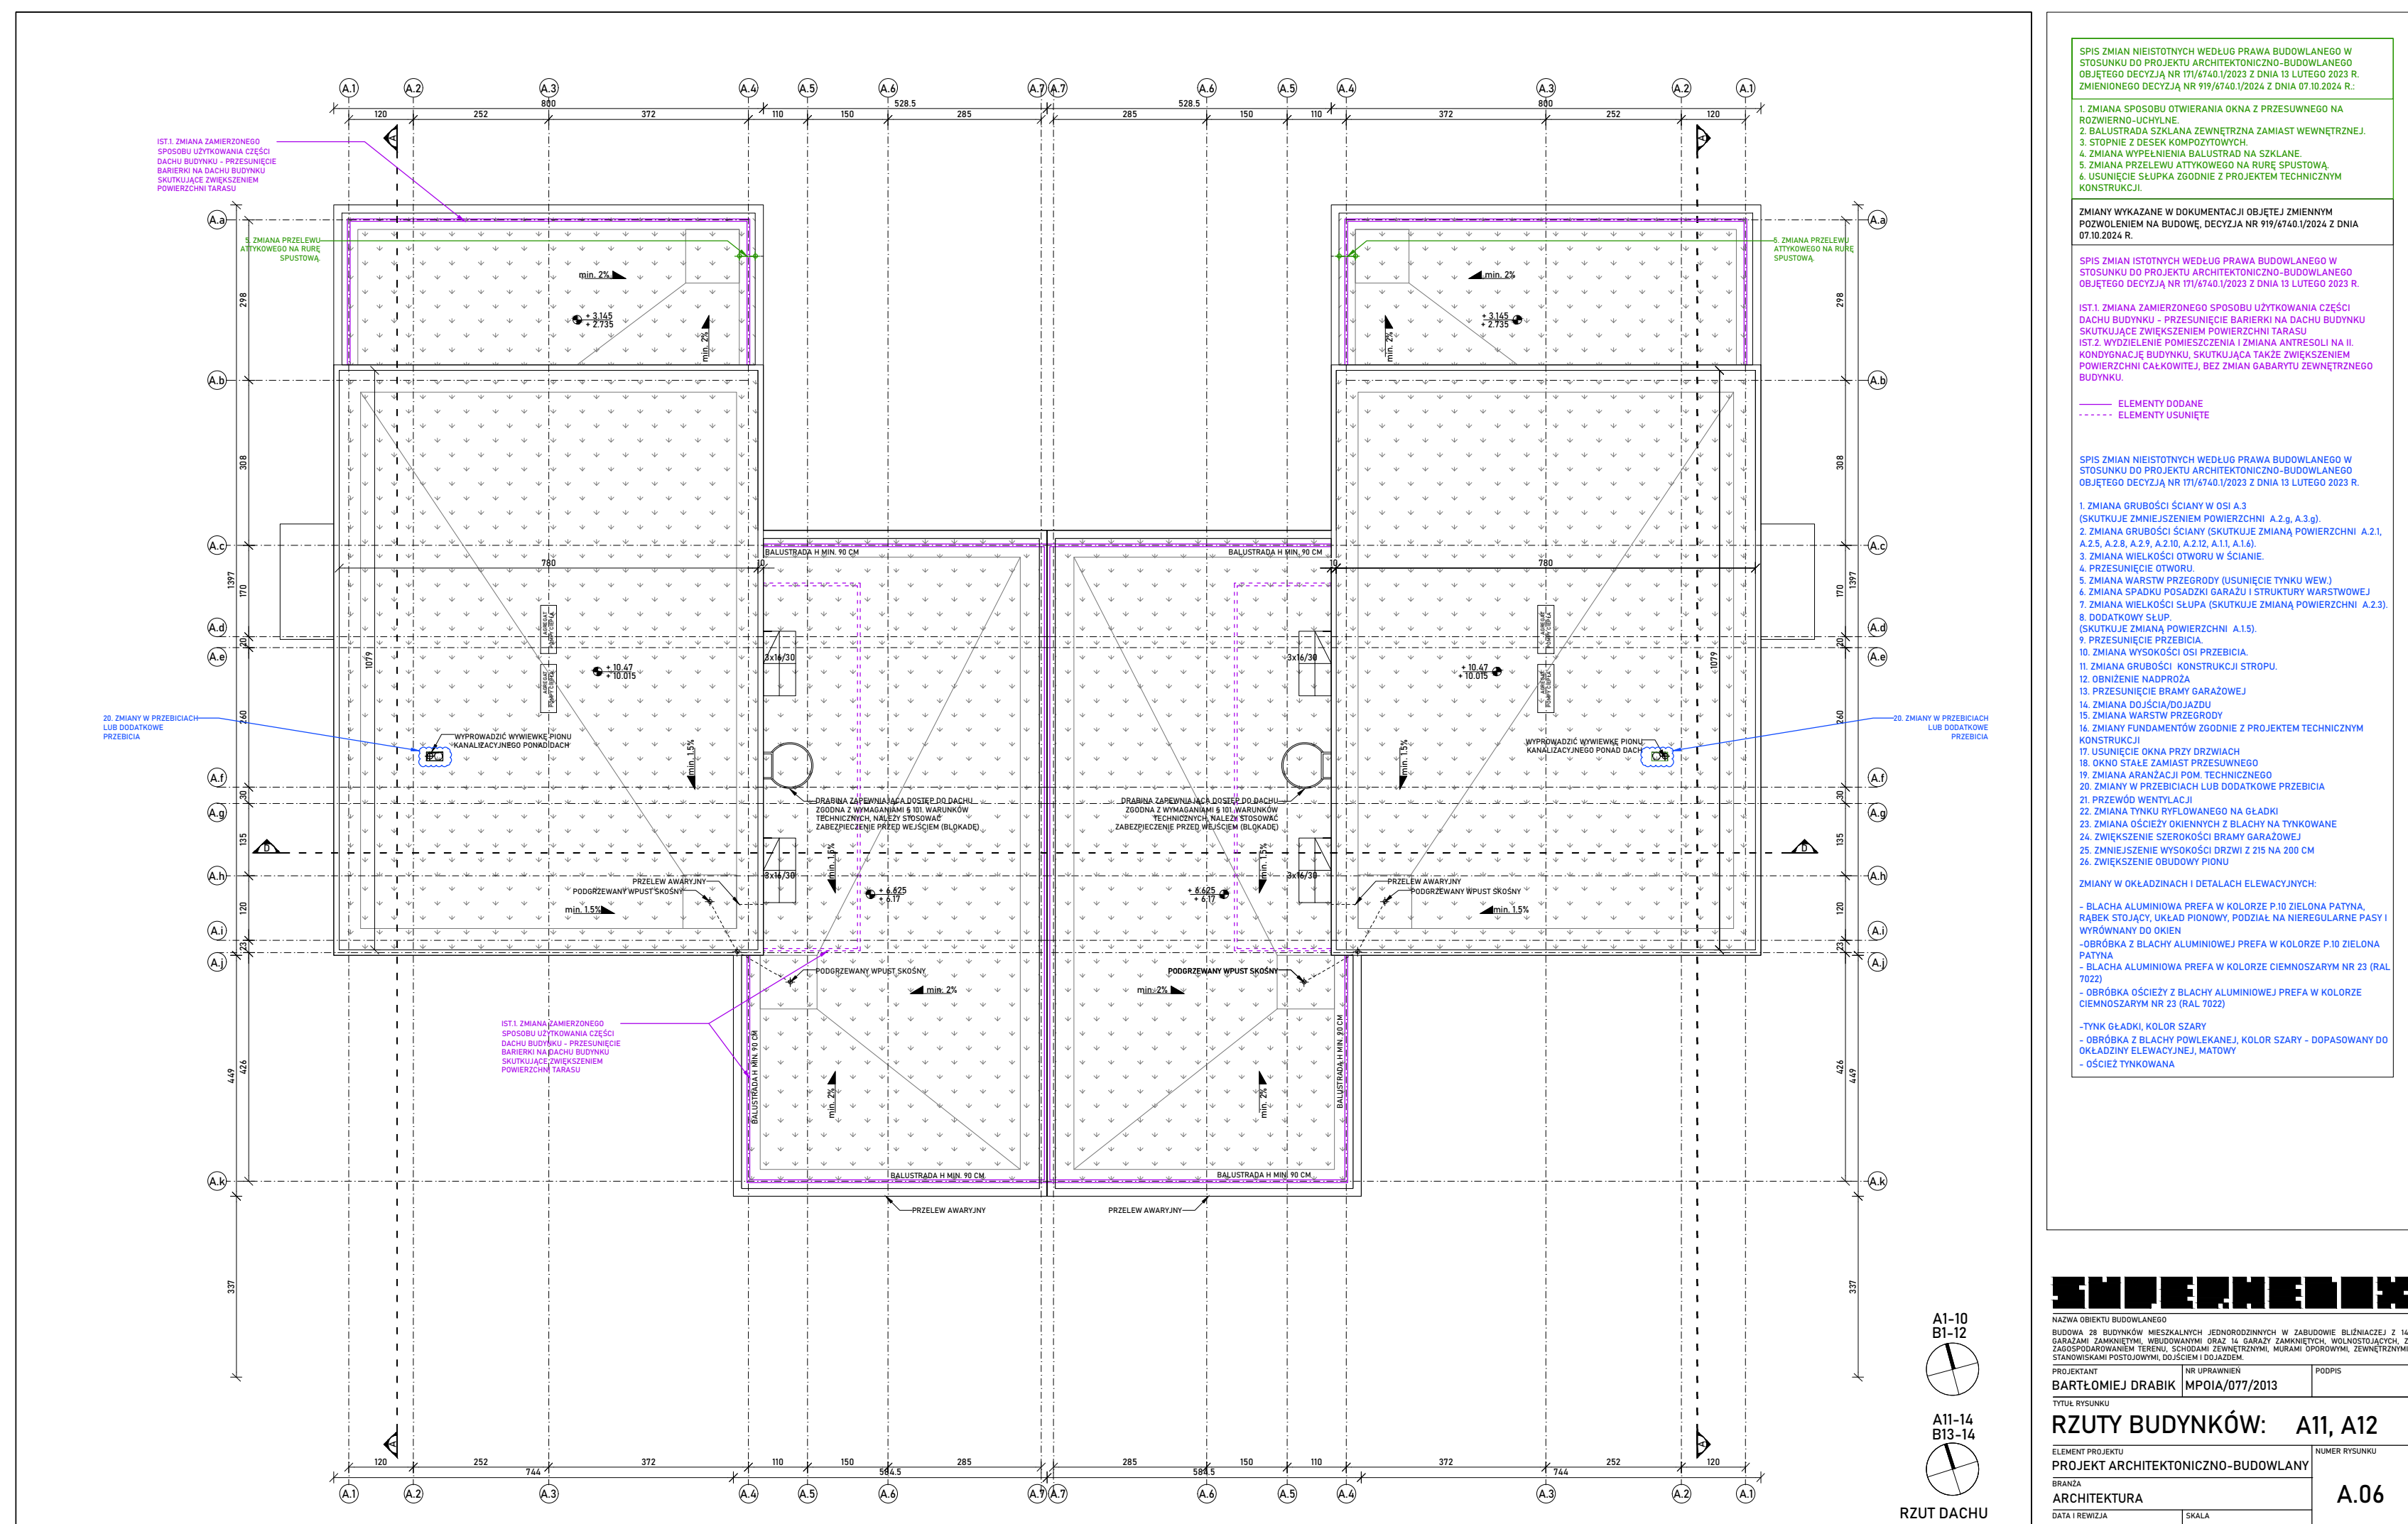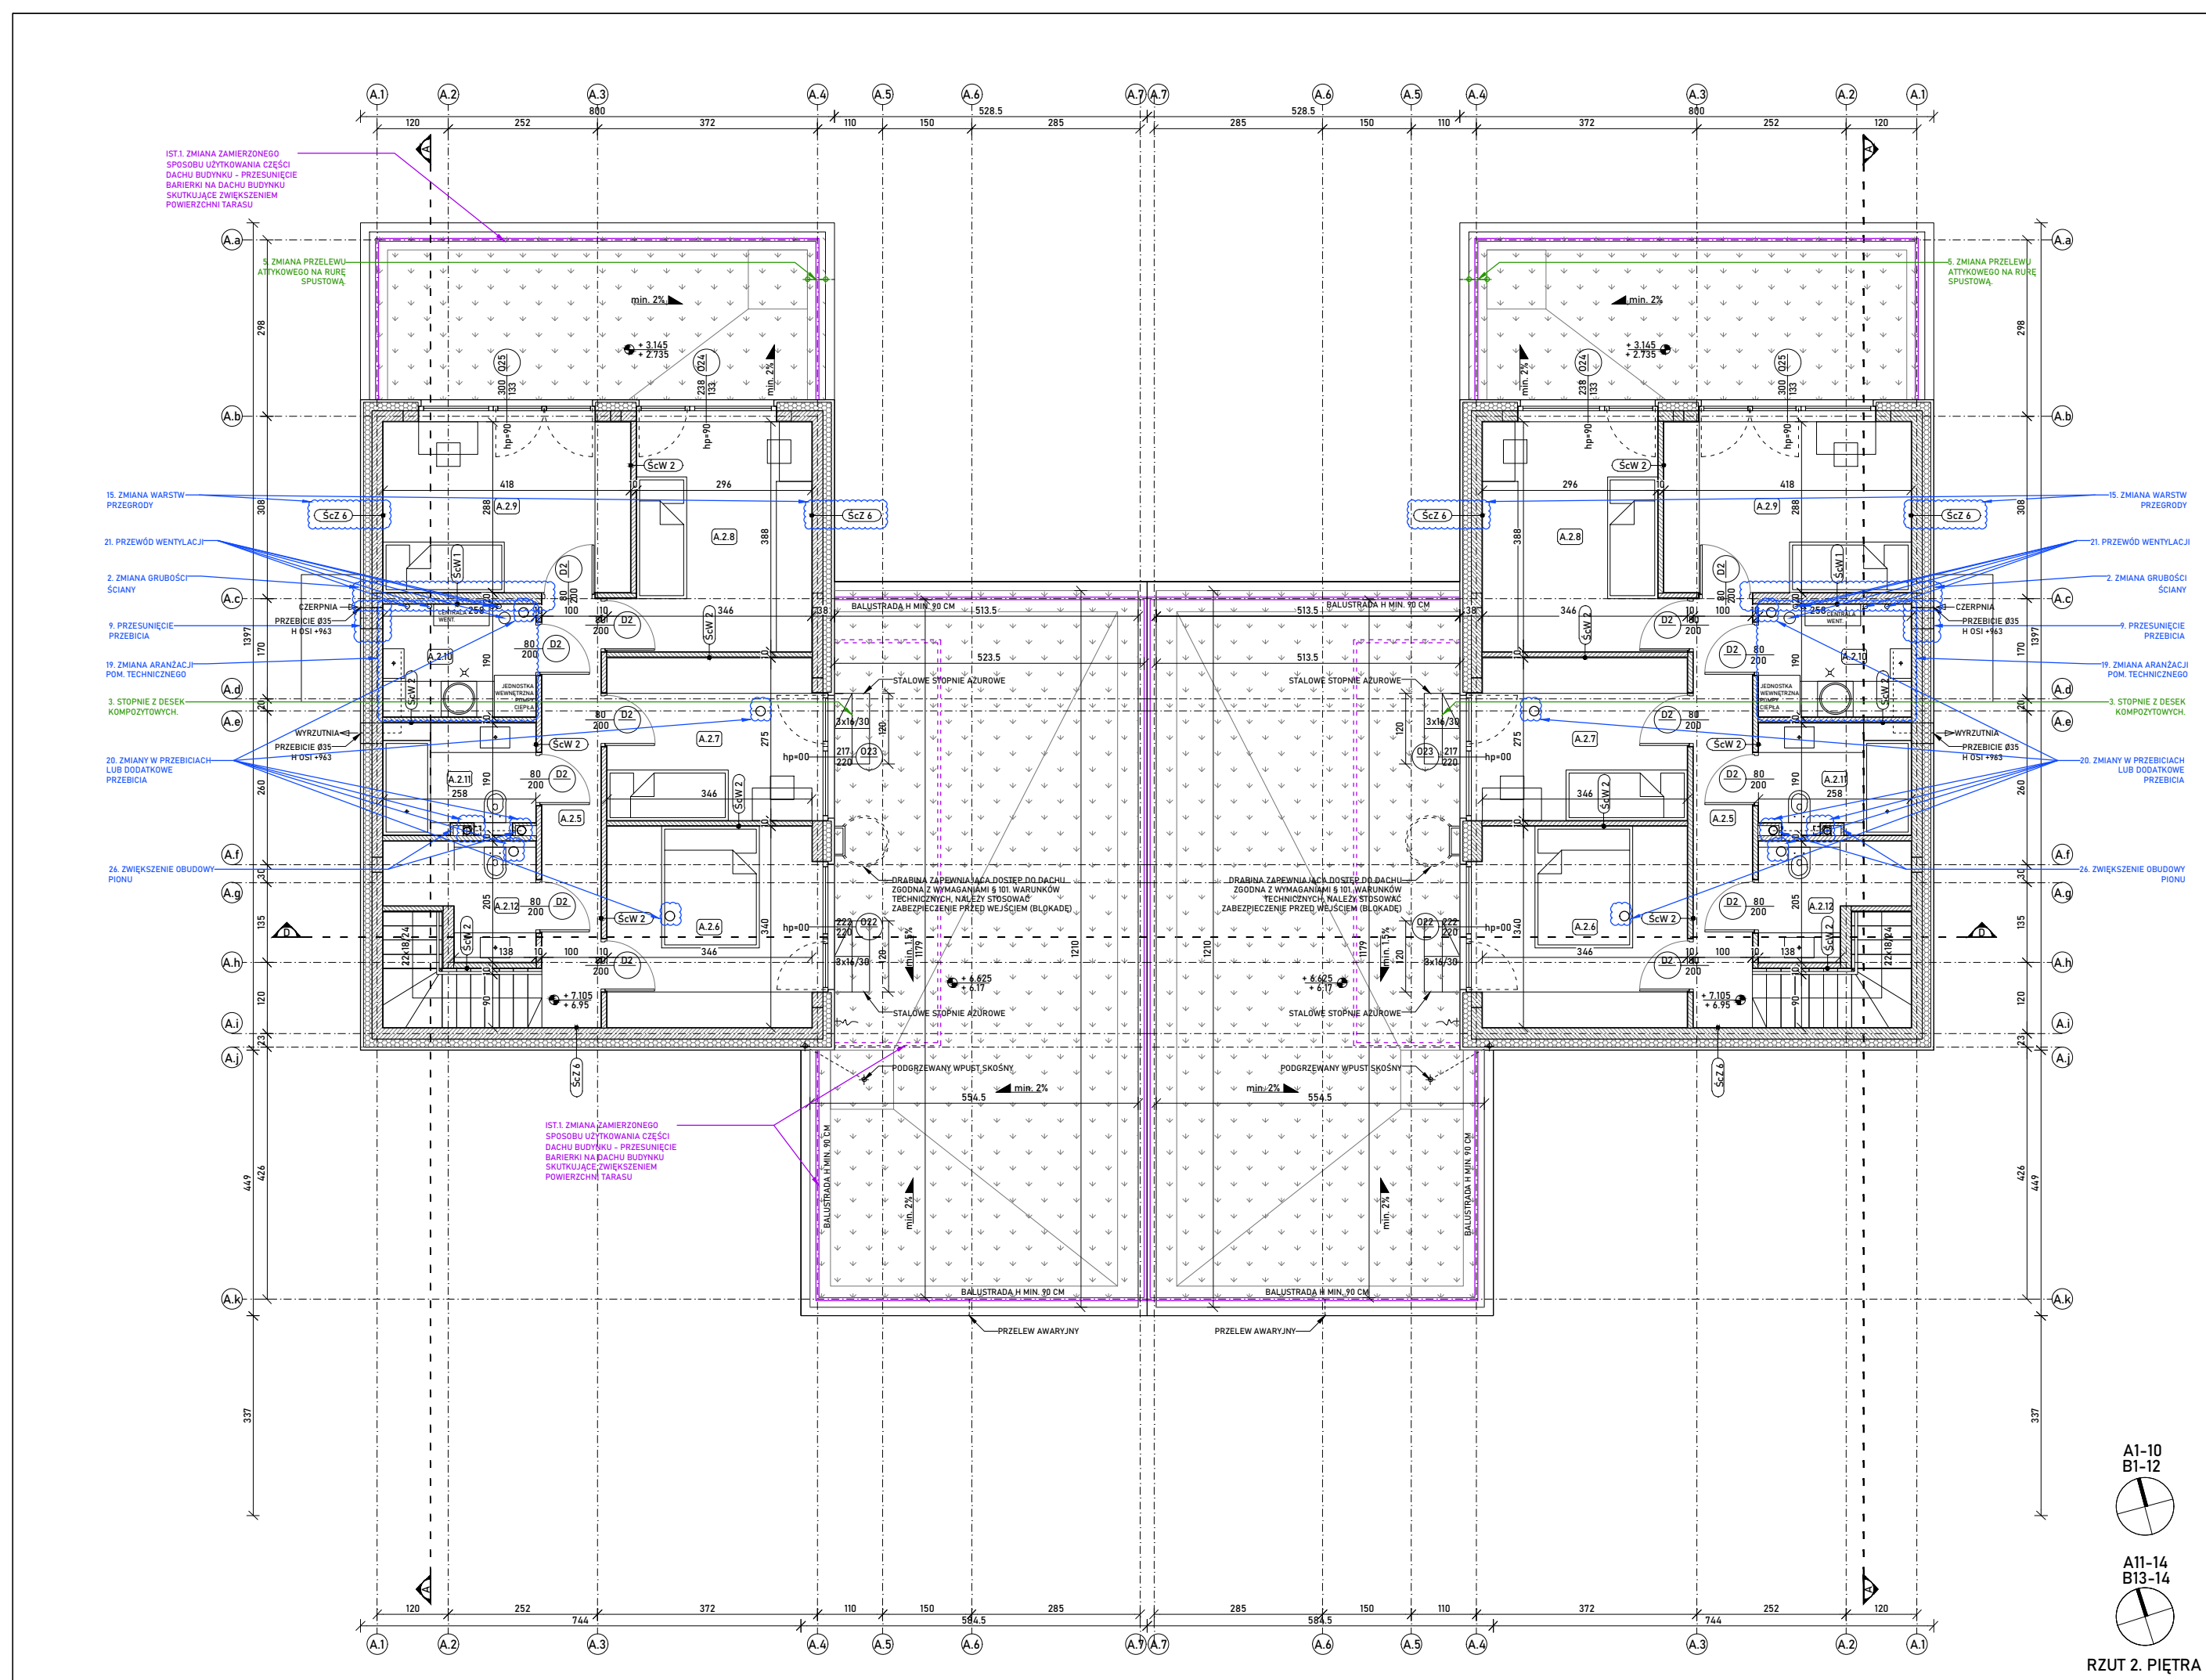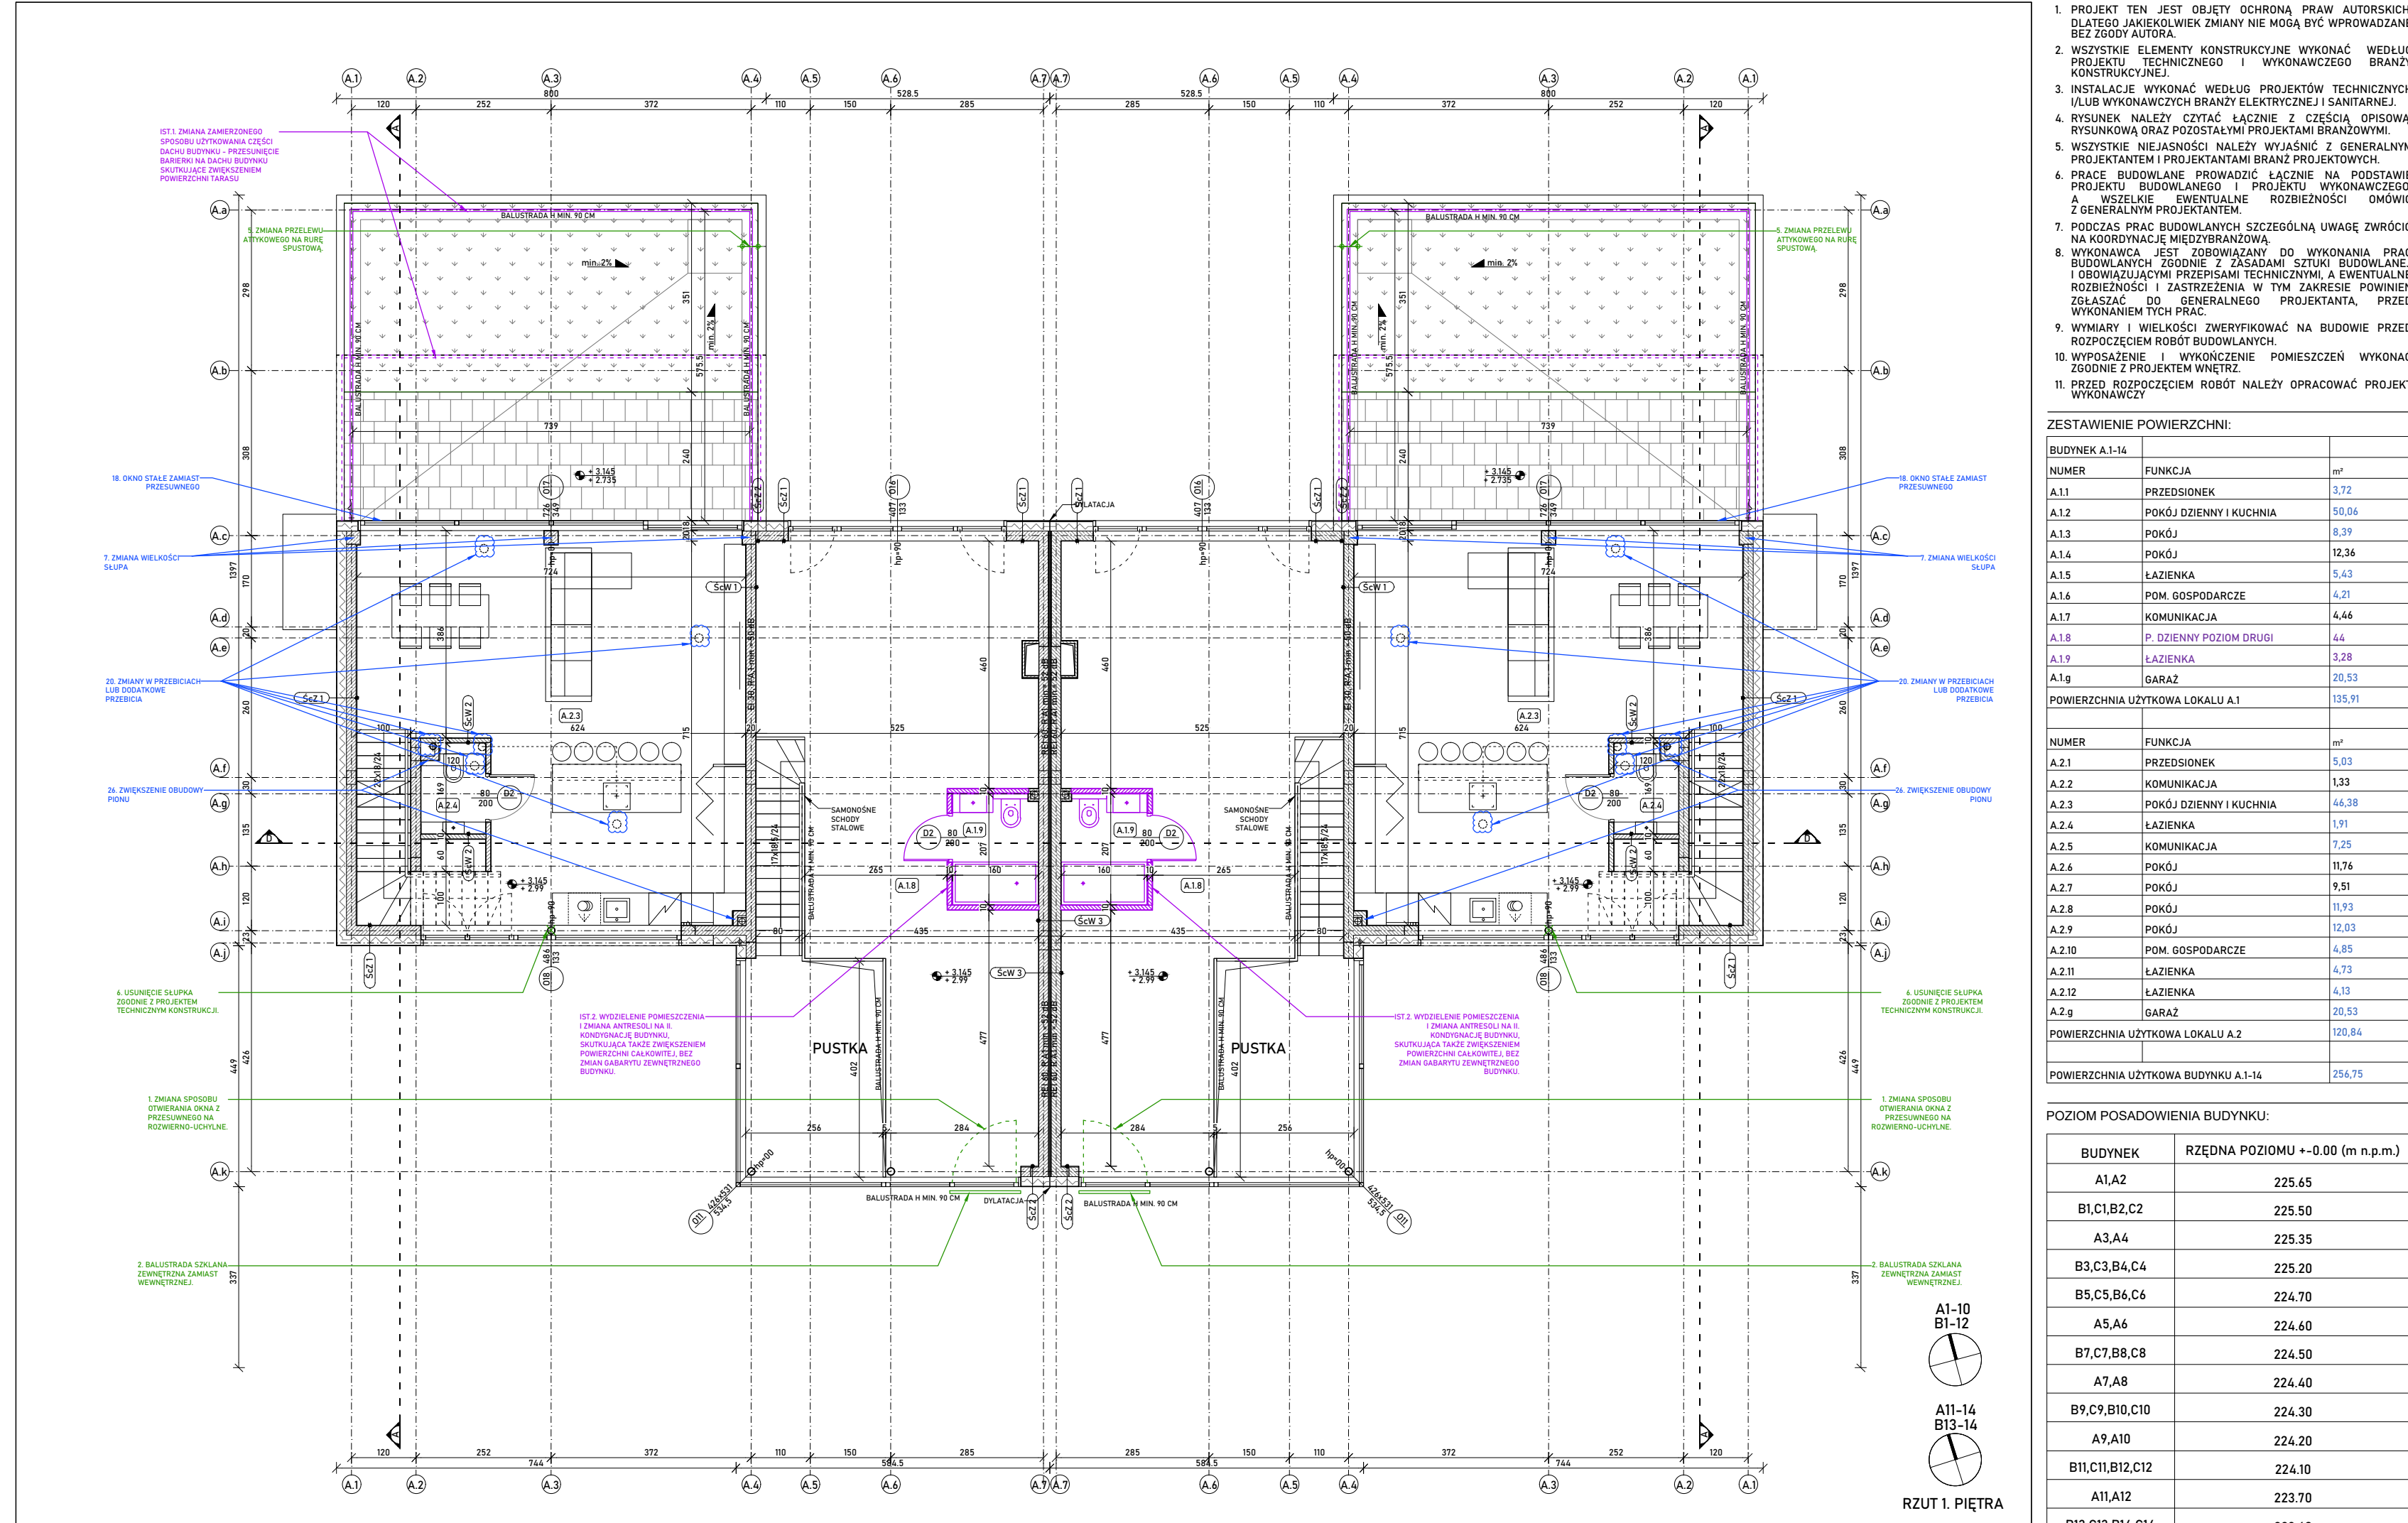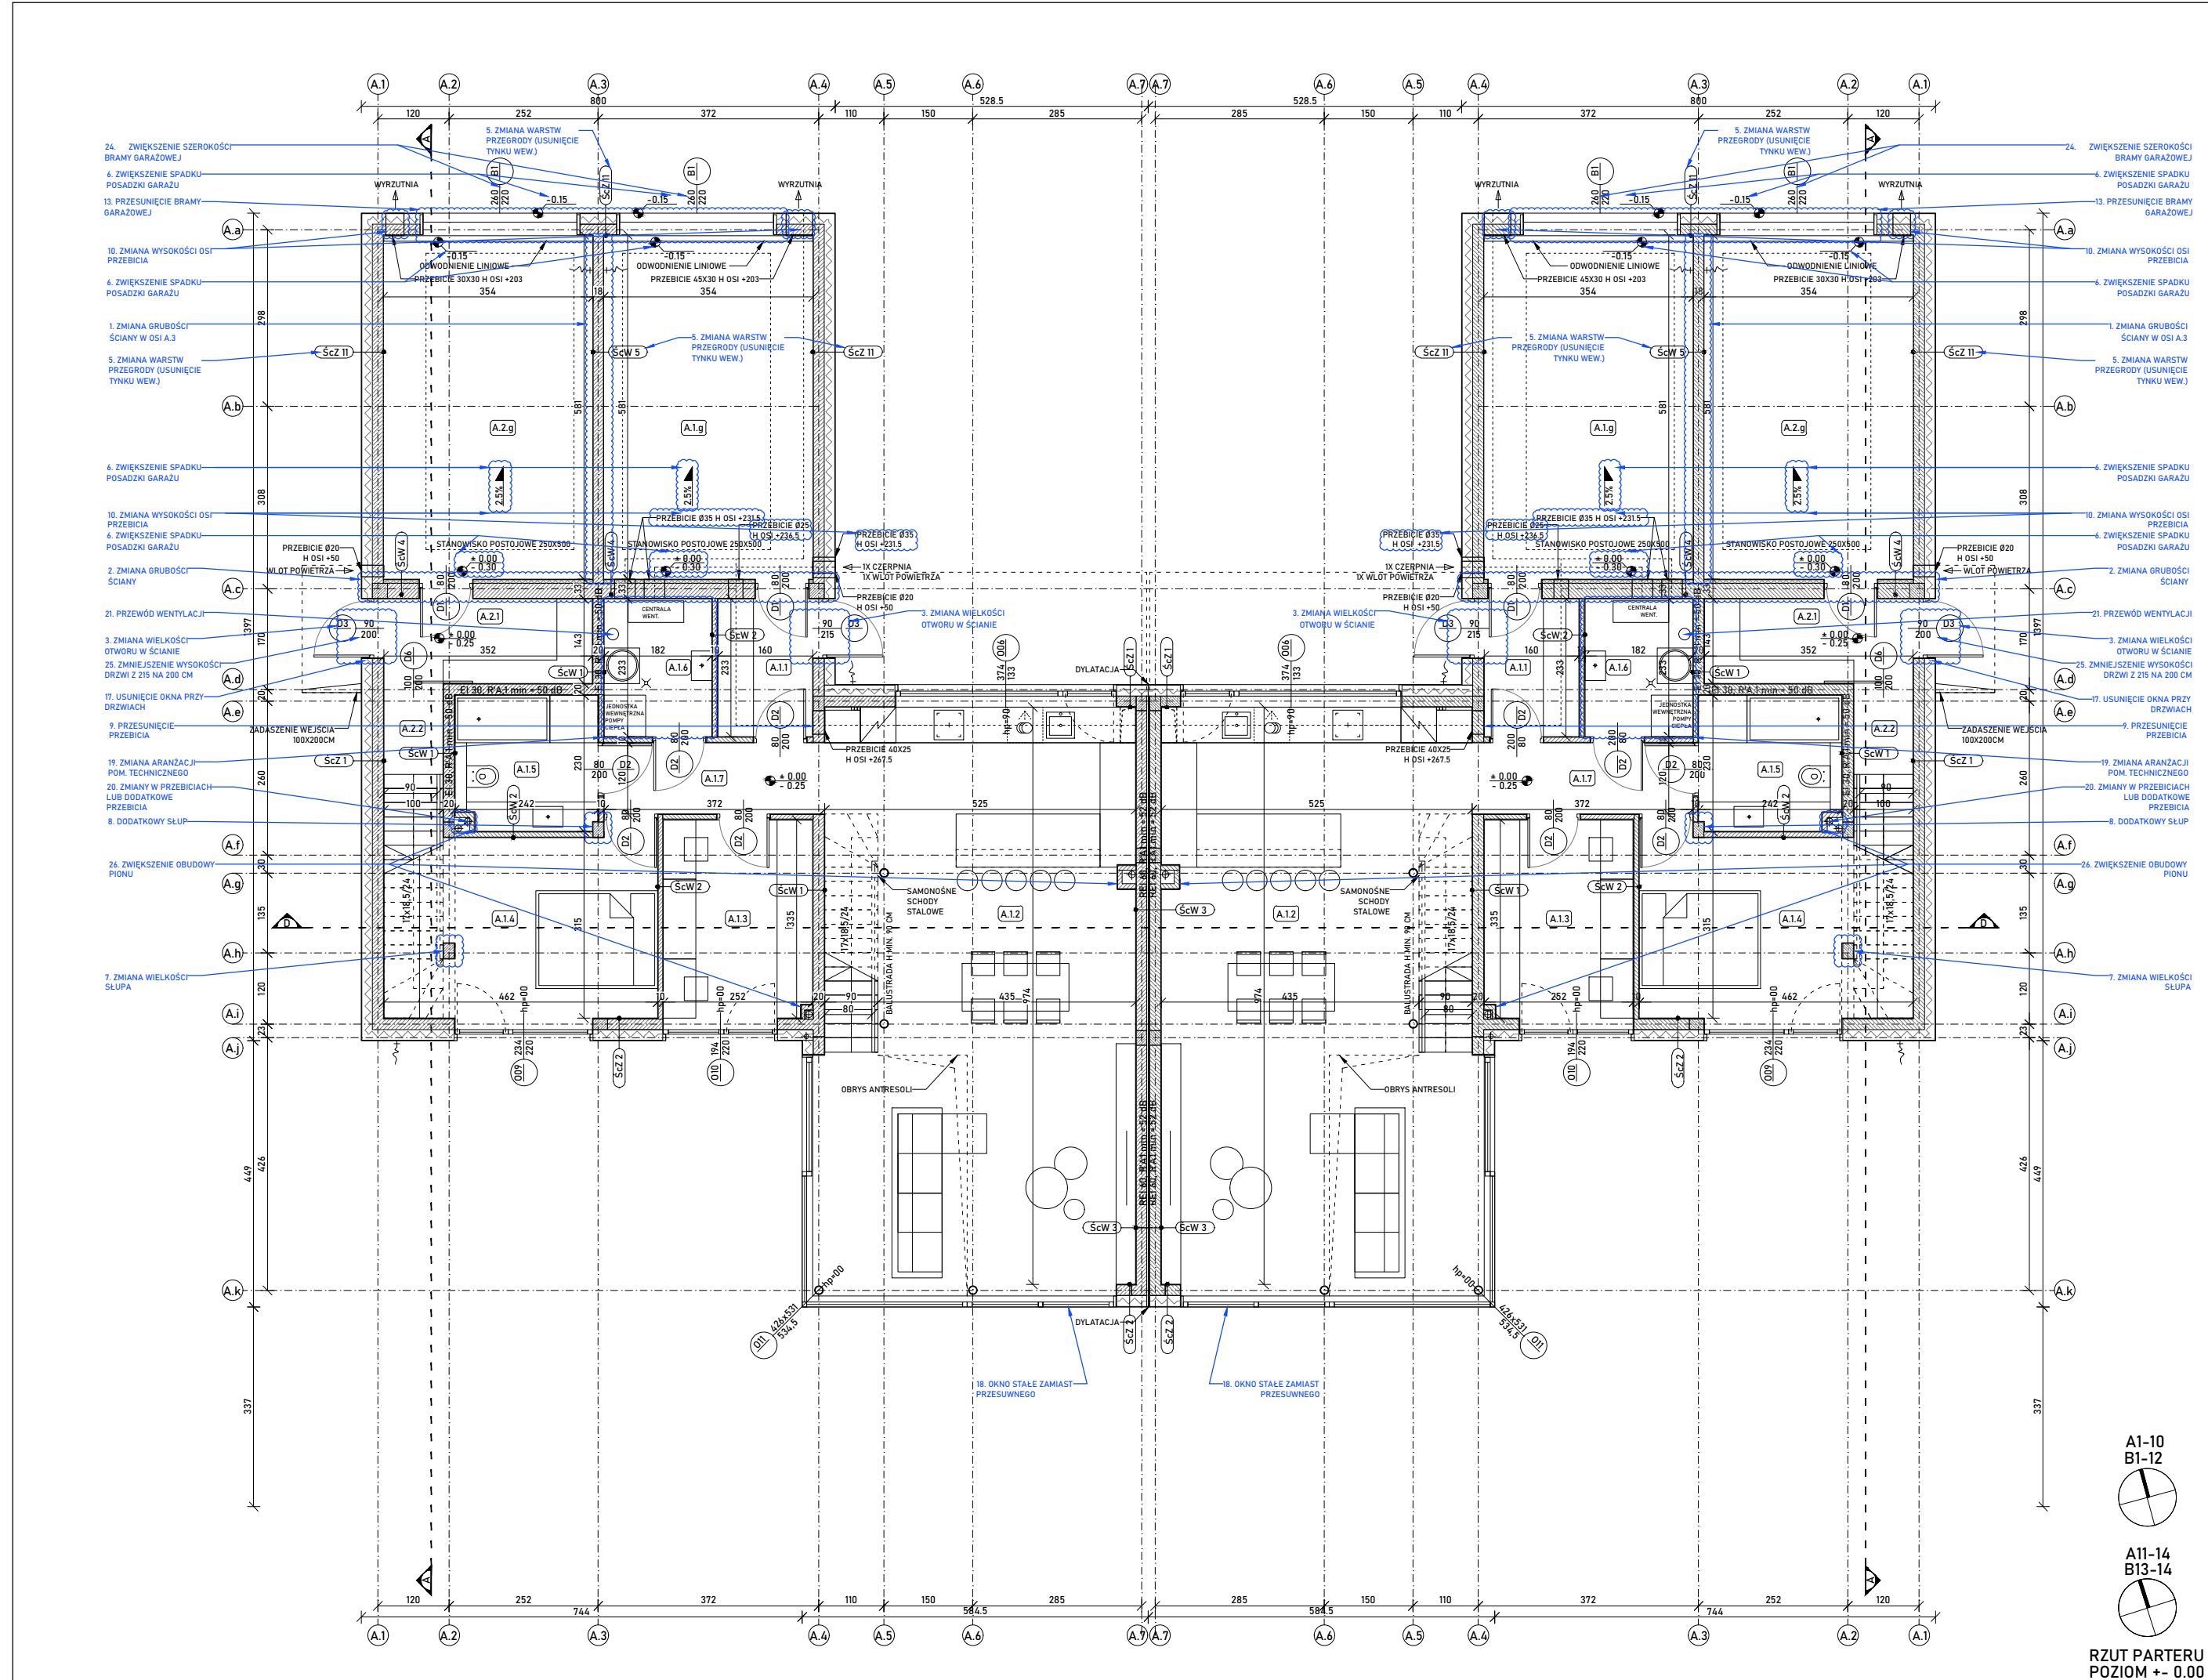[illegible]

ZESTAWIENIE POWIERZCHNI:		
BUDYNEK A.1-14		
NUMER	FUNKCJA	m ²
A.1.1	PRZEDSIĘBIO	3,72
A.1.2	POKÓJ, DZIENNY I KUCHNIA	99,06
A.1.3	POKÓJ	8,397
A.1.4	POM. GOSPOD.	12,26
A.1.5	ŁAZIENKA	5,43
A.1.6	POM. GOSPODARCZE	6,21
A.1.7	KOMUNIKACJA	4,46
A.1.8	P. DZIENNY POZIOM DRUGI	4,46
A.1.9	ŁAZIENKA	3,28
A.1.9	GARAŻ	20,53
POWIERZCHNIA UŻYTKOWA LOKAŁU A.1		195,91
BUDYNEK A.2-14		
NUMER	FUNKCJA	m ²
A.2.1	PRZEDSIĘBIO	5,03
A.2.2	KOMUNIKACJA	1,33
A.2.3	POKÓJ, DZIENNY I KUCHNIA	64,38
A.2.4	ŁAZIENKA	1,91
A.2.5	KOMUNIKACJA	7,25
A.2.6	POM. GOSPOD.	11,74
A.2.7	POKÓJ	9,51
A.2.8	POKÓJ	11,93
A.2.9	POKÓJ	12,03
A.2.10	POM. GOSPODARCZE	6,85
A.2.11	ŁAZIENKA	4,73
A.2.12	ŁAZIENKA	4,03
A.2.13	GARAŻ	20,53
POWIERZCHNIA UŻYTKOWA LOKAŁU A.2		190,84
POWIERZCHNIA UŻYTKOWA BUDYNKU A.1-14		256,75

POZIOM POSADOWIENIA BUDYNKU:	
BUDYNEK	RZĘDNA POZIOMU +0.00 (m n.p.m.)
A1,A2	225.65
B1,C1,B2,C2	225.50
A3,A4	225.35
B3,C3,B4,C4	225.20
B5,C5,B6,C6	224.70
A5,A6	224.60
B7,C7,B8,C8	224.50
A7,A8	224.40
B9,C9,B10,C10	224.30
A9,A10	224.20
B11,C11,B12,C12	224.10
A11,A12	223.70
B13,C13,B14,C14	223.60
A13,A14	223.50

SPIS ZMIAN NIEISTOTNYCH WEDŁUG PRAWA BUDOWLANEGO W STOSUNKU DO PROJEKTU ARCHITEKTONICZNO-BUDOWLANEGO OBJĘTEGO DECYZJĄ NR 171/6740.1/2023 Z DNIA 13 LUTEGO 2023 R. ZMIENIONEGO DECYZJĄ NR 919/6740.1/2024 Z DNIA 07.10.2024 R.:

1. ZMIANA SPŁOSOBU OTWIERANIA OKNA Z PRZESUWNEGO NA RĘCZNO-UCIYNE.
2. BALUSTRA SZKLANA ZEWNĘTRZNA ZAMIAST WEWNĘTRZNEJ.
3. STOPNIE Z DŁEKKOMPOZYTYWNYCH.
4. ZMIANA WYPEŁNIENIA BALUSTRAD NA SZKLANE.
5. ZMIANA PRZEŁĘWU ATTYKOWEGO NA RURĘ SPŁUSTOWĄ.
6. USUNIĘCIE SŁUPKA ZGODNIE Z PROJEKTEM TECHNICZNYM KONSTRUKCJI.

ZMIANY WYKAZANE W DOKUMENTACJI OBJĘTEJ ZMIENNĄ
POZWOLENIEM NA BUDOWĘ, DECYZJA NR 999/6740.1/2024 Z DNIA
07.10.2024 R.

SPIS ZMIAN ISTOTNYCH WEDŁUG PRAWA BUDOWLANEGO W STOSUNKU DO PROJEKTU ARCHITEKTONICZNO-BUDOWLANEGO OBJĘTEGO DECYZJĄ NR 171/8740.3/2023 Z DNIA 13 LUTEGO 2023 R.

IST.1. ZMIANA ZAMIERZONEGO SPOSOBU UŻYTKOWANIA CZĘŚCI DACHU BUDYNKU - PRZESUNIĘCIE BARIERKI NA DACHU BUDYNKU SKUTKUJĄCE ZWIĘKSZENIEM POWIERZCHNI TARASU

———— ELEMENTY DOŁANE
----- ELEMENTY USUNIĘTE

SPIS ZMIAN NIEISTOTNYCH WEDŁUG PRAWA BUDOWLANEGO W
STOSUNKU DO PROJEKTU ARCHITEKTONICZNO-BUDOWLANEGO
OBJĘTEGO DECYZJĄ NR 171/6740/2023 Z DNIA 13 LUTEGO 2023 R.

1. ZMIANA GRUBOŚCI ŚCIĄNY W OSI A,3
(SKUTKUJE ZMNIJSZENIEM SIŁOWNOŚCI A,2 g. A,3 g).

2. ZMIANA GRUBOŚCI ŚCIĄNY (SKUTKUJE ZMIANĄ POWIERZCHNI A,2,1,

- 4.25; A.2.9; A.9; A.2.12; R.2.2; A.1; (A.1.8).
5. ZMIANA WIELKOŚCI WYMIARÓW W ŚCIĄGaniu.
6. PRZESUNIĘCIE OTWORU.
7. ZMIANA WARTOŚCI PRZEGRODY (JUSNIĘCIE TYNKU WŁĘ).
8. ZMIANA SPADKU POSADZKI GARAŻU I STRUKTURY WARTOŚCI.
9. ZMIANA WIELKOŚCI SŁUPA (SKUTKOWE ZMIANĄ POWIERZCHNI A.2.3).
10. DODATKOWY SŁUP.
11. SKUTKOWE ZMIANĄ POWIERZCHNI A.1.5).

10. ZMIANA WYSOKOŚCI OSI PRZEBIECIA.
11. ZMIANA GRUBOŚCI KONSTRUKCJI STROPU.
12. OBNIŻENIE NADPROŻA
13. PRZESUNIĘCIE BRAMY GARAŻOWEJ
14. ZMIANA DOJŚCIA/DOJAZDU
15. ZMIANA WARSTW PRZEGRODY
16. ZMIANY FUNDAMENTÓW ZGODNIE Z PROJEKTEM TECHNICZNYM

17. USUNIECIE OKNA PRZY DRZWIACH
18. OKNO STAŁE ZAMIAST PRZESUWNEGO
19. ZMIANA ARANŻACJI POM. TECHNICZNEGO
20. ZMIANY W PRZEBIECIACH LUB DODATKOWE PRZEBIECIA
21. PRZEWÓD WENTYLACJI
22. ZMIANA TYNKU RYTLIOWANE NA GŁADKI
23. ZMIANA OŚCIEŻY OKIENNYCH Z BLACHY NA TYNKOWANE

25. ZMNIJSZENIE WYSOKOŚCI DRZWI Z 215 NA 200 CM
26. ZWIĘKSZENIE OBUDOWY PIONU

ZMIANY W OKŁADZINACH I DETALACH ELEWACYJNYCH:

- BLACHA ALUMINIOWA PREFA W KOLORZE P30 ZIELONA PATYNA,
RĄBEK STOJĄCY, UKŁAD PIONOWY, PODZIAŁ NA NIEREGULARNE PASY I
WYRÓWNYWANO DO OKIEN





- OBROBKA Z BLACHY ALUMINIOWEJ PREFA W KOLORZE P.10 ZIELONA PATYNA
- BLACHA ALUMINIOWA PREFA W KOLORZE CIEMNOSZARYM NR 23 (RAL 7022)
- OBROBKA OŚCIEŻY Z BLACHY ALUMINIOWEJ PREFA W KOLORZE CIEMNOSZARYM NR 23 (RAL 7022)
- TYNK GŁADKI, KOLOR SZARY

- OBRÓBKA Z BLACHY PÓWLEKANEJ, KOLOR SZARY - DOPASOWANY DO OKŁADZINY ELEWACYJNEJ, MATOWY
- OŚCIEŻ TYNKOWANA

WZROK

GARAŻAMI: ZAMKNIĘTYMI, WYŁUDKOWANYMI GARAŻ 14 GARAŻY ZAMKNIĘTYMI, WŁAŚCICIELCYCH, Z ZAGROŻENIEM WYBUCHU, SPODŁOŻENIEM, WYBUCHU, WYBUCHU, WYBUCHU, WYBUCHU, WYBUCHU, STANOWISKAMI POSTOJOWYMI, DO JEDNOSTKI	
PROJEKTANT	NR UPRAWNIENI
BARTŁOŃSKI DRABIK	MPOIA/077/2013
TYTUŁ RYSUNKU	PCOSP:
ZAGROŻENIEM WYBUCHU, SPODŁOŻENIEM, WYBUCHU, WYBUCHU, WYBUCHU, WYBUCHU, WYBUCHU, STANOWISKAMI POSTOJOWYMI, DO JEDNOSTKI	

ELEMENT PROJEKTU PROJEKT ARCHITEKTONICZNO-BUDOWLANY		NUMER RYSUNKU A.06
BRANŻA ARCHITEKTURA		
DATA I WERSJA	SKALA	

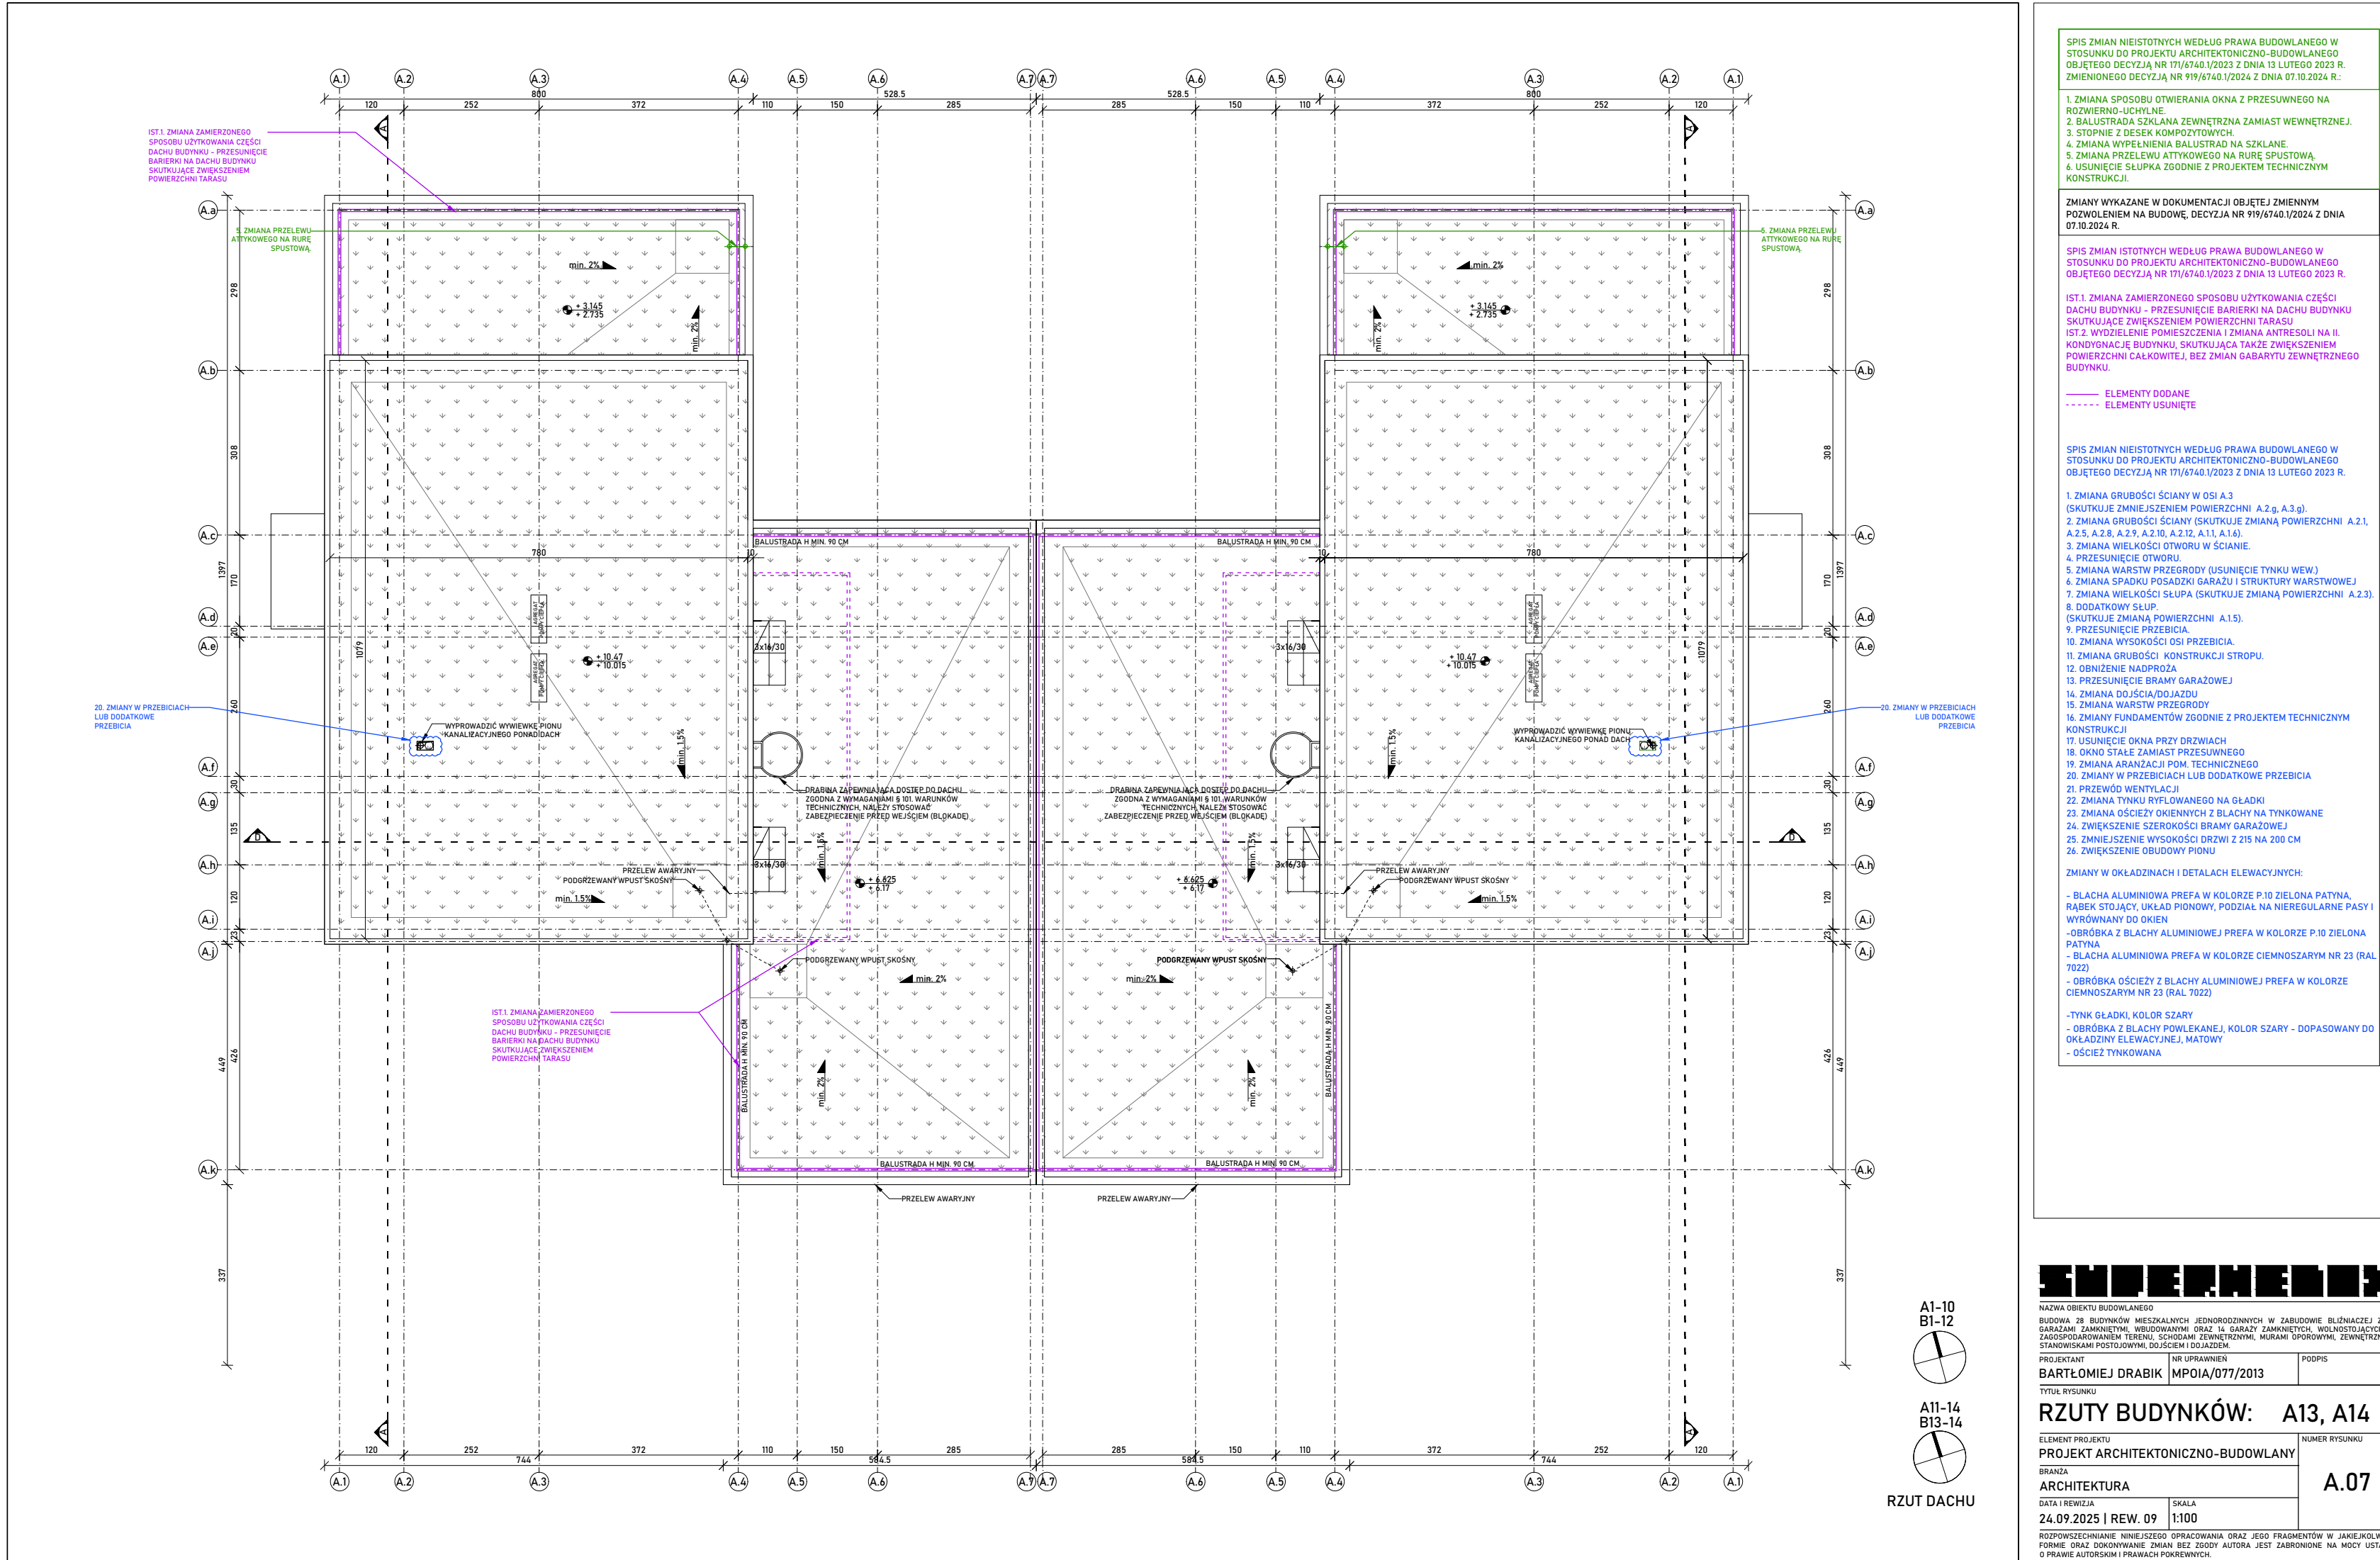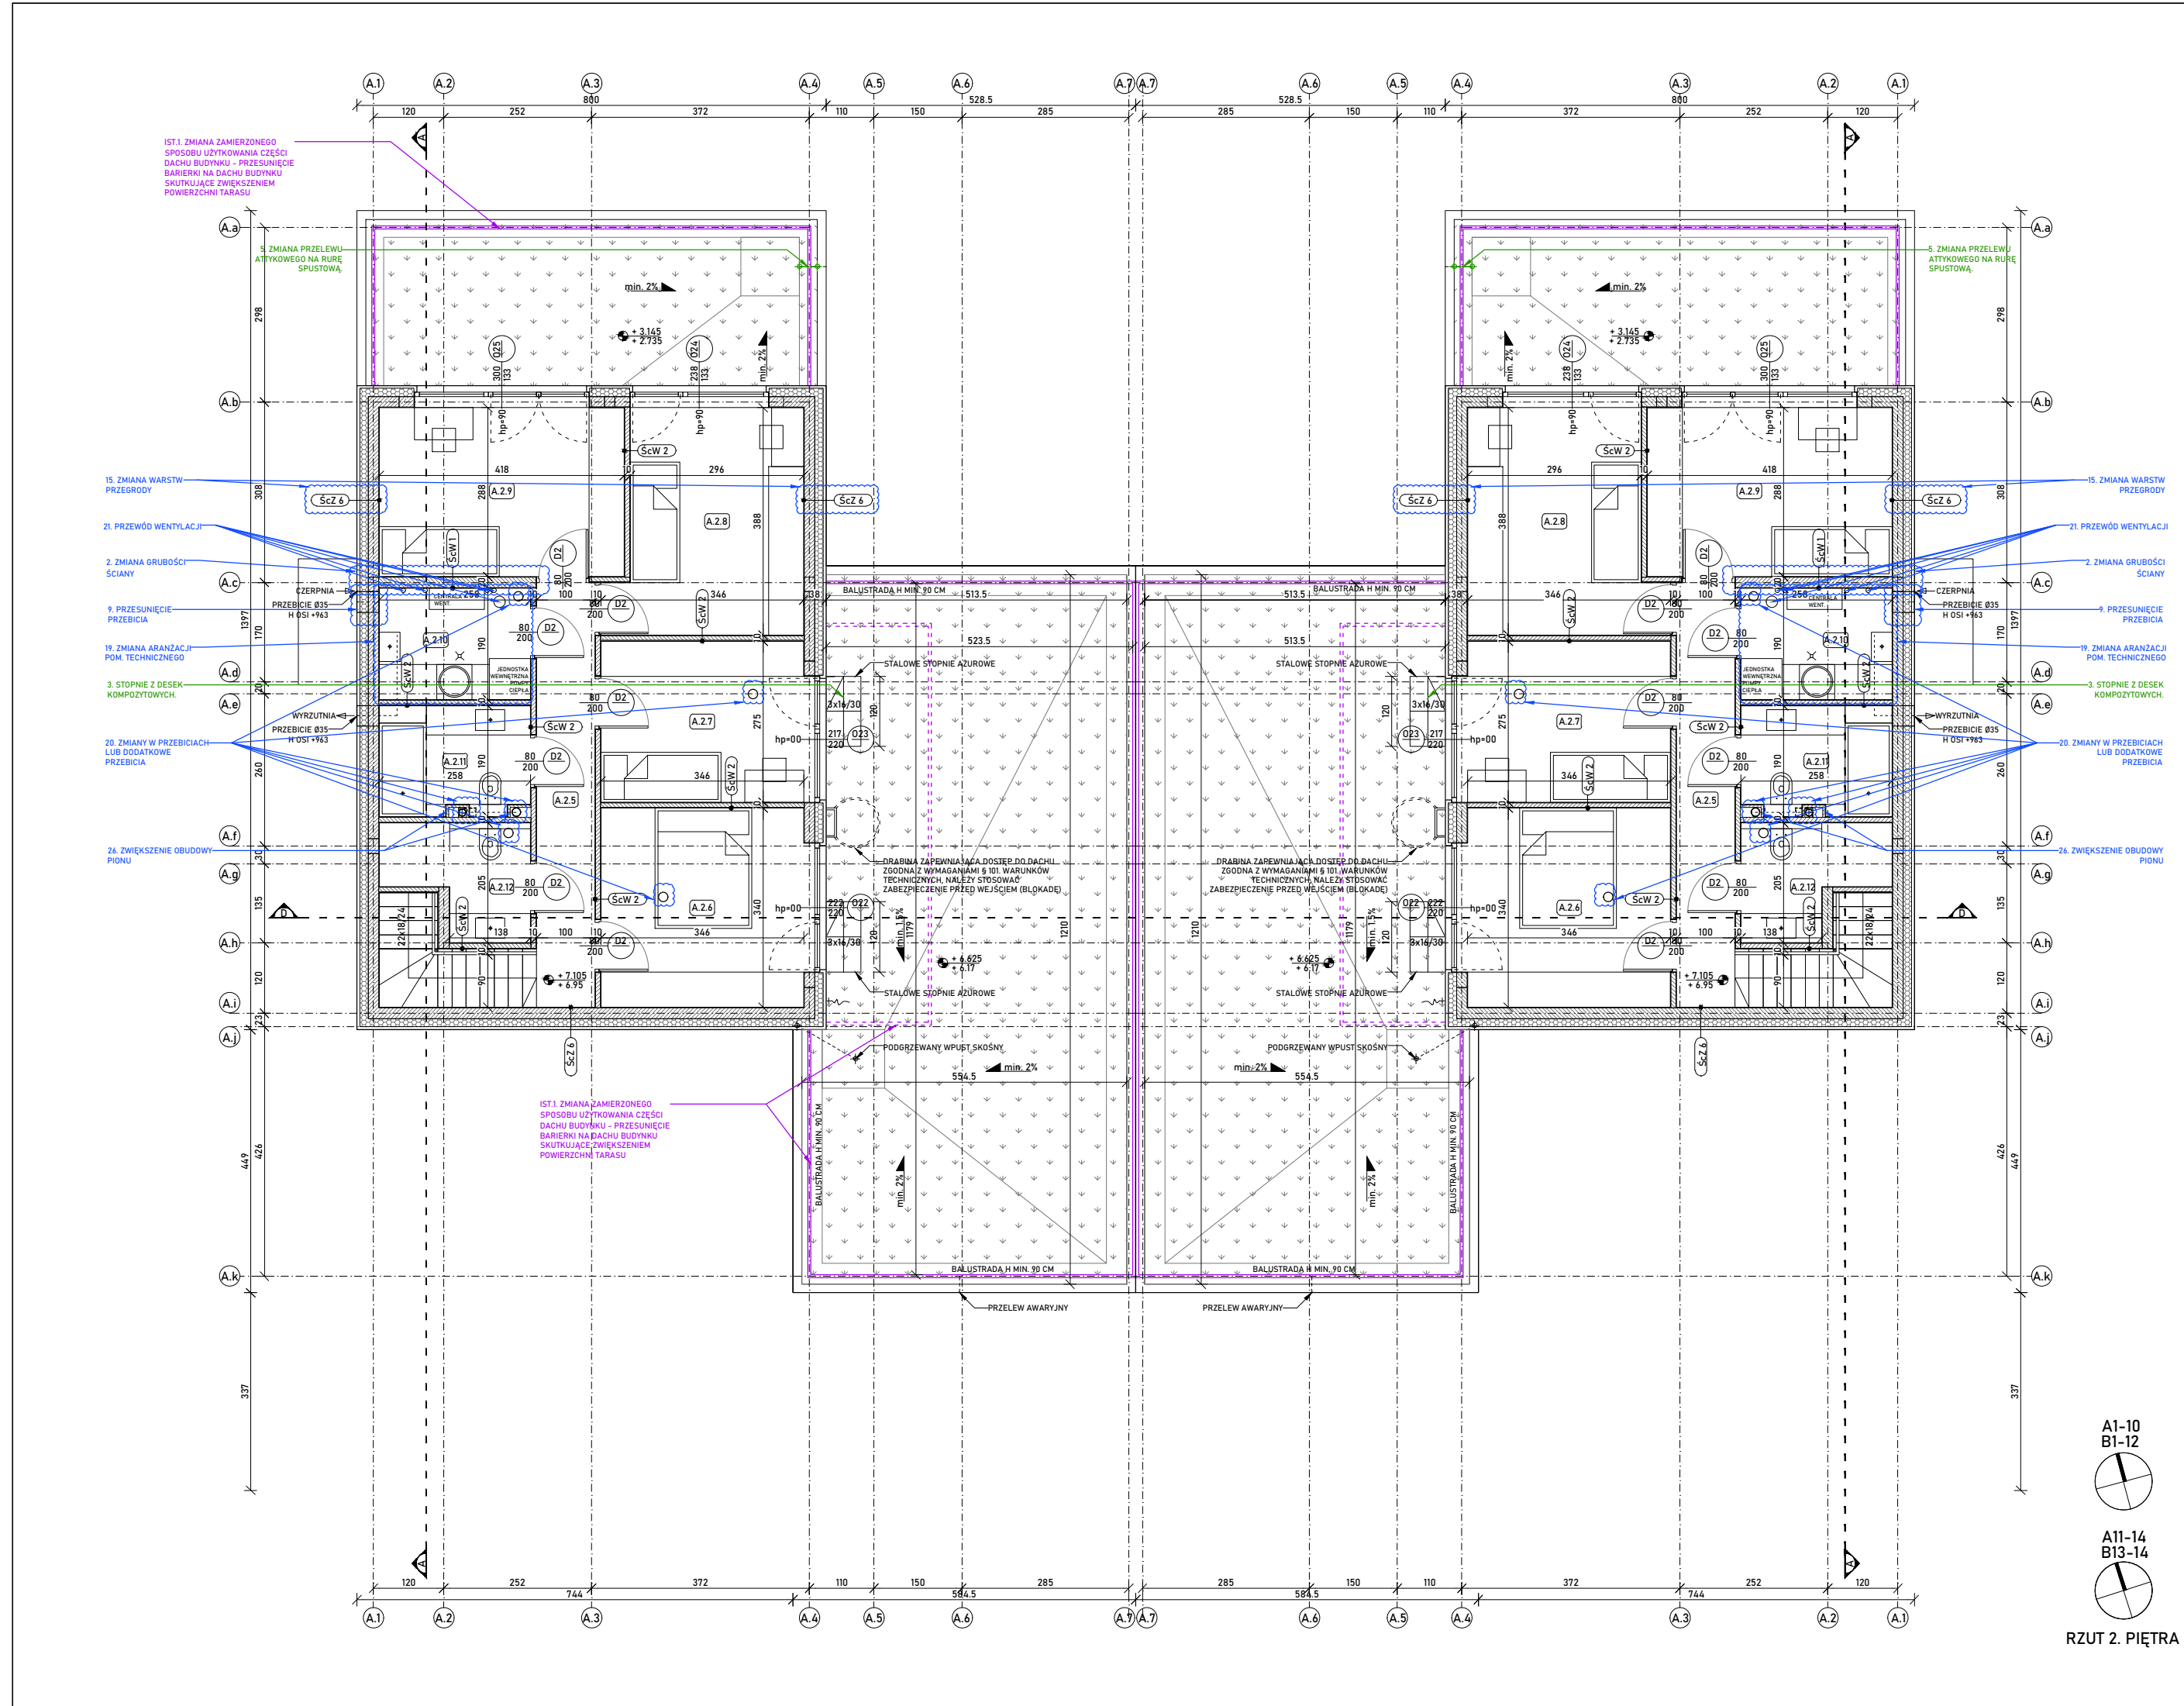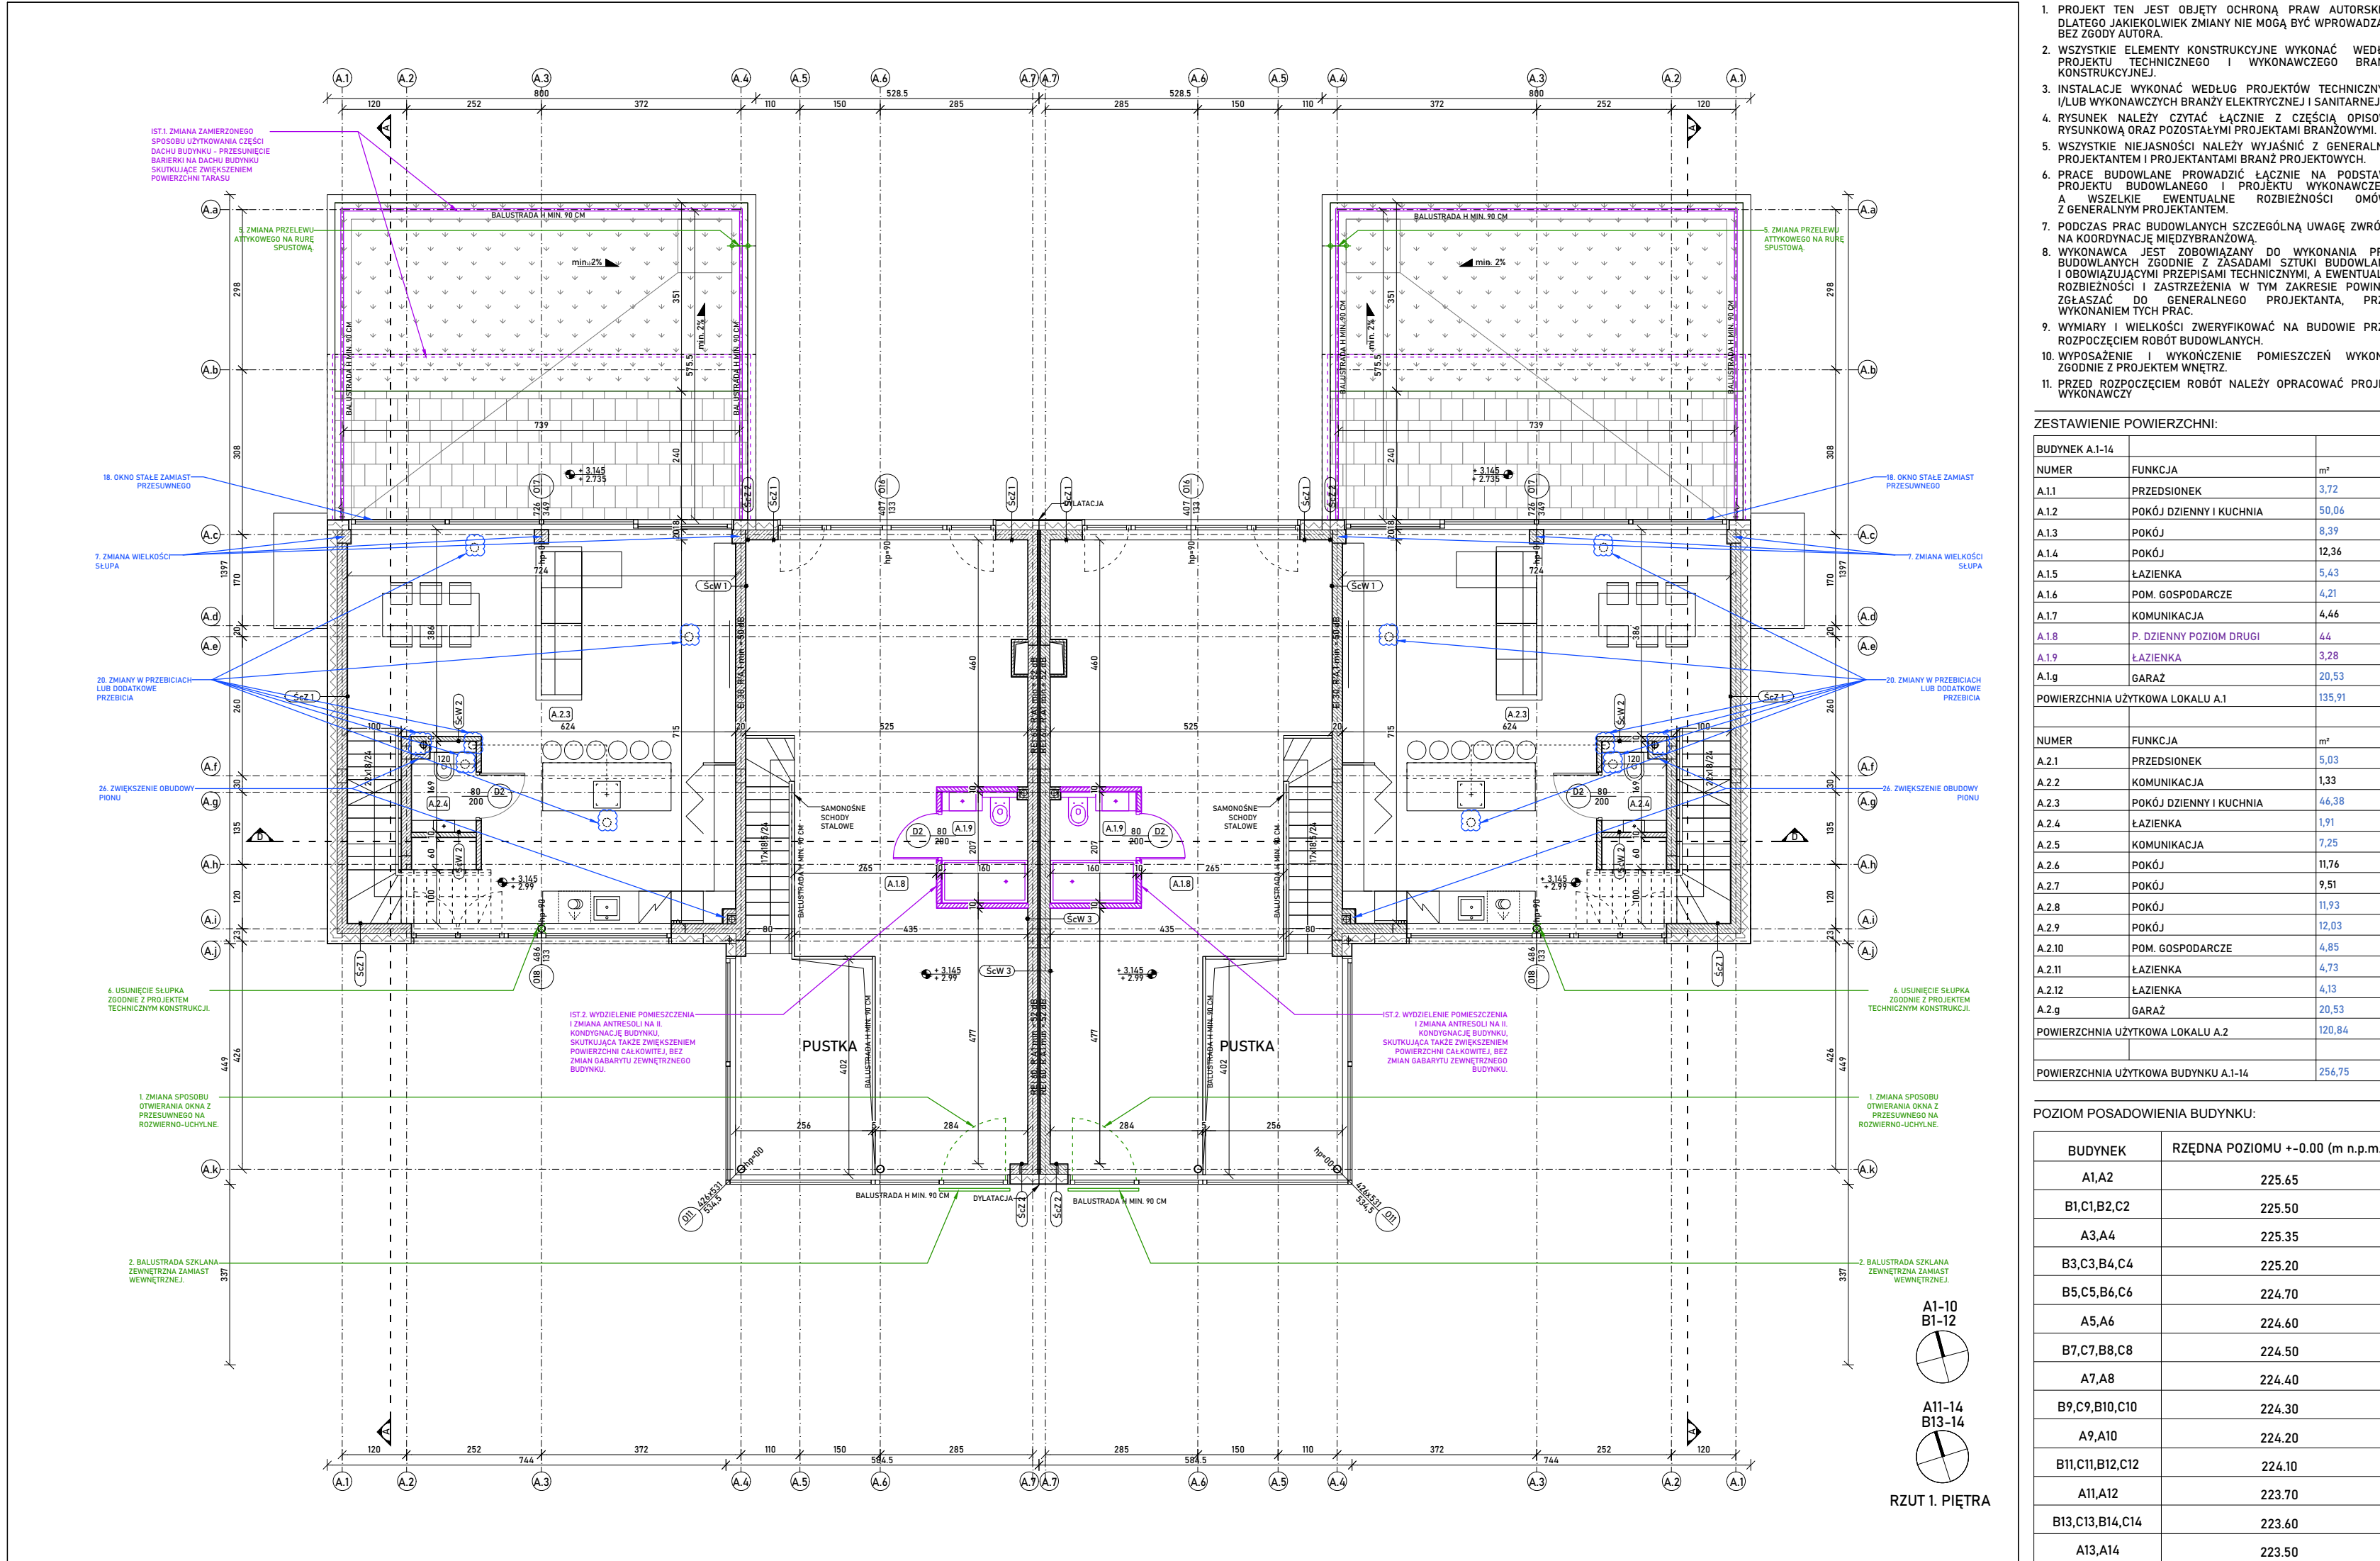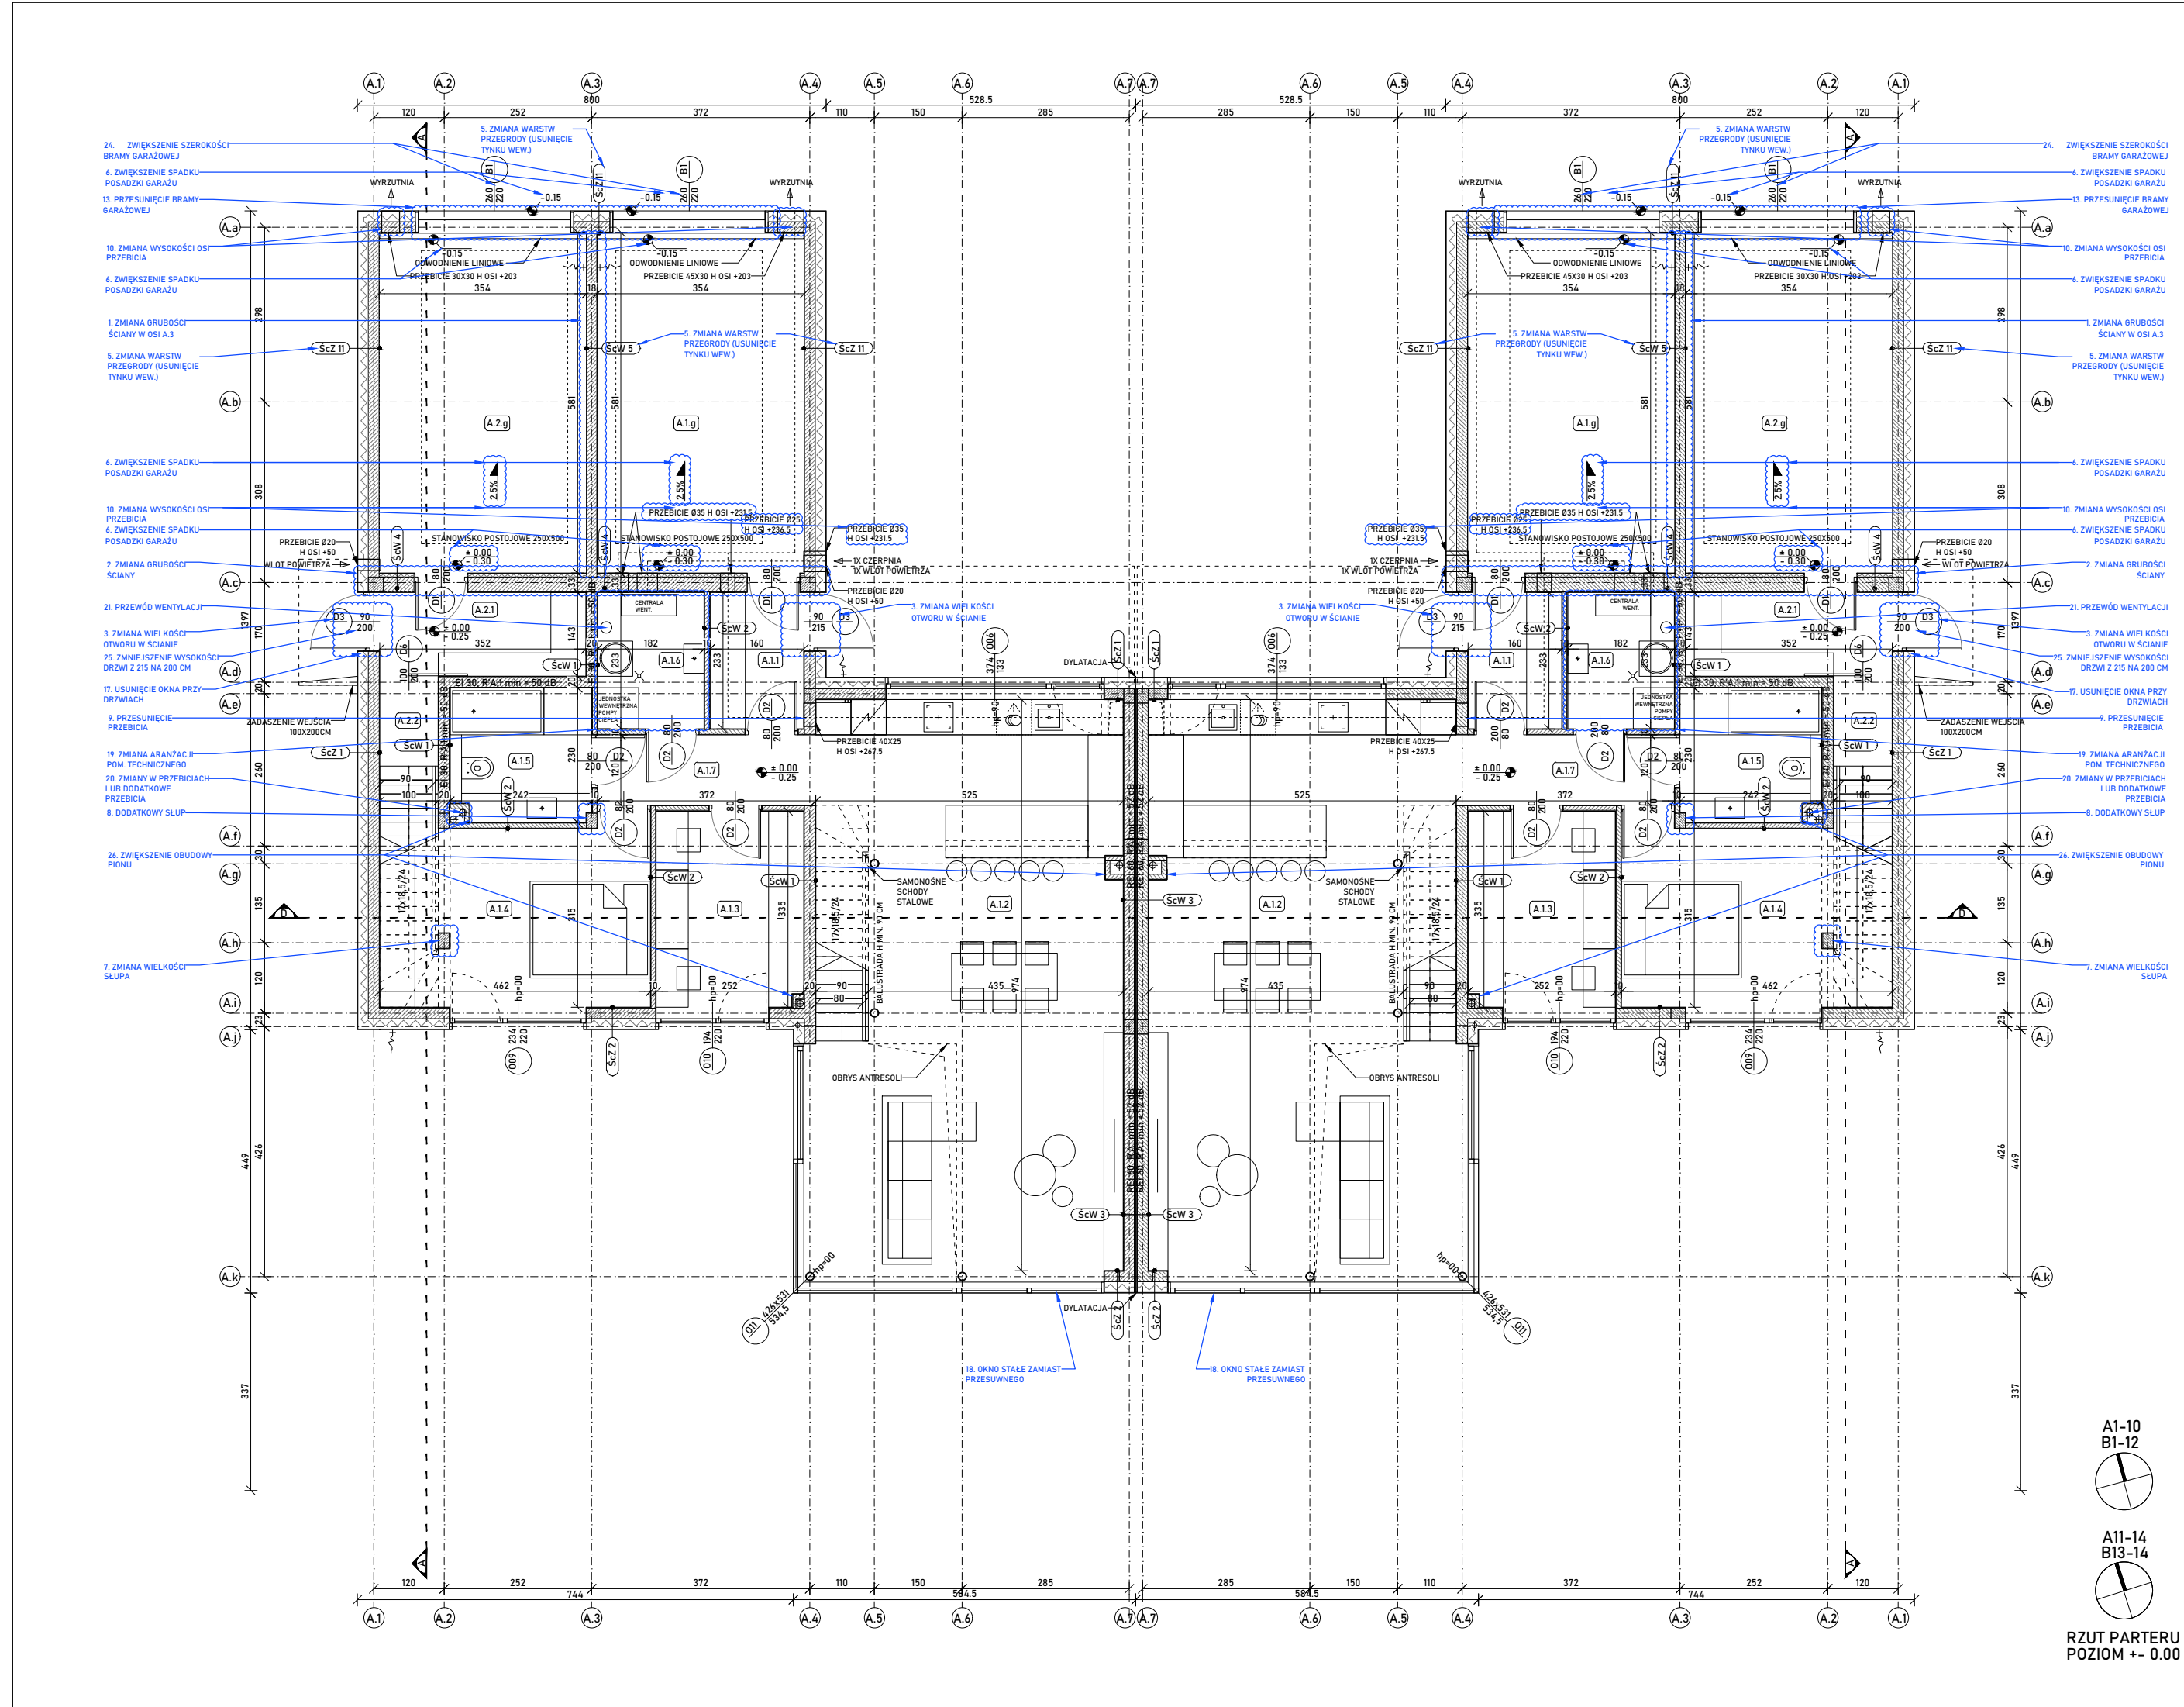

PROJEKT NIE JEST OBJEKT OCHRONY PRAW AUTORSKICH.

WSKAZANE ELEMENTY KONSTRUKCYJNE SĄ WYKONANE WEDŁUG PROJEKTU TECHNICZNEGO I WYKONAWCZEGO KONSTRUKCJI.

INSTALACJE WYKONANE WEDŁUG PROJEKTU TECHNICZNEGO (LUB WYKONAWCZEGO) BRANŻY ELEKTRYCZNEJ I SANITARNEJ.

RYSUNEK NALEŻY CZYTAĆ ŁĄCZNIE Z CZĘŚCIĄ SPISOWĄ, RYSUNKOWĄ ORAZ DOPOSIĄTAMI PROJEKTANTÓW.

WSKAZANE NIEJASNOŚCI NALEŻY WYJAŚNIĆ Z GENERALNYM PROJEKTANTEM I PROJEKTANTAMI BRANŻ PROJEKTOWYCH.

PRACE BUDOWLANE PROWADZIĆ ŁĄCZNIE NA PRZEDSTAWIENIE PROJEKTU BUDOWLANEGO I PROJEKTU WYKONAWCZEGO, Z GENERALNYM PROJEKTANTEM.

PODZAS PRAC BUDOWLANICH SZCZEGÓLNA UWAGĘ ZWRÓCIĆ NA WYKONANIE WIEDZĄCZĄCĄ.

WYKONAWCA JEST ZOBOWIĄZANY DO WYKONANIA PRAC BUDOWLANICH ZGODNIE Z ZAŁOŻENIAMI I WSKAZANAMI I OBLICZENIAMI PRZEPISAMI TECHNICZNYMI, A EWENTUALNE ROZBIENNOŚCI I ZASTRZEŻENIA W TYM ZAKRESIE POWINIEN ZASŁAŻĄ DO GENERALNEGO PROJEKTANTA, PRZED WYKONANIEM TYCH PRAC.

WYMIARY I WIELKOŚCI ZWERYFIKOWAĆ NA BUDOWIE PRZED ZACZĄTKIEM PRAC BUDOWLANICH.

WYPOSAŻENIE I WYKONCZENIE POMIESZCZEŃ WYKONAĆ ZGODNIE Z PROJEKTEM WNEŹRZ.

PRZED ROZPOCZĘCIEM ROBÓT NALEŻY OPRAWIĆ PROJEKT WYKONAWCZY.

ZESTAWIENIE POWIERZCHNI:

BUDYNEK A1-A14

NUMER	FUNKCJA	m ²
A1.1	PRZEDSIÓDNEK	3,72
A1.2	POM. DZIENNY KUCHNIA	10,08
A1.3	POM. DZIENNY KUCHNIA	9,39
A1.4	POM. DZIENNY KUCHNIA	12,36
A1.5	ŁAZIENKA	5,63
A1.6	POM. GOSPODARCZE	6,31
A1.7	KOMUNIKACJA	4,46
A1.8	P. DZIENNY POZIOM DRUGI	46
A1.9	ŁAZIENKA	3,28
A1.10	GARAŻ	191
POWIERZCHNIA UŻYTKOWA LOKALU A1		185,91

NUMER

FUNKCJA

m²

A2.1	PRZEDSIÓDNEK	5,03
A2.2	KOMUNIKACJA	1,33
A2.3	POM. DZIENNY KUCHNIA	48,58
A2.4	ŁAZIENKA	191
A2.5	KOMUNIKACJA	7,76
A2.6	POM. DZIENNY KUCHNIA	10,75
A2.7	POM. DZIENNY KUCHNIA	9,93
A2.8	POM. DZIENNY KUCHNIA	11,91
A2.9	POM. DZIENNY KUCHNIA	12,03
A2.10	POM. GOSPODARCZE	4,85
A2.11	ŁAZIENKA	20,53
A2.12	ŁAZIENKA	20,53
A2.13	GARAŻ	26,53
POWIERZCHNIA UŻYTKOWA LOKALU A2		120,86

NUMER

FUNKCJA

m²

A3.1	PRZEDSIÓDNEK	25,67
A3.2	POM. DZIENNY KUCHNIA	25,67
A3.3	POM. DZIENNY KUCHNIA	25,67
A3.4	POM. DZIENNY KUCHNIA	25,67
A3.5	ŁAZIENKA	25,67
A3.6	POM. GOSPODARCZE	25,67
A3.7	KOMUNIKACJA	25,67
A3.8	P. DZIENNY POZIOM DRUGI	25,67
A3.9	ŁAZIENKA	25,67
A3.10	GARAŻ	25,67
POWIERZCHNIA UŻYTKOWA LOKALU A3		256,7

NUMER

FUNKCJA

m²

A4.1	PRZEDSIÓDNEK	225,50
A4.2	POM. DZIENNY KUCHNIA	225,50
A4.3	POM. DZIENNY KUCHNIA	225,50
A4.4	POM. DZIENNY KUCHNIA	225,50
A4.5	ŁAZIENKA	225,50
A4.6	POM. GOSPODARCZE	225,50
A4.7	KOMUNIKACJA	225,50
A4.8	P. DZIENNY POZIOM DRUGI	225,50
A4.9	ŁAZIENKA	225,50
A4.10	GARAŻ	225,50
POWIERZCHNIA UŻYTKOWA LOKALU A4		2255,0

NUMER

FUNKCJA

m²

A5.1	PRZEDSIÓDNEK	225,50
A5.2	POM. DZIENNY KUCHNIA	225,50
A5.3	POM. DZIENNY KUCHNIA	225,50
A5.4	POM. DZIENNY KUCHNIA	225,50
A5.5	ŁAZIENKA	225,50
A5.6	POM. GOSPODARCZE	225,50
A5.7	KOMUNIKACJA	225,50
A5.8	P. DZIENNY POZIOM DRUGI	225,50
A5.9	ŁAZIENKA	225,50
A5.10	GARAŻ	225,50
POWIERZCHNIA UŻYTKOWA LOKALU A5		2255,0

NUMER

FUNKCJA

m²

A6.1	PRZEDSIÓDNEK	225,50
A6.2	POM. DZIENNY KUCHNIA	225,50
A6.3	POM. DZIENNY KUCHNIA	225,50
A6.4	POM. DZIENNY KUCHNIA	225,50
A6.5	ŁAZIENKA	225,50
A6.6	POM. GOSPODARCZE	225,50
A6.7	KOMUNIKACJA	225,50
A6.8	P. DZIENNY POZIOM DRUGI	225,50
A6.9	ŁAZIENKA	225,50
A6.10	GARAŻ	225,50
POWIERZCHNIA UŻYTKOWA LOKALU A6		2255,0

NUMER

FUNKCJA

m²

A7.1	PRZEDSIÓDNEK	225,50
A7.2	POM. DZIENNY KUCHNIA	225,50
A7.3	POM. DZIENNY KUCHNIA	225,50
A7.4	POM. DZIENNY KUCHNIA	225,50
A7.5	ŁAZIENKA	225,50
A7.6	POM. GOSPODARCZE	225,50
A7.7	KOMUNIKACJA	225,50
A7.8	P. DZIENNY POZIOM DRUGI	225,50
A7.9	ŁAZIENKA	225,50
A7.10	GARAŻ	225,50
POWIERZCHNIA UŻYTKOWA LOKALU A7		2255,0

NUMER

FUNKCJA

m²

A8.1	PRZEDSIÓDNEK	225,50
A8.2	POM. DZIENNY KUCHNIA	225,50
A8.3	POM. DZIENNY KUCHNIA	225,50
A8.4	POM. DZIENNY KUCHNIA	225,50
A8.5	ŁAZIENKA	225,50
A8.6	POM. GOSPODARCZE	225,50
A8.7	KOMUNIKACJA	225,50
A8.8	P. DZIENNY POZIOM DRUGI	225,50
A8.9	ŁAZIENKA	225,50
A8.10	GARAŻ	225,50
POWIERZCHNIA UŻYTKOWA LOKALU A8		2255,0

NUMER

FUNKCJA

m²

A9.1	PRZEDSIÓDNEK	225,50
A9.2	POM. DZIENNY KUCHNIA	225,50
A9.3	POM. DZIENNY KUCHNIA	225,50
A9.4	POM. DZIENNY KUCHNIA	225,50
A9.5	ŁAZIENKA	225,50
A9.6	POM. GOSPODARCZE	225,50
A9.7	KOMUNIKACJA	225,50
A9.8	P. DZIENNY POZIOM DRUGI	225,50
A9.9	ŁAZIENKA	225,50
A9.10	GARAŻ	225,50
POWIERZCHNIA UŻYTKOWA LOKALU A9		2255,0

NUMER

FUNKCJA

m²

A10.1	PRZEDSIÓDNEK	225,50
A10.2	POM. DZIENNY KUCHNIA	225,50
A10.3	POM. DZIENNY KUCHNIA	225,50
A10.4	POM. DZIENNY KUCHNIA	225,50
A10.5	ŁAZIENKA	225,50
A10.6	POM. GOSPODARCZE	225,50
A10.7	KOMUNIKACJA	225,50
A10.8	P. DZIENNY POZIOM DRUGI	225,50
A10.9	ŁAZIENKA	225,50
A10.10	GARAŻ	225,50
POWIERZCHNIA UŻYTKOWA LOKALU A10		2255,0

NUMER

FUNKCJA

m²

A11.1	PRZEDSIÓDNEK	225,50
A11.2	POM. DZIENNY KUCHNIA	225,50
A11.3	POM. DZIENNY KUCHNIA	225,50
A11.4	POM. DZIENNY KUCHNIA	225,50
A11.5	ŁAZIENKA	225,50
A11.6	POM. GOSPODARCZE	225,50
A11.7	KOMUNIKACJA	225,50
A11.8	P. DZIENNY POZIOM DRUGI	225,50
A11.9	ŁAZIENKA	225,50
A11.10	GARAŻ	225,50
POWIERZCHNIA UŻYTKOWA LOKALU A11		2255,0

NUMER

FUNKCJA

m²

A12.1	PRZEDSIÓDNEK	225,50
A12.2	POM. DZIENNY KUCHNIA	225,50
A12.3	POM. DZIENNY KUCHNIA	225,50
A12.4	POM. DZIENNY KUCHNIA	225,50
A12.5	ŁAZIENKA	225,50
A12.6	POM. GOSPODARCZE	225,50
A12.7	KOMUNIKACJA	225,50
A12.8	P. DZIENNY POZIOM DRUGI	225,50
A12.9	ŁAZIENKA	225,50
A12.10	GARAŻ	225,50
POWIERZCHNIA UŻYTKOWA LOKALU A12		2255,0

NUMER

FUNKCJA

m²

A13.1	PRZEDSIÓDNEK	225,50
A13.2	POM. DZIENNY KUCHNIA	225,50
A13.3	POM. DZIENNY KUCHNIA	225,50
A13.4	POM. DZIENNY KUCHNIA	225,50
A13.5	ŁAZIENKA	225,50
A13.6	POM. GOSPODARCZE	225,50
A13.7	KOMUNIKACJA	225,50
A13.8	P. DZIENNY POZIOM DRUGI	225,50
A13.9	ŁAZIENKA	225,50
A13.10	GARAŻ	225,50
POWIERZCHNIA UŻYTKOWA LOKALU A13		2255,0

NUMER

FUNKCJA

m²

A14.1	PRZEDSIÓDNEK	225,50
A14.2	POM. DZIENNY KUCHNIA	225,50
A14.3	POM. DZIENNY KUCHNIA	225,50
A14.4	POM. DZIENNY KUCHNIA	225,50
A14.5	ŁAZIENKA	225,50
A14.6	POM. GOSPODARCZE	225,50
A14.7	KOMUNIKACJA	225,50
A14.8	P. DZIENNY POZIOM DRUGI	225,50
A14.9	ŁAZIENKA	225,50
A14.10	GARAŻ	225,50
POWIERZCHNIA UŻYTKOWA LOKALU A14		2255,0

NUMER

FUNKCJA

m²

A15.1	PRZEDSIÓDNEK	225,50
A15.2	POM. DZIENNY KUCHNIA	225,50
A15.3	POM. DZIENNY KUCHNIA	225,50
A15.4	POM. DZIENNY KUCHNIA	225,50
A15.5	ŁAZIENKA	225,50
A15.6	POM. GOSPODARCZE	225,50
A15.7	KOMUNIKACJA	225,50
A15.8	P. DZIENNY POZIOM DRUGI	225,50
A15.9	ŁAZIENKA	225,50
A15.10	GARAŻ	225,50
POWIERZCHNIA UŻYTKOWA LOKALU A15		2255,0

NUMER

FUNKCJA

m²

A16.1	PRZEDSIÓDNEK	225,50
A16.2	POM. DZIENNY KUCHNIA	225,50
A16.3	POM. DZIENNY KUCHNIA	225,50
A16.4	POM. DZIENNY KUCHNIA	225,50
A16.5	ŁAZIENKA	225,50
A16.6	POM. GOSPODARCZE	225,50
A16.7	KOMUNIKACJA	225,50
A16.8	P. DZIENNY POZIOM DRUGI	225,50
A16.9	ŁAZIENKA	225,50
A16.10	GARAŻ	225,50
POWIERZCHNIA UŻYTKOWA LOKALU A16		2255,0

NUMER

FUNKCJA

m²

A17.1	PRZEDSIÓDNEK	225,50
A17.2	POM. DZIENNY KUCHNIA	225,50
A17.3	POM. DZIENNY KUCHNIA	225,50
A17.4	POM. DZIENNY KUCHNIA	225,50
A17.5	ŁAZIENKA	225,50
A17.6	POM. GOSPODARCZE	225,50
A17.7	KOMUNIKACJA	225,50
A17.8	P. DZIENNY POZIOM DRUGI	225,50
A17.9	ŁAZIENKA	225,50
A17.10	GARAŻ	225,50
POWIERZCHNIA UŻYTKOWA LOKALU A17		2255,0

NUMER

FUNKCJA

m²

A18.1	PRZEDSIÓDNEK	225,50
A18.2	POM. DZIENNY KUCHNIA	225,50
A18.3	POM. DZIENNY KUCHNIA	225,50
A18.4	POM. DZIENNY KUCHNIA	225,50
A18.5	ŁAZIENKA	225,50
A18.6	POM. GOSPODARCZE	225,50
A18.7	KOMUNIKACJA	225,50
A18.8	P. DZIENNY POZIOM DRUGI	225,50
A18.9	ŁAZIENKA	225,50
A18.10	GARAŻ	225,50
POWIERZCHNIA UŻYTKOWA LOKALU A18		2255,0

NUMER

FUNKCJA

m²

A19.1	PRZEDSIÓDNEK	225,50
A19.2	POM. DZIENNY KUCHNIA	225,50
A19.3	POM. DZIENNY KUCHNIA	225,50
A19.4	POM. DZIENNY KUCHNIA	225,50
A19.5	ŁAZIENKA	225,50
A19.6	POM. GOSPODARCZE	225,50
A19.7	KOMUNIKACJA	225,50
A19.8	P. DZIENNY POZIOM DRUGI	225,50
A19.9	ŁAZIENKA	225,50
A19.10	GARAŻ	225,50
POWIERZCHNIA UŻYTKOWA LOKALU A19		2255,0

NUMER

FUNKCJA

m²

A20.1	PRZEDSIÓDNEK	225,50
A20.2	POM. DZIENNY KUCHNIA	225,50
A20.3	POM. DZIENNY KUCHNIA	225,50
A20.4	POM. DZIENNY KUCHNIA	225,50
A20.5	ŁAZIENKA	225,50
A20.6	POM. GOSPODARCZE	225,50
A20.7	KOMUNIKACJA	225,50
A20.8	P. DZIENNY POZIOM DRUGI	225,50
A20.9	ŁAZIENKA	225,50
A20.10	GARAŻ	225,50
POWIERZCHNIA UŻYTKOWA LOKALU A20		2255,0

NUMER

FUNKCJA

m²

A21.1	PRZEDSIÓDNEK	225,50
A21.2	POM. DZIENNY KUCHNIA	225,50
A21.3	POM. DZIENNY KUCHNIA	225,50
A21.4	POM. DZIENNY KUCHNIA	225,50
A21.5	ŁAZIENKA	225,50
A21.6	POM. GOSPODARCZE	225,50
A21.7	KOMUNIKACJA	225,50
A21.8	P. DZIENNY POZIOM DRUGI	225,50
A21.9	ŁAZIENKA	225,50
A21.10	GARAŻ	225,50
POWIERZCHNIA UŻYTKOWA LOKALU A21		2255,0

NUMER

FUNKCJA

m²

A22.1	PRZEDSIÓDNEK	225,50
A22.2	POM. DZIENNY KUCHNIA	225,50
A22.3	POM. DZIENNY KUCHNIA	225,50
A22.4	POM. DZIENNY KUCHNIA	225,50
A22.5	ŁAZIENKA	225,50
A22.6	POM. GOSPODARCZE	225,50
A22.7	KOMUNIKACJA	225,50
A22.8	P. DZIENNY POZIOM DRUGI	225,50
A22.9	ŁAZIENKA	225,50
A22.10	GARAŻ	225,50
POWIERZCHNIA UŻYTKOWA LOKALU A22		2255,0

NUMER

FUNKCJA

m²

A23.1	PRZEDSIÓDNEK	225,50
A23.2	POM. DZIENNY KUCHNIA	225,50
A23.3	POM. DZIENNY KUCHNIA	225,50
A23.4	POM. DZIENNY KUCHNIA	225,50
A23.5	ŁAZIENKA	225,50
A23.6	POM. GOSPODARCZE	225,50
A23.7	KOMUNIKACJA	225,50
A23.8	P. DZIENNY POZIOM DRUGI	225,50
A23.9	ŁAZIENKA	225,50
A23.10	GARAŻ	225,50
POWIERZCHNIA UŻYTKOWA LOKALU A23		2255,0

NUMER

FUNKCJA

m²

A24.1	PRZEDSIÓDNEK	225,50
A24.2	POM. DZIENNY KUCHNIA	225,50
A24.3	POM. DZIENNY KUCHNIA	225,50
A24.4	POM. DZIENNY KUCHNIA	225,50
A24.5	ŁAZIENKA	225,50
A24.6	POM. GOSPODARCZE	225,50
A24.7	KOMUNIKACJA	225,50
A24.8	P. DZIENNY POZIOM DRUGI	225,50
A24.9	ŁAZIENKA	225,50
A24.10	GARAŻ	225,50
POWIERZCHNIA UŻYTKOWA LOKALU A24		2255,0

NUMER

FUNKCJA

m²

A25.1	PRZEDSIÓDNEK	225,50
A25.2	POM. DZIENNY KUCHNIA	225,50
A25.3	POM. DZIENNY KUCHNIA	225,50
A25.4	POM. DZIENNY KUCHNIA	225,50
A25.5	ŁAZIENKA	225,50
A25.6	POM. GOSPODARCZE	225,50
A25.7	KOMUNIKACJA	225,50
A25.8	P. DZIENNY POZIOM DRUGI	225,50
A25.9	ŁAZIENKA	225,50
A25.10	GARAŻ	225,50
POWIERZCHNIA UŻYTKOWA LOKALU A25		2255,0

NUMER

FUNKCJA

m²





A26.1	PRZEDSIÓDNEK	225,50
A26.2	POM. DZIENNY KUCHNIA	225,50
A26.3	POM. DZIENNY KUCHNIA	225,50
A26.4	POM. DZIENNY KUCHNIA	225,50
A26.5	ŁAZIENKA	225,50
A26.6	POM. GOSPODARCZE	225,50
A26.7	KOMUNIKACJA	225,50
A26.8	P. DZIENNY POZIOM DRUGI	225,50
A26.9	ŁAZIENKA	225,50
A26.10	GARAŻ	225,50
POWIERZCHNIA UŻYTKOWA LOKALU A26		2255,0

NUMER





FUNKCJA

m²

A27.1	PRZEDSIÓDNEK	225,50
A27.2	POM. DZIENNY KUCHNIA	225,50
A27.3	POM. DZIENNY KUCHNIA	225,50
A27.4	POM. DZIENNY KUCHNIA	225,50
A27.5	ŁAZIENKA	225,50
A27.6	POM. GOSPODARCZE	225,50
A27.7	KOMUNIKACJA	225,50
A27.8	P. DZIENNY POZIOM DRUGI	225,50
A27.9	<	

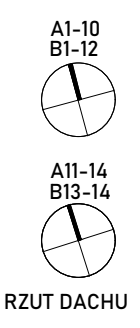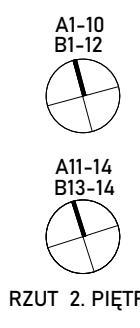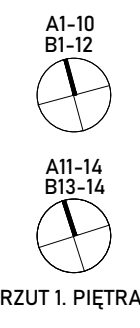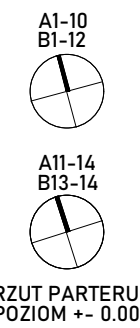

- FORMY ORAZ DOKONYWANIE ZMIAN BEZ ZGODY AUTORA JEST ZABRONIONE NA MOCY USTAW
O PRAWIE AUTORSKIM I PRAWACH POWIĄZANYCH.

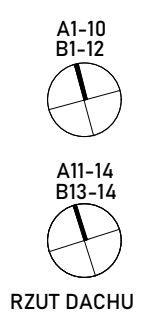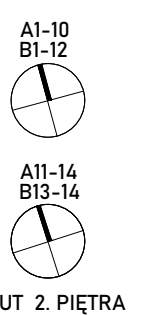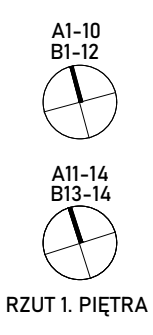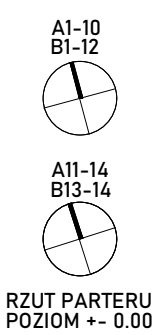

- ZESTAWIENIE POWIERZCHNI:

NUMER	FUNKCJA	m ²
B.2.1	PRZEDSIONEK	3,52
B.2.2	POM. GOSPODARCZE	5,44
B.2.3	ŁAZIENKA	5,35
B.2.4	POKÓJ	16,56
B.2.5	KOMUNIKACJA	2,34
B.2.6	POKÓJ DZIENNY I KUCHNIA	57,65
B.2.7	P. DZIENNY POZIOM DRUGI	51,74
B.2.8	ŁAZIENKA	3,91
POWIERZCHNIA UŻYTKOWA LOKALU B.2		144,49

POZIOM POSADOWIENIA BUDYNKU:

BUDYNEK	RZĘDNA PODZIOMU +0.00 (m n.p.m.)
A1,A2	225.65
B1,C1,B2,C2	225.50
A3,A4	225.35
B3,C3,B4,C4	225.20
B5,C5,B6,C6	224.70
A5,A6	224.60
B7,C7,B8,C8	224.50
A7,A8	224.40
B9,C9,B10,C10	224.30
A9,A10	224.20
B11,C11,B12,C12	224.10
A11,A12	223.70
B13,C13,B14,C14	223.60
A13,A14	223.50

1. ZMIANA WYPEŁNIENIA BALUSTRAD NA SZKLANE.
2. SCHODY ZEWNĘTRZNE STALOWE LAKIEROWANE NA KOLOR SZARY, STOPNIE Z PŁYT GRANITOWYCH.
3. STOPNIE Z DESEK KOMPÓZYTOWYCH.
4. TYNK GŁADKI ZAMIAST BETONU IMPREGNOWANEGO.
5. WYPEŁNIENIE STROPU Z LEKKIEJ KONSTRUKCJI DREWNIANEJ

- SPIS ZMIAN ISTOTNYCH WEDŁUG PRAWA BUDOWLANEGO W
STOSUNKU DO PROJEKTU ADAPTACYJNOGO BUDOWLANEGO

STOSUNKU DO PROJEKTU ARCHITEKTONICZNO-BUDOWLANEGO
OBJĘTEGO DECYZJĄ NR 171/6740.1/2023 Z DNIA 13 LUTEGO 2023 R.

- IST.1. ZMIANA ZAMIERZONEGO SPOSOBU UŻYTKOWANIA CZĘŚCI DACHU BUDYNKU - PRZESUNIĘCIE BARIERKI NA DACHU BUDYNKU SKUTKUJĄCE ZWIĘKSZENIEM POWIERZCHNI TERASU
IST.2. WYDZIELENIE POMIESZCZENIA I ZMIANA ANTRESOLI NA III. KONDYGNACJĘ BUDYNKU, SKUTKUJĄCĄ TAKŻE ZWIĘKSZENIEM POWIERZCHNI CAŁKOWITEJ, BEZ ZMIAN GABARYTU ZEWNĘTRZNEGO BUDYNKU.

IST.3. LIKWIDACJA OTWORU W STROPIE

———— ELEMENTY DODANE
***** ELEMENTY USUNIĘTE

SPIS ZMIAN NIEISTOTNYCH WEDŁUG PRAWA BUDOWLANEGO W STOSUNKU
DO PROJEKTU ARCHITEKTONICZNO-BUDOWLANEGO OBJĘTEGO DECYZJĄ
NR 171/6740.1/2023 Z DNIA 13 LUTEGO 2023 R.

1. ZNAJOMA GRUBOŚCI SIŁY
2. ZNAJOMA CIĘŻARNOŚĆ POWIERZCHNI c_1, c_2, c_3
3. ZNAJOMA WYSOKOŚĆ SIŁY
4. PRZECIECZNE BRAMY GARARZE
5. ZNAJOMA WYSOKOŚĆ SIŁY PRZEBIEGA
6. ZNAJOMA WARTOŚĆ PRZECIECZA
7. ZNAJOMA PODZIAŁ SIŁY GARARZE I STRUKTURY WARTOŚĆ
8. ZNAJOMA WARTOŚĆ SIŁY PRZEBIEGA
9. OZNACZENIE NAPIĘCIA
10. PRZECIECZNE PRZECIECZA
11. ZNAJOMA GRUBOŚĆ KONSTRUKCJI STROPU
12. ZNAJOMA WARTOŚĆ PRZECIECZNE SIŁY OPORU
13. PRZECIECZNE DŹ
14. ZNAJOMA DZIAŁAJĄCY
15. ZNAJOMA WARTOŚĆ PRZECIECZA
16. ZNAJOMA FUNDAMENTOWANIE ZDROJEM I PROJEKTEM TECHNICZNYM KONSTRUKCJI
17. ZNAJOMA ABRAZJA I POM TECHNICZNY
18. DZIAŁAJĄCY WYWIŁA
19. ZNAJOMA WARTOŚĆ PRZECIECZA I DZIAŁAJĄCY
20. PRZECIECZNE PRZECIECZA
21. ZNAJOMA WARTOŚĆ PRZECIECZA
22. ZNAJOMA SIŁY KONSTRUKCJI I ZŁĄCZY NA PRZYKŁADACH
23. ZNAJOMA SIŁY KONSTRUKCJI I ZŁĄCZY NA PRZYKŁADACH
24. ZNAJOMA WARTOŚĆ PRZECIECZA
25. ZNAJOMA WARTOŚĆ PRZECIECZA
- STOJĄCY, UKŁAD PIONOWY, PODZIAŁ NA NIEREGULARNE PASY I WYRÓWNYANY DO OKIEN
- OBRÓBKA Z BLACHY ALUMINIOWEJ PREFA W KOLORZE P10 ZIELONA PATYNA
 - BLACHA ALUMINIOWA PREFA W KOLORZE CIEMNOSZARYM NR 23 (RAL 7022)
 - OBRÓBKA OŚCIEŻY Z BLACHY ALUMINIOWEJ, PREFA W KOLORZE CIEMNOSZARYM NR 23 (RAL 7022)
- TYNK ŁAGWKI, KOLOR SZARY
- OBRÓBKA Z BLACHY DOWLEKANEJ, KOLOR SZARY - DOPASOWANY DO OKŁADZINY ELEWACYJNEJ, MATOWY
 - OŚCIEŻ TYNKOWANA

	- GOOD! FLEXIBILITY
--	---------------------

[illegible]

REFERENCES

NAZWA OBIEKTU BUDOWLANEGO
BUDOWA 28 KUTYŃKÓW MIESZKALNYCH JEDNORODZINNYCH W ZABUDOWIE BLIŃNACZEJ

GARAŻAMI ZAMKNIĘTYMI, WŁÓDZANYMI ORAZ 14 GARAŻY ZAMKNIĘTYCH, WOLNOSTOJĄCYCH ZAGOSPODAROWANIEM TERENU, SCHODAMI ZEWNĘTRZNYMI, MURAMI OPIOROWYMI, ZEWNĘTRZNYMI STANOWISKAMI POSTOJOWYMI, DOJAZDEM I DOJAZDEM.

PROJEKTANT	NR UPRAWNIEN	PODPIS
BARTŁOMIEJ DRABIK	MPOIA/077/2013	

RZUTY BUDYNKÓW: B5 C5 B6 C6



ELEMENT PROJEKTU	NUMER RYSUNKU
000 - WIELKIE A - POLIMERYZACJA HETEROGENNA - DODATEK 1.1.1	

PRACOWNIA ARCHITEKTURA I BUDOWNICTWO	A 10
BRANŻA	

ARCHITETTURA		A.10
DATA E REVISIONE	SCALA	



ROZPOWISZCZNIANIE NIWIJSZEGO OPRACOWANIA ORAZ JEGO FRAGMENTÓW W JAKIEJŚOLW
EDYSCIE ORAZ POWYKAZANIE ZMIAN BEZ ZOSTAWIENIA JEST ZAPROWADZANE NA MOCY UC





O PRAWIE AUTORSKIM I PRAWACH POŚREDNICH

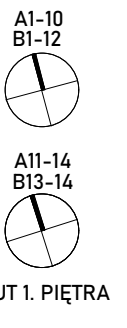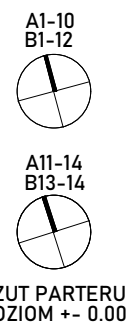

ZESTAWIENIE POWIERZCHNI:		
BUDYNEK B-9-12		
NUMER	FUNKCJA	m ²
B.1.1	PRZEDSIĘBIE	3,68
B.1.2	KOMUNIKACJA	6,22
B.1.3	POKOJ DZIENNY I KUCHNIA	12,24
B.1.4	POKOJ	9,36
B.1.5	POKOJ	9,33
B.1.6	POKOJ	14,34
B.1.7	ŁAZIENKA	5,7
B.1.8	ŁAZIENKA	4,84
B.1.9	POM. GOSPODARCZE	6,19
POWIERZCHNIA UŻYTKOWA LOKALI B.1		89,7
BUDYNEK B-9-2		
NUMER	FUNKCJA	m ²
B.2.1	PRZEDSIĘBIE	3,92
B.2.2	POM. GOSPODARCZE	5,66
B.2.3	ŁAZIENKA	5,35
B.2.4	POKOJ	14,54
B.2.5	KOMUNIKACJA	2,34
B.2.6	POKOJ DZIENNY I KUCHNIA	37,45
B.2.7	ANTYKAL	40,75
POWIERZCHNIA UŻYTKOWA LOKALI B.2		126,99
POWIERZCHNIA UŻYTKOWA LOKALI B.1-1.4		226,69
BUDYNEK C-1-14		
C.1.9	GARAŻ	70,8
C.2.9	GARAŻ	70,8
POWIERZCHNIA RUCHU BUDYNKU C-1-14		41,2

POZIOMY POŚADOWIENIA BUDYNKU:	
BUDYNEK	RZĘDNA POZIOMU +0.00 (m n.p.m.)
A1,A2	225.65
B1,C1,B2,C2	225.50
A3,A4	225.35
B3,C3,B4,C4	225.20
B5,C5,B6,C6	224.70
A5,A6	224.60
B7,C7,B8,C8	224.50
A7,A8	224.40
B7,C7,B10,C10	224.30
A9,A10	224.20
B11,C11,B12,C12	224.10
A11,A12	223.70
B13,C13,B14,C14	223.60
A13,A14	223.50

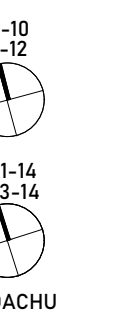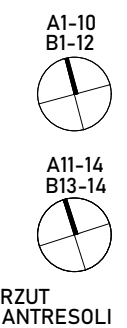[illegible]

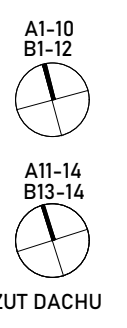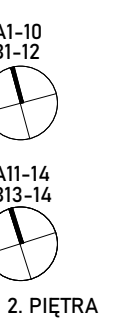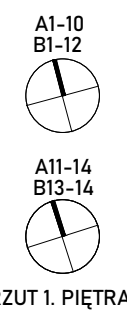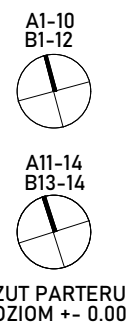



BUDYNEK	RZĘDNA POZIOMU +0.00 (m.n.p.m.)
A1A2	225.65
B1,C1,B2,C2	225.50
A3A4	225.35
B3,C3,B4,C4	225.20
B5,C5,B6,C6	224.70
A5A6	224.40
B7,C7,B8,C8	224.50
A7A8	224.40
B9,C9,B10,C10	224.30
A9A10	224.20
B11,C11,B12,C12	224.10
A11A12	223.70
B13,C13,B14,C14	223.60
A13A14	223.50

ZMIANY W OKŁADZINACH I DETALACH ELEWACYJNYCH:

- BLACHA ALUMINIOWA PREFAB W KOLORZE P.10 ZIELONA PATYNA, RABE STOJĄCY, UKŁAD PIONOWY, PODZIAŁ NA NIEREGULARNE PASY I WYRÓWNAW DO OKIEN
- OBERÓGA Z BLACHY ALUMINIOWEJ PREFAB W KOLORZE P.10 ZIELONA PATYNA
- BLACHA ALUMINIOWA PREFAB W KOLORZE CIEMNOSZARY NR 23 (RAL 7022)
- OBERÓGA OŚCIEŻY Z BLACHY ALUMINIOWEJ PREFAB W KOLORZE CIEMNOSZARY NR 23 (RAL 7022)



- TYNK GŁADKI, KOLOR SZARY

- OBERÓGA Z BLACHY POWŁEKANEJ, KOLOR SZARY - DOPASOWANY DO OKŁADZINY ELEWACYJNEJ, MATOWY
- OŚCIEŻ TYNKOWANA



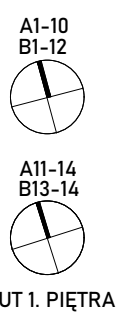
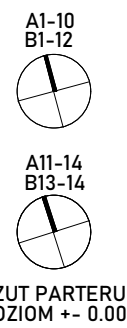


ZESTAWIENIE POWIERZCHNI:		
BUDYNEK B 9-12		
NUMER	FUNKCJA	m ²
B.1.1	PRZEDSIĘBÓR	3,48
B.1.2	KOMUNIKACJA	6,22
B.1.3	POKÓJ DZIENNY I KUCHNIA	12,24
B.1.4	POKÓJ	9,16
B.1.5	POKÓJ	9,33
B.1.6	POKÓJ	14,34
B.1.7	ŁAZIENKA	4,57
B.1.8	ŁAZIENKA	6,84
B.1.9	POM. GOSPODARCZE	4,19
POWIERZCHNIA UŻYTKOWA LOKALU B.1		89,7
BUDYNEK B 1-14		
NUMER	FUNKCJA	m ²
B.2.1	PRZEDSIĘBÓR	3,52
B.2.2	POM. GOSPODARCZE	5,46
B.2.3	ŁAZIENKA	5,35
B.2.4	KOMUNIKACJA	14,54
B.2.5	KOMUNIKACJA	26,54
B.2.6	POKÓJ DZIENNY I KUCHNIA	17,34
B.2.7	ANTYKOR	46,15
POWIERZCHNIA UŻYTKOWA LOKALU B.2		135,89
POWIERZCHNIA UŻYTKOWA BUDYNKU B.1-14		225,69
BUDYNEK C.1-14		
C.1.6	SARAJ	70,6
C.2.9	SARAJ	29,6
POWIERZCHNIA UŻYTKOWA BUDYNKU C.1-14		100,2

POZIOMY POŚADOWIENIA BUDYNKU:	
BUDYNEK	RZĘDNA POZIOMU +-0.00 (0 m n.p.m.)
A1A2	225.65
B1,C1,B2,C2	225.50
A3A4	225.35
B3,C3,B4,C4	225.20
B5,C5,B6,C6	224.70
A5A6	224.60
B7,C7,B8,C8	224.50
A7A8	224.40
B9,C9,B10,C10	224.30
A9,A10	224.20
B11,C11,B12,C12	224.10
A11A12	223.70
B13,C13,B14,C14	223.60
A13,A14	223.50

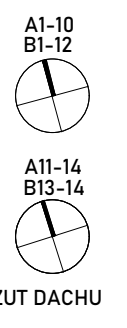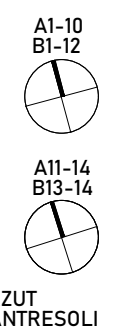

BIURO ARCHITEKTÓW	
NADCA OKREŚLIŁ BUDOWLANĄ	
BUDOWA 2 BUDYNKÓW MIESZKALNYCH JEDNOSTANOWYCH W ZAKRESIE ELEKTROENERGII Z 14 MIEJSCAMI POKOJÓW W BUDYNKU PRZY UL. GARAŻY ZAWARTOŚĆ WSKAZUJĄCĄ NA ZAKŁADANIE PRACOWNI, SZKOLENIE ZAWODNICZYNI, MIAKĄĆ OPIKOWNI, ZWIERZĄTKA WŁASNOŚCI, WYSTĘPIENIE, OŚCIEŻNIE, OŚCIEŻNIE	
PROJEKTANT	NR SPRAWOZDANIA
BARTŁOMIEJ DRABIK	MP/OIA/077/2013
FIDOPS	
TYTUŁ RYSUNKU	
RZUTY BUDYNKÓW: B1, C1, B12, C1	
ELEMENT PROJEKTU	NUMER RYSUNKU
PROJEKT ARCHYTEKTONICZNO-BUDOWLANY	
BRANŻA	
ARCHITEKTURA	
DATA RYSUNKU	SKALA
24.09.2025 REW. 07	1:50A
ROZPOSIĄDZENIEM NUMER 22/200 SPRAWOZDANIE ORAZ JEJ FRAKCYJNYCH W AVALIOWYCH FIDOPS ORAZ KONKREJNEJ DZIS DO DZIS ORAZ JEJ ZAWARTOŚĆ NA MOCY USŁUG	

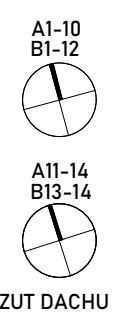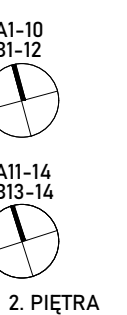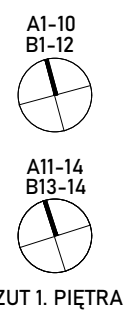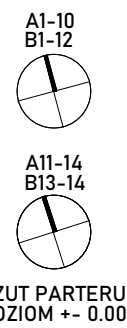ZESTAWIENIE POWIERZCHNI:

POWIERZCHNIA UŻYTKOWA LOKALU B.2	144,69
----------------------------------	--------

POWERTECHNOLÓGIAI ÜZEMTARTÁS ÉS ELLENŐRZÉS

1. ZMIANA WYPEŁNIENIA BALUSTRAD NA SZKLANE.

ZMIANY WYKAZANE W DOKUMENTACJI OBJĘTEJ ZMIENNĄ
POZWOLENIEM NA BUDOWĘ, DECYZJA NR 319/6740/2024 Z DNIA

IST. ZMIANA ZAMIERZONEGO SPOSOBU UŻYTKOWANIA CZĘŚCI

BUDYNKU,
IST.3. LIKWIDACJA OTWORU W STROPIE

SPIS ZAWRÓTNY INDYSTYTUTU WĘGÓW I KRAJÓW GOSPODARSTWA W STOSUNKU DO PROJEKTU ARCHITEKTONICZNO-BUDOWLANEGO OBJĘTEGO DECYZJĄ NR 1214/2346/12013 Z DNIA 15 LUTEGO 2013 R.

4. ZMIANA KIERUNKU SPADKU

11. ZMIANA GRUBOŚCI I PRZESUNIĘCIE ŚCIANY OPOROWEJ

16. ZMIANA ARANŻACJI POM. TECHNICZNEGO
17. DODATKOWA WYWIEWKA

23. ZMNIJSZENIE WYSOKOŚCI DRZWI Z 215 NA 210 CM
24. ZMIANA I OKAL (ZAC II DRABINKI)

STOJĄCY, UKŁAD PIONOWY, PODZIAŁ NA NIEREGULARNE PASY I WYRÓWNIANY DO OKIEN

CIEMNOSZARYM NR 23 (RAL 7022)

[illegible]

GARAŻAMI ZAMKNIĘTYMI, WŁĄCZANYMI ORAZ 14 GARAŻY ZAMKNIĘTYCH, WOLNOSTOJĄCYCH
ZAGOSPODAROWANIEM TERENU, SCHODAMI ZEWNĘTRZNYMI, MURAMI OGRÓWYMI, ZEWNĘTRZ-
NYMI KŁADKAMI, DOSTĘP WYCHODZĄCY DO KUCHNI I DO KUCHNI

RZUTY BUDYNKOW: B13,C13,B14,C14

DATA I PŘEZVJKA	SKALA
-----------------	-------