
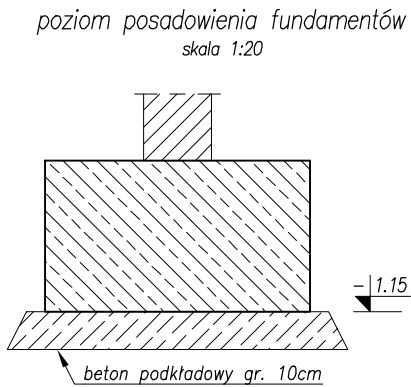
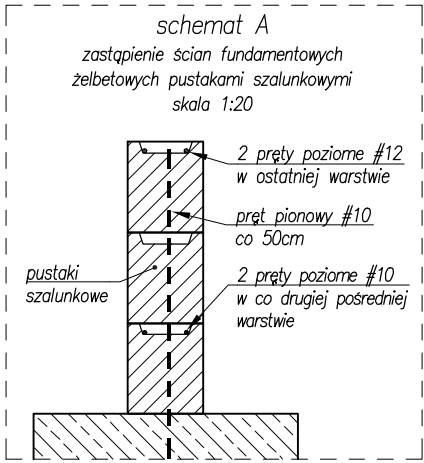


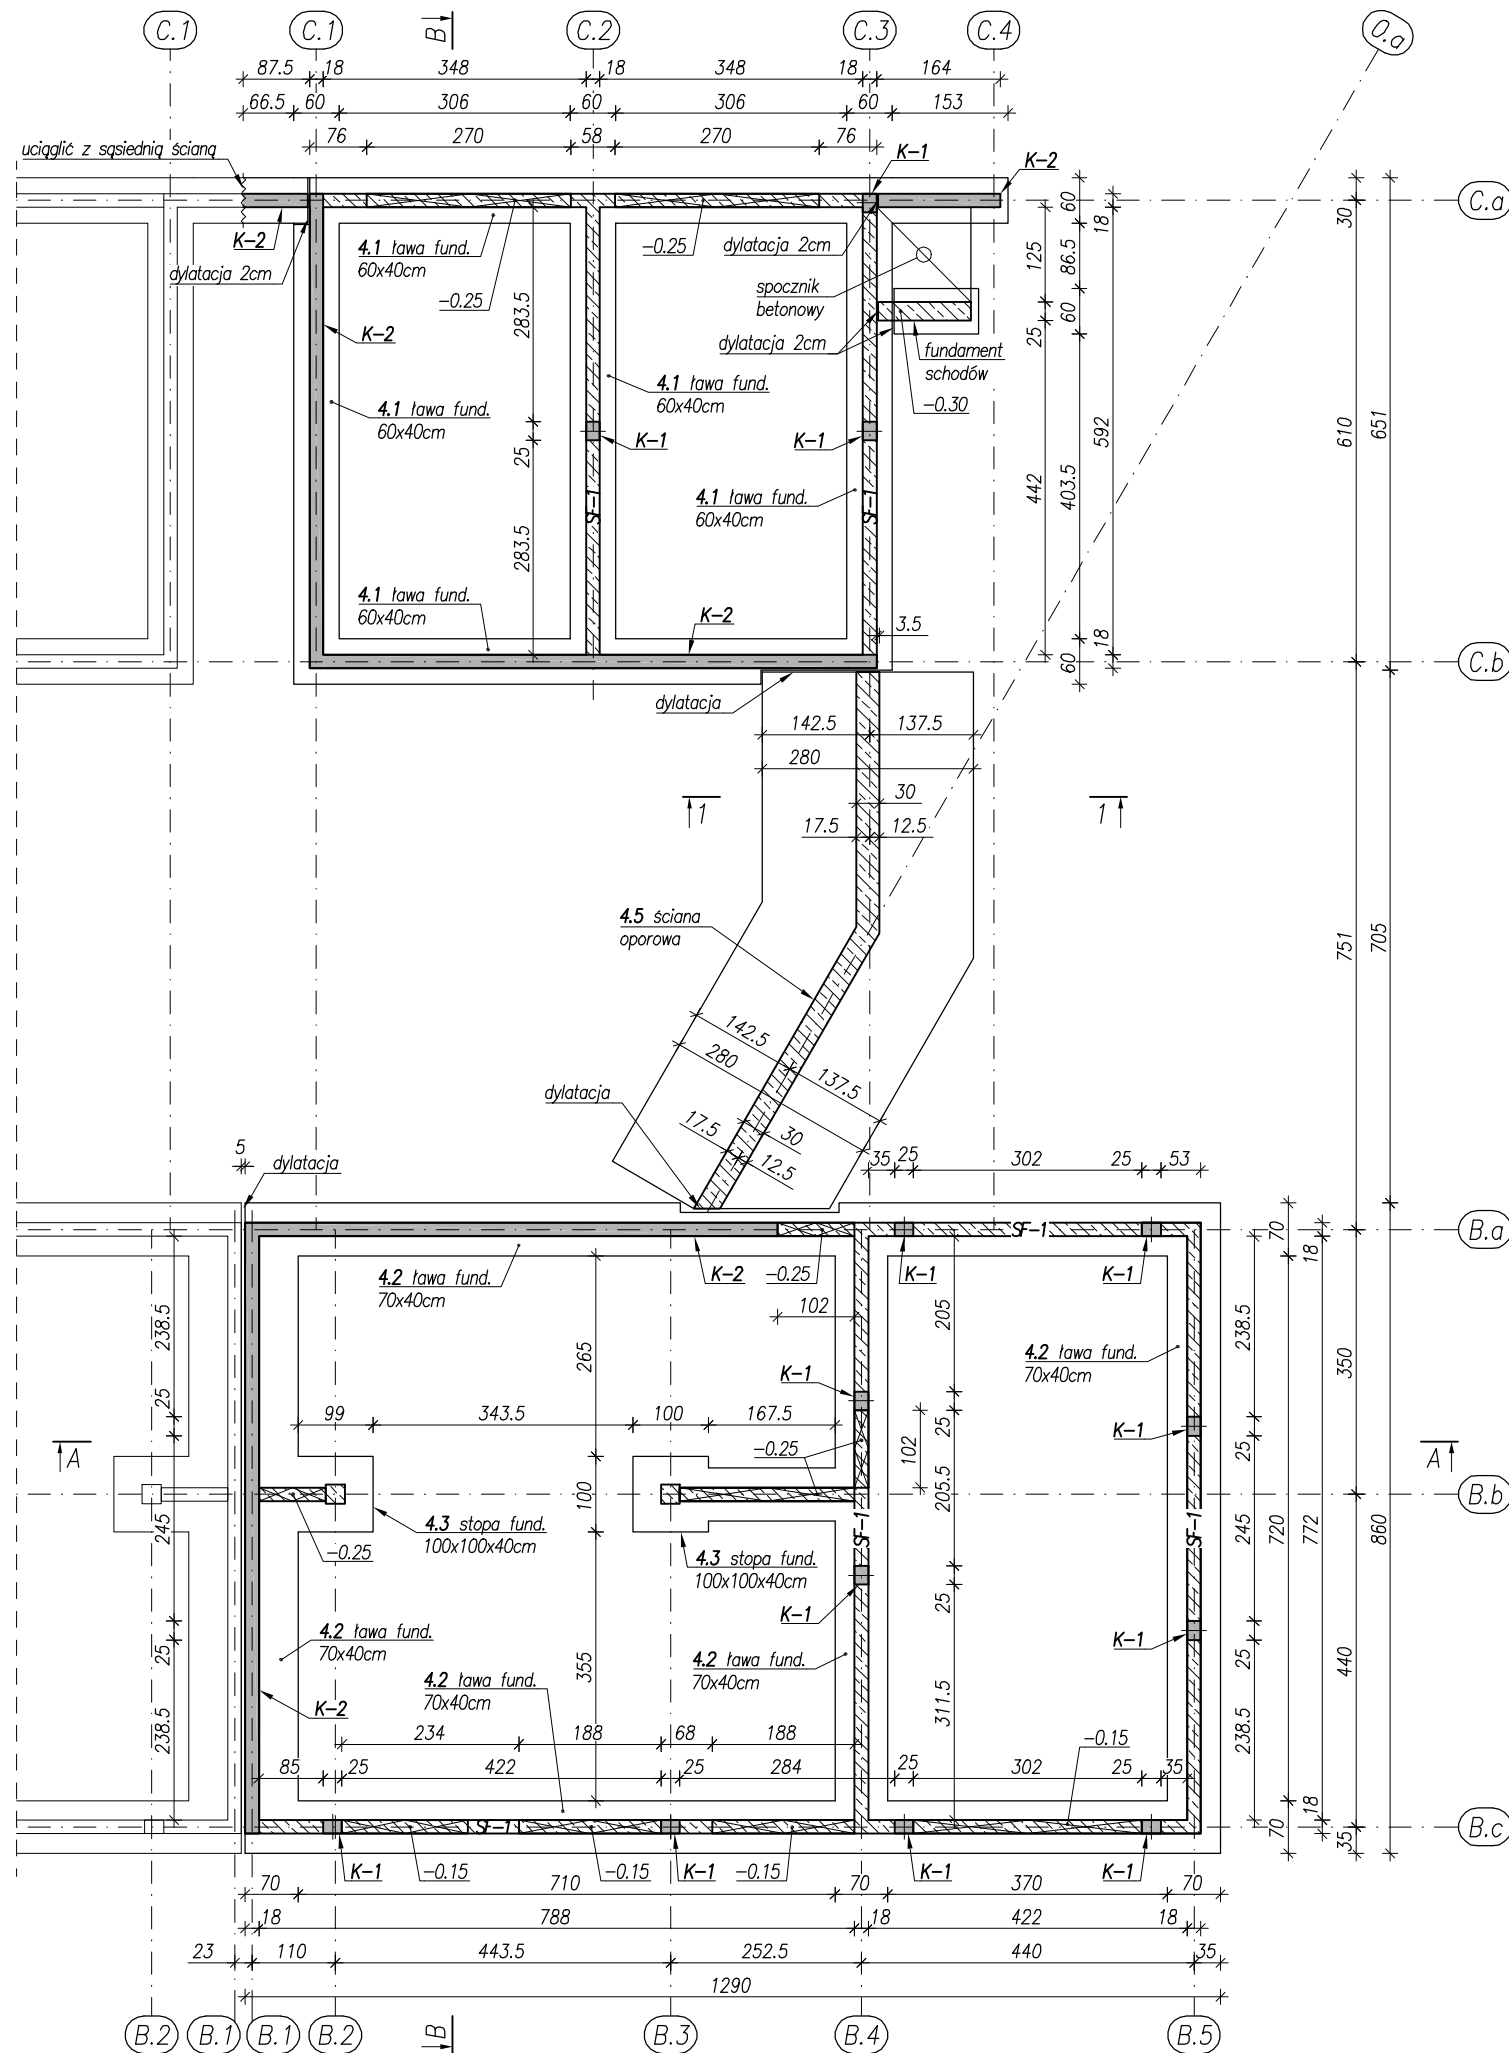

OZNACZENIA:

	wykotwienia elementów żelbetowych
	elementy żelbetowe
	ściany murowane
	obniżenia ścian

BETON:	
ławy:	C20/25
pozostałe:	C25/30
STAL:	A-IIIIN RB500W
	A-0 St0S
OTULINA:	25mm
	spód fund: 50mm

UWAGI:

- Wymiary podano w [cm], poziomy w [m].
- Rozpatrywać łącznie z pozostałymi rysunkami konstrukcyjnymi kondygnacji.
- Beton podkładowy C8/10.
- Dopuszcza się zastąpienie ścian fundamentowych żelbetowych ścianami z pustaka szalunkowego (zalewowego) zgodnie ze schematem A oraz wytycznymi zamieszczonymi w opisie technicznym. Beton wypełniający C20/25. W miejscach ścian oporowych, rdzeni, słupów i ścian żelbetowych wykonać pełnowymiarowy element żelbetowy.

c	dodano schemat A oraz zapis w uwagach zmieniono klasę betonu ław fundamentowych	13.09.2023	M.Raducki
b	zmierzono poziom góry ścian fundamentowych dodano opisy obniżen wraz z pozycją legendy	09.08.2023	M.Raducki
a	zmiana gabarytu ściany oporowej 4.5 zmiana fundamentu w osi B.1	05.07.2023	M.Raducki
Rewizja	Opis	Data	Nazwisko

±0.00 = 225.50m n.p.m.

Inwestor	DZMT KROWDRZA SP. Z O. O., ul. Kołetek 4/2, 31-069 Kraków			
Inwestycja	BUDOWA 28 BUDYNKÓW MIESZKALNYCH JEDNORODZINNYCH W ZABUDOWIE BLIŹNIACZEJ Z 14 GARAŻAMI ZAMKNIĘTYMI, WBUDOWANYMI ORAZ 14 GARAŻY ZAMKNIĘTYCH, WOLNOSTOJĄCYCH, Z ZAGOSPODAROWANIEM TERENU, SCHODAMI ZEWNĘTRZNYMI, MURAMI OPOROWYMI, ZEWNĘTRZNYMI STANOWISKAMI POSTOJOWYMI, DOJŚCIEM I DOJAZDEM.			
Adres	Kraków 126102_9, obr. Krowdrza 0033, 773, 774, 775			
Zakres	BUDYNEK B1, C1			
Treść rysunku	RZUT FUNDAMENTÓW			
Projektant	mgr inż. Łukasz Sekuła Upr. SWK/POOK/0027/12		Podpis	
Faza	Skala	Branża	Nr rysunku	Data
PW	1:100	KONSTR.	K-01c	04.2023