


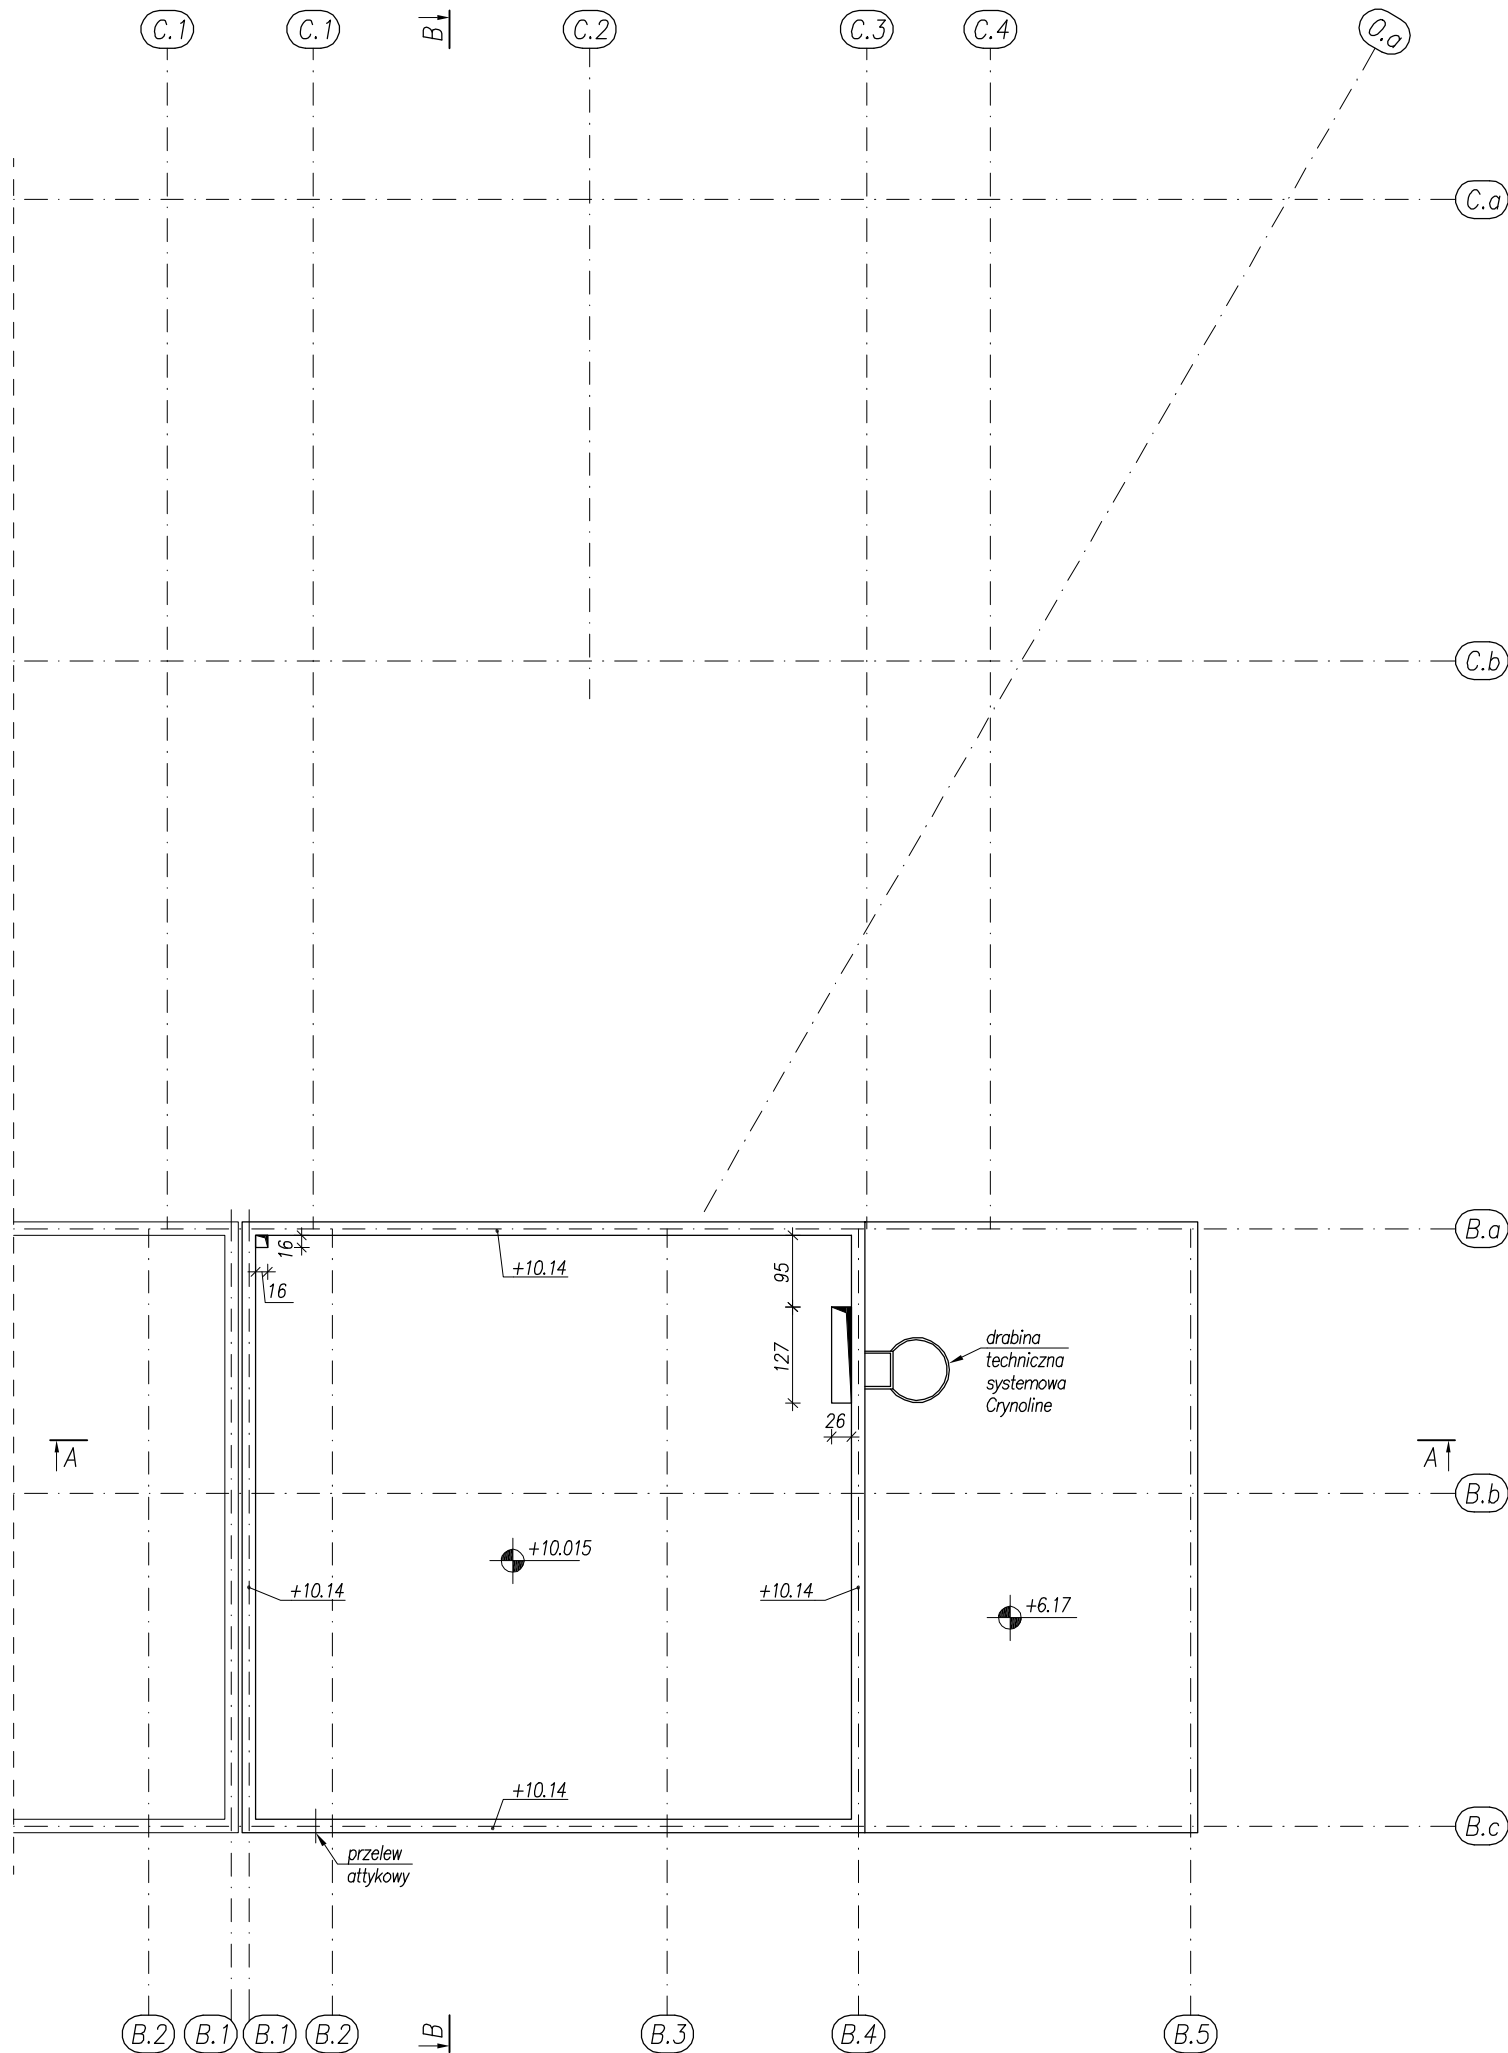

OZNACZENIA:

wykotwienia elementów żelbetowych

elementy żelbetowe

ściany murowane

belki

LEGENDA:

GB – góra betonu konstrukcyjnego
SB – spód betonu konstrukcyjnego

BETON: C25/30
STAL: A-IIIIN RB500W
A-O St0S
OTULINA: 25mm

UWAGI:

- Wymiary podano w [cm], poziomy w [m].
- Rozpatrywać łącznie z pozostałymi rysunkami konstrukcyjnymi kondygnacji.

a	dodano otwór strapy	13.10.2023	M.Raducki
Rewizja	Opis	Data	Nazwisko

±0.00 = 225.50m n.p.m.

Inwestor	DZMT KROWDRZA SP. Z O. O., ul. Kołetek 4/2, 31-069 Kraków		
Inwestycja	BUDOWA 28 BUDYNKÓW MIESZKALNYCH JEDNORODZINNYCH W ZABUDOWIE BLIŹNIACZEJ Z 14 GARAŻAMI ZAMKNIĘTYMI, WBUDOWANYMI ORAZ 14 GARAŻY ZAMKNIĘTYCH, WOLNOSTOJĄCYCH, Z ZAGOSPODAROWANIEM TERENU, SCHODAMI ZEWNĘTRZNYMI, MURAMI OPOROWYMI, ZEWNĘTRZNYMI STANOWISKAMI POSTOJOWYMI, DOJŚCIEM I DOJAZDEM.		
Adres	Kraków 126102_9, obr. Krowdrza 0033, 773, 774, 775		
Zakres	BUDYNEK B1, C1		
Treść rysunku	RZUT DACHU		
Projektant	mgr inż. Łukasz Sekuła Upr. SWK/POOK/0027/12		Podpis
Faza	Skala	Branża	Nr rysunku
PW	1:100	KONSTR.	K-05a
			Data
			04.2023