




W-1 wieniec
skala 1:20

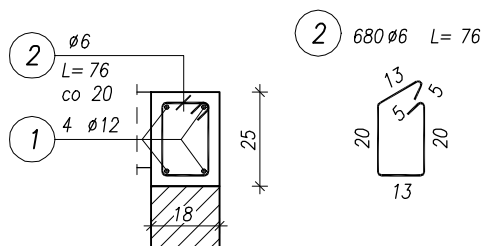

W-2 wieniec
skala 1:20

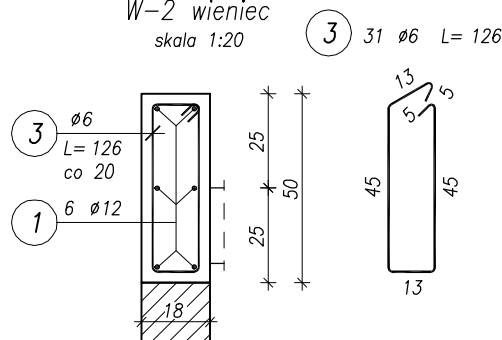

W-S wykotwienia słupów
skala 1:20

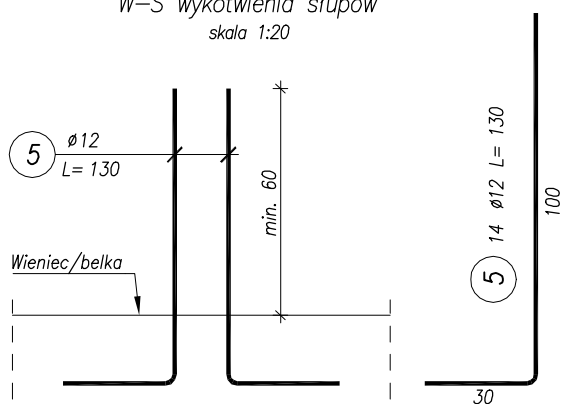

uwaga:

– rozstaw i ilość wykotwień dopasować do prętów pionowych słupa

ZESTAWIENIE STALI ZBROJENIOWEJ

Nr pręta	ø	Długość [cm]	Ilość [szt.]	Ilość pozycji	Dł. ogólna [m]	
					A-0	A-IIIIN
	[mm]				ø6	#12
Poz.: W-1 wieniec						
1	12	1200	71	1		852,00
2	6	76	680	1	516,80	
Poz.: W-2 wieniec						
1	12	1200	4	1		48,00
4	6	126	31	1	39,06	
Poz.: W-S wykotwienia słupów						
5	12	130	14	1		18,20
Długość razem:				[m]	555,86	918,20
Masa jednostkowa:				[kg/m]	0,222	0,888
Masa razem:				[kg]	123,4	815,4
Masa ogólna:				[kg]	938,8	


BETON: C25/30
STAL: A-IIIIN RB500W
A-0 St0S
OTULINA: 25mm

UWAGI:

- Wymiary podano w [cm], poziomy w [m].
- Rozpatrywać łącznie z pozostałymi rysunkami konstrukcyjnymi kondygnacji.
- Zmniejszyć wysokość wienca w miejscach przejść instalacyjnych. Nad otworem dołożyć pręty zbrojeniowe zgodnie z przekrojem.

a	zmieniono wieniec W-2	31.10.2023	M.Raducki
Rewizja	Opis	Data	Nazwisko

$\pm 0.00 = 225.50m$ n.p.m.

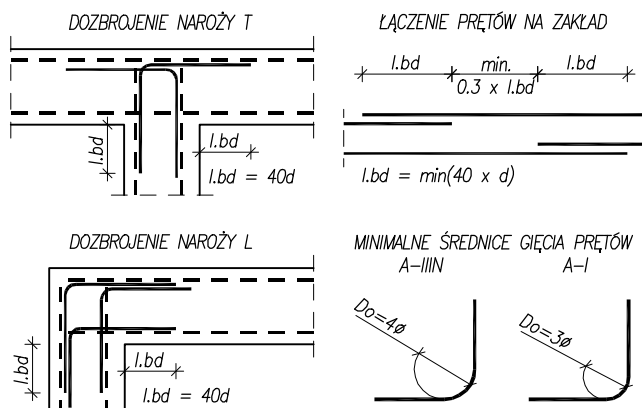

Inwestor	DZMT KROWODRZA SP. Z O. O., ul. Koletek 4/2, 31-069 Kraków		
Inwestycja	BUDOWA 28 BUDYNKÓW MIESZKALNYCH JEDNORODZINNYCH W ZABUDOWIE BLIŹNIACZEJ Z 14 GARAŻAMI ZAMKNIĘTYMI, WBUDOWANYMI ORAZ 14 GARAŻY ZAMKNIĘTYCH, WOLNOSTOJĄCYCH, Z ZAGOSPODAROWANIEM TERENU, SCHODAMI ZEWNĘTRZNYMI, MURAMI OPOROWYMI, ZEWNĘTRZNYMI STANOWISKAMI POSTOJOWYMI, DOJŚCIEM I DOJAZDEM.		
Adres	Kraków 126102_9, obr. Krowodrza 0033, 773, 774, 775		
Zakres	BUDYNEK B1, C1		
Treść rysunku	ELEMENTY OGÓLNE		
Projektant	mgr inż. Łukasz Sekuła Upr. SWK/POOK/0027/12		Podpis
Faza	Skala	Branża	Nr rysunku
PW	1:50	KONSTR.	K-07a
			Data
			04.2023