



4.3 Stopa fundamentowa (szt. 2)
skala 1:20

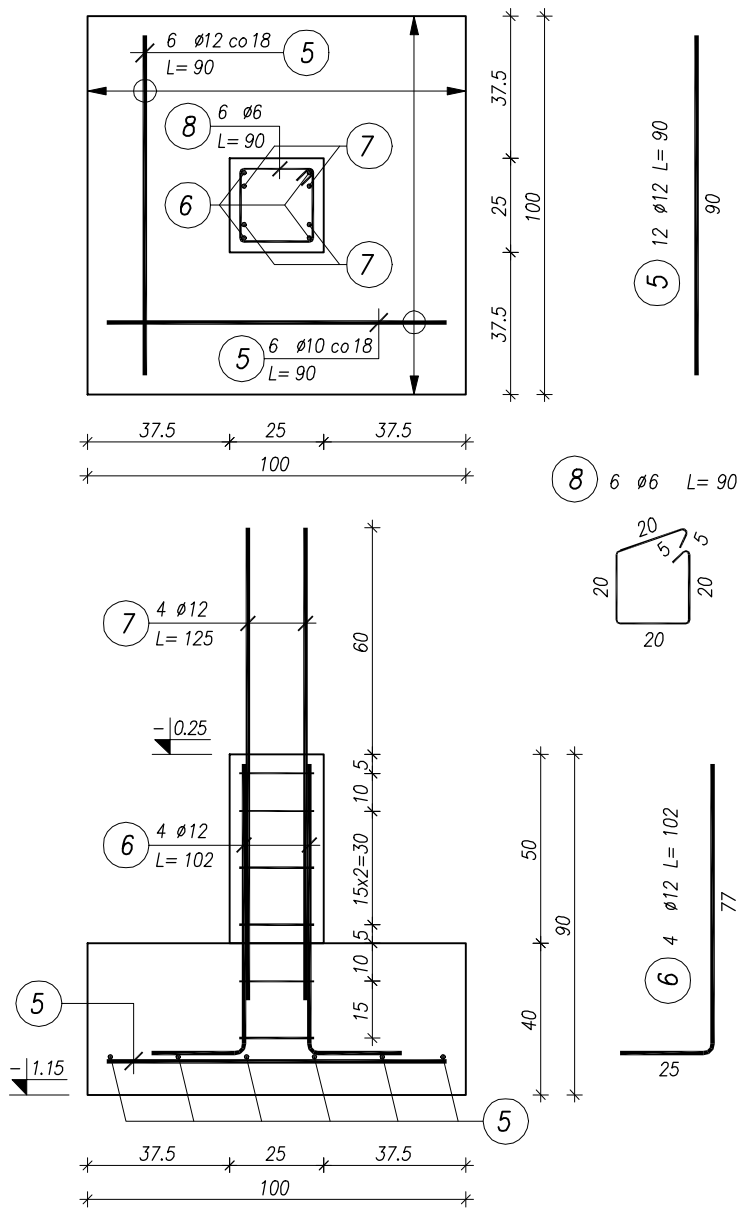


SF-1 ściana fundamentowa
skala 1:25

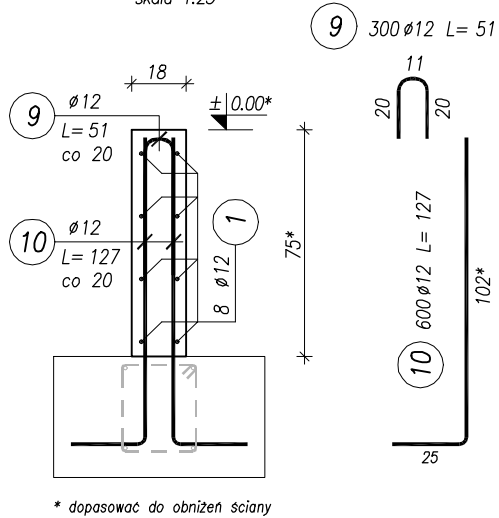


* dopasować do obniżen ściany

K-1 wykotwienie rdzeni
skala 1:25

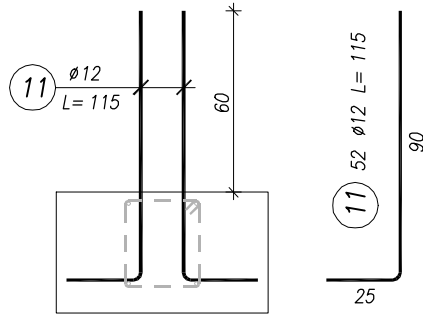


rozstaw prętów dopasować do rdzeni


4.1 ława fundamentowa
skala 1:25

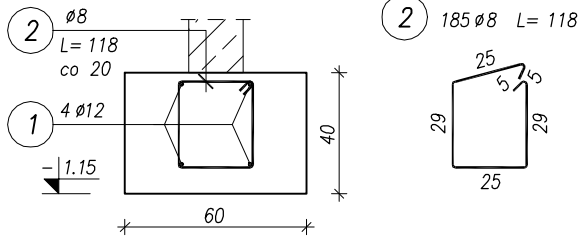

4.2 ława fundamentowa
skala 1:25

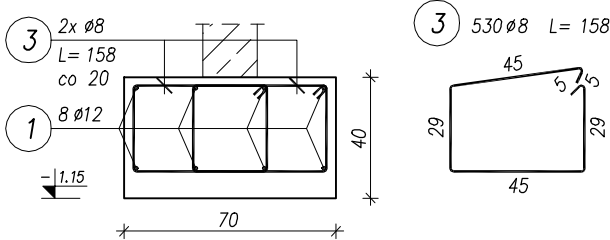

K-2 wykotwienie ścian
skala 1:25




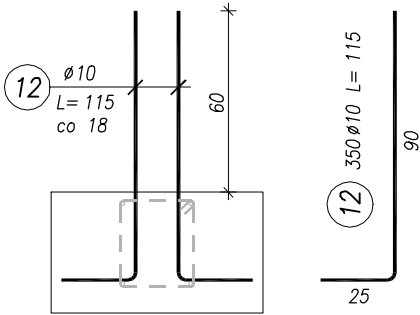


rozstaw prętów dopasować do ścian

ZESTAWIENIE STALI ZBROJENIOWEJ								
Nr pręta	ø	Długość	Ilość	Ilość pozycji	Dł. ogólna [m]			
					A-0		A-IIIIN	
	[mm]	[cm]	[szt.]	[szt.]	ø6	ø8	#10	#12
Poz.:	4.1 ława fundamentowa							
1	12	1200	13	1				156,00
2	8	118	185	1		218,30		
Poz.:	4.2 ława fundamentowa							
1	12	1200	36	1				432,00
3	8	158	530	1		837,40		
Poz.:	4.3 stopa fundamentowa							
5	12	90	12	2				21,60
6	12	102	4	2				8,16
7	12	125	4	2				10,00
8	6	90	6	2	10,80			
Poz.:	SF-1 ściana fundamentowa							
1	12	1200	42	1				504,00
9	12	51	300	1				153,00
10	12	127	600	1				762,00
Poz.:	K-1 wykolwienie rdzeni							
11	12	115	52	1				59,80
Poz.:	K-2 wykolwienie ścian							
12	10	115	350	1			402,50	
Długość razem:				[m]	10,80	1055,70	402,50	2106,56
Masa jednostkowa:				[kg/m]	0,222	0,395	0,617	0,888
Masa razem:				[kg]	2,4	417,0	248,3	1870,6
Masa ogólna:				[kg]	2538,4			

BETON:
ławy: C20/25
pozostałe: C25/30
STAL: A-IIIIN RB500W
A-0 StOS
OTULINA: 25mm
spód fund: 50mm

- UWAGI:
- Wymiary podano w [cm], poziomy w [m].
 - Rozpatrywać łącznie z pozostałymi rysunkami konstrukcyjnymi kondygnacji.

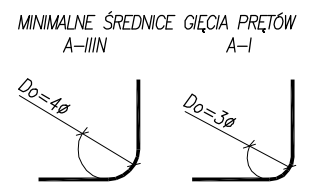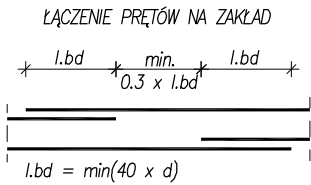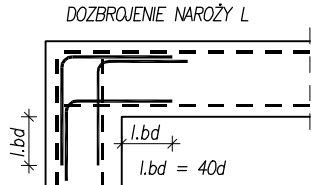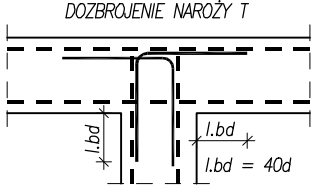

c	zmieniono klasę betonu ław fundamentowych	13.09.2023	M.Raducki
b	zmieniono wysokość poz. SF-1	09.08.2023	M.Raducki
a	usunięto ławę 4.3 oraz zmieniono kolejność pozycji	05.07.2023	M.Raducki
Rewizja	Opis	Data	Nazwisko

±0.00 = 225.50m n.p.m.

Inwestor	DZMT KROWODRZA SP. Z O. O., ul. Kołetek 4/2, 31-069 Kraków			
Inwestycja	BUDOWA 28 BUDYNKÓW MIESZKALNYCH JEDNORODZINNYCH W ZABUDOWIE BLIŹNIACZEJ Z 14 GARAŻAMI ZAMKNIĘTYMI, WBUDOWANYMI ORAZ 14 GARAŻY ZAMKNIĘTYCH, WOLNOSTOJĄCYCH, Z ZAGOSPODAROWANIEM TERENU, SCHODAMI ZEWNĘTRZNYMI, MURAMI OPOROWYMI, ZEWNĘTRZNYMI STANOWISKAMI POSTOJOWYMI, DOJŚCIEM I DOJAZDEM.			
Adres	Kraków 126102_9, obr. Krowodrza 0033, 773, 774, 775			
Zakres	BUDYNEK B1, C1			
Treść rysunku	FUNDAMENTY			
Projektant	mgr inż. Łukasz Sekuła Upr. SWK/POOK/0027/12		Podpis	
Faza	Skala	Branża	Nr rysunku	Data
PW	1:20	KONSTR.	K-08c	04.2023