
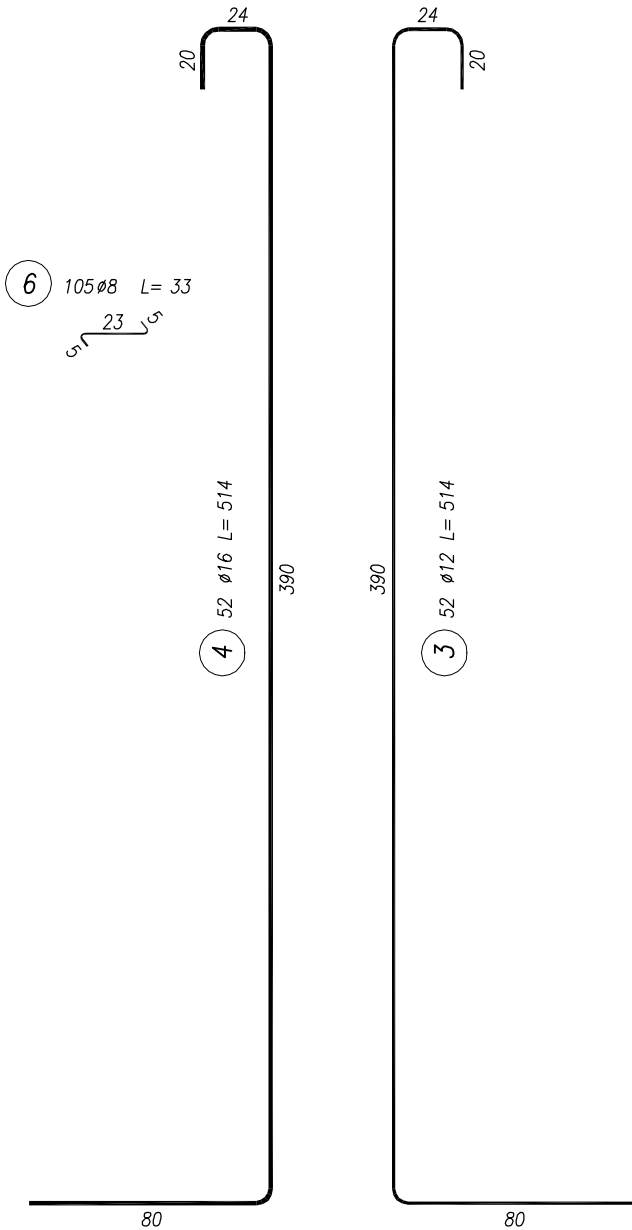


4.5 ściana oporowa
skala 1:25

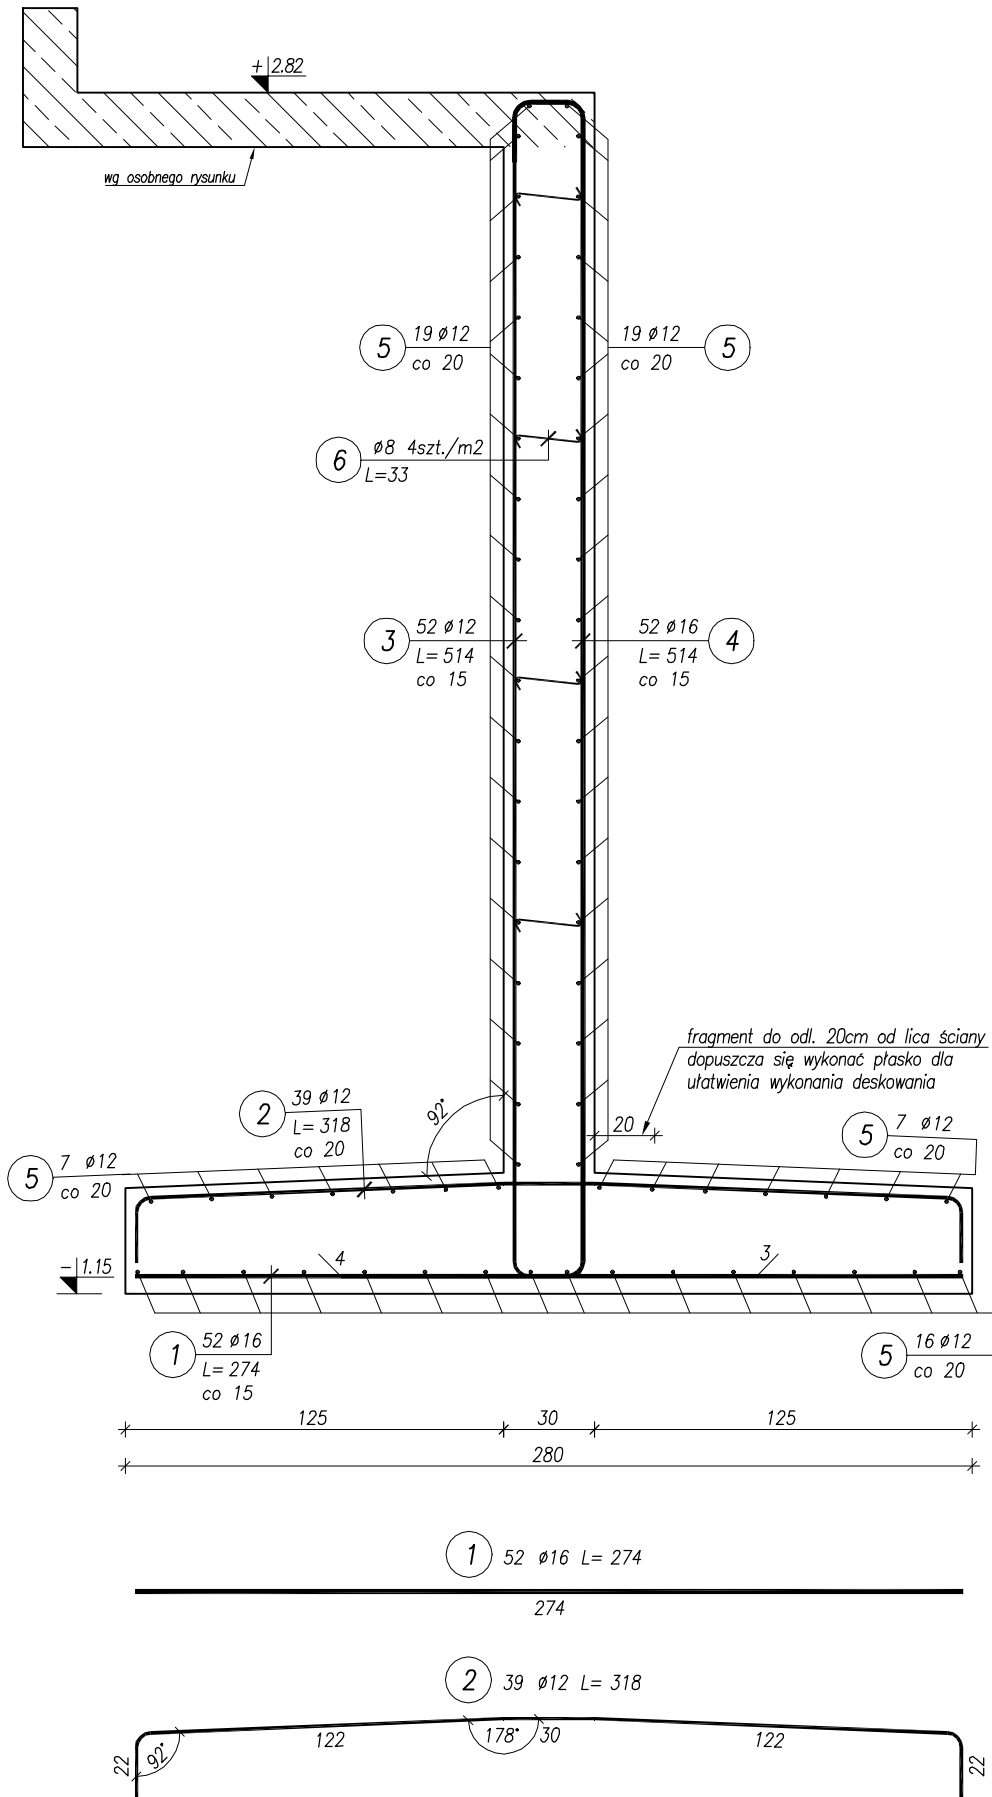

ZESTAWIENIE STALI ZBROJENIOWEJ							
Nr pręta	o	Długość	Ilość	Ilość pozycji	Dł. ogólna [m]		
					A-0	A-IIIIN	
	[mm]	[cm]	[szt.]	[szt.]	ø8	#12	#16
Poz.:	4.5 ściana oporowa						
1	16	274	52	1			142,48
2	12	318	39	1		124,02	
3	12	514	52	1		267,28	
4	16	514	52	1			267,28
5	12	1200	46	1		552,00	
6	8	33	105	1	34,65		
Długość razem:				[m]	34,65	943,30	409,76
Masa jednostkowa:				[kg/m]	0,395	0,888	1,578
Masa razem:				[kg]	13,7	837,7	646,6
Masa ogólna:				[kg]	1497,9		

BETON: C25/30
STAL: A-IIIIN RB500W
A-0 StOS
OTULINA: 25mm

- UWAGI:
- Wymiary podano w [cm], poziomy w [m].
 - Rozpatrywać łącznie z pozostałymi rysunkami konstrukcyjnymi kondygnacji.

a	zmiana gabarytu oraz zbrojenia poz. 4.5	05.07.2023	M.Raducki
Rewizja	Opis	Data	Nazwisko

±0.00 = 225.50m n.p.m.

Inwestor	DZMT KROWODRZA SP. Z O. O., ul. Kołetek 4/2, 31-069 Kraków		
Inwestycja	BUDOWA 28 BUDYNKÓW MIESZKALNYCH JEDNORODZINNYCH W ZABUDOWIE BLIŹNIACZEJ Z 14 GARAŻAMI ZAMKNIĘTYMI, WBUDOWANYMI ORAZ 14 GARAŻY ZAMKNIĘTYCH, WOLNOSTOJĄCYCH, Z ZAGOSPODAROWANIEM TERENU, SCHODAMI ZEWNĘTRZNYMI, MURAMI OPOROWYMI, ZEWNĘTRZNYMI STANOWISKAMI POSTOJOWYMI, DOJŚCIEM I DOJAZDEM.		
Adres	Kraków 126102_9, obr. Krowodrza 0033, 773, 774, 775		
Zakres	BUDYNEK B1, C1		
Treść rysunku	ŚCIANA OPOROWA 4.5		
Projektant	mgr inż. Łukasz Sekuła Upr. SWK/POOK/0027/12		Podpis
Faza	Skala	Branża	Nr rysunku
PW	1:25	KONSTR.	K-09a
			Data
			04.2023