
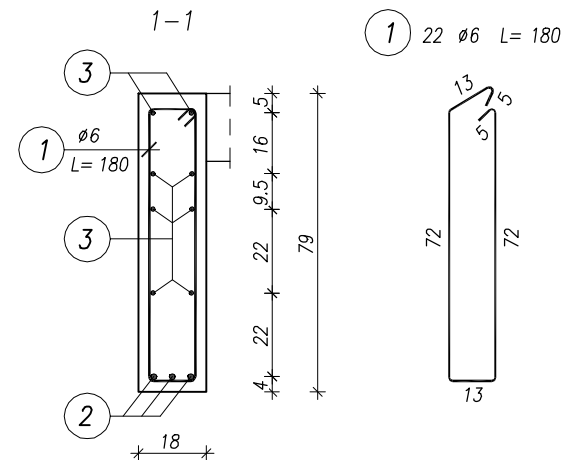
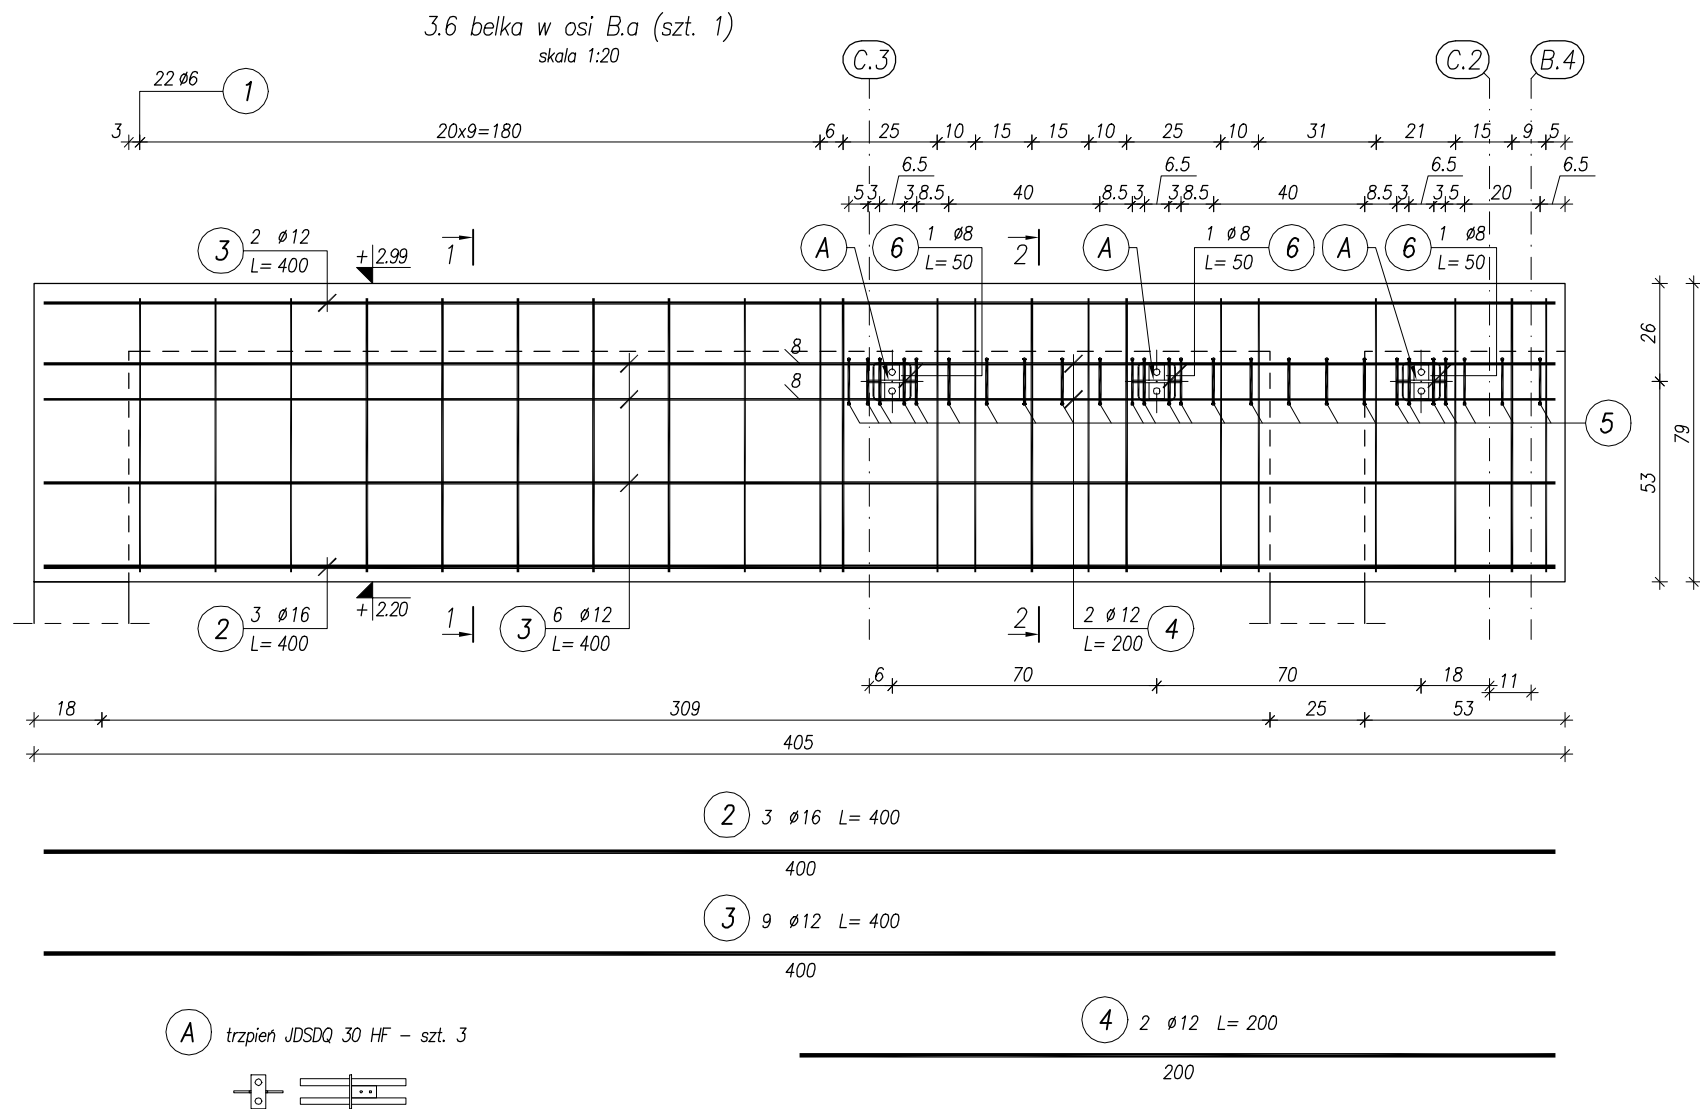


BETON: C25/30
STAL: A-IIIIN RB500W
A-0 StOS
OTULINA: 25mm

- UWAGI:
- Wymiary podano w [cm], poziomy w [m].
 - Rozpatrywać łącznie z pozostałymi rysunkami konstrukcyjnymi kondygnacji.
 - Dopuszcza się zamianę miejscami tulei posługowej z trzpieniem (montaż tulei w belce, trzpienia w płycie stropowej).

a	dodano uwagę dotyczącą trzpieni dylatacyjnych	31.10.2023	M.Raducki
Rewizja	Opis	Data	Nazwisko

±0.00 = 225.50m n.p.m.

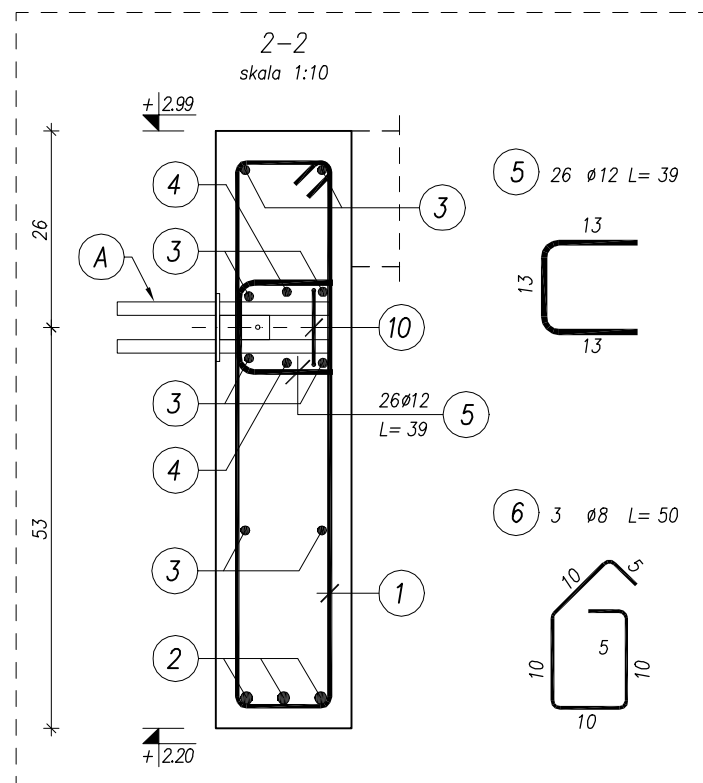

ELEMENTY DODATKOWE		
poz.	nazwa	ilość [szt.]
A	trzpień JDSDQ 30 HF	3

ZESTAWIENIE STALI ZBROJENIOWEJ								
Nr pręta	ø	Długość	Ilość	Ilość pozycji	Dł. ogólna [m]			
					A-0 ø6	A-IIIIN #8	A-IIIIN #12	A-IIIIN #16
	[mm]	[cm]	[szt.]	[szt.]				
Poz.: 3.6 belka w osi B.a								
1	6	180	22	1	39,60			
2	16	400	3	1				12,00
3	12	400	9	1			36,00	
4	12	200	2	1			4,00	
5	12	39	26	1			10,14	
6	8	50	3	1		1,50		
Długość razem:					[m]	39,60	1,50	50,14
Masa jednostkowa:					[kg/m]	0,222	0,395	0,888
Masa razem:					[kg]	8,8	0,6	44,5
Masa ogólna:					[kg]	72,8		

Inwestor	DZMT KROWODRZA SP. Z O. O., ul. Koletek 4/2, 31-069 Kraków		
Inwestycja	BUDOWA 28 BUDYNKÓW MIESZKALNYCH JEDNORODZINNYCH W ZABUDOWIE BLIŹNIACZEJ Z 14 GARAZAMI ZAMKNIĘTYMI, WBUDOWANYMI ORAZ 14 GARAZAMI ZAMKNIĘTYCH, WOLNOSTOJĄCYCH, Z ZAGOSPODAROWANIEM TERENU, SCHODAMI ZEWNĘTRZNYMI, MURAMI OPOROWYMI, ZEWNĘTRZNYMI STANOWISKAMI POSTOJOWYMI, DOJŚCIEM I DOJAZDEM.		
Adres	Kraków 126102_9, obr. Krowodrza 0033, 773, 774, 775		
Zakres	BUDYNEK B1, C1		
Treść rysunku	BELKI 3.6		
Projektant	mgr inż. Łukasz Sekuła Upr. SWK/POOK/0027/12	Podpis	
Faza	PW	Skala	1:50
Skala	KONSTR.	Nr rysunku	K-13a
		Data	04.2023