
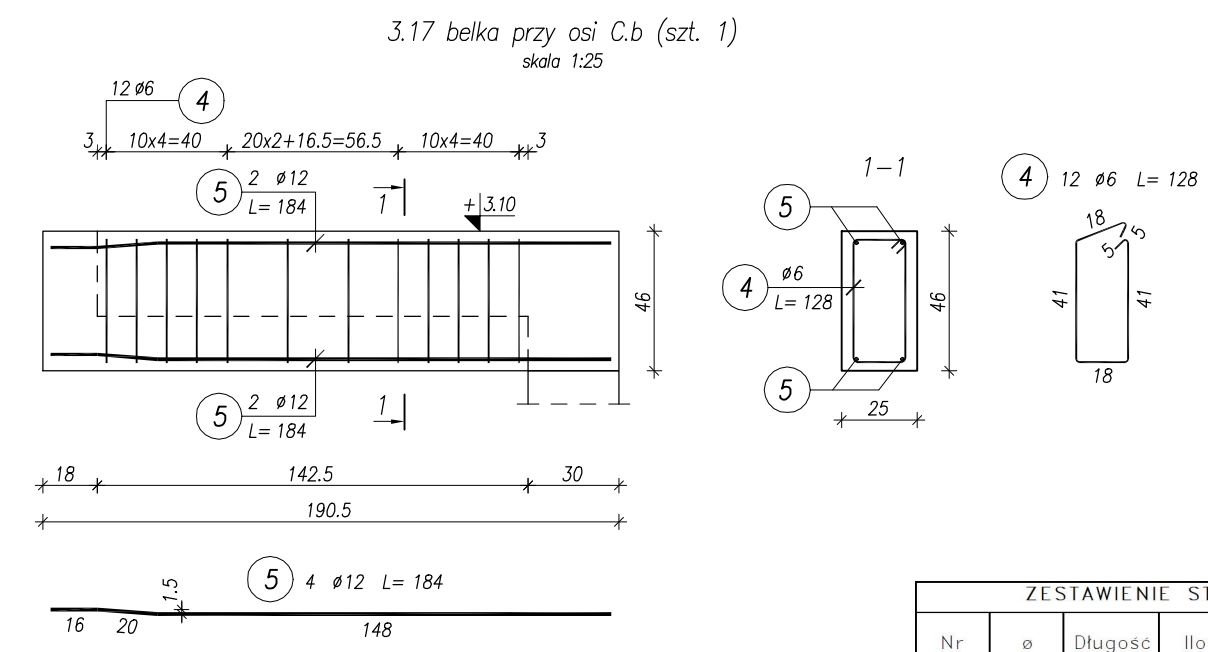


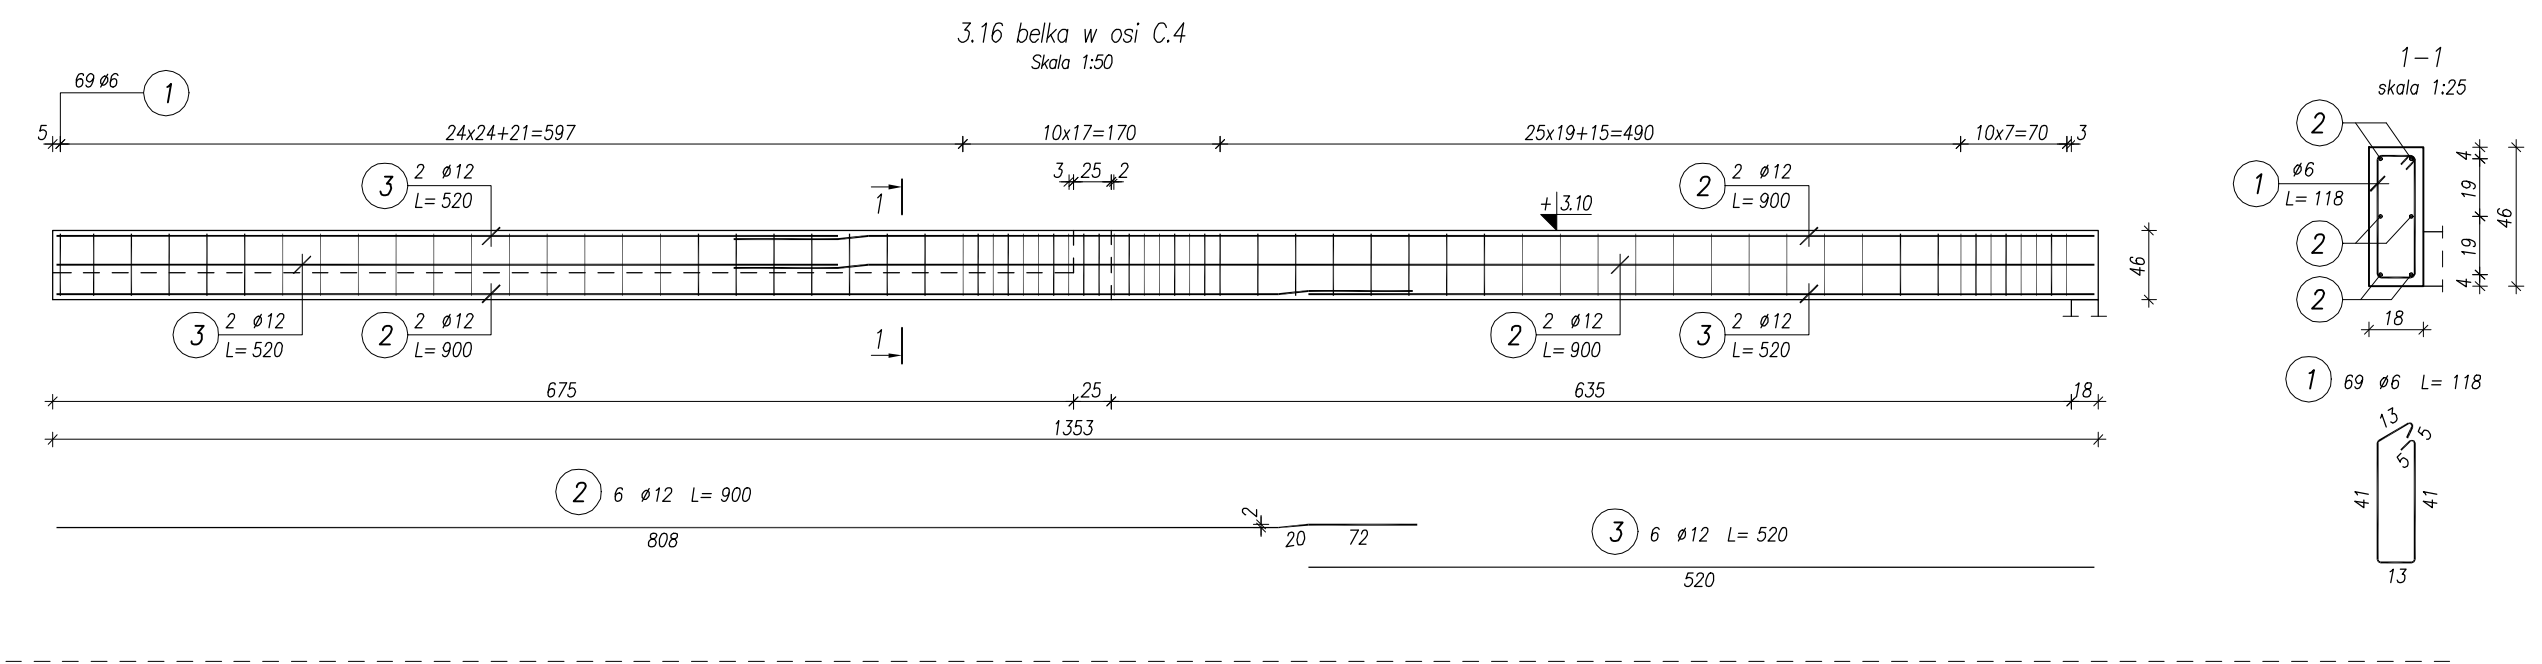

MINIMALNE ŚREDNICE GIECIA PRĘTÓW
A-IIIIN A-I

BETON: C25/30
STAŁ: A-IIIIN RB500W
A-0 StOS
OTULINA: 25mm

UWAGI:
- Wymiary podano w [cm], poziomy w [m].
- Rozpatrywać łącznie z pozostałymi rysunkami konstrukcyjnymi kondygnacji.

±0.00 = 225.50m n.p.m.

ZESTAWIENIE STALI ZBROJENIOWEJ						
Nr pręta	ø	Długość	Ilość	Ilość	Dł. ogólna [m]	
	[mm]	[cm]	[szt.]	pozycji [szt.]	A-0 ø6	A-IIIIN #12
Poz.: 3.16 belka w osi C.4						
1	6	118	69	1	81,42	
2	12	900	6	1		54,00
3	12	520	6	1		31,20
Poz.: 3.17 belka przy osi C.b						
4	6	128	12	1	15,36	
5	12	184	4	1		7,36
Długość razem:				[m]	96,78	92,56
Masa jednostkowa:				[kg/m]	0,222	0,888
Masa razem:				[kg]	21,5	82,2
Masa ogólna:				[kg]	103,7	

Inwestor DZMT KROWODRZA SP. Z O. O., ul. Kołetek 4/2, 31-069 Kraków				
Inwestycja BUDOWA 28 BUDYNKÓW MIESZKALNYCH JEDNORODZINNYCH W ZABUDOWIE BLIŹNIACZEJ Z 14 GARAŻAMI ZAMKNIĘTYMI, WBUDOWANYMI ORAZ 14 GARAŻY ZAMKNIĘTYCH, WOLNOSTOJĄCYCH, Z ZAGOSPODAROWANIEM TERENU, SCHODAMI ZEWNĘTRZNYMI, MURAMI OPOROWYMI, ZEWNĘTRZNYMI STANOWISKAMI POSTOJOWYMI, DOJŚCIEM I DOJAZDEM.				
Adres Kraków 126102_9, obr. Krowodrza 0033, 773, 774, 775				
Zakres BUDYNEK B1, C1				
Treść rysunku BELKI 3.16, 3.17				
Projektant mgr inż. Łukasz Sekuła Upr. SWK/POOK/0027/12			Podpis	
Faza PW	Skala 1:50	Branża KONSTR.	Nr rysunku K-17	Data 04.2023