


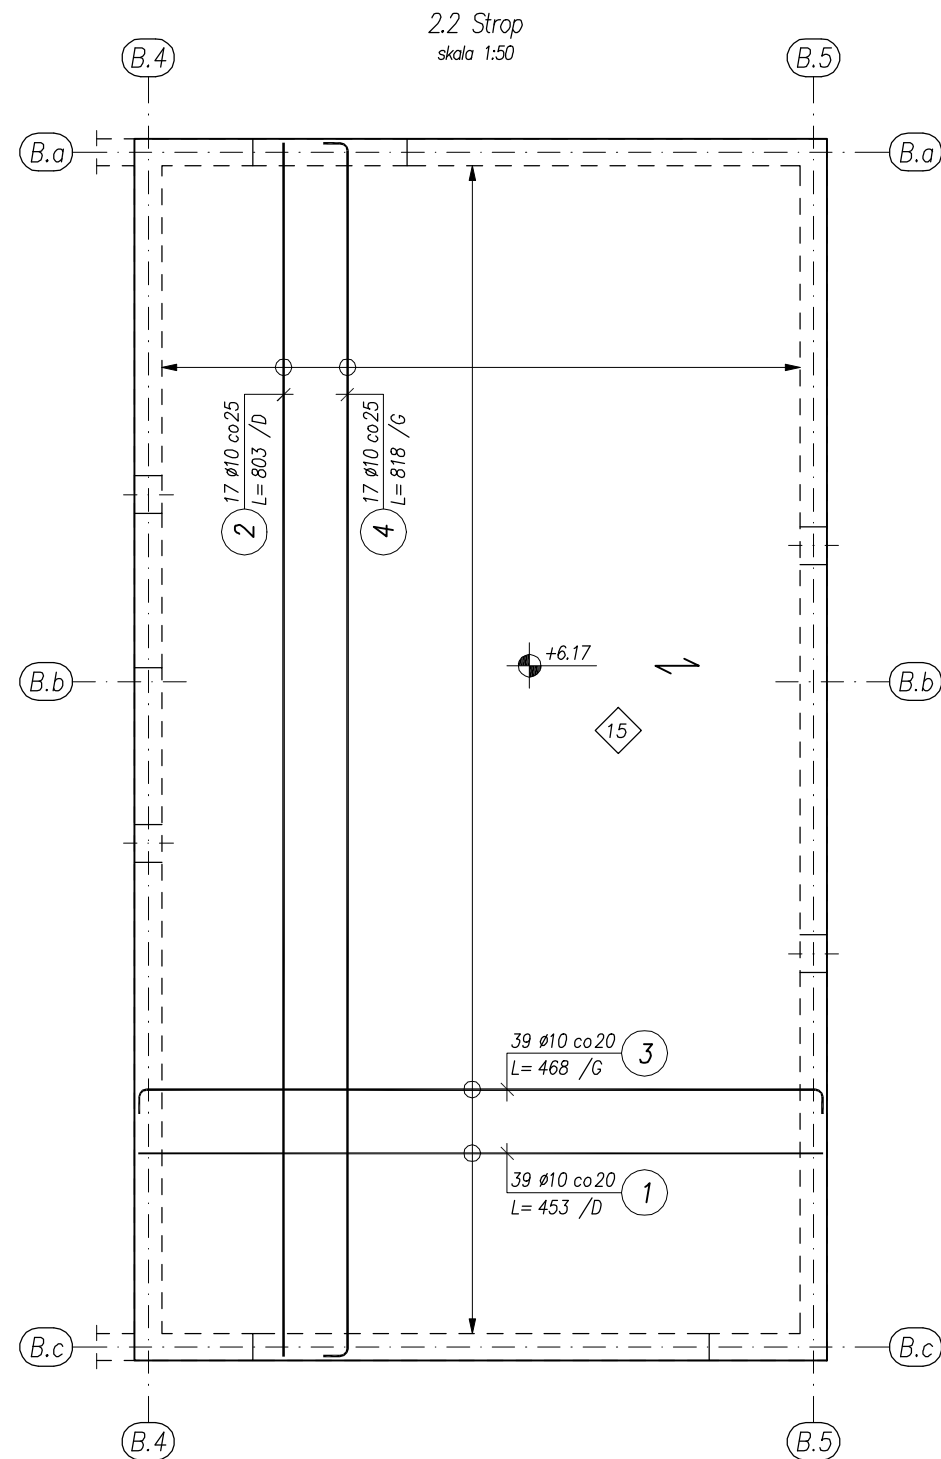

ZESTAWIENIE STALI ZBROJENIOWEJ						
Nr preta	ø	Długość	Ilość	Ilość pozycji	Dł. ogólna [m]	
	[mm]	[cm]	[szt.]	[szt.]	A-0 ø8	A-IIIIN #10
Poz.: 2.2 strop						
1	10	453	39	1		176,67
2	10	803	17	1		136,51
3	10	468	39	1		182,52
4	10	818	17	1		139,06
5	8	89	64	1	56,96	
Długość razem:				[m]	56,96	634,76
Masa jednostkowa:				[kg/m]	0,395	0,617
Masa razem:				[kg]	22,5	391,6
Masa ogólna:				[kg]	414,1	




BETON: C25/30
STAL: A-IIIIN RB500W
A-0 St0S
OTULINA: 25mm

- UWAGI:
- Wymiary podano w [cm], poziomy w [m].
 - Rozpatrywać łącznie z pozostałymi rysunkami konstrukcyjnymi kondygnacji.

±0.00 = 225.50m n.p.m.

LEGENDA:
G - pręty górne
D - pręty dolne
* - pręt dociąć przy krawędzi/otworze

OZNACZENIA:
20 grubość płyty
↑ kierunek główny zbrojenia

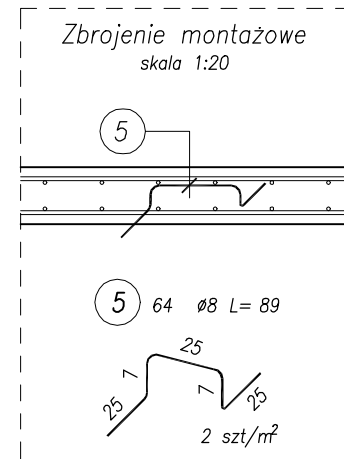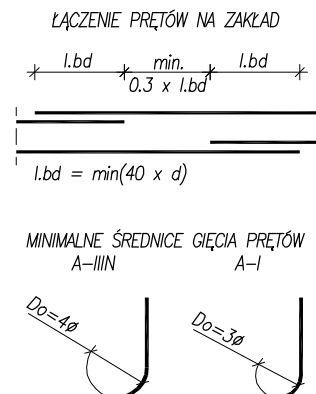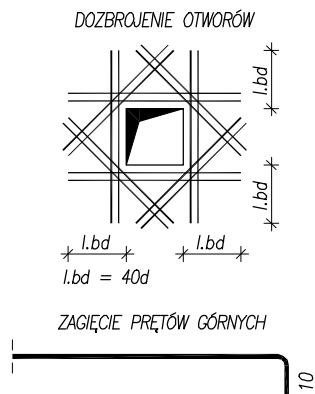

Inwestor DZMT KROWODRZA SP. Z O. O., ul. Koletek 4/2, 31-069 Kraków				
Inwestycja				
BUDOWA 28 BUDYNKÓW MIESZKALNYCH JEDNORODZINNYCH W ZABUDOWIE BLIŹNIACZEJ Z 14 GARAŻAMI ZAMKNIĘTYMI, WBUDOWANYMI ORAZ 14 GARAŻY ZAMKNIĘTYCH, WOLNOSTOJĄCYCH, Z ZAGOSPODAROWANIEM TERENU, SCHODAMI ZEWNĘTRZNYMI, MURAMI OPOROWYMI, ZEWNĘTRZNYMI STANOWISKAMI POSTOJOWYMI, DOJŚCIEM I DOJAZDEM.				
Adres Kraków 126102_9, obr. Krowodrza 0033, 773, 774, 775				
Zakres BUDYNEK B1, C1				
Treść rysunku STROP 2.2				
Projektant mgr inż. Łukasz Sekuła Upr. SWK/POOK/0027/12			Podpis	
Faza PW	Skala 1:50	Branża KONSTR.	Nr rysunku K-19	Data 04.2023