



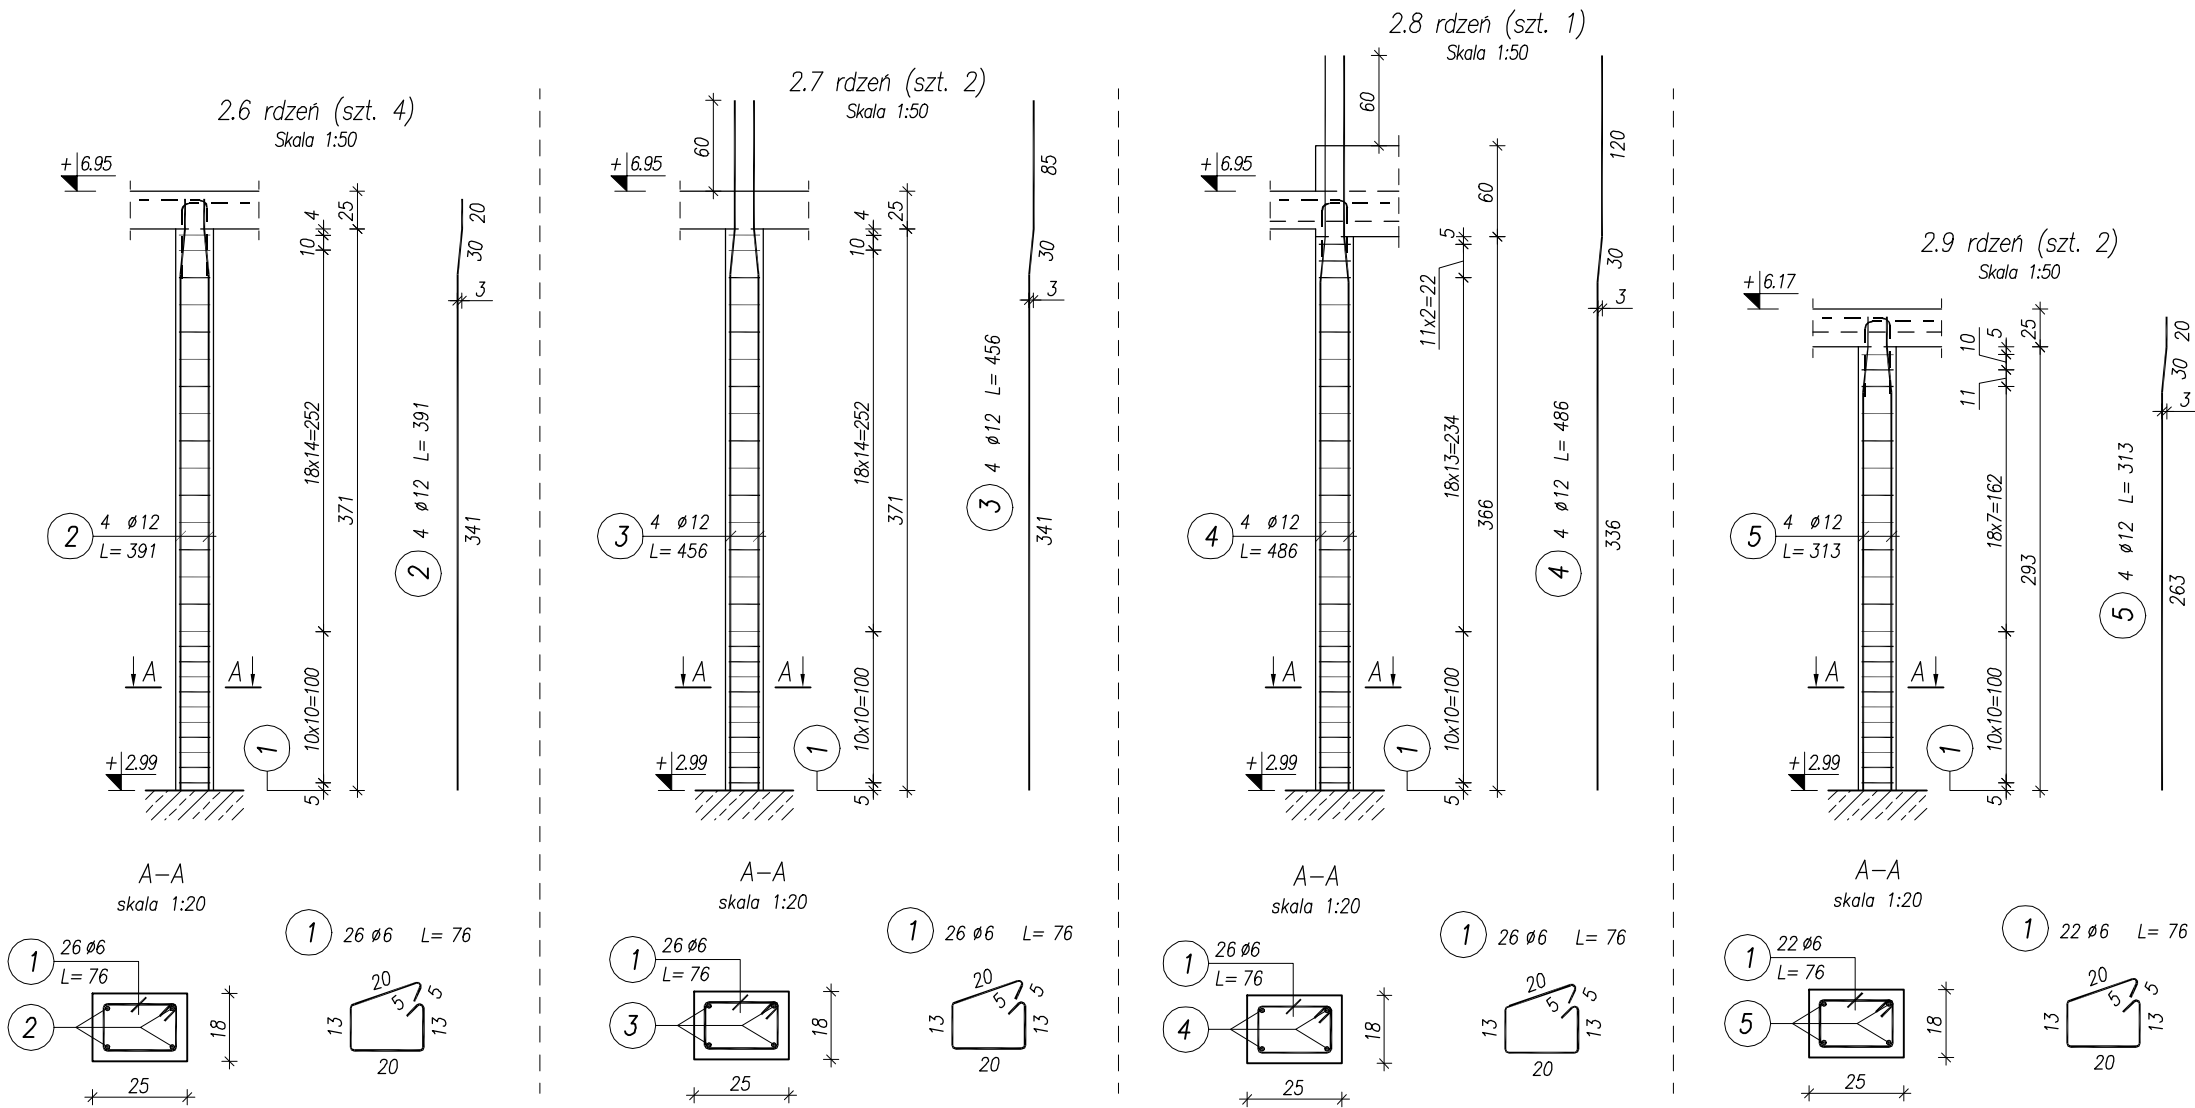

ZESTAWIENIE STALI ZBROJENIOWEJ						
Nr pręta	ø	Długość	Ilość	Ilość pozycji	Dł. ogólna [m]	
	[mm]	[cm]	[szt.]	[szt.]	A-0 ø6	A-IIIIN #12
Poz.: 2.6 rdzeń						
1	6	76	26	4	79,04	
2	12	391	4	4		62,56
6	12	130	4	4		20,80
Poz.: 2.7 rdzeń						
1	6	76	26	2	39,52	
3	12	456	4	2		36,48
Poz.: 2.8 rdzeń						
1	6	76	26	1	19,76	
4	12	486	4	1		19,44
6	12	130	4	1		5,20
Poz.: 2.9 rdzeń						
1	6	76	22	2	33,44	
5	12	313	4	2		25,04
6	12	130	4	2		10,40
Długość razem:				[m]	171,76	179,92
Masa jednostkowa:				[kg/m]	0,222	0,888
Masa razem:				[kg]	38,1	159,8
Masa ogólna:				[kg]	197,9	

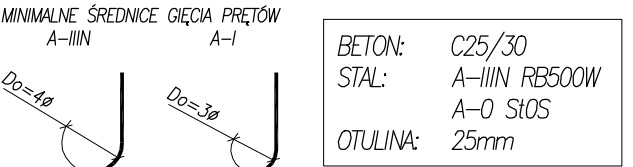

UWAGI:

- Wymiary podano w [cm], poziomy w [m].
- Rozpatrywać łącznie z pozostałymi rysunkami konstrukcyjnymi kondygnacji.

±0.00 = 225.50m n.p.m.

Inwestor	DZMT KROWODRZA SP. Z O. O., ul. Kołetek 4/2, 31-069 Kraków				
Inwestycja	BUDOWA 28 BUDYNKÓW MIESZKALNYCH JEDNORODZINNYCH W ZABUDOWIE BLIŹNIACZEJ Z 14 GARAŻAMI ZAMKNIĘTYMI, WBUDOWANYMI ORAZ 14 GARAŻY ZAMKNIĘTYCH, WOLNOSTOJĄCYCH, Z ZAGOSPODAROWANIEM TERENU, SCHODAMI ZEWNĘTRZNYMI, MURAMI OPOROWYMI, ZEWNĘTRZNYMI STANOWISKAMI POSTOJOWYMI, DOJŚCIEM I DOJAZDEM.				
Adres	Kraków 126102_9, obr. Krowodrza 0033, 773, 774, 775				
Zakres	BUDYNEK B1, C1				
Treść rysunku	SŁUPY 2.6 – 2.9				
Projektant	mgr inż. Łukasz Sekuła Upr. SWK/POOK/0027/12			Podpis	
Faza	Skala	Branża	Nr rysunku	Data	
PW	1:50	KONSTR.	K-21	04.2023	