


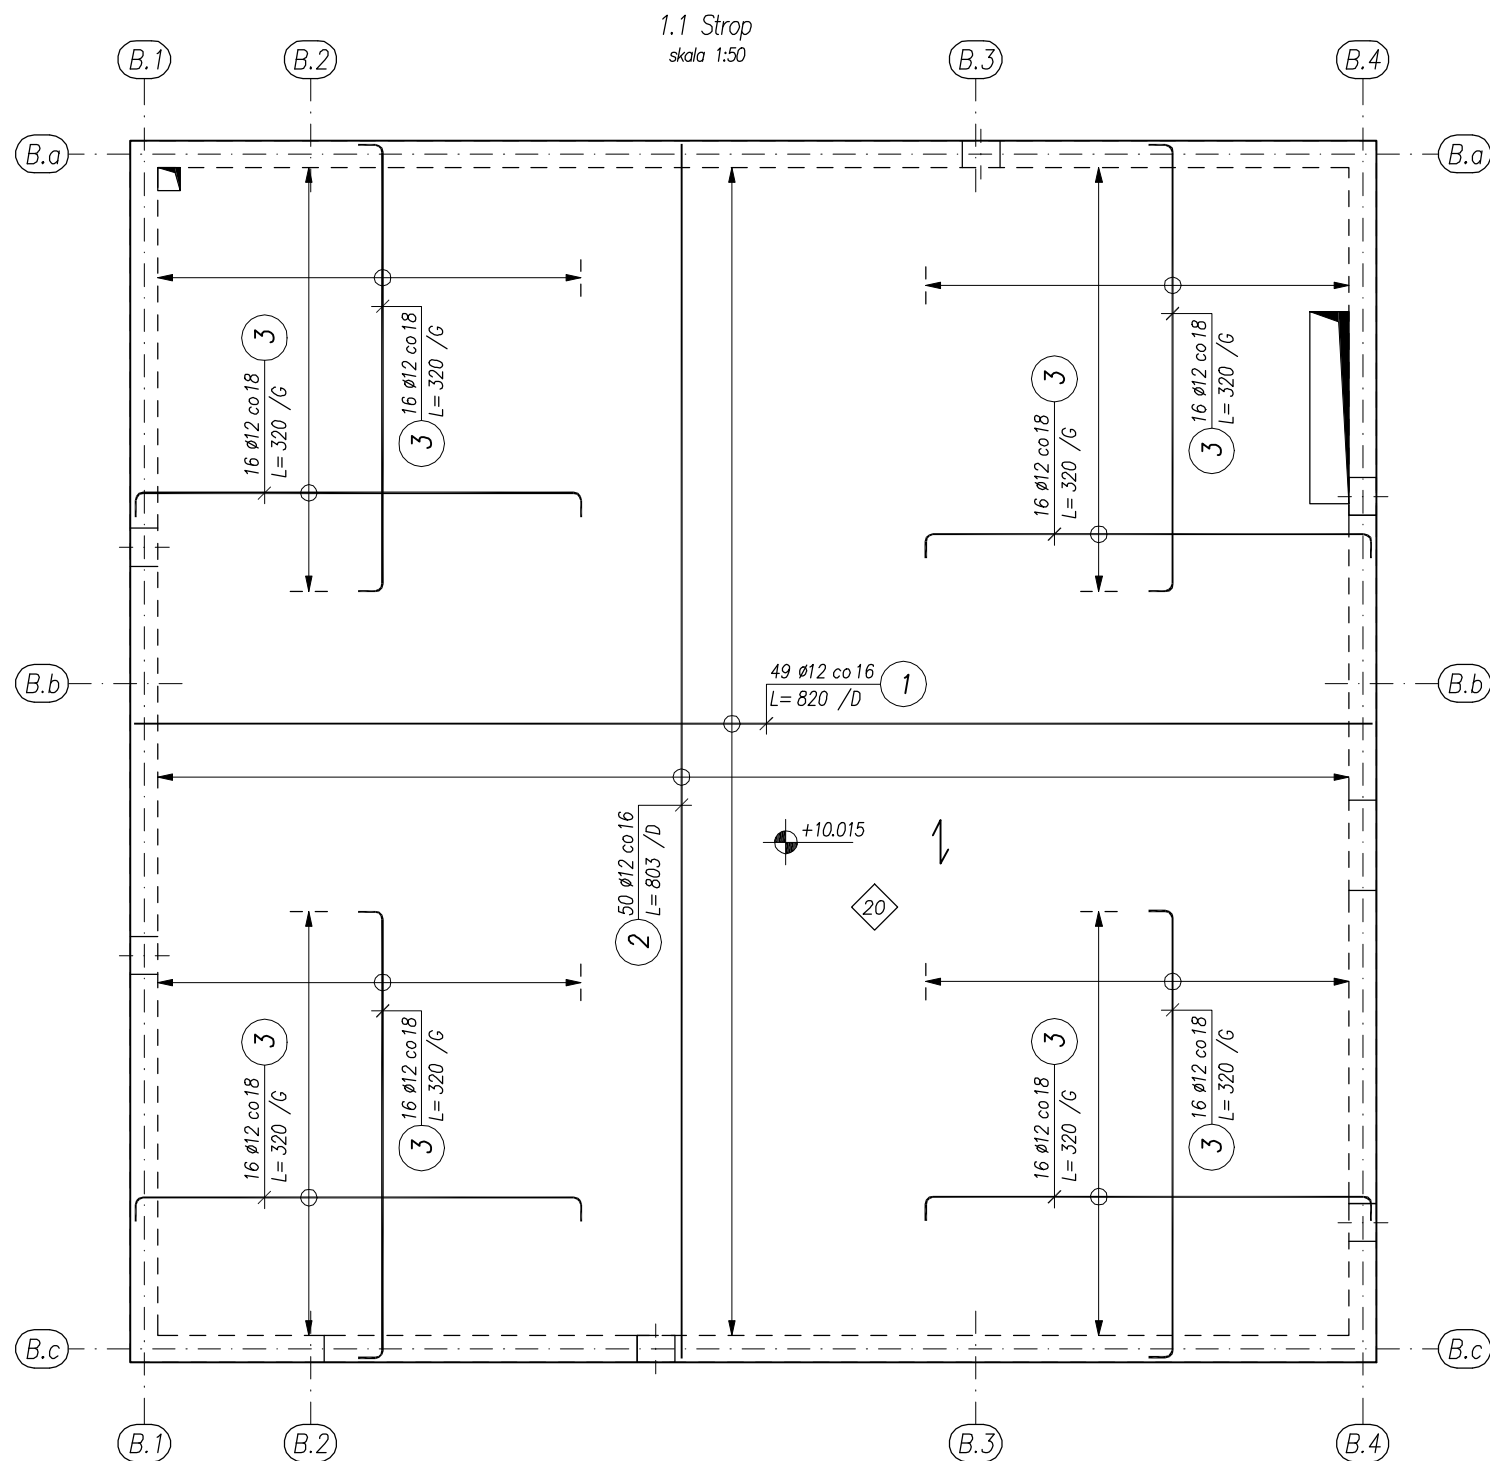

ZESTAWIENIE STALI ZBROJENIOWEJ						
Nr pręta	ø	Długość	Ilość	Ilość pozycji	Dł. ogólna [m]	
	[mm]	[cm]	[szt.]	[szt.]	A-0 ø8	A-IIIIN #12
Poz.: 1.1 strop						
1	12	820	49	1		401,80
2	12	803	50	1		401,50
3	12	320	128	1		409,60
4	8	97	64	1	62,08	
Długość razem:				[m]	62,08	1212,90
Masa jednostkowa:				[kg/m]	0,395	0,888
Masa razem:				[kg]	24,5	1077,1
Masa ogólna:				[kg]		1101,6

BETON: C25/30
STAL: A-IIIIN RB500W
A-0 SŁOS
OTULINA: 25mm

- UWAGI:
- Wymiary podano w [cm], poziomy w [m].
 - Rozpatrywać łącznie z pozostałymi rysunkami konstrukcyjnymi kondygnacji.

a	dodano otwór stropu	13.10.2023	M.Raducki
Rewizja	Opis	Data	Nazwisko

±0.00 = 225.50m n.p.m.

Inwestor	DZMT KROWODRZA SP. Z O. O., ul. Kołetek 4/2, 31-069 Kraków		
Inwestycja	BUDOWA 28 BUDYNKÓW MIESZKALNYCH JEDNORODZINNYCH W ZABUDOWIE BLIŹNIACZEJ Z 14 GARAJAMI ZAMKNIĘTYMI, WBUDOWANYMI ORAZ 14 GARAJÓW ZAMKNIĘTYCH, WOLNOSTOJĄCYCH, Z ZAGOSPODAROWANIEM TERENU, SCHODAMI ZEWNĘTRZNYMI, MURAMI OPOROWYMI, ZEWNĘTRZNYMI STANOWISKAMI POSTOJOWYMI, DOJŚCIEM I DOJAZDEM.		
Adres	Kraków 126102_9, obr. Krowodrza 0033, 773, 774, 775		
Zakres	BUDYNEK B1, C1		
Treść rysunku	STROP 1.1		
Projektant	mgr inż. Łukasz Sekuła Upr. SWK/POOK/0027/12	Podpis	
Faza	Skala	Branża	Nr rysunku
PW	1:50	KONSTR.	K-22a
			Data
			04.2023

LEGENDA:
G - pręty górne
D - pręty dolne
* - pręt docięć przy krawędzi/otworze

OZNACZENIA:
20 grubość płyty
↑ kierunek główny zbrojenia

