
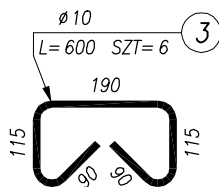
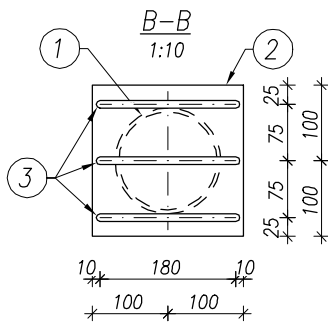
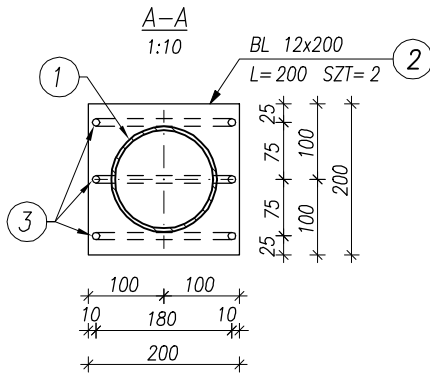


S-01 słup (szt. 2)
skala 1:25

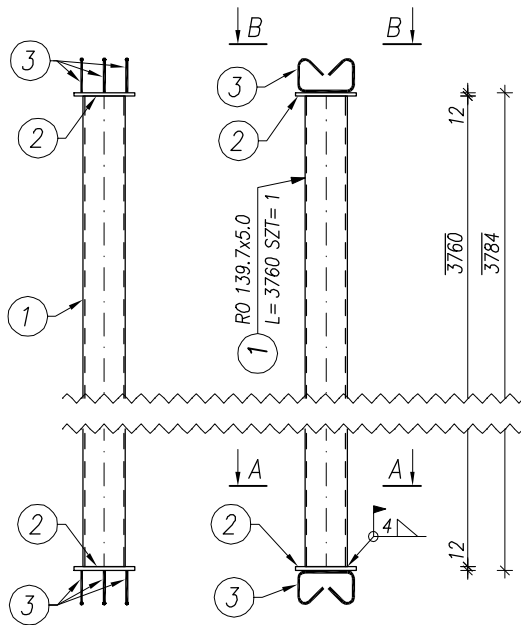

STAŁ KONSTRUKCYJNA S235

SPOINY

jeżeli nie opisano stosować wg:



- spoiny pachwinowe:

$\min(0,2t_2; 2,5\text{mm}) < a < \min(0,7t_1; 16\text{mm})$; $t_2 > t_1$

- podwójne spoiny pachwinowe: 0,5t

- spoiny V i 1/2V: $\min(t_1; t_2)$

BR-1 barierka (50.6 mb)
skala 1:25

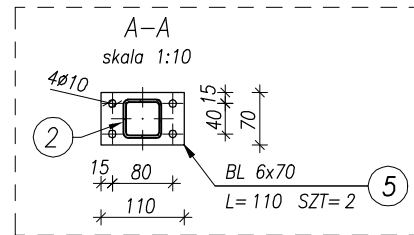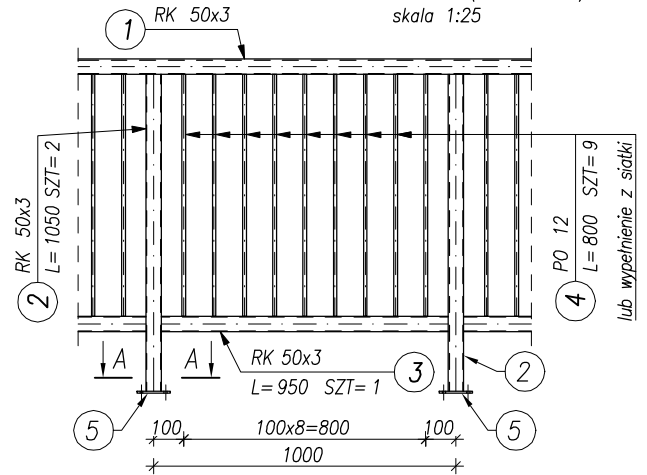

UWAGI:

- Wymiary podano w [mm], poziomy w [m].
- Projekt rozpatrywać łącznie z pozostałymi projektami branżowymi.
- Spawanie elementów wykonać na warsztacie.
- Stal malować farbą podkładową antykorozyjną, atestowanym zestawem farb malarskich do zastosowań zewnętrznych lub ocynkować.
- Po wykonaniu elementu wszystkie naroża blach lub profili o ostrych kątach należy zeszlifować.
- Ostateczny wygląd barierki do decyzji na etapie projektu wnętrza.
- Dopuszcza się montowanie słupów na 4 kotwach chemicznych M16 z zachowaniem minimalnego odstępu od krawędzi betonu wynoszącego 65mm. W przypadku zastosowania innych kotew należy lokalizować je w odległości od krawędzi betonu zgodnej z wytycznymi Producenta.

b	zmieniono pozycję S-01, dodano uwagę dotyczącą montażu	31.10.2023	M.Raducki
a	zmiana pozycji BR-1	05.07.2023	M.Raducki
Rewizja	Opis	Data	Nazwisko

$\pm 0.00 = 225.50\text{m n.p.m.}$

Inwestor	DZMT KROWODRZA SP. Z O. O., ul. Kołetek 4/2, 31-069 Kraków		
Inwestycja	BUDOWA 28 BUDYNKÓW MIESZKALNYCH JEDNORODZINNYCH W ZABUDOWIE BLIŹNIACZEJ Z 14 GARAŻAMI ZAMKNIĘTYMI, WBUDOWANYMI ORAZ 14 GARAŻY ZAMKNIĘTYCH, WOLNOSTOJĄCYCH, Z ZAGOSPODAROWANIEM TERENU, SCHODAMI ZEWNĘTRZNYMI, MURAMI OPOROWYMI, ZEWNĘTRZNYMI STANOWISKAMI POSTOJOWYMI, DOJŚCIEM I DOJAZDEM.		
Adres	Kraków 126102_9, obr. Krowodrza 0033, 773, 774, 775		
Zakres	BUDYNEK B1, C1		
Treść rysunku	SŁUP S-01 BARIERKA BR-1		
Projektant	mgr inż. Łukasz Sekuła Upr. SWK/POOK/0027/12		Podpis
Faza	Skala	Branża	Nr rysunku
PW	1:25	KONSTR.	K-24b
			Data
			04.2023