

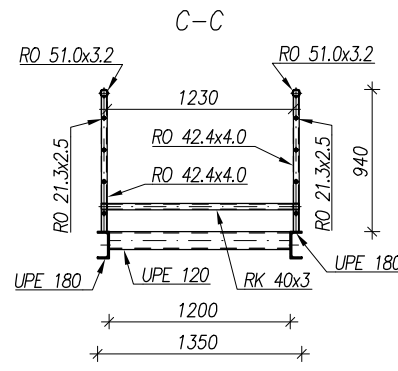


5.1 schody (1 szt.)
skala 1:50

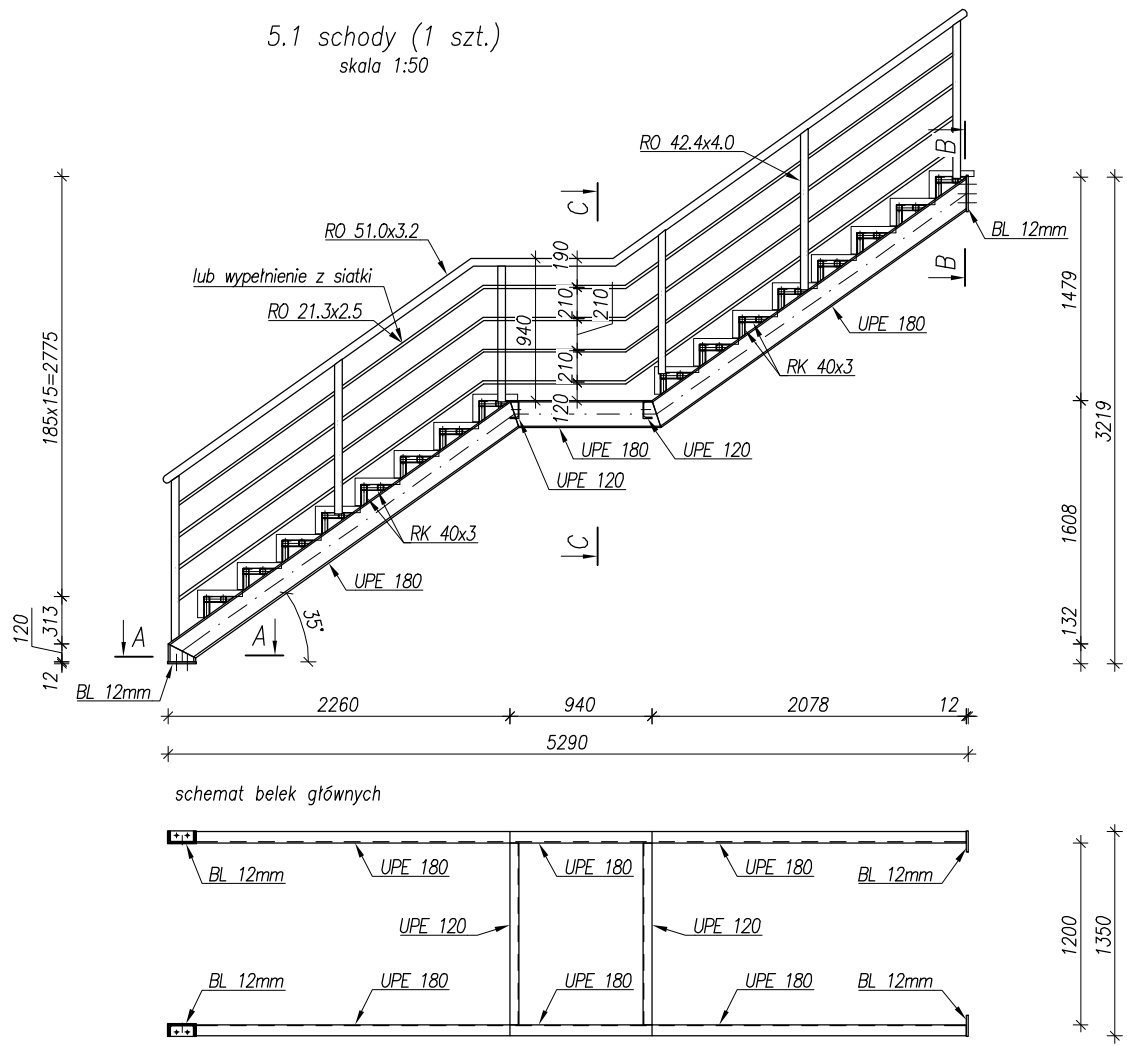

stopnie betonowe gr.40mm 260x1350mm 17 szt

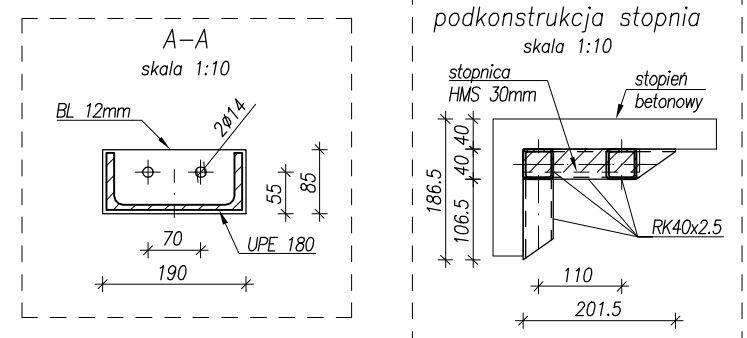

STAL KONSTRUKCYJNA S235

SPOINY
jeżeli nie opisano stosować wg:
- spoiny pachwinowe:
 $\min(0,2t_2; 2,5\text{mm}) < a < \min(0,7t_1; 16\text{mm})$; $t_2 > t_1$
- podwójne spoiny pachwinowe: 0,5t
- spoiny V i 1/2V: $\min(t_1; t_2)$


- UWAGI:
- Wymiary podano w [mm], poziomy w [m].
 - Projekt rozpatrywać łącznie z pozostałymi projektami branżowymi.
 - Spawanie elementów wykonać na warsztacie.
 - Stal malować farbą podkładową antykorozyjną, atestowanym zestawem farb malarskich do zastosowań zewnętrznych lub ocynkować.
 - Po wykonaniu elementu wszystkie naroża blach lub profili o ostrych kątach należy zeszlifować.

a	zmiana podkonstrukcji stopnia i sposobu wykonczenia	05.07.2023	M.Raducki
Rewizja	Opis	Data	Nazwisko

±0.00 = 225.50m n.p.m.

ZESTAWIENIE STALI KONSTRUKCYJNEJ

Nazwa elementu	Długość [mm]	Materiał	Ilość	Dł. razem [m]	Masa jedn. [kg/m]	Masa razem [kg]
			[szt.]			
UPE 180	120	S235	2	0,24	21,60	5,18
UPE 180	2775	S235	2	5,55	21,60	119,88
UPE 180	1000	S235	2	2,00	21,60	43,20
UPE 180	2610	S235	2	5,22	21,60	112,75
UPE 120	1200	S235	2	2,40	13,20	31,68
BL 12x85	190	S235	2	0,38	8,01	3,04
BL 12x140	240	S235	2	0,48	13,19	6,33
RK 40x2.5	106	S235	16	1,70	2,89	4,90
RK 40x2.5	202	S235	16	3,23	2,89	9,34
RK 40x2.5	1230	S235	32	39,36	2,89	113,75
RO 42.4x4.0	1150	S235	12	13,80	3,79	52,30
RO 51.0x3.2	6500	S235	2	13,00	3,77	49,01
RO 21.3x2.5	6500	S235	8	52,00	1,16	60,32
razem [kg]						611,70

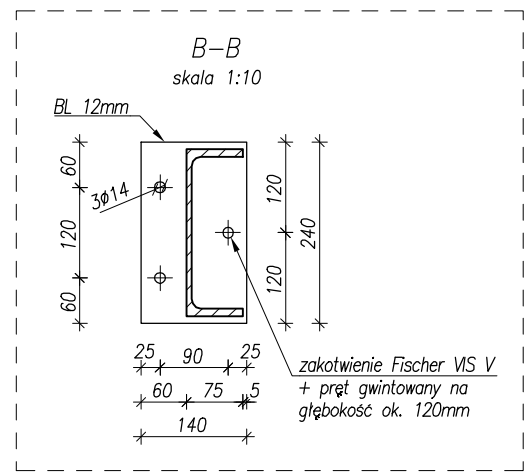

Inwestor	DZMT KROWDRZA SP. Z O. O., ul. Koletek 4/2, 31-069 Kraków			
Inwestycja	BUDOWA 28 BUDYNKÓW MIESZKALNYCH JEDNORODZINNYCH W ZABUDOWIE BLIŹNIACZEJ Z 14 GARAŻAMI ZAMKNIĘTYMI, WBUDOWANYMI ORAZ 14 GARAŻY ZAMKNIĘTYCH, WOLNOSTOJĄCYCH, Z ZAGOSPODAROWANIEM TERENU, SCHODAMI ZEWNĘTRZNYMI, MURAMI OPOROWYMI, ZEWNĘTRZNYMI STANOWISKAMI POSTOJOWYMI, DOJŚCIEM I DOJAZDEM.			
Adres	Kraków 126102_9, obr. Krowdrza 0033, 773, 774, 775			
Zakres	BUDYNEK B1, C1			
Treść rysunku	SCHODY 5.1			
Projektant	mgr inż. Łukasz Sekuła Upr. SWK/POOK/0027/12		Podpis	
Faza	Skala	Branża	Nr rysunku	Data
PW	1:50	KONSTR.	K-25a	04.2023