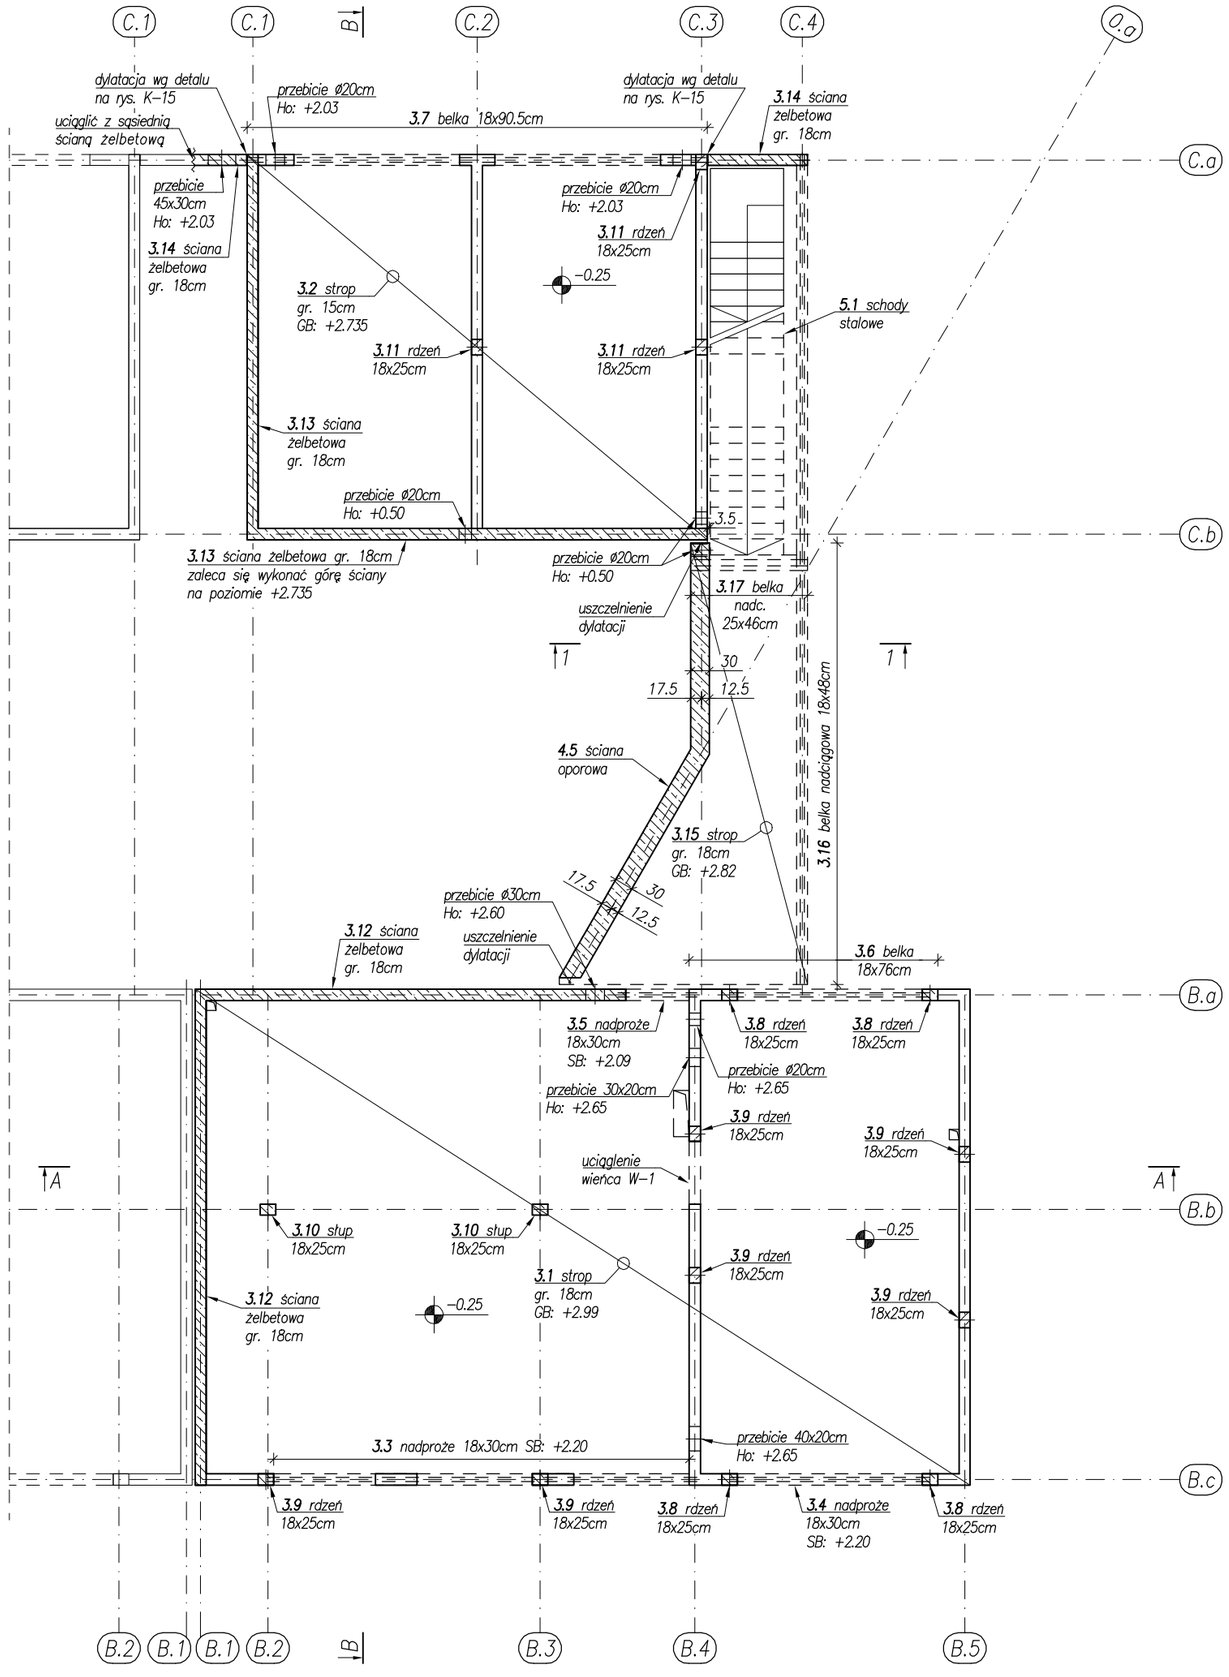


OZNACZENIA:

- wykotwienia elementów żelbetowych
- elementy żelbetowe
- ściany nośne pod belkami
- ściany murowane
- belki

LEGENDA:
GB – góra betonu konstrukcyjnego
SB – spód betonu konstrukcyjnego

BETON:	C25/30
STAL:	A–IIIN RB500W A–0 StOS
OTULINA:	25mm

UWAGI:
- Wymiary podano w [cm], poziomy w [m].
- Rozpatrywać łącznie z pozostałymi rysunkami konstrukcyjnymi kondygnacji.

Rewizja	Opis	Data	Nazwisko
b	zmiana ściany 3.13	31.10.2023	M.Raducki
a	zmiana gabarytu ściany oporowej 4.5	05.07.2023	M.Raducki

±0.00 = 225.50m n.p.m.

Inwestor: DZMT KROWODRZA SP. Z O. O., ul. Koletek 4/2, 31–069 Kraków

Inwestycja:
BUDOWA 28 BUDYNKÓW MIESZKALNYCH JEDNORODZINNYCH W ZABUDOWIE BLIŹNIACZEJ Z 14 GARAŻAMI ZAMKNIĘTYMI, WBUDOWANYMI ORAZ 14 GARAŻY ZAMKNIĘTYCH, WOLNOSTOJĄCYCH, Z ZAGOSPODAROWANIEM TERENU, SCHODAMI ZEWNĘTRZNYMI, MURAMI OPOROWYMI, ZEWNĘTRZNYMI STANOWISKAMI POSTOJOWYMI, DOJŚCIEM I DOJAZDEM.

Adres: Kraków 126102_9, obr. Krowodrza 0033, 773, 774, 775

Zakres: BUDYNEK B1, C1

Treść rysunku: RZUT PARTERU

Projektant: mgr inż. Łukasz Sekuła
Upr. SWK/POOK/0027/12

Podpis:

Faza	Skala	Branża	Nr rysunku	Data
PW	1:100	KONSTR.	K–02b	04.2023