


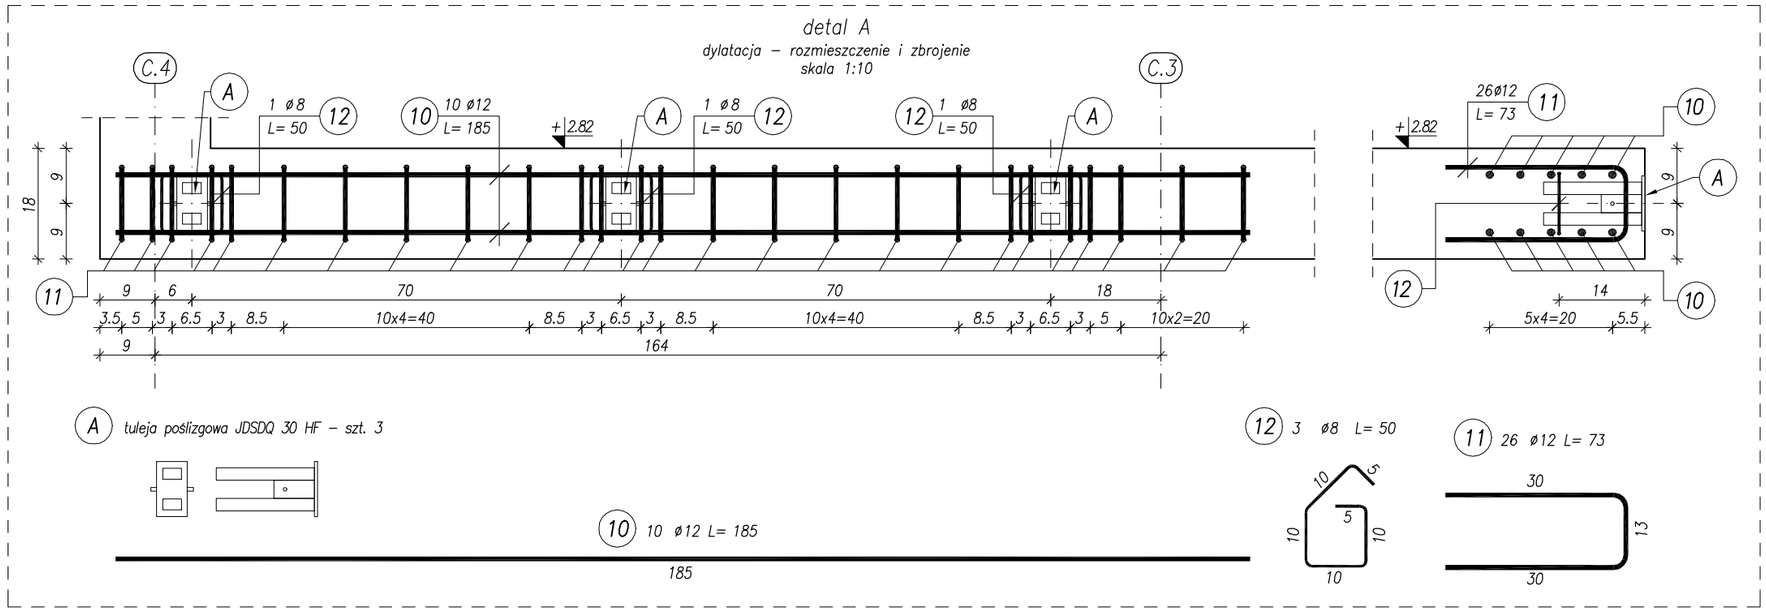



ELEMENTY DODATKOWE		
poz.	nazwa	ilość [szt].
A	tuleja poślizgowa JDSDQ 30 HF	3

ZESTAWIENIE STALI ZBROJENIOWEJ							
Nr pręta	ø	Długość	Ilość	Ilość pozycji	Dł. ogólna [m]		
					A–0	A–IIIN	
	[mm]	[cm]	[szt.]	[szt.]	ø8	#8	#12
Poz.:	3.15 strop						
1	12	180	12	1			21,60
2	12	290	8	1			23,20
3	12	400	9	1			36,00
4	12	698	14	1			97,72
5	12	400	23	1			92,00
6	12	260	20	1			52,00
7	12	370	13	1			48,10
8	12	480	14	1			67,20
9	8	93	30	1	27,90		
10	12	185	10	1			18,50
11	12	73	26	1			18,98
12	8	50	3	1		1,50	
Długość razem:				[m]	27,90	1,50	475,30
Masa jednostkowa:				[kg/m]	0,395	0,395	0,888
Masa razem:				[kg]	11,0	0,6	422,1
Masa ogólna:				[kg]	433,7		

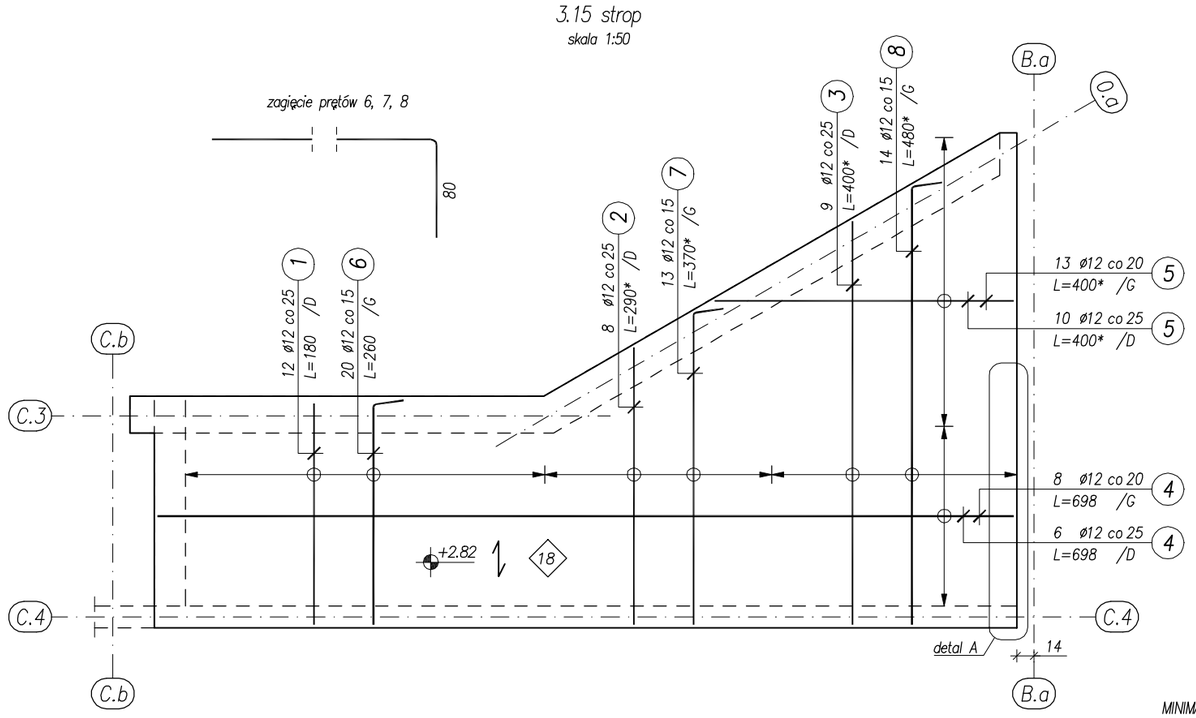

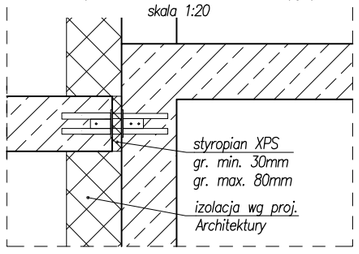

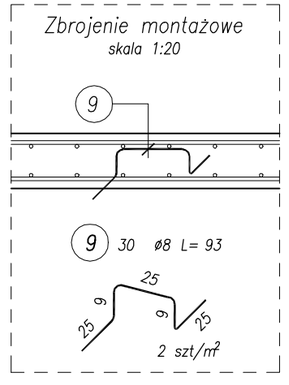

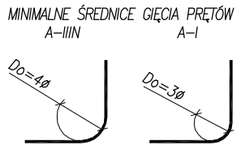

BETON:	C25/30
STAL:	A–IIIN RB500W A–0 St0S
OTULINA:	25mm

OZNACZENIA:

18 grubość płyty

kierunek główny zbrojenia

LEGENDA:
G – pręty górne
D – pręty dolne
* – pręt dociąć przy krawędzi/otworze

UWAGI:
- Wymiary podano w [cm], poziomy w [m].
- Rozpatrywać łącznie z pozostałymi rysunkami konstrukcyjnymi kondygnacji.
- Dopuszcza się zamianę miejscami tulei poślizgowej z trzpieniem (montaż tulei w belce, trzpienia w płycie stropowej).

Rewizja	Opis	Data	Nazwisko
b	dodano uwagę dotyczącą trzpieni dylatacyjnych	31.10.2023	M.Raducki
a	dodano detal izolacji przy dylatacji	05.07.2023	M.Raducki

±0.00 = 225.50m n.p.m.

Inwestor	DZMT KROWODRZA SP. Z O. O., ul. Koletek 4/2, 31–069 Kraków
Inwestycja	BUDOWA 28 BUDYNKÓW MIESZKALNYCH JEDNORODZINNYCH W ZABUDOWIE BLIŹNIACZEJ Z 14 GARAŻAMI ZAMKNIĘTYMI, WBUDOWANYMI ORAZ 14 GARAŻY ZAMKNIĘTYCH, WOLNOSTOJĄCYCH, Z ZAGOSPODAROWANIEM TERENU, SCHODAMI ZEWNĘTRZNYMI, MURAMI OPOROWYMI, ZEWNĘTRZNYMI STANOWISKAMI POSTOJOWYMI, DOJŚCIEM I DOJAZDEM.
Adres	Kraków 126102_9, obr. Krowodrza 0033, 773, 774, 775
Zakres	BUDYNEK B1, C1
Treść rysunku	STROP 3.15
Projektant	mgr inż. Łukasz Sekuła Upr. SWK/POOK/0027/12
Podpis	

Faza	Skala	Branża	Nr rysunku	Data
PW	1:50	KONSTR.	K–16b	04.2023