


FIRMA PROJEKTOWO-HANDLOWA "M" Architekt Michał 30-020 Kraków, ul. Włostowa 9/16 tel. 607 985 279, e-mail: architektm@gmail.com NIP: 677-004-96-66 REGON: 003923573			
INWESTOR	HAMAK LOKALITA Spółka z o.o. ul. Armii Krajowej 25 30-150 Kraków		
TEMAT	Budowa 28 budynków mieszkalnych jednorodzinnych w zabudowie bliźniaczej z 14 garażami zamkniętymi, wzdłużowymi oraz 14 garaży zamkniętych, wzdłużowych, z zagospodarowaniem terenu, schodami zewnętrznymi, murami oporowymi, zewnętrznyimi stawkami postojowymi, dojściem i dojazdem na dz. nr 773, 774 i 775 obr. 0033 Krowodrza w Krakowie		
OPRACOWANIE	INSTALACJE SANITARNE		
FAZA	PROJEKT TECHNICZNY		
TITUL RYSUNKU	BUDYNKI B I C – RZUT DACHU – INSTALACJE WOD-KAN		
DATA	SERPIEŃ 2023 r.		
SKALA	1:100	POOS	DATA
PROJEKTANT	mgr inż. D. Dziubina MAP/0226/POOS/10		
SPRAWDZAJĄCY	mgr inż. W. Czerwaka MAP/0359/POOS/08		
WSPÓŁPRACUJĄCY	mgr inż. A. Michalec		
			NR RYS. PT/IS-01.10

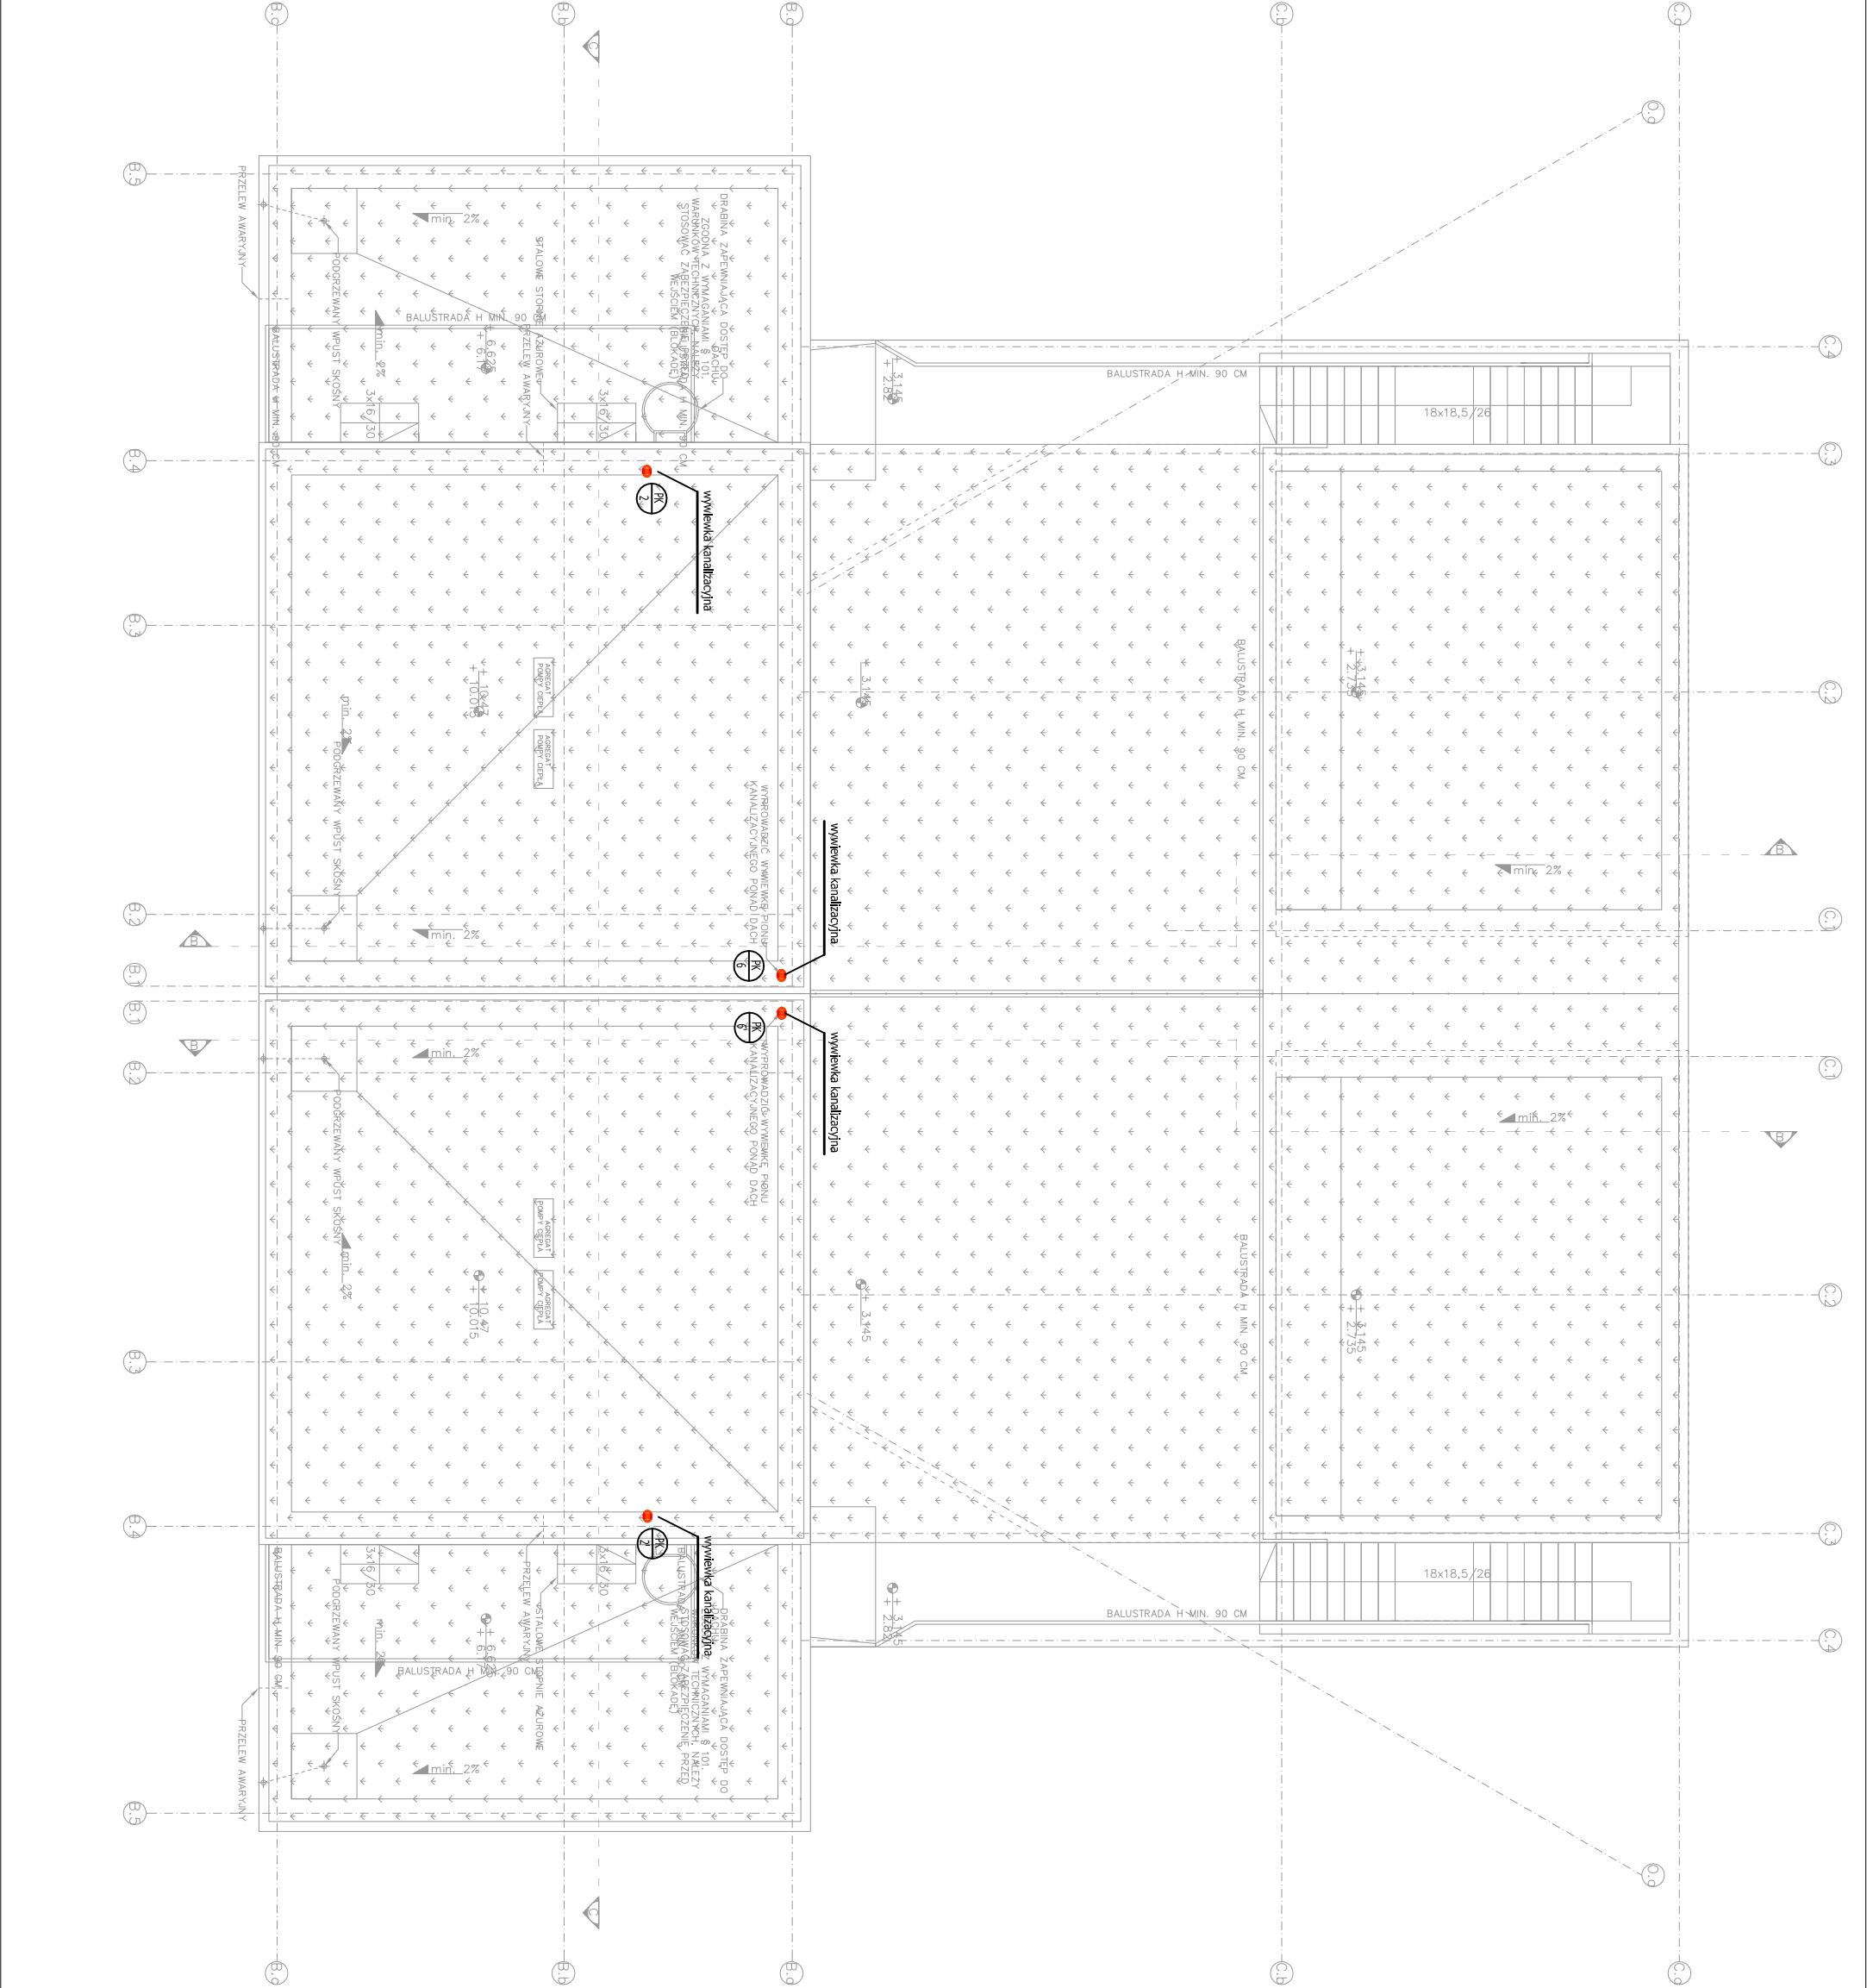

Oznaczenia:

- Woda zimna prowadzona w posadzce
- Woda zimna prowadzona pod stropem
- Woda ciepła prowadzona w posadzce
- Woda ciepła prowadzona pod stropem
- Kanalizacja sanitarna prowadzona pod stropem
- Kanalizacja sanitarna prowadzona w posadzce
- Kanalizacja sanitarna prowadzona pod stropem

Plan instalacji wododopływowej

Plan instalacji kanalizacji sanitarnej