

Objaśnienia:

- projektowana instalacja wody zimnej
- prowadzona w posadzce
- projektowana instalacja wody ciepłej
- prowadzona w posadzce

- kulowy zawór odcinający

- umywalka z baterią stojącą

- zlew z baterią stojącą

- wanna z baterią ścienną


- pralka, zmywarka

- miska usępowa

BUDYNKI C1-C14

BUDYNKI B1-B14

Dach

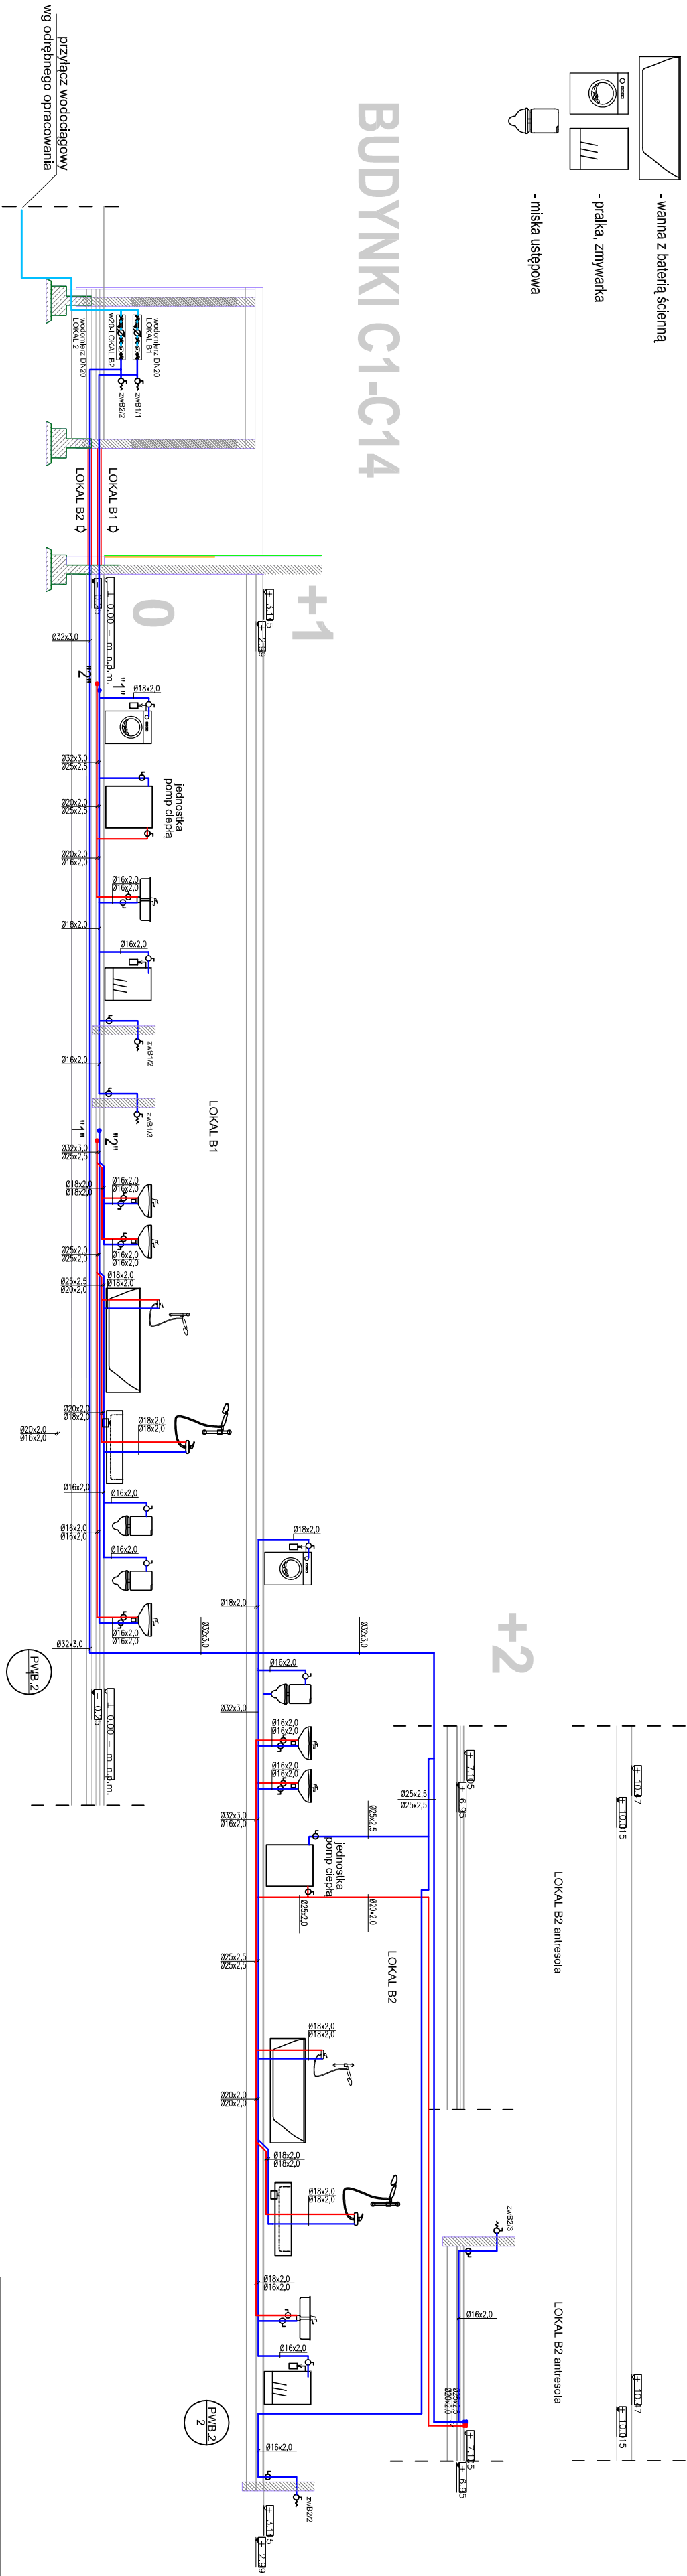

FIRMA PROJEKTOWO-HANDLOWA "MAX" Arcadiusz Micholice 30-020 Kraków, ul. Włodowska 8/16 tel. 607 895 279, e-mail: oremicholice@maxi.pl NIP: 677-060-56-89 REGON: 08382573			
INWESTOR	HANNAK LOKIETA Spółka z o.o. ul. Armii Krajowej 25 30-150 Kraków		
TEMAT Kawodrzo na dz. nr 773, 774 i 775 obr. 0033 Kawodrzo na w Krakowie			
OPRACOWANIE	INSTALACJE SANITARNE		
FAZA	PROJEKT TECHNICZNY		
TITUL RSUNKU	BUDYNKI B I C – INSTALACJE WOD-KAN ROZWIĄZANIE INSTALACJI WODY ZIMNEJ I Ciepłej		
DATA	SIERPIEŃ 2023 r.		
SKALA	1:100/100	POW. 08.2023	DATA
PROJEKTANT	mgr inż. D. Dziubyna MMP/0359/PO05/08		
SPRAWDZĄCY	mgr inż. W. Ciołowska MMP/0359/PO05/08		
WSPÓŁPRAC	mgr inż. A. Micholice nr ms. PT/IS-01.12		