


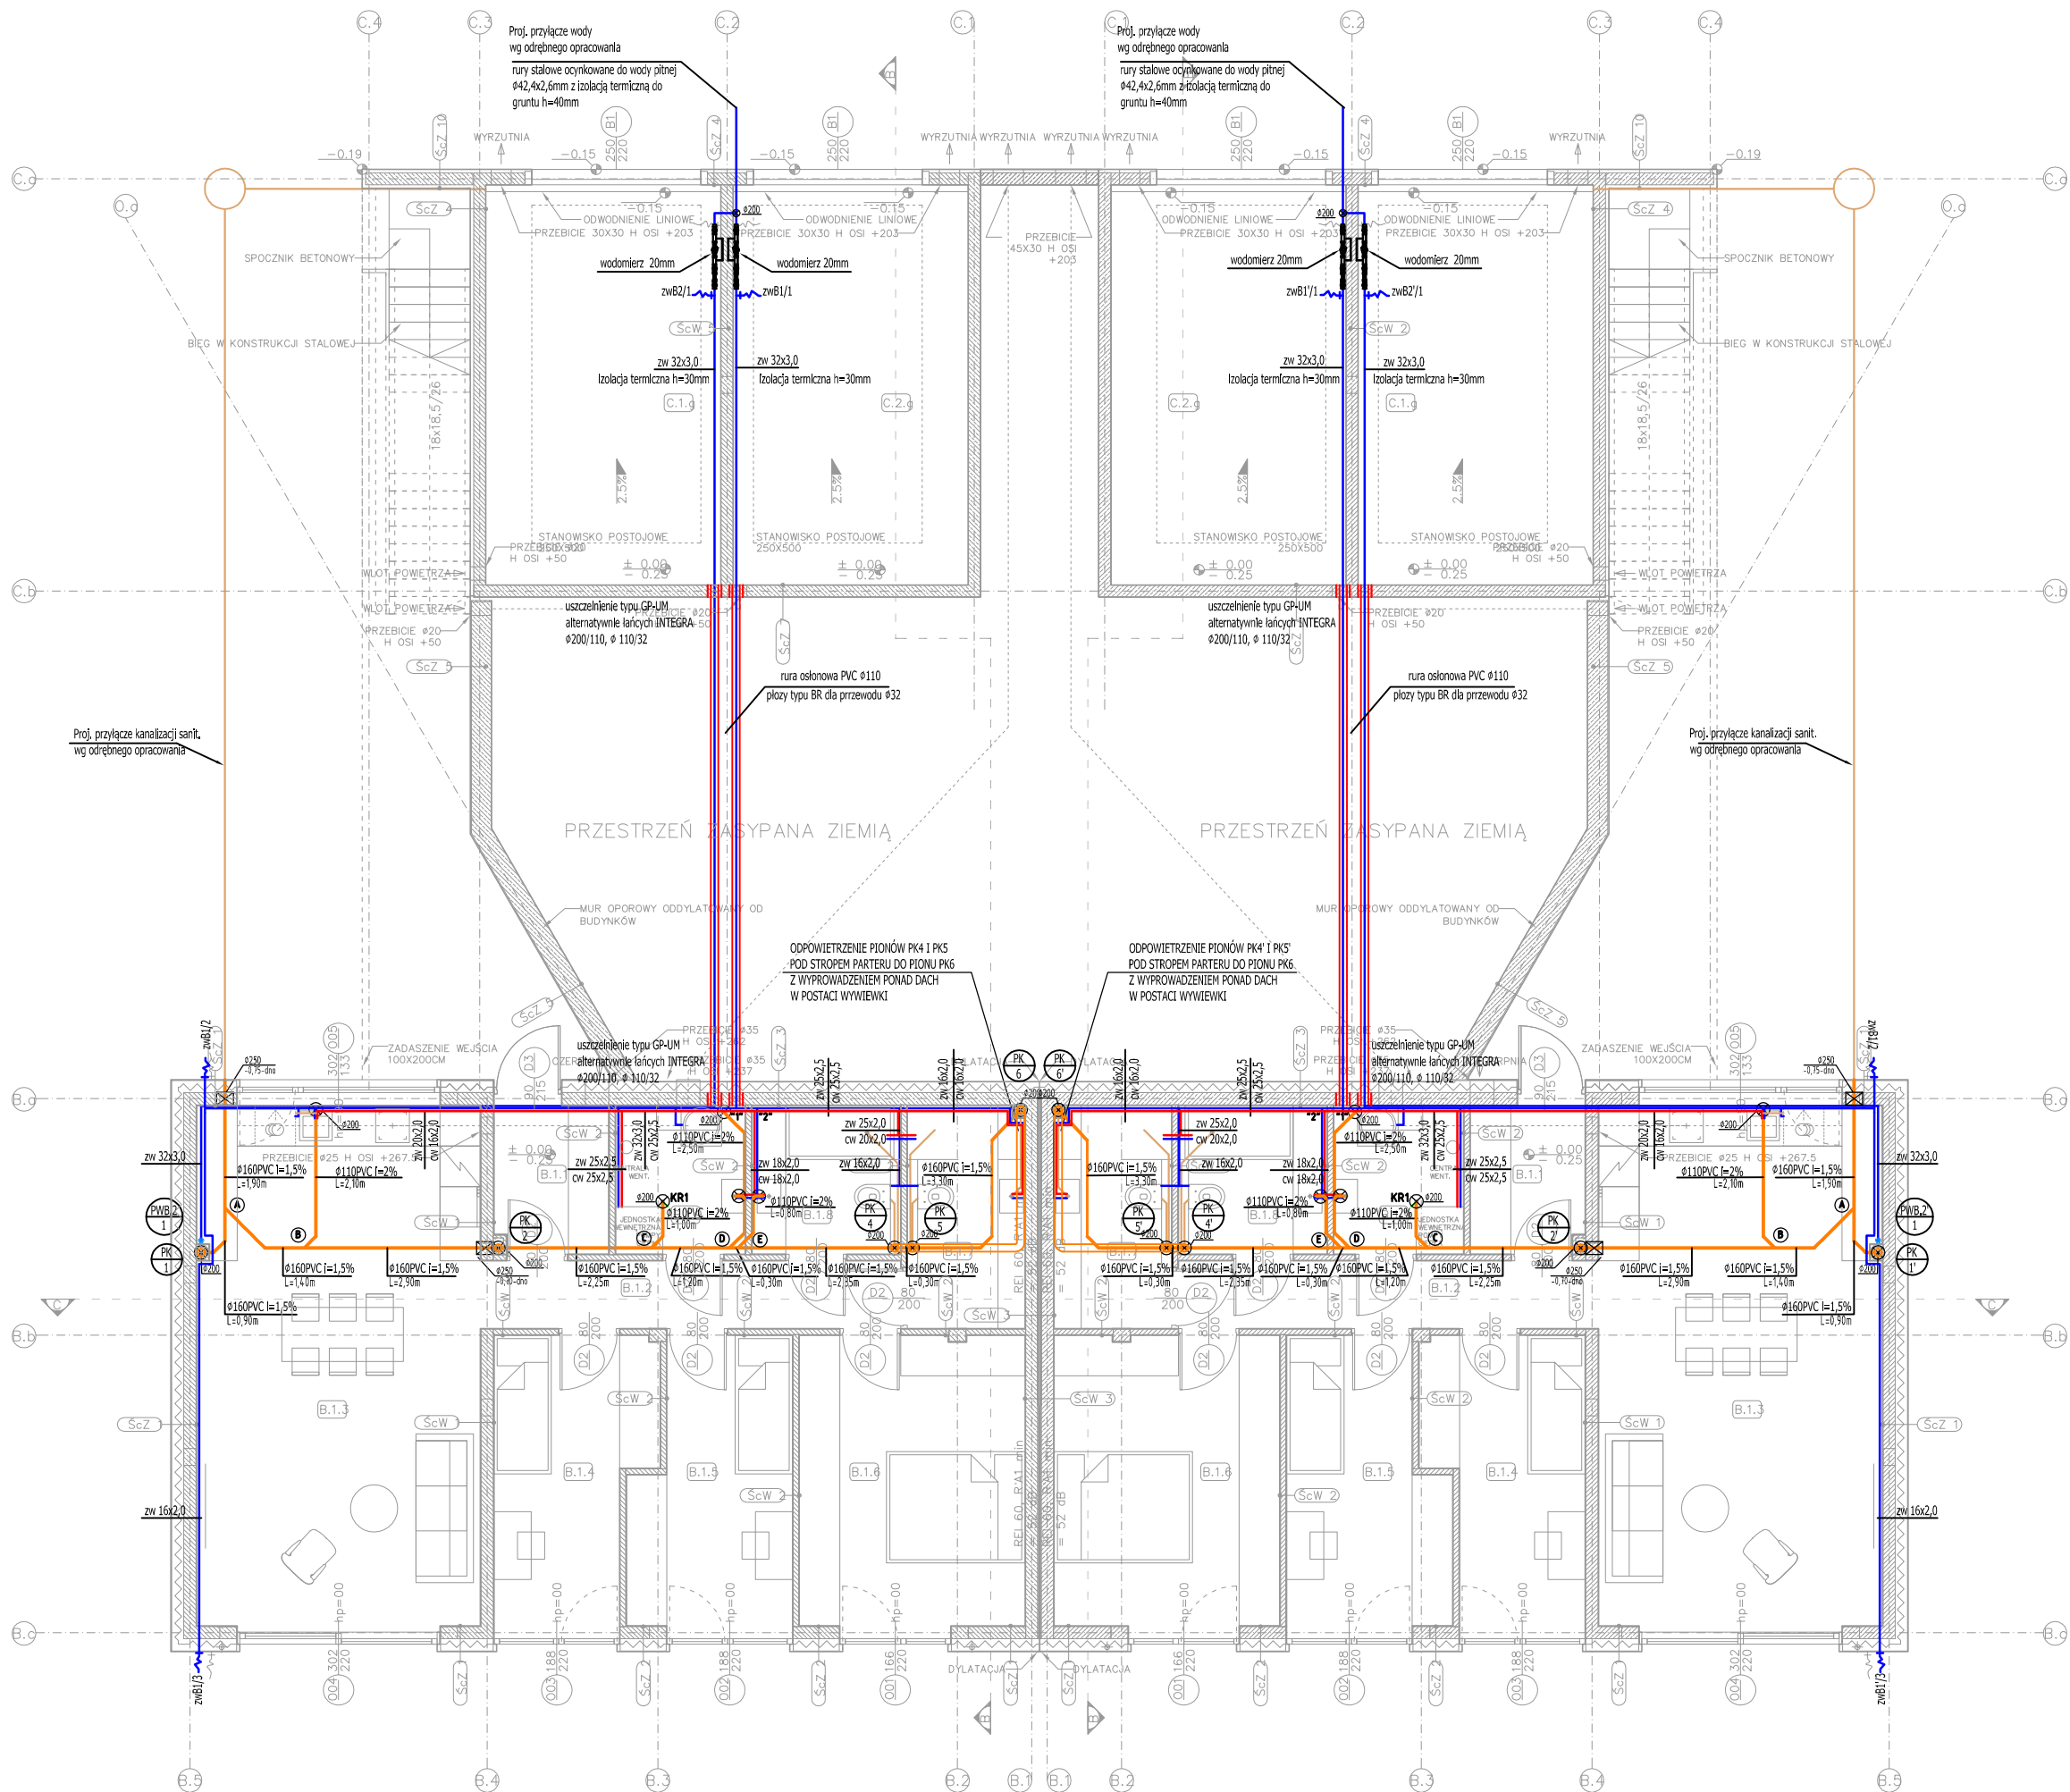

- Oznaczenia:
- Woda zimna prowadzona w posadzce
 - Woda zimna prowadzona pod stropem
 - Woda ciepła prowadzona w posadzce
 - Woda ciepła prowadzona pod stropem
 - Kanalizacja sanitarna prowadzona pod płytą
 - Kanalizacja sanitarna prowadzona w posadzce
 - Kanalizacja sanitarna prowadzona pod stropem
 - Pion instalacji wodociągowej
 - Pion instalacji kanalizacji sanitarnej

FIRMA PROJEKTOWO-HANDLOWA "MIX" Arkadiusz Michalec 30-020 Kraków, ul. Wójcowska 9/16 tel. 607 985 279, e-mail: arekmichalec@gmail.com NIP: 677-004-96-66 REGON: 003923573			
INWESTOR	HAMMAK ŁOKIETKA Spółka z o.o. ul. Armii Krajowej 25 30-150 Kraków		
TEMAT	Budowa 28 budynków mieszkalnych jednorodzinnych w zabudowie bliźniaczej z 14 garażami zamkniętymi, wbudowanymi oraz 14 garażami zamkniętymi, wolnostojących, z zagospodarowaniem terenu, schodami zewnętrznymi, murami oporowymi, zewnętrznymi stanowiskami postojowymi, dojściem i dojazdem na dz. nr 773, 774 i 775 obr. 0033 Krowodrza w Krakowie		
OPRACOWANIE	INSTALACJE SANITARNE		
FAZA	PROJEKT TECHNICZNY		
TYTUŁ RYSUNKU	BUDYNKI B I C - RZUT PARTERU - INSTALACJE WOD-KAN		
DATA	SIERPIEŃ 2023 r.		
SKALA	1:100	PODPIS	DATA
PROJEKTANT	mgr inż. D. Dziubyna MAP/0228/POOS/10		08.2023
SPRAWDZAJĄCY	mgr inż. W. Cisowska MAP/0359/POOS/08		
WSPÓŁPRACA	mgr inż. A. Michalec		NR RYS. PT/IS-01.7