


Rozdzielacz		1 - 2-gie piętro	
Symbol:	KAN ROZDZ UFS1 T3	Producent:	KAN
Śred. (G):	34,9 / 29,0	Szafka:	SZAFKA PODTYPKOWA SLIM+ KAN
Q (l/min):	4,8	Δp (Pa):	14544
Pomieszczenie-Odbiornik			
Nastawa	A	Ap	Tp
	m ²	m ²	m
2.A - (A)	0,9 l/min	7,9	0,20
2.A - (B)	1,9 l/min	14,7	0,20
2.A - (C)	2,2 l/min	18,2	0,20

Rozdzielacz		2 - 2-gie piętro	
Symbol:	KAN ROZDZ UFS1 T3	Producent:	KAN
Śred. (G):	34,9 / 29,1	Szafka:	SZAFKA PODTYPKOWA SLIM+ KAN
Q (l/min):	4,9	Δp (Pa):	14619
Pomieszczenie-Odbiornik			
Nastawa	A	Ap	Tp
	m ²	m ²	m
2.A-A - (C)	2,3 l/min	18,2	0,20
2.A-A - (B)	1,9 l/min	14,7	0,20
2.A-A - (A)	0,9 l/min	7,9	0,20

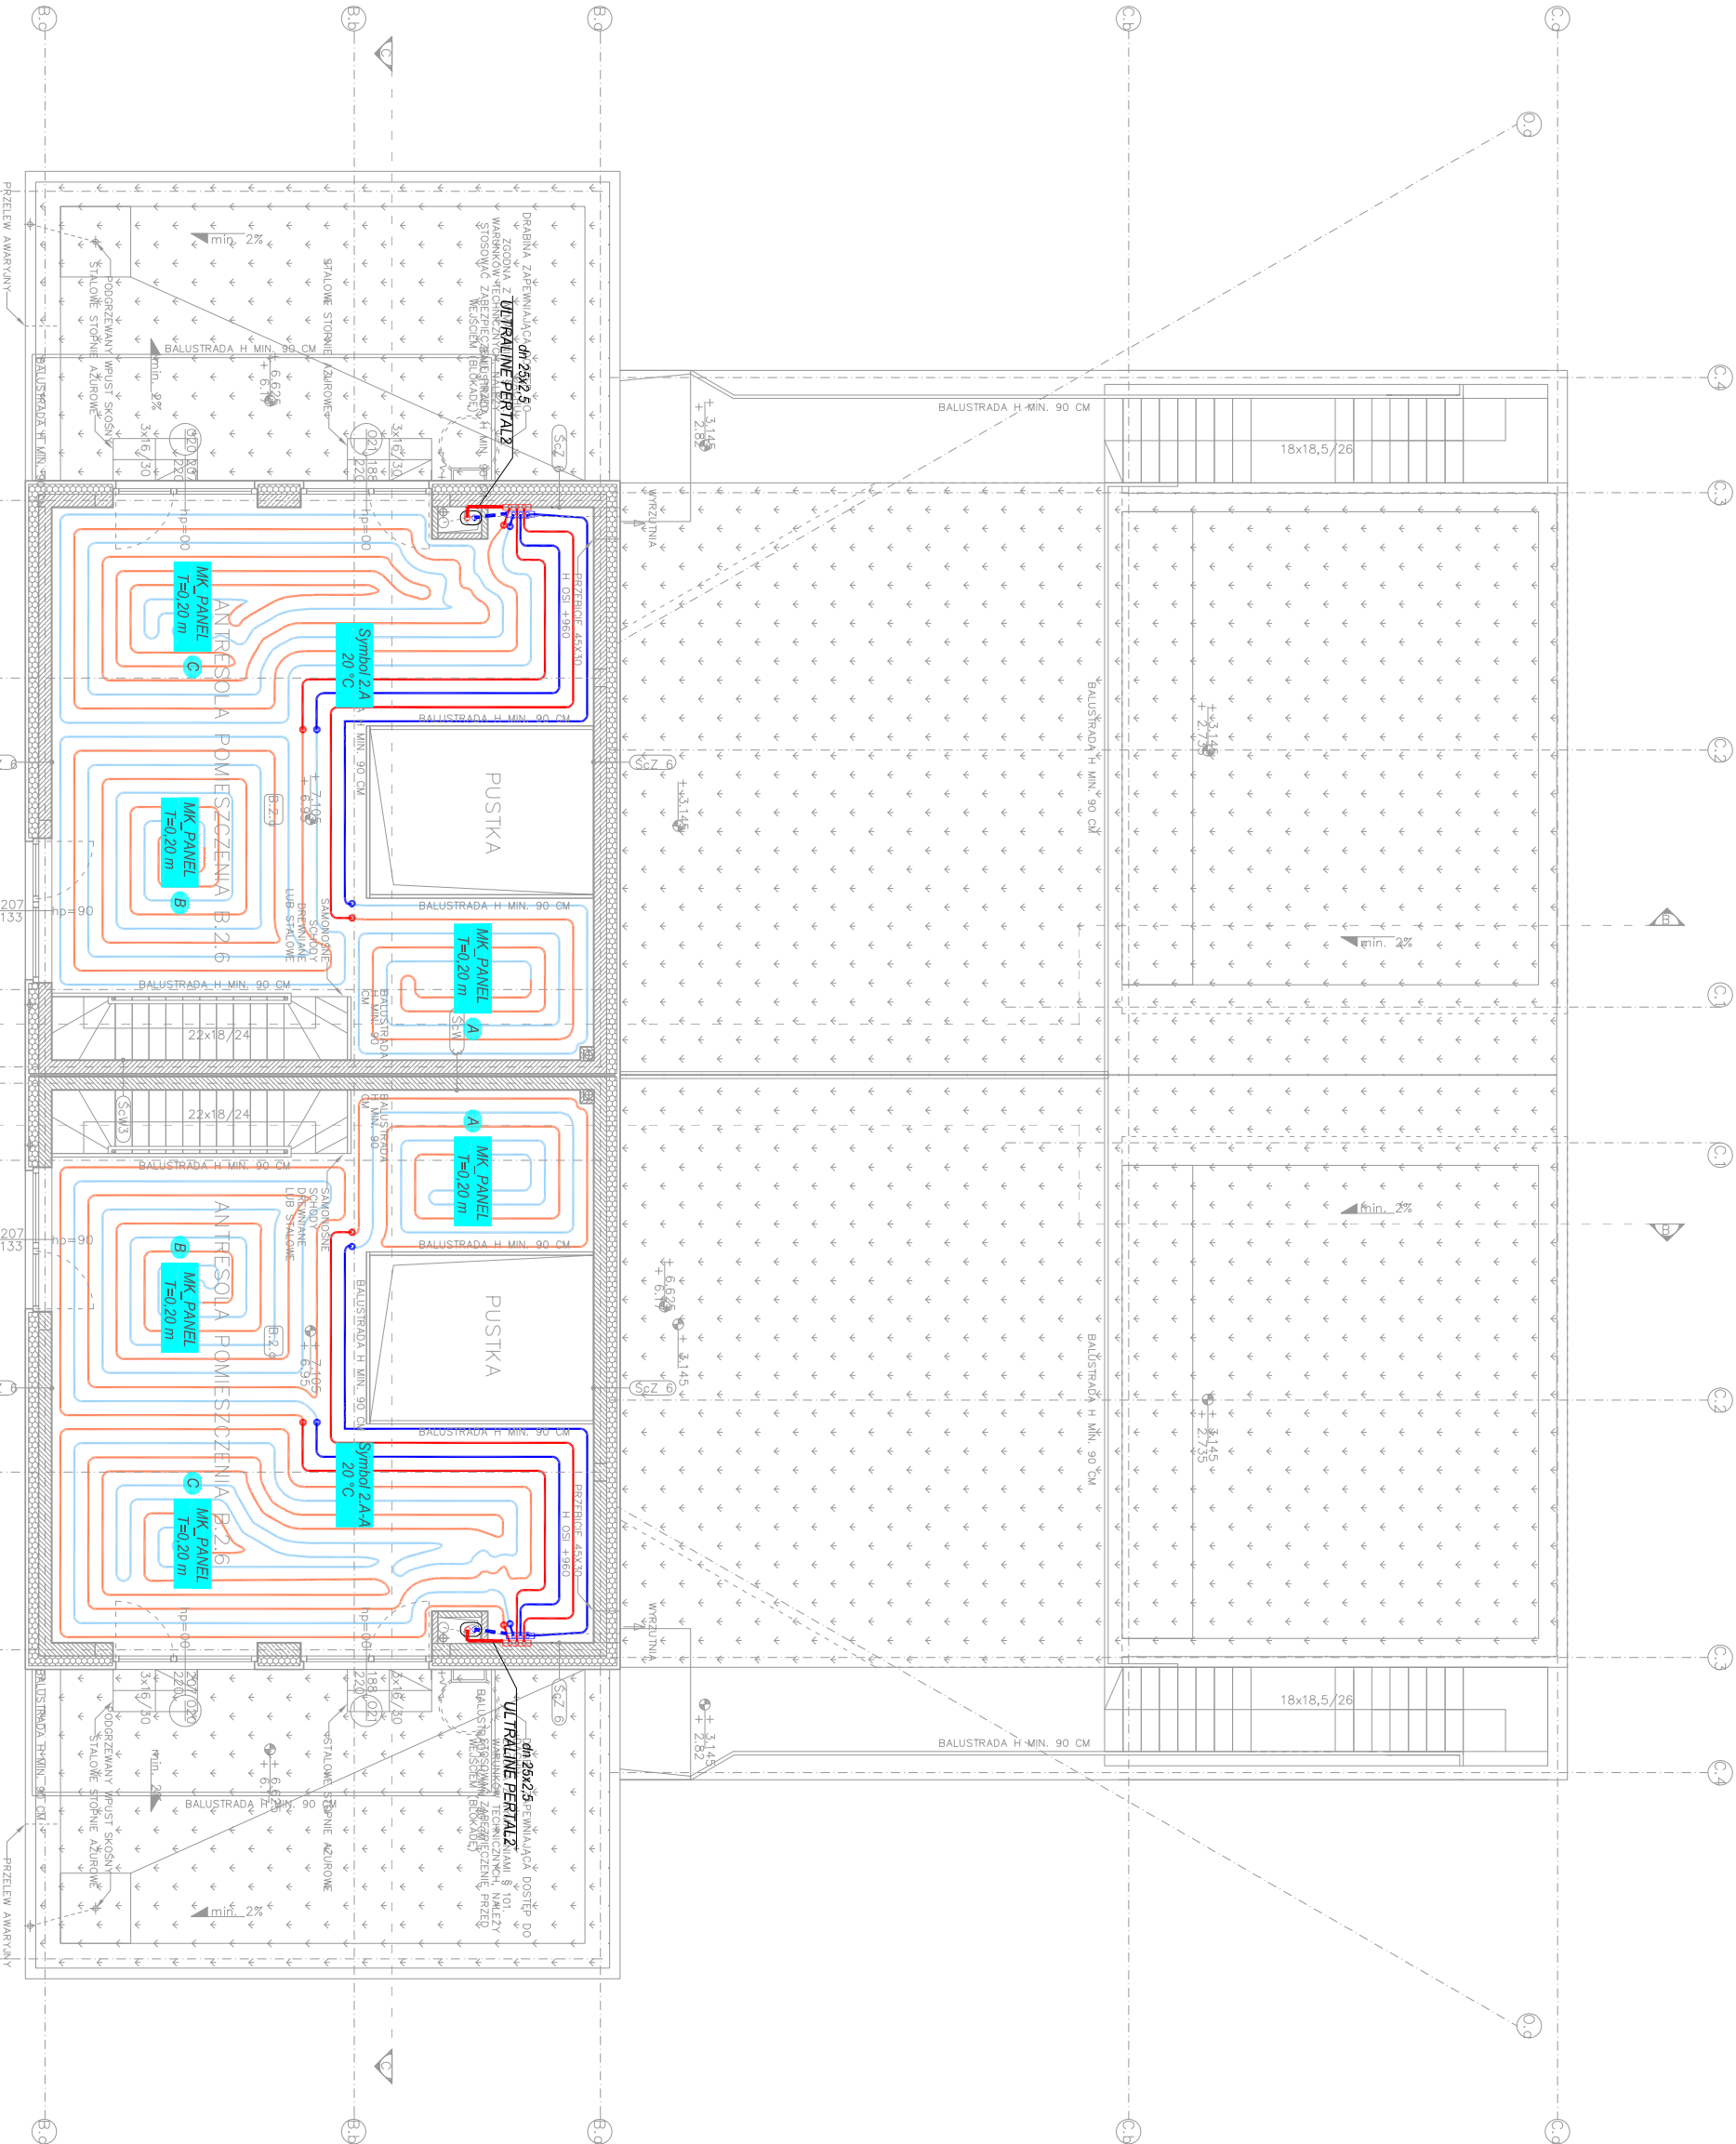

FIRMA PROJEKTOWA HANDLOWA "MK" Artur Michalec 30-020 Kraków, ul. Włodowa 9/16 tel. 607 985 279, e-mail: artur.michalec@gmail.com NIP: 677-004-96-66 REGON: 003923573		INWESTOR HAMAK ŁOKIETA Spółka z o.o. ul. Armii Krajowej 25 30-150 Kraków	
TEMAT Opracowanie instalacji sanitarnej		BUDOWA 28 budynków mieszkalnych jednorodzinnych w zabudowie bliźniaczej z 14 garażami zamkniętymi, wbudowanymi oraz 14 garaży zamkniętych, wolnostojących, z zagospodarowaniem terenu, schodami zewnętrznymi, murami oporowymi, zewnętrznymi stnamiśkami postojowymi, dojściem i dojazdem na dz. nr 773, 774 i 775 obr. 0033 Krowodrza w Krakowie	
FAZA PROJEKT TECHNICZNY		PROJEKT TECHNICZNY	
TYTUŁ RYSUNKU		BUDYNKI B I C – RZUT ANTRESOL – INSTALACJE C.O.	
DATA		SIERPIEŃ 2023 r.	
SKALA		1:100	
PROJEKTANT		mgr inż. D. Dziubyno MAP/0228/POOS/10	
SPRAWDZAJĄCY		mgr inż. W. Czerwko MAP/0359/POOS/08	
WSPÓŁPRACOWNIK		mgr inż. A. Michalec	
		NR RYS. PT/IS-02.6	

