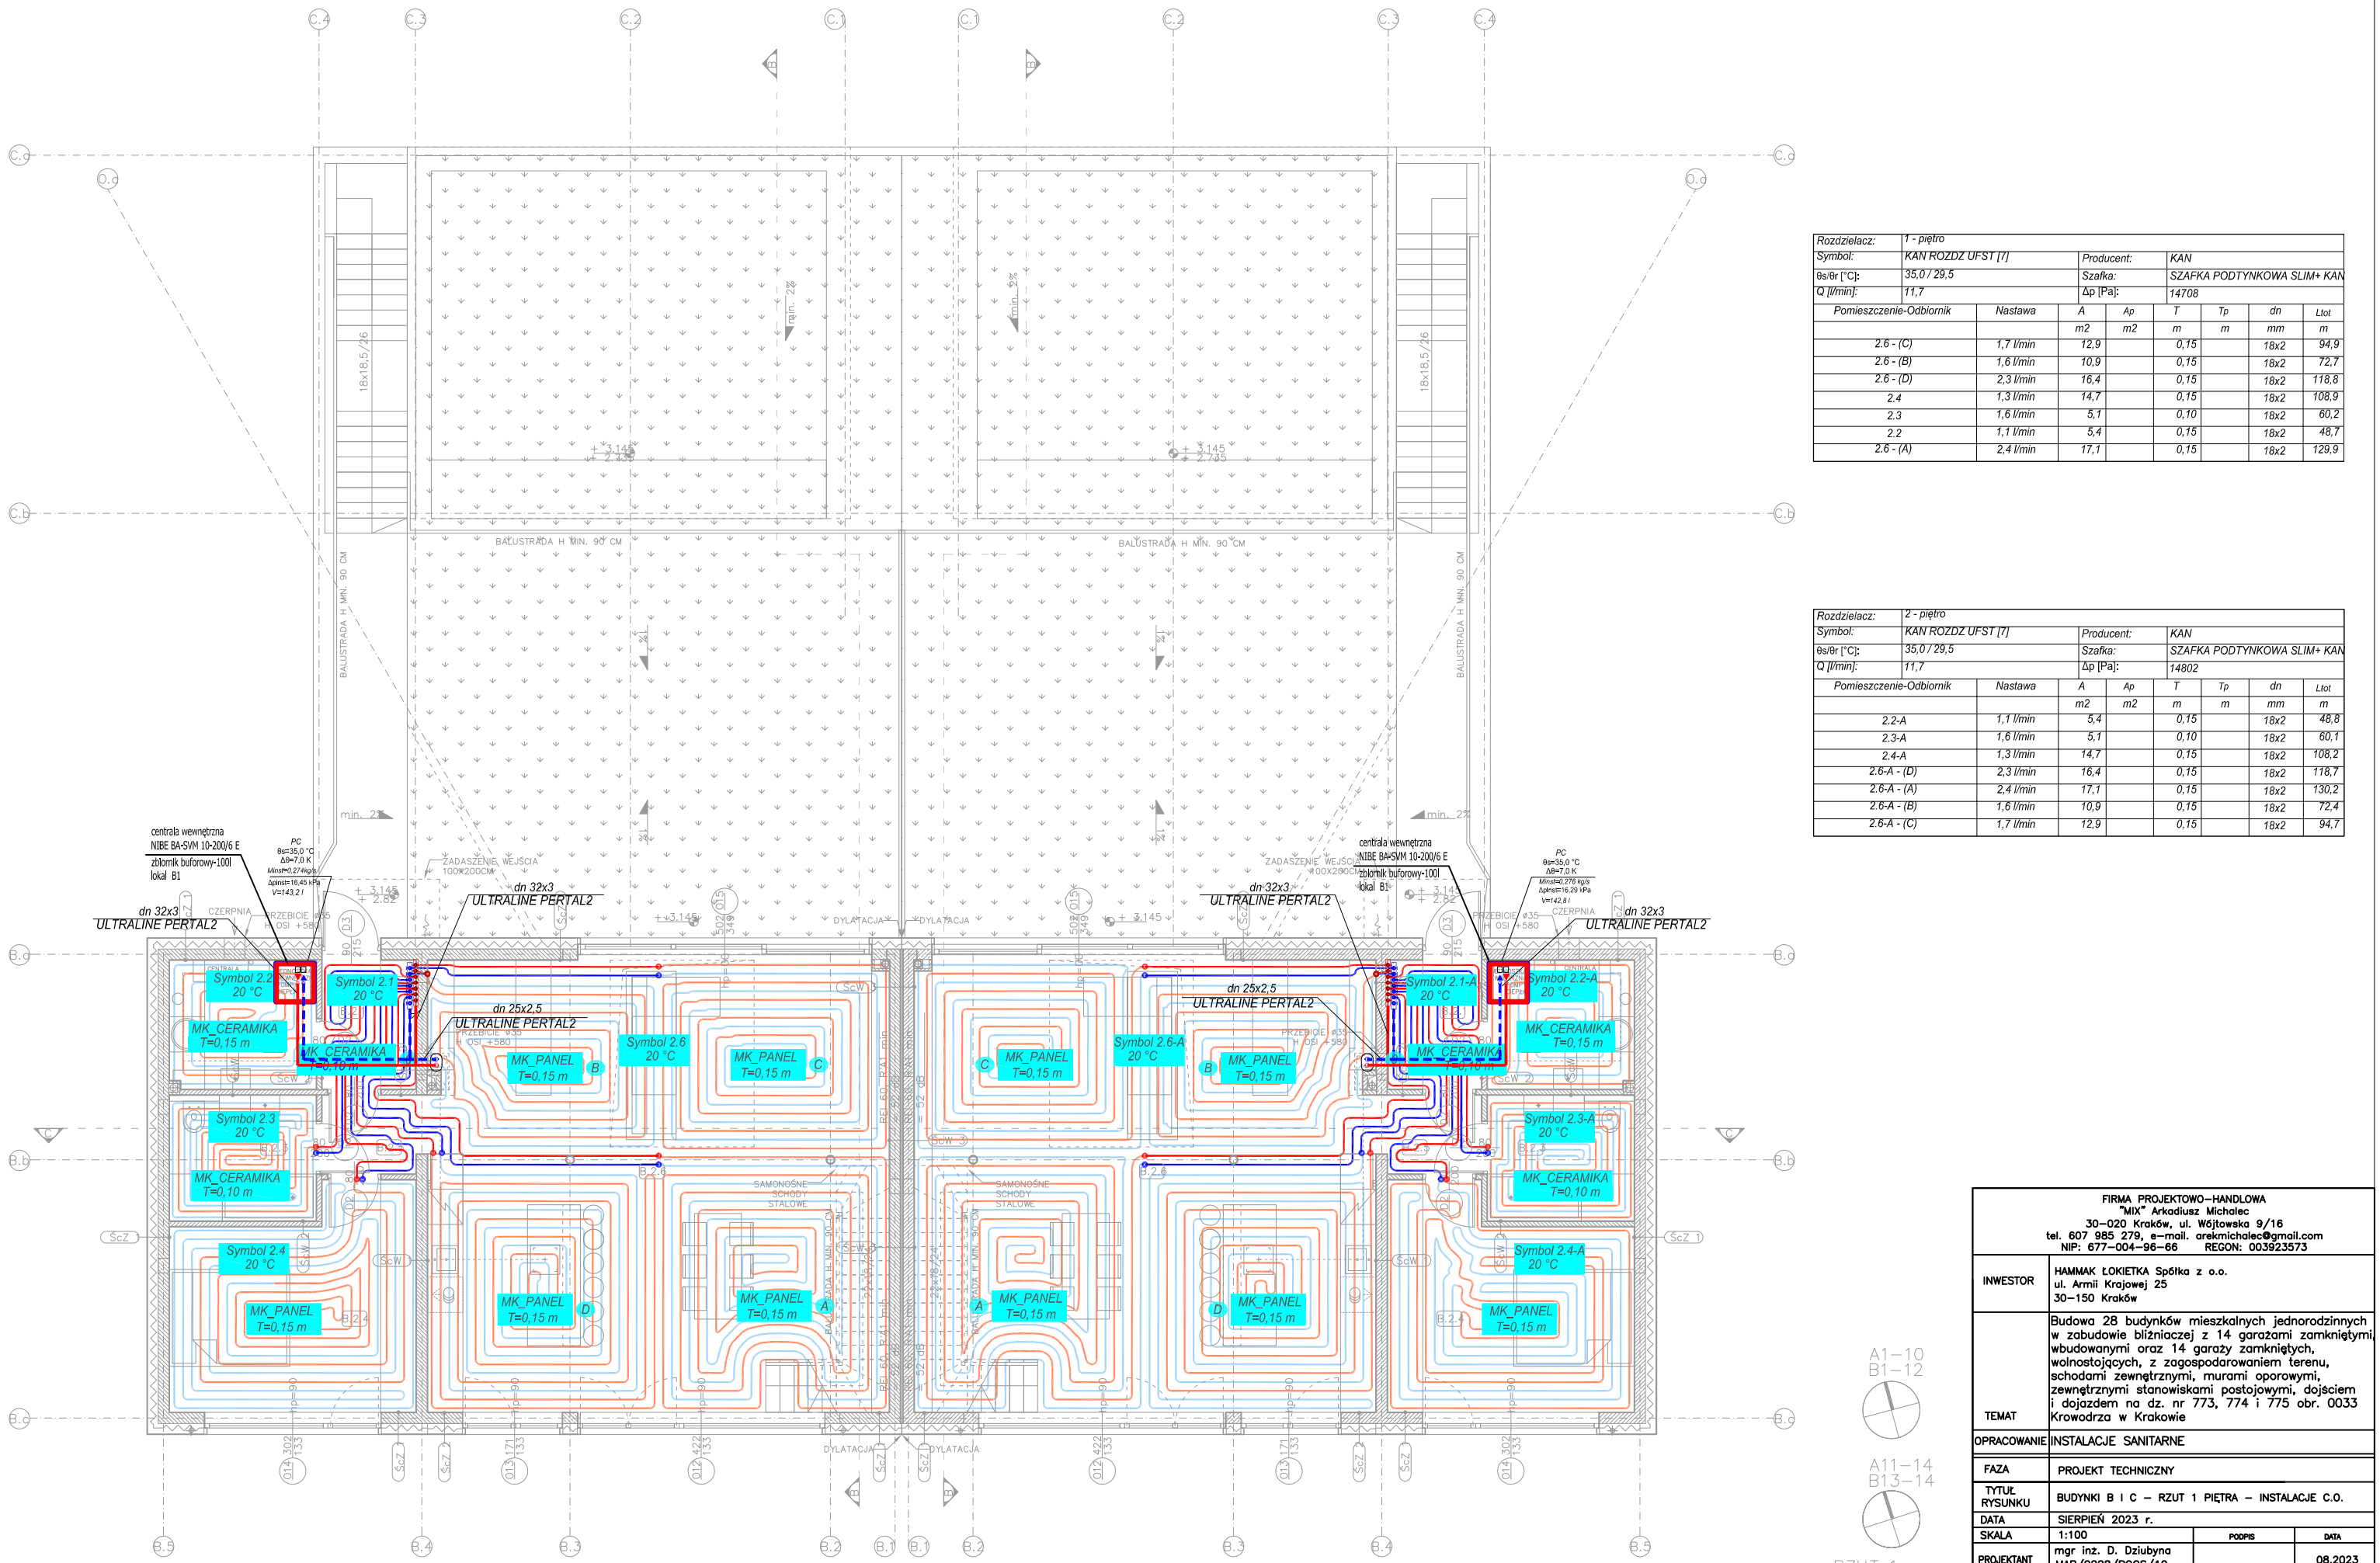


Rozdzielacz:	1 - piętro						
Symbol:	KAN ROZDZ UFST [7]	Producent:	KAN				
θs/θr [°C]:	35,0 / 29,5	Szafka:	SZAFKA PODTYNKOWA SLIM+ KAN				
Q [l/min]:	11,7	Δp [Pa]:	14708				

Pomieszczenie-Odbiornik	Nastawa	A	Ap	T	Tp	dn	Ltot
		m2	m2	m	m	mm	m
2.6 - (C)	1,7 l/min	12,9		0,15		18x2	94,9
2.6 - (B)	1,6 l/min	10,9		0,15		18x2	72,7
2.6 - (D)	2,3 l/min	16,4		0,15		18x2	118,8
2.4	1,3 l/min	14,7		0,15		18x2	108,9
2.3	1,6 l/min	5,1		0,10		18x2	60,2
2.2	1,1 l/min	5,4		0,15		18x2	48,7
2.6 - (A)	2,4 l/min	17,1		0,15		18x2	129,9

Rozdzielacz:	2 - piętro						
Symbol:	KAN ROZDZ UFST [7]	Producent:	KAN				
θs/θr [°C]:	35,0 / 29,5	Szafka:	SZAFKA PODTYNKOWA SLIM+ KAN				
Q [l/min]:	11,7	Δp [Pa]:	14802				

Pomieszczenie-Odbiornik	Nastawa	A	Ap	T	Tp	dn	Ltot
		m2	m2	m	m	mm	m
2.2-A	1,1 l/min	5,4		0,15		18x2	48,8
2.3-A	1,6 l/min	5,1		0,10		18x2	60,1
2.4-A	1,3 l/min	14,7		0,15		18x2	108,2
2.6-A - (D)	2,3 l/min	16,4		0,15		18x2	118,7
2.6-A - (A)	2,4 l/min	17,1		0,15		18x2	130,2
2.6-A - (B)	1,6 l/min	10,9		0,15		18x2	72,4
2.6-A - (C)	1,7 l/min	12,9		0,15		18x2	94,7

FIRMA PROJEKTOWO–HANDLOWA
"MIX" Arkadiusz Michalec
30–020 Kraków, ul. Wójtowska 9/16
tel. 607 985 279, e–mail. arekmichalec@gmail.com
NIP: 677–004–96–66 REGON: 003923573

INWESTOR	HAMMAK ŁOKIETKA Spółka z o.o. ul. Armii Krajowej 25 30–150 Kraków
TEMAT	Budowa 28 budynków mieszkalnych jednorodzinnych w zabudowie bliźniaczej z 14 garażami zamkniętymi, wbudowanymi oraz 14 garaży zamkniętych, wolnostojących, z zagospodarowaniem terenu, schodami zewnętrznymi, murami oporowymi, zewnętrznymi stanowiskami postojowymi, dojściem i dojazdem na dz. nr 773, 774 i 775 obr. 0033 Krowodrza w Krakowie
OPRACOWANIE	INSTALACJE SANITARNE
FAZA	PROJEKT TECHNICZNY
TYTUŁ RYSUNKU	BUDYNKI B I C – RZUT 1 PIĘTRA – INSTALACJE C.O.

DATA	SIERPIEŃ 2023 r.		
SKALA	1:100	PODPIS	DATA
PROJEKTANT	mgr inż. D. Dziubyna MAP/0228/POOS/10		08.2023
SPRAWDZAJĄCY	mgr inż. W. Cisowska MAP/0359/POOS/08		
WSPÓŁPRACA	mgr inż. A. Michalec		NR RYS. PT/IS–02.5