


RZUT 1 PIĘTRA

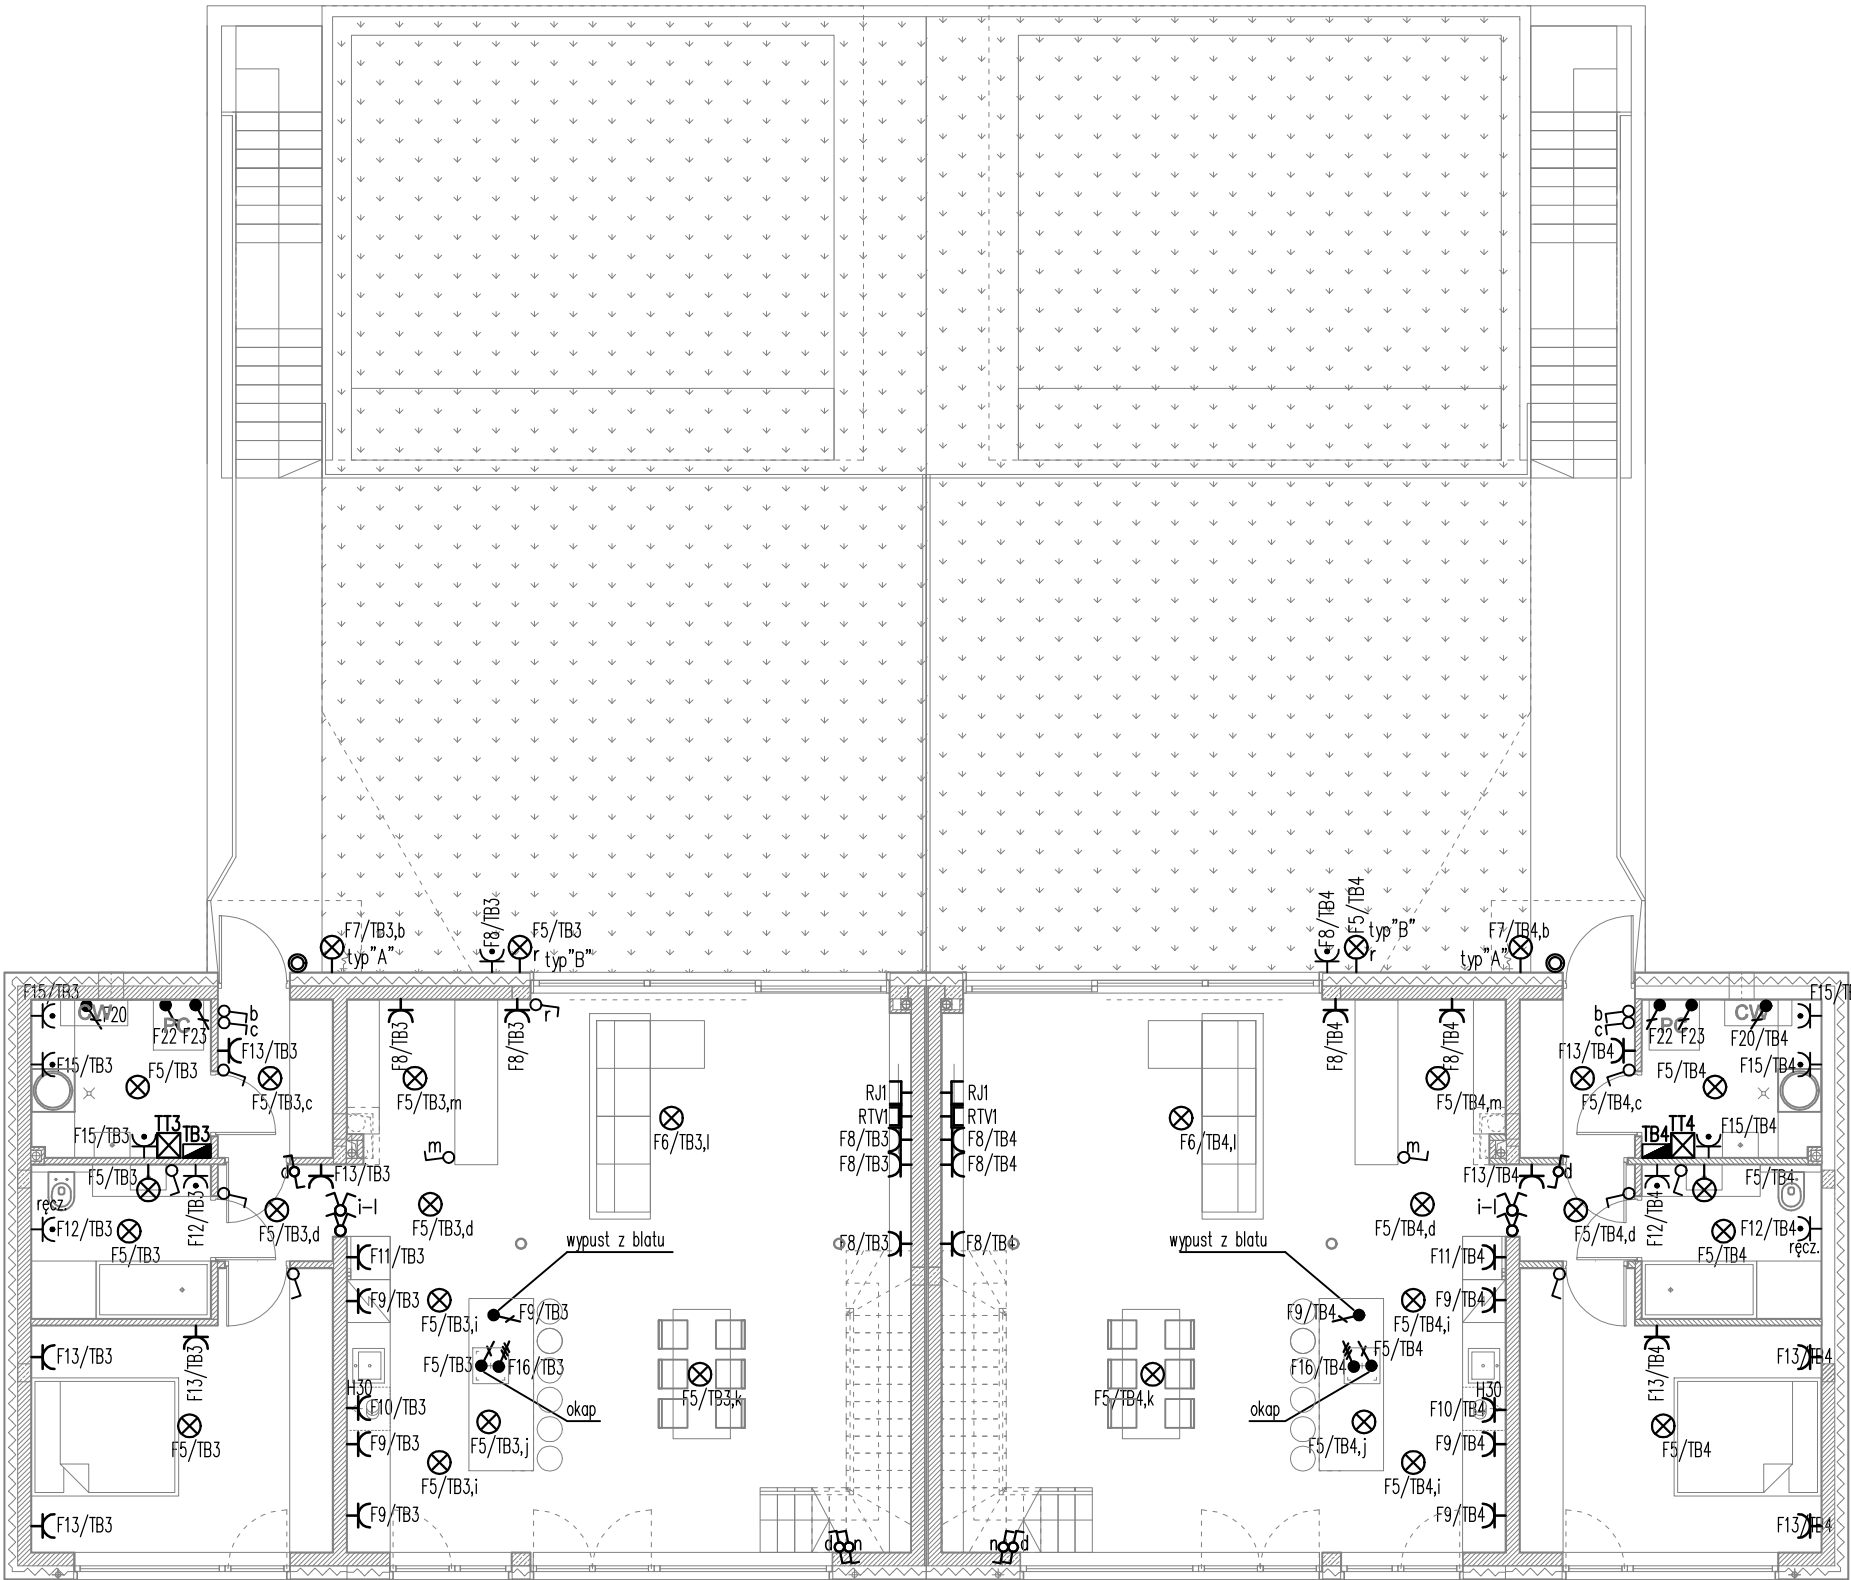

LEGENDA:

- tablica bezpiecznikowa
- TT - szafa teletechniczna
- łącznik podtynkowy klawiszowy pojedynczy, 10A, 230V
- łącznik podtynkowy klawiszowy świecznikowy, 10A, 230V
- łącznik podtynkowy klawiszowy schodowy, 10A, 230V
- wypust oświetleniowy P+N+PE, sufitowy
- wypust oświetleniowy P+N+PE, naścienny
- gniazdo 230V podtynkowe, 2P+Z/16A/230V, IP20
- gniazdo 230V podtynkowe, 2P+Z/16A/230V, IP44
- gniazdo trójfazowe, natynkowe, 3xL+N+PE/16A/400V
- gniazdo RTV
- gniazdo internet
- wypust trójfazowy, zasilanie kuchni elektr.
- złącze kontrolne instalacji odgromowej
- dzwonek 230V
- przycisk dzwonekowy
- typ "A" - zewnętrzny kinkiet biały, 2-punktowy, Czujnik ruchu, np. Lucide TAYLOR
- typ "B" - zewnętrzny kinkiet biały, 1-punktowy, np. Lucide TAYLOR
- typ "C" - reflektor wpuszczany 1-punktowy kolor czarny mat

NAZWA OBIEKTU BUDOWLANEGO
BUDOWA 28 BUDYNKÓW MIESZKALNYCH JEDNORODZINNYCH W
ZABUDOWIE BLIŹNIACZEJ Z 14 GARAŻAMI ZAMKNIĘTymi, WBUDOWANYMI
ORAZ 14 GARAŻY ZAMKNIĘTYCH, WOLNOSTOJĄCYCH, Z
ZAGOSPODAROWANIEM TERENU, SCHODAMI ZEWNĘTRZNYMI, MURAMI
OPOROWYMI, ZEWNĘTRZNYMI STANOWISKAMI POSTOJOWYMI, DOJŚCIEM I
DOJAZDEM.

PROJEKTANT PAWEŁ PAWŁOWSKI	NR UPRAWNIEŃ SWK/PWOE/0099/12
-------------------------------	----------------------------------

TYTUŁ RYSUNKU
PLAN INSTALACJI ELEKTRYCZNYCH - 1 PIĘTRO. BUDYNEK B I C

ELEMENT PROJEKTU PROJEKT TECHNICZNY		NUMER RYSUNKU E10
BRANŻA ELEKTRYCZNA		
DATA 01.2023	SKALA 1:100	