


RZUT 2 PIETRA

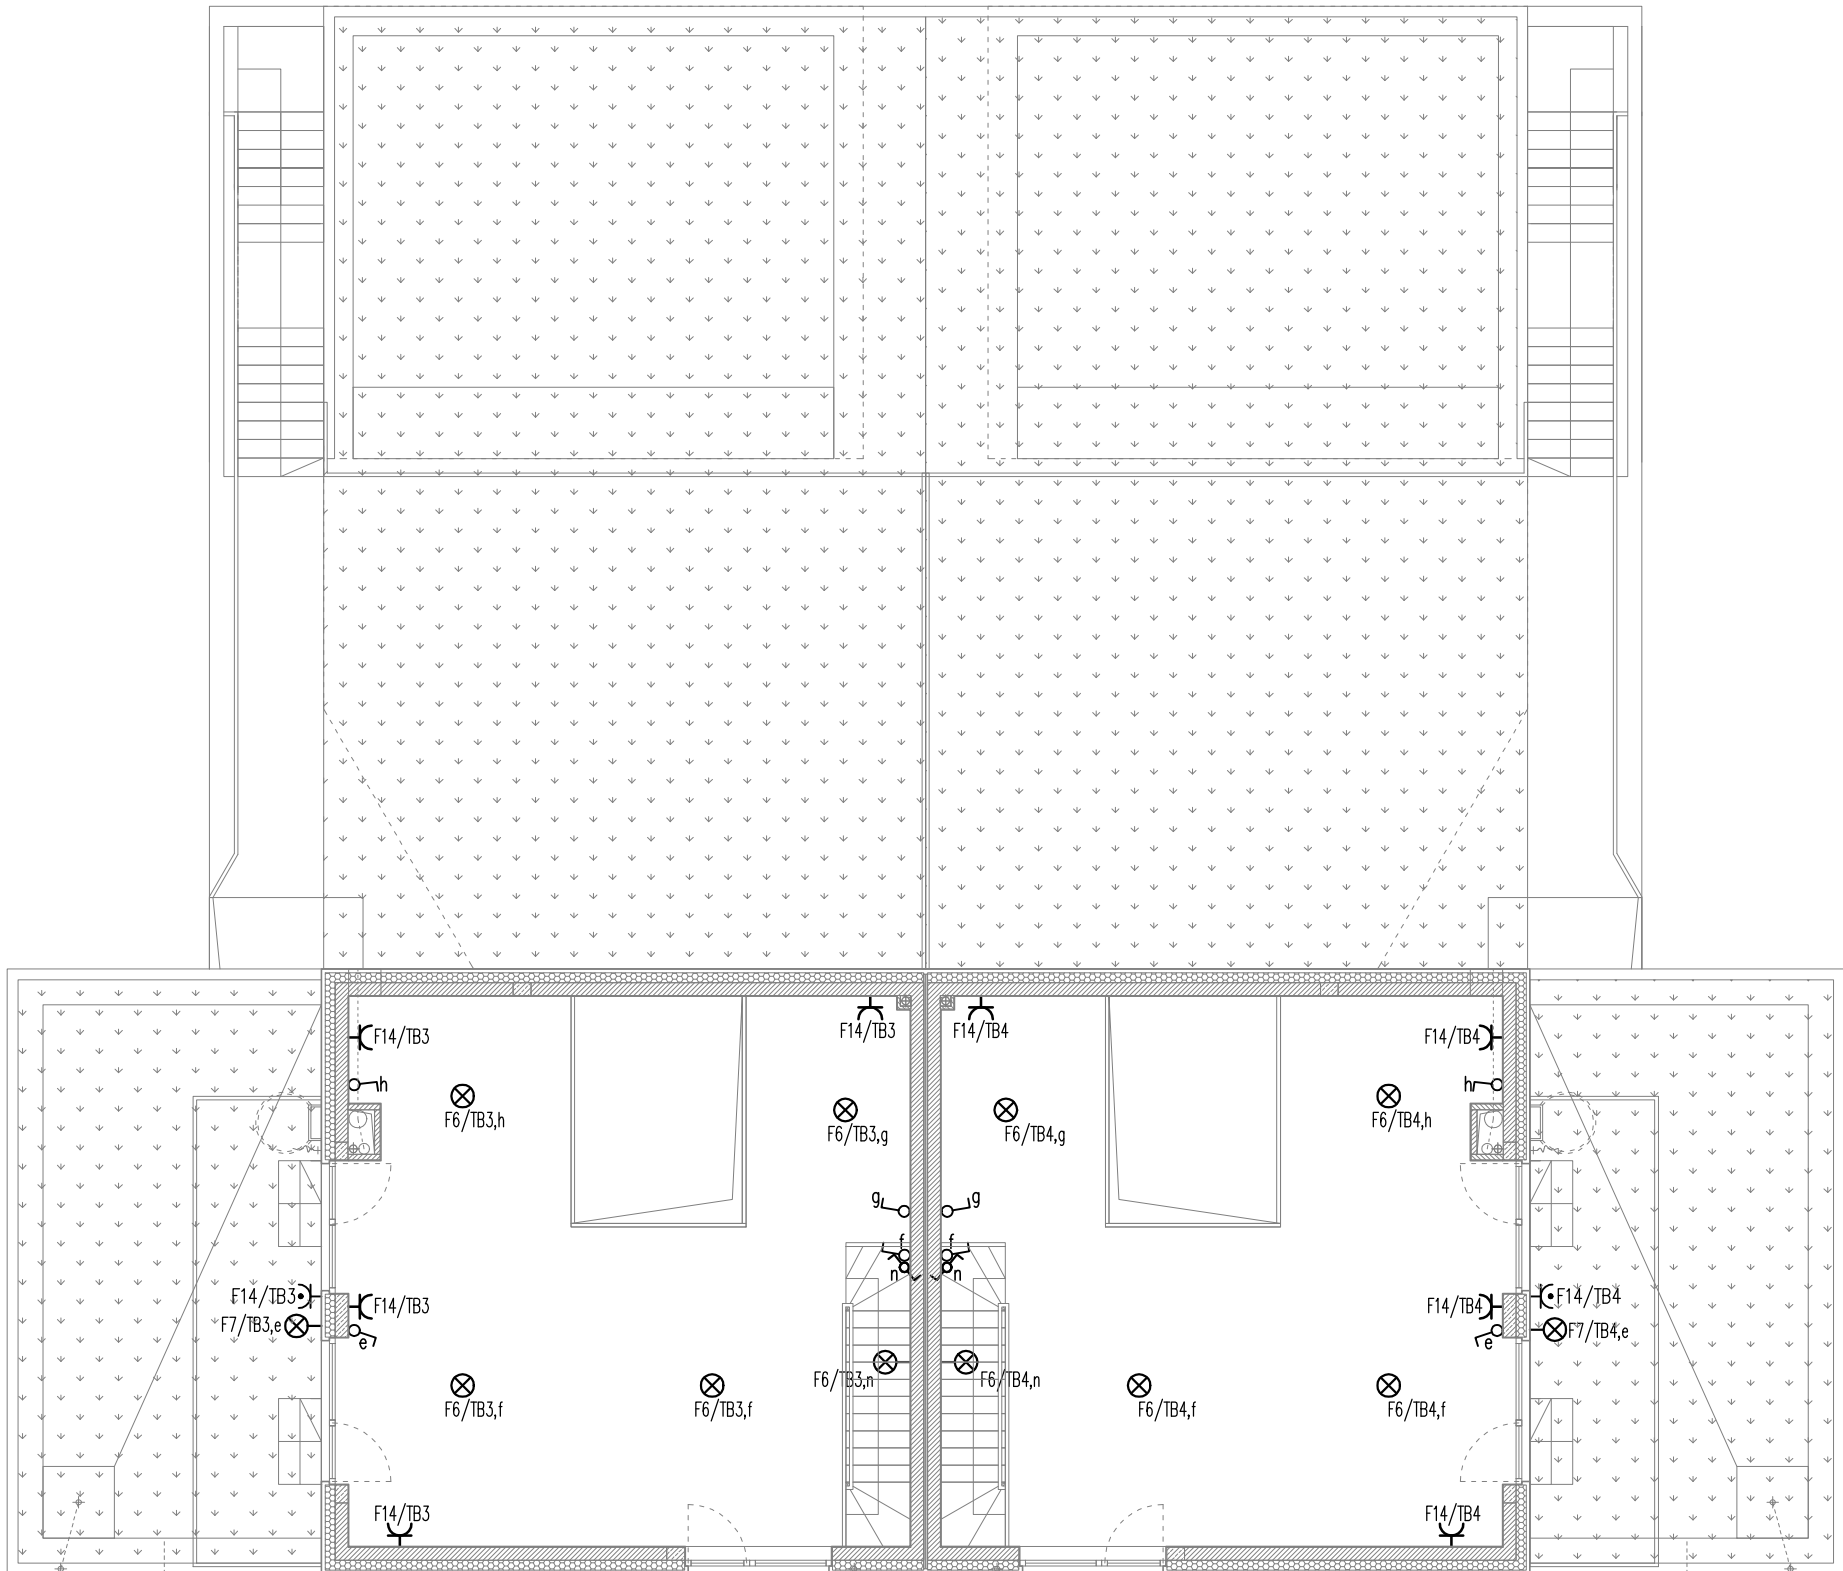

LEGENDA:

-  - tablica bezpiecznikowa
-  - łącznik podtynkowy klawiszowy pojedynczy, 10A, 230V
-  - łącznik podtynkowy klawiszowy świecznikowy, 10A, 230V
-  - łącznik podtynkowy klawiszowy schodowy, 10A, 230V
-  - wypust oświetleniowy P+N+PE, sufitowy
-  - wypust oświetleniowy P+N+PE, ścienny
-  - gniazdo 230V podtynkowe, 2P+Z/16A/230V, IP20
-  - gniazdo 230V podtynkowe, 2P+Z/16A/230V, IP44
-  - gniazdo trójfazowe, natynkowe, 3xL+N+PE/16A/400V
-  - gniazdo RTV
-  - gniazdo internet
-  - wypust trójfazowy, zasilanie kuchni elektr.
-  - złaczce kontrolne instalacji odgromowej
-  - dzwonek 230V
-  - przycisk dzwonkowy
-  - zewnętrzny kinkiet biały, 2-punktowy, Czujnik ruchu, np. Lucide TAYLOR
-  - zewnętrzny kinkiet biały, 1-punktowy, np. Lucide TAYLOR
-  - reflektor wpuszczany 1-punktowy kolor czarny mat

NAZWA OBIEKTU BUDOWLANEGO
BUDOWA 28 BUDYNKÓW MIESZKALNYCH JEDNORODZINNYCH W
ZABUDOWIE BLIŹNIACZEJ Z 14 GARAŻAMI ZAMKNIĘTYMI, WBUDOWANYMI
ORAZ 14 GARAŻY ZAMKNIĘTYCH, WOLNOSTOJĄCYCH, Z
ZAGOSPODAROWANIEM TERENU, SCHODAMI ZEWNĘTRZNYMI, MURAMI
OPOROWYMI, ZEWNĘTRZNYMI STANOWISKAMI POSTOJOWYMI, DOJŚCIEM
DOJAZDEM.

PROJEKTANT	NR UPRAWNIEŃ
PAWEŁ PAWŁOWSKI	SWK/PW0E/0099/12

TYTUŁ RYSUNKU

PLAN INSTALACJI ELEKTRYCZNYCH - 2 PIĘTRO. BUDYNEK B I C

ELEMENT PROJEKTU
PROJEKT TECHNICZNY

BRANŻA
ELEKTRYCZNA

DATA	01.2023
------	---------

NUMER RYSUNKU

E11