


RZUT DACHU

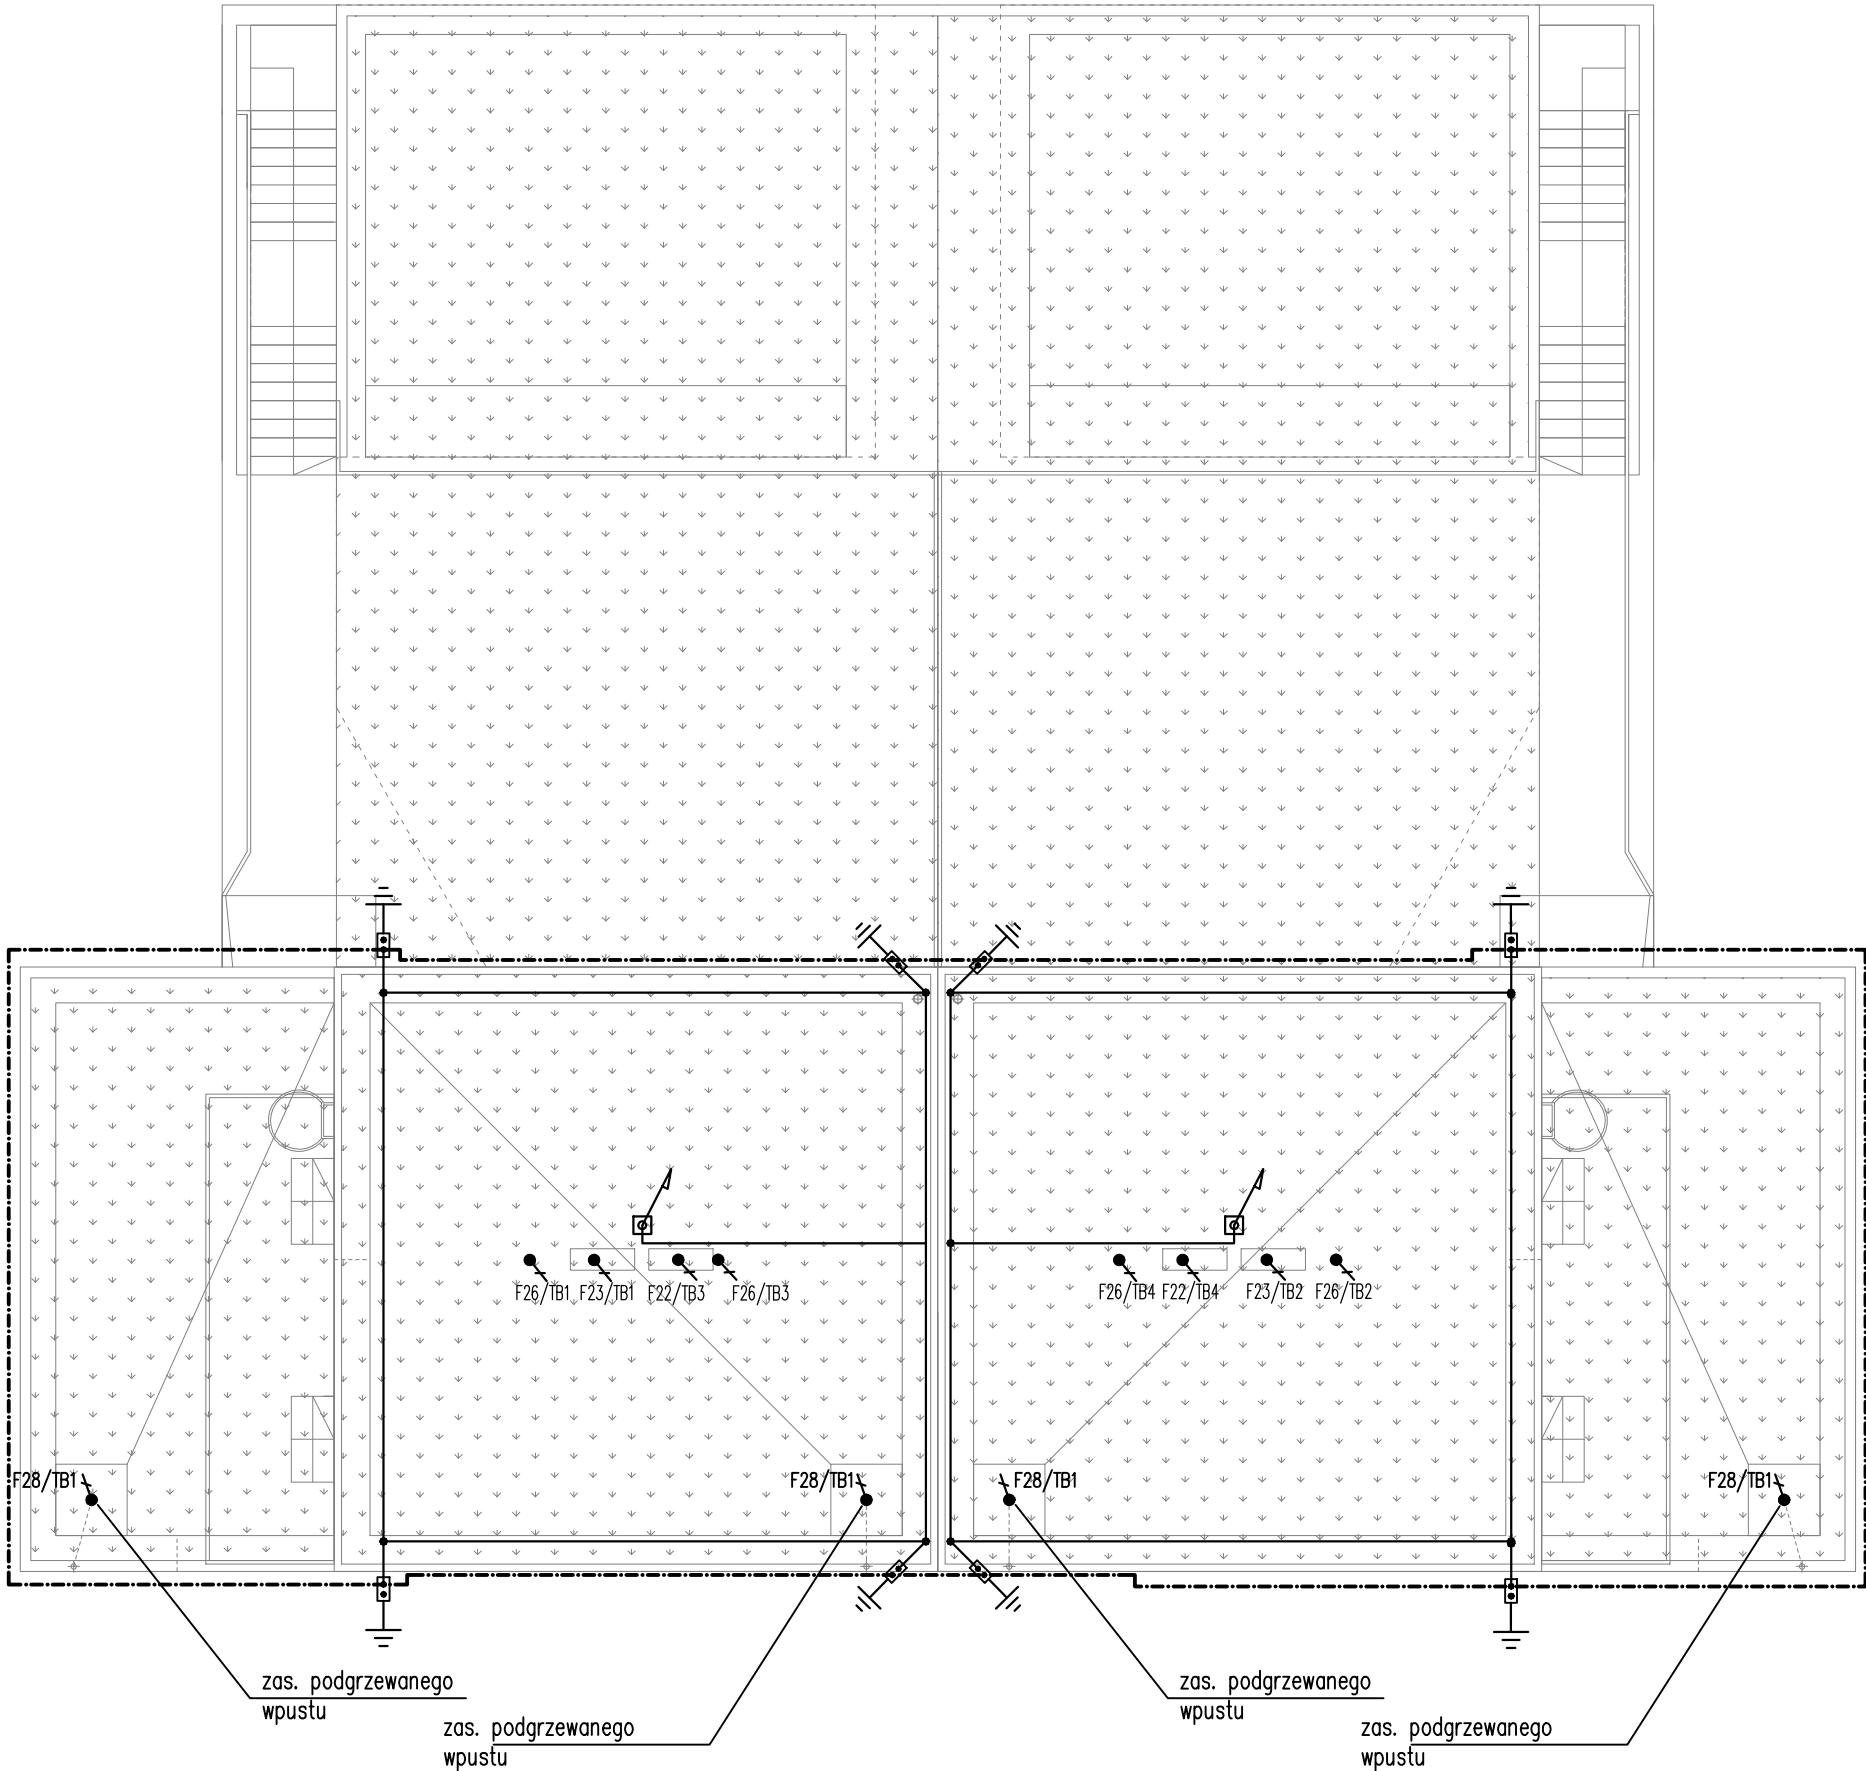

LEGENDA

- Drut instalacji odgromowej ze drutu FeZn Ø8mm
- Uziom otokowy, bednarka 40x5mm
- ⊞ Złącze kontrolne pomiarowe
- ° Zacisk krzyżowy
- ⊞ Maszt odgromowy H=2m

- UWAGI:
1. Instalację odgromową należy wykonać z wykorzystaniem drutu FeZn Ø8mm.
 2. Złącza kontrolne należy montować na wysokości 0,5m nad poziomem terenu.
 3. Przewody odprowadzające należy wykonać z wykorzystaniem drutu FeZn Ø8mm.
 4. Przewody uziemiające należy wykonać z wykorzystaniem bednarki ocynkowanej 40x3mm.
 5. metalowe elementy na dachu należy przyłączyć do instalacji odgromowej.

NAZWA OBIEKTU BUDOWLANEGO
BUDOWA 28 BUDYNKÓW MIESZKALNYCH JEDNORODZINNYCH W ZABUDOWIE BLIŹNIACZEJ Z 14 GARAŻAMI ZAMKNIĘTAMI, WBUDOWANYMI ORAZ 14 GARAŻY ZAMKNIĘTYCH, WOLNOSTOJĄCYCH, Z ZAGOSPODAROWANIEM TERENU, SCHODAMI ZEWNĘTRZNYMI, MURAMI OPOROWYMI, ZEWNĘTRZNYMI STANOWISKAMI POSTOJOWYMI, DOJŚCIEM I DOJAZDEM.

PROJEKTANT
PAWEŁ PAWŁOWSKI

NR UPRAWNIEŃ
SWK/PW0E/0099/12

TYTUŁ RYSUNKU
PLAN INSTALACJI ODGORMOWEJ. BUDYNEK B I C

ELEMENT PROJEKTU
PROJEKT TECHNICZNY

BRANŻA
ELEKTRYCZNA

DATA
01.2023

SKALA
1:100

NUMER RYSUNKU

E12