




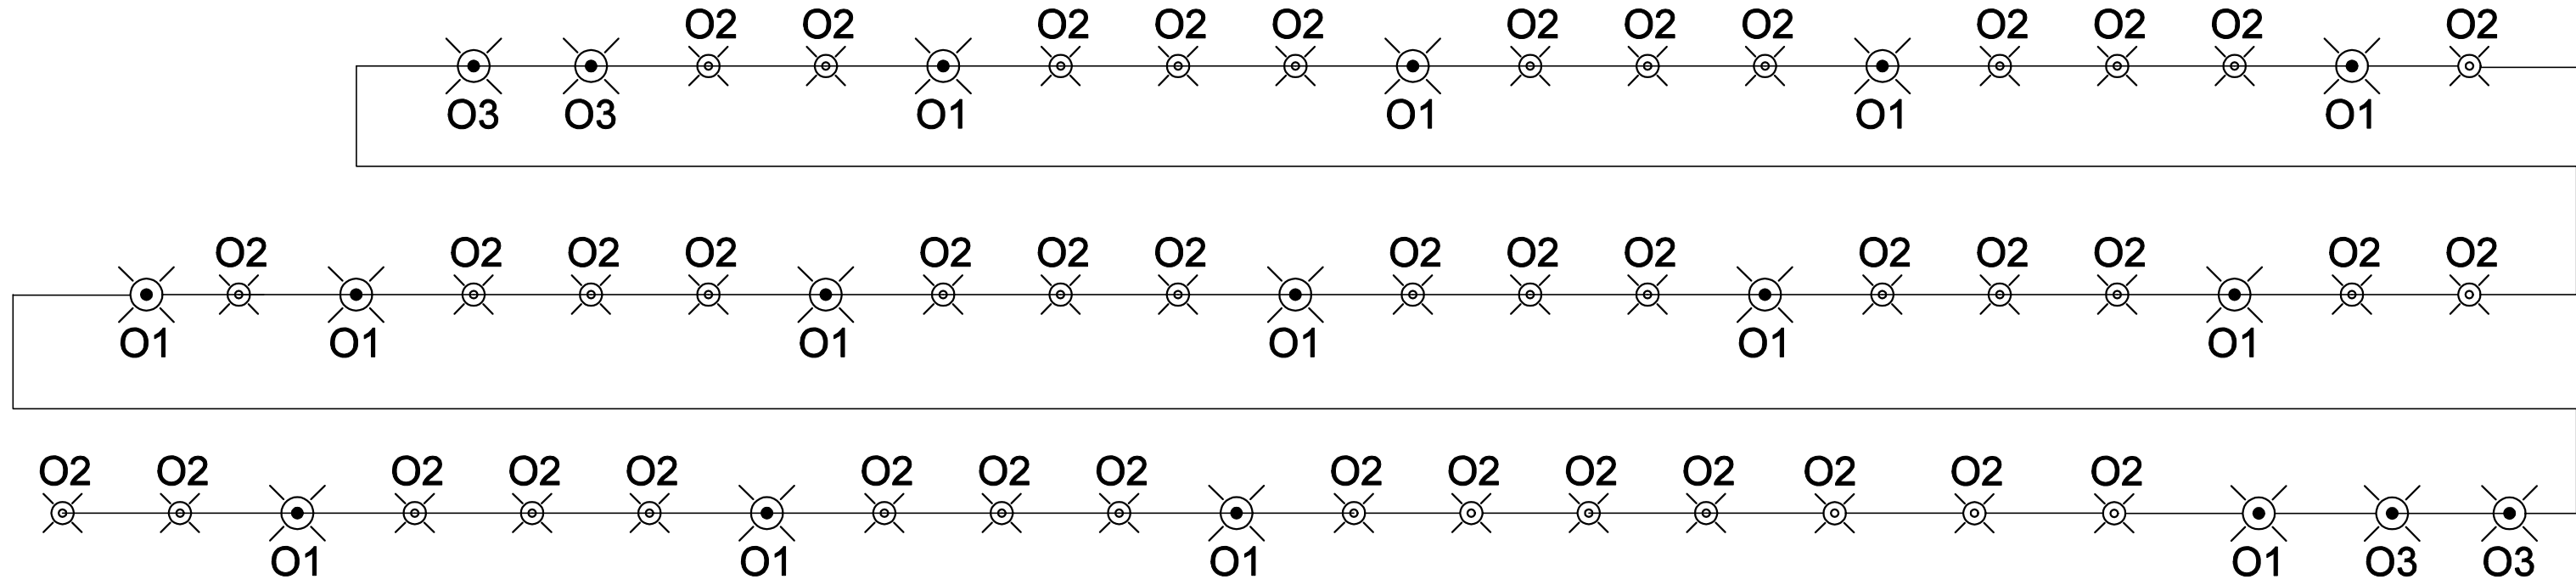


TA

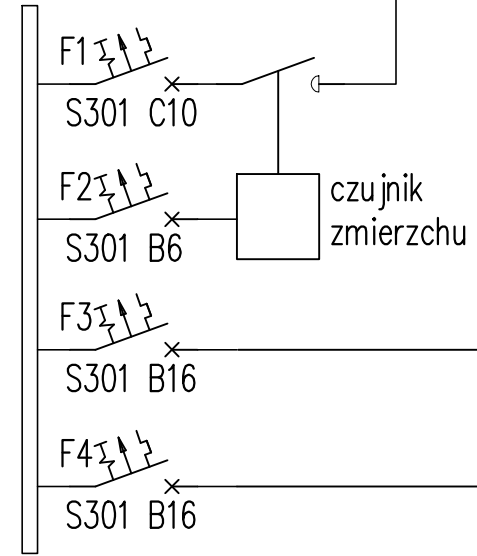

YKY 3x6mm²

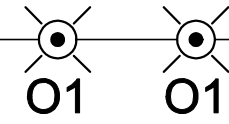

YKY 3x4mm²

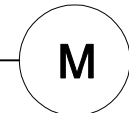

Szlaban

PWO



Przepompownia
wód opadowych

NAZWA OBIEKTU BUDOWLANEGO BUDOWA 28 BUDYNKÓW MIESZKALNYCH JEDNORODZINNYCH W ZABUDOWIE BLIŹNIACZEJ Z 14 GARAŻAMI ZAMKNIĘTYMI, WBUROWANYMI ORAZ 14 GARAŻY ZAMKNIĘTYCH, WOLNOSTOJĄCYCH, Z ZAGOSPODAROWANIEM TERENU, SCHODAMI ZEWNĘTRZNYMI, MURAMI OPOROWYMI, ZEWNĘTRZNYMI STANOWISKAMI POSTOJOWYMI, DOJŚCIEM I DOJAZDEM.			
PROJEKTANT PAWEŁ PAWŁOWSKI		NR UPRAWNIEN SWK/PWOE/0099/12	
TYTUŁ RYSUNKU SCHEMAT INSTALACJI ELEKTRYCZNYCH ZEWNĘTRZNYCH			
ELEMENT PROJEKTU PROJEKT TECHNICZNY			NUMER RYSUNKU E2
BRANŻA ELEKTRYCZNA			
DATA 01.2023		SKALA 1:500	