


RZUT PARTERU

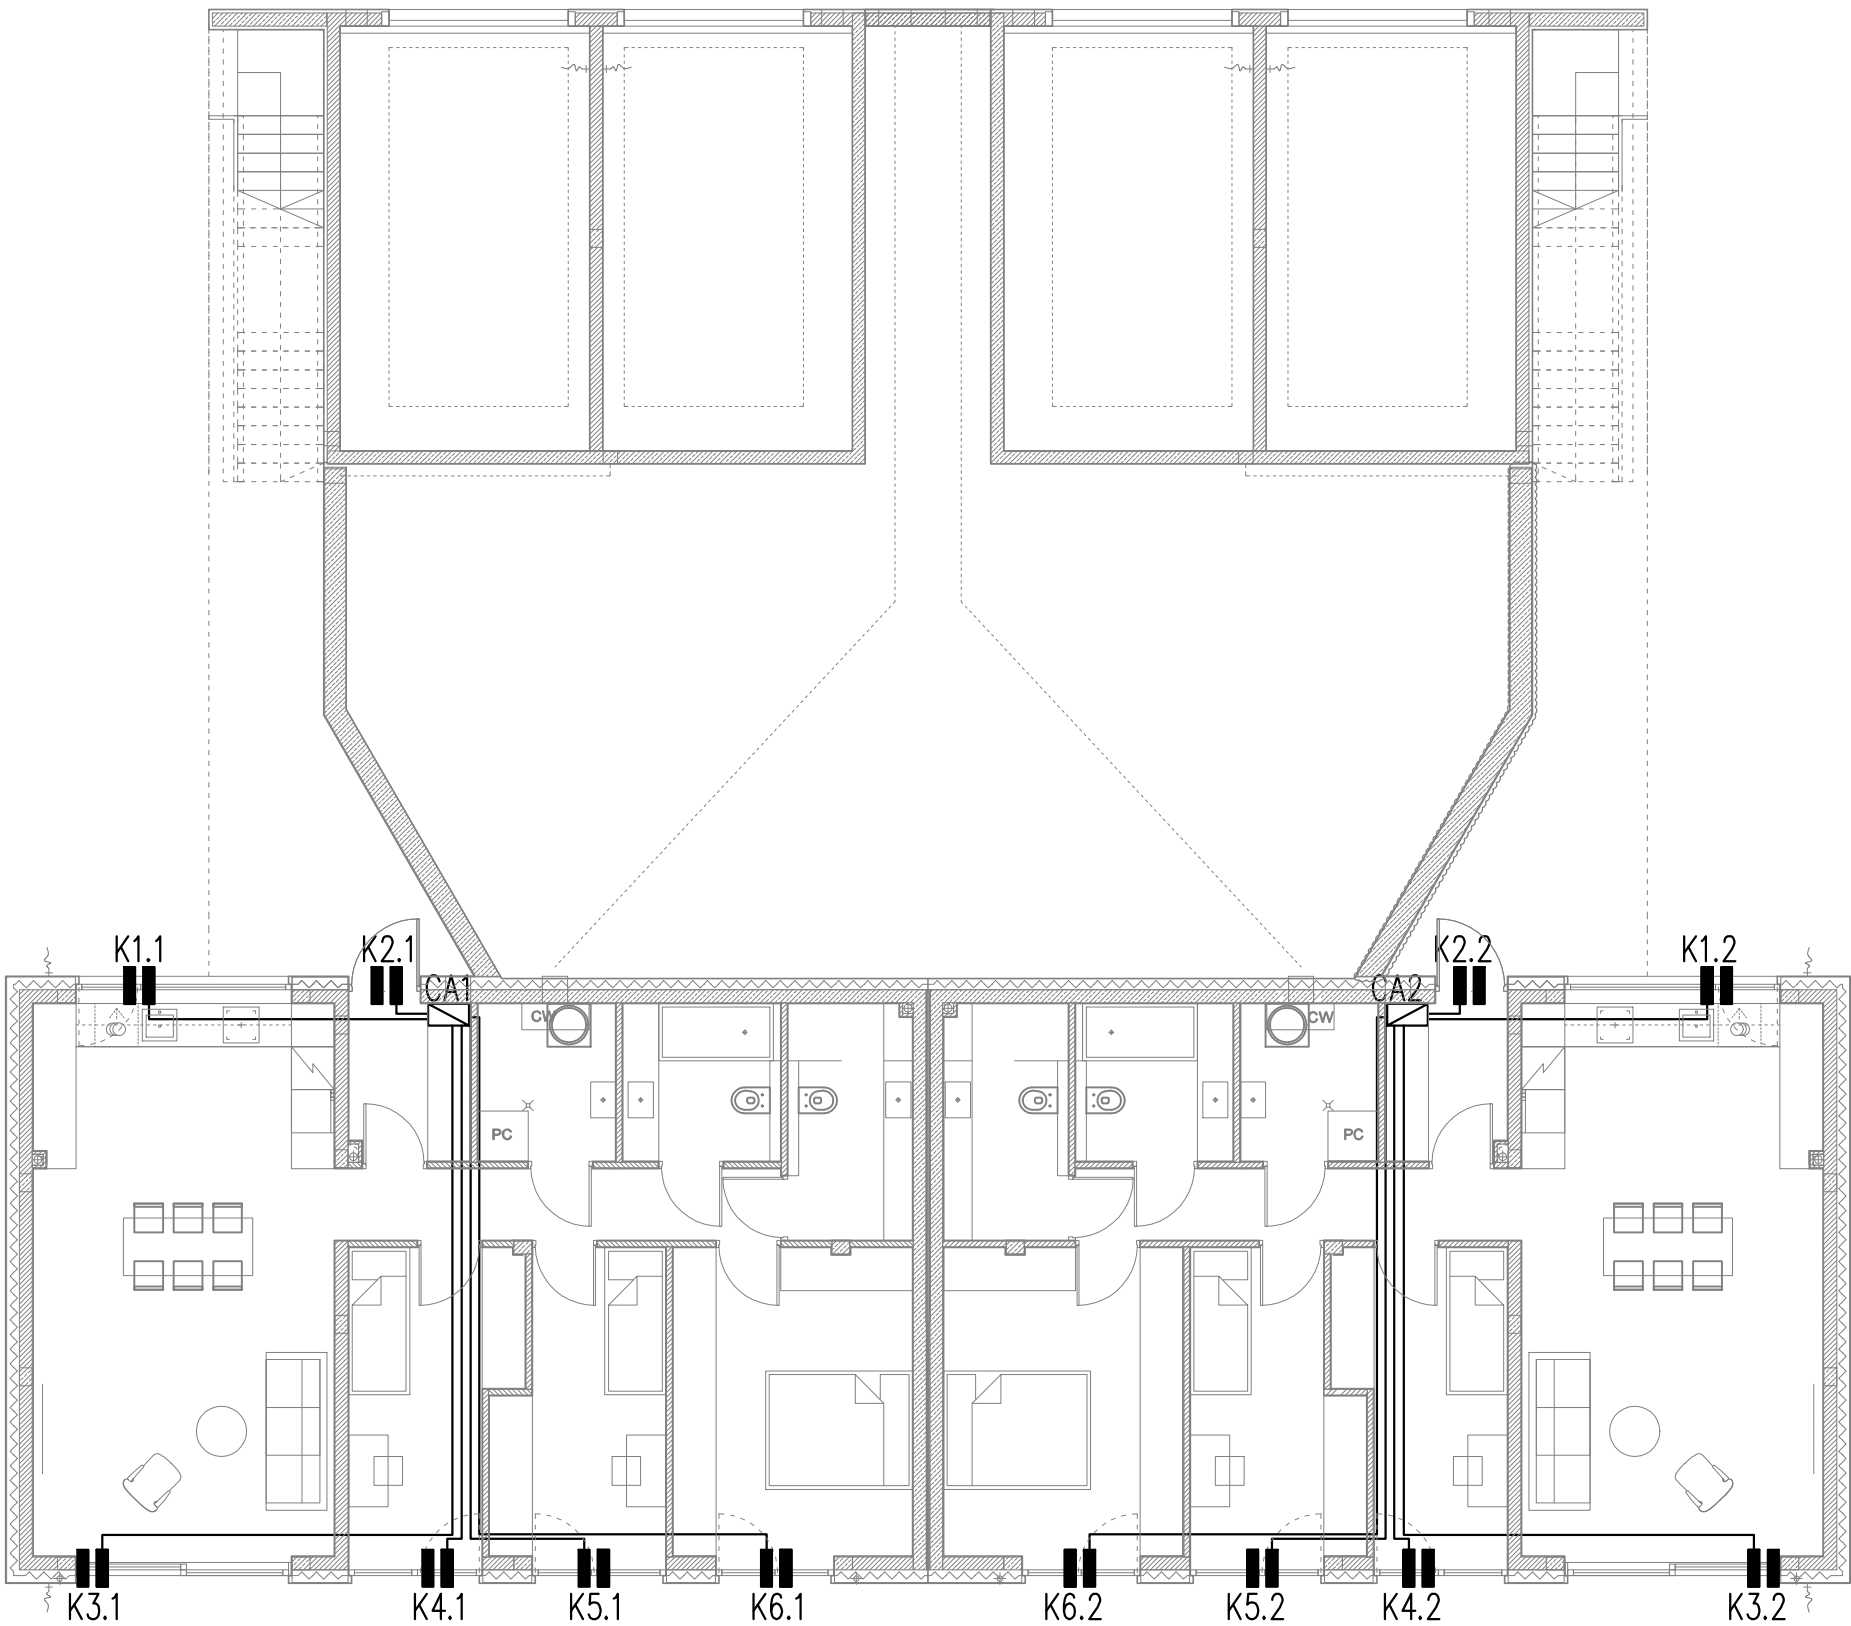

UWAGA:

- Okablowanie od lokalizacji centrali alarmowej do kontaktronów wykonać z wykorzystaniem przewodów typu YTDY 4x0,5mm.
- Stosować połączenia w gwiazdę, to dla każdego kontaktronu należy ułożyć odrębny przewód.

LEGENDA:

- – kontaktron (wypożyczenie drzwi i okien)
- CA – lokalizacja centrali alarmowej (centrala poza zakresem projektu)

NAZWA OBIEKTU BUDOWLANEGO  
BUDOWA 28 BUDYNKÓW MIESZKALNYCH JEDNORODZINNYCH W  
ZABUDOWIE BLIŹNIACZEJ Z 14 GARAŻAMI ZAMKNIĘTYMI, WBUDOWANYMI  
ORAZ 14 GARAŻY ZAMKNIĘTYCH, WOLNOSTOJĄCYCH, Z  
ZAGOSPODAROWANIEM TERENU, SCHODAMI ZEWNĘTRZNYMI, MURAMI  
OPOROWYMI, ZEWNĘTRZNYMI STANOWISKAMI POSTOJOWYMI, DOJŚCIEM I  
DOJAZDEM.

|                               |                                  |
|-------------------------------|----------------------------------|
| PROJEKTANT<br>PAWEŁ PAWŁOWSKI | NR UPRAWNIEŃ<br>SWK/PW0E/0099/12 |
|-------------------------------|----------------------------------|

|                                                                  |
|------------------------------------------------------------------|
| TYTUŁ RYSUNKU<br>PLAN INSTALACJI KONTAKTRONÓW - PARTER BUDYNEK B |
|------------------------------------------------------------------|

|                                        |                             |
|----------------------------------------|-----------------------------|
| ELEMENT PROJEKTU<br>PROJEKT TECHNICZNY | NUMER RYSUNKU<br><b>EK4</b> |
| BRANŻA<br>ELEKTRYCZNA                  |                             |
| DATA<br>01.2023                        |                             |
| SKALA<br>1:100                         |                             |