


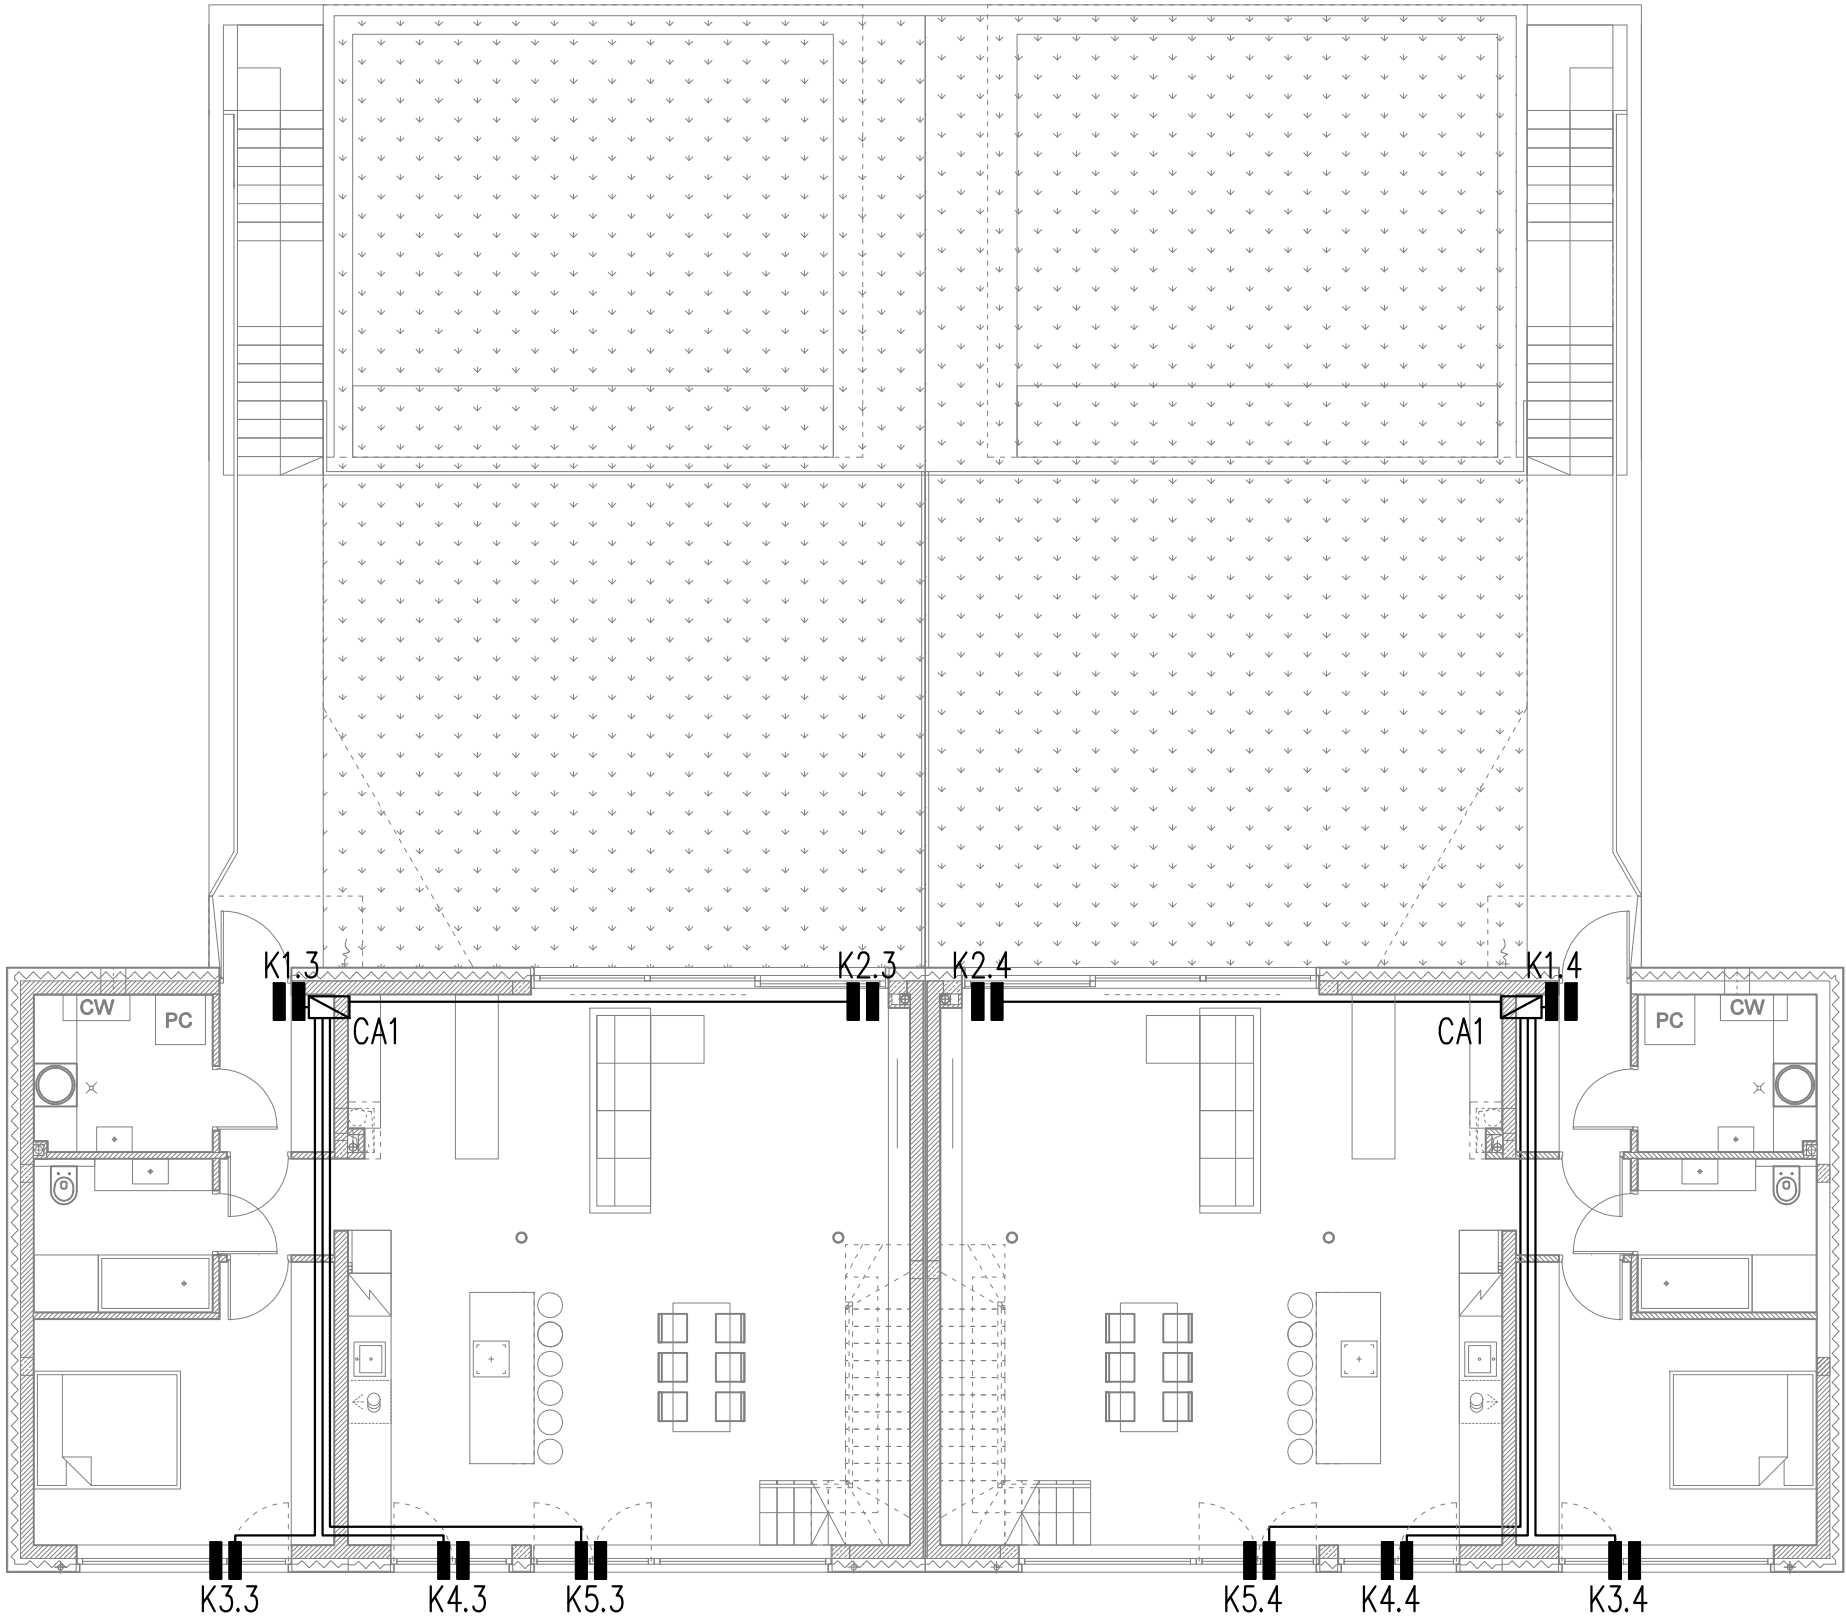

UWAGA:

- 1. Okablowanie od lokalizacji centrali alarmowej do kontaktronów wykonać z wykorzystaniem przewodów typu YTDY 4x0,5mm.
- 2. Stosować połączenia w gwiazdę, to dla każdego kontaktronu należy ułożyć odrębny przewód.

LEGENDA:

- – kontaktron (wyposażenie drzwi i okien)
- CA – lokalizacja centrali alarmowej (centrala poza zakresem projektu)

NAZWA OBIEKTU BUDOWLANEGO BUDOWA 28 BUDYNKÓW MIESZKALNYCH JEDNORODZINNYCH W ZABUDOWIE BLIŹNIACZEJ Z 14 GARAŻAMI ZAMKNIĘTYMI, WBUDOWANYMI ORAZ 14 GARAŻY ZAMKNIĘTYCH, WOLNOSTOJĄCYCH, Z ZAGOSPODAROWANIEM TERENU, SCHODAMI ZEWNĘTRZNYMI, MURAMI OPOROWYMI, ZEWNĘTRZNYMI STANOWISKAMI POSTOJOWYMI, DOJŚCIEM I DOJAZDEM.			
PROJEKTANT PAWEŁ PAWŁOWSKI		NR UPRAWNIEN SWK/PW0E/0099/12	
TYTUŁ RYSUNKU PLAN INSTALACJI KONTAKTRONÓW - 1 PIĘTRO BUDYNEK B			
ELEMENT PROJEKTU PROJEKT TECHNICZNY			NUMER RYSUNKU EK5
BRANŻA ELEKTRYCZNA			
DATA 01.2023		SKALA 1:100	