


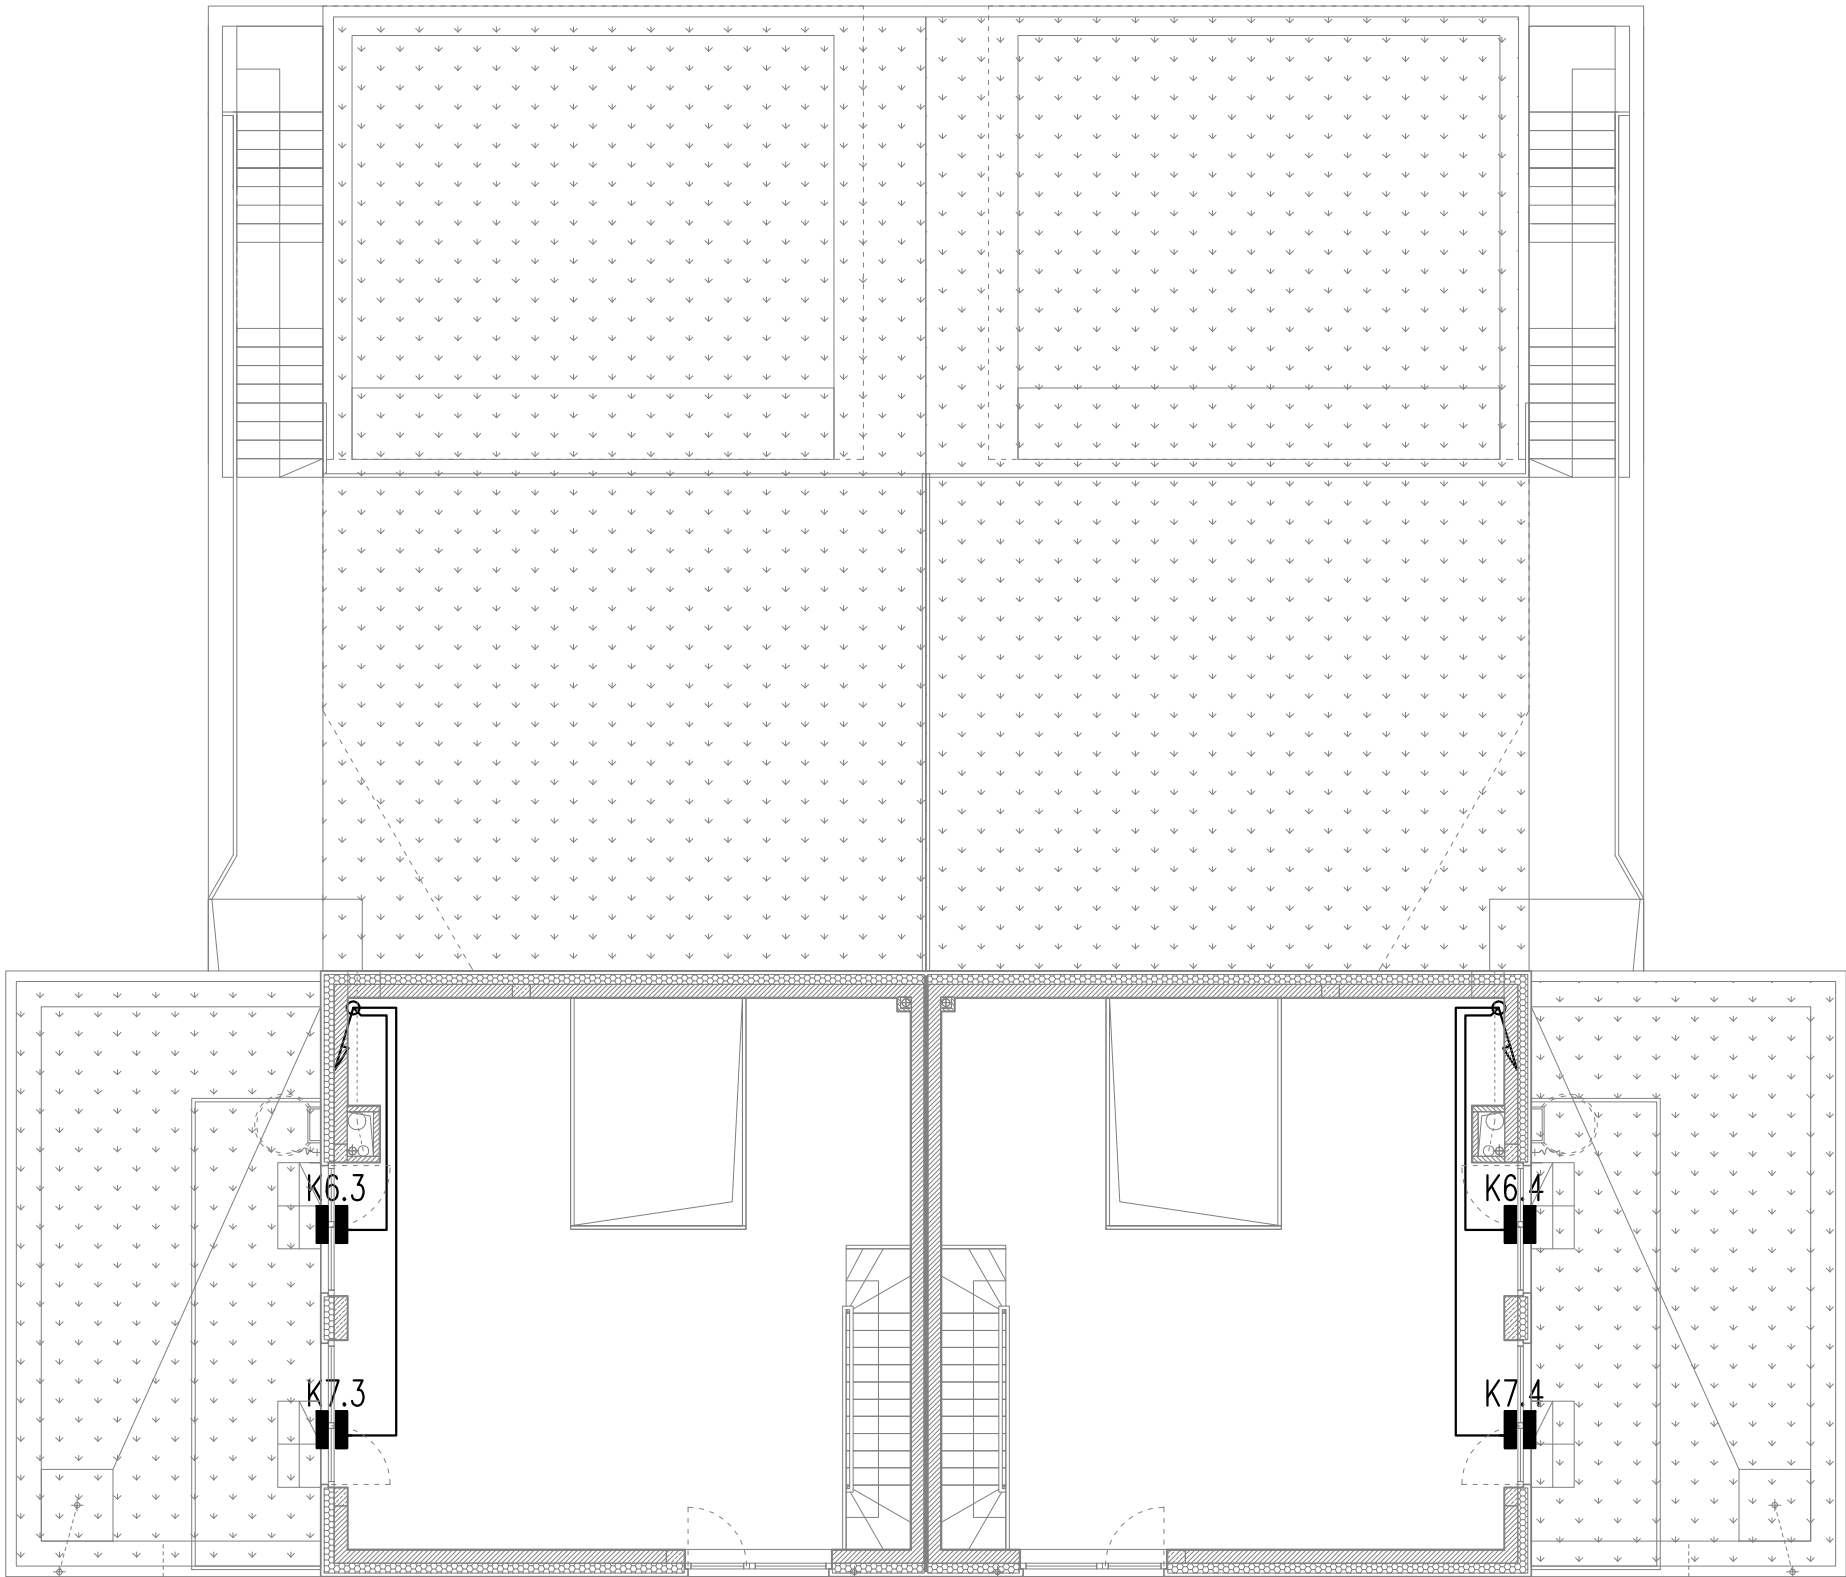

UWAGA:

- Okablowanie od lokalizacji centrali alarmowej do kontaktronów wykonać z wykorzystaniem przewodów typu YTDY 4x0,5mm.
- Stosować połączenia w gwiazdę, to dla każdego kontaktronu należy ułożyć odrębny przewód.

LEGENDA:

- – kontaktron (wyposażenie drzwi i okien)
- CA – lokalizacja centrali alarmowej (centrala poza zakresem projektu)

NAZWA OBIEKTU BUDOWLANEGO
BUDOWA 28 BUDYNKÓW MIESZKALNYCH JEDNORODZINNYCH W
ZABUDOWIE BLIŹNIACZEJ Z 14 GARAŻAMI ZAMKNIĘTYMI, WBUDOWANYMI
ORAZ 14 GARAŻY ZAMKNIĘTYCH, WOLNOSTOJĄCYCH, Z
ZAGOSPODAROWANIEM TERENU, SCHODAMI ZEWNĘTRZNYMI, MURAMI
OPOROWYMI, ZEWNĘTRZNYMI STANOWISKAMI POSTOJOWYMI, DOJŚCIEM I
DOJAZDEM.

PROJEKTANT PAWEŁ PAWŁOWSKI	NR UPRAWNIEN SWK/PWOE/0099/12
-------------------------------	----------------------------------

TYTUŁ RYSUNKU PLAN INSTALACJI KONTAKTRONÓW - 2 PIĘTRO BUDYNEK C
--

ELEMENT PROJEKTU PROJEKT TECHNICZNY	NUMER RYSUNKU
--	---------------

BRANŻA ELEKTRYCZNA	EK6
-----------------------	-----

DATA 01.2023	SKALA 1:100
-----------------	----------------