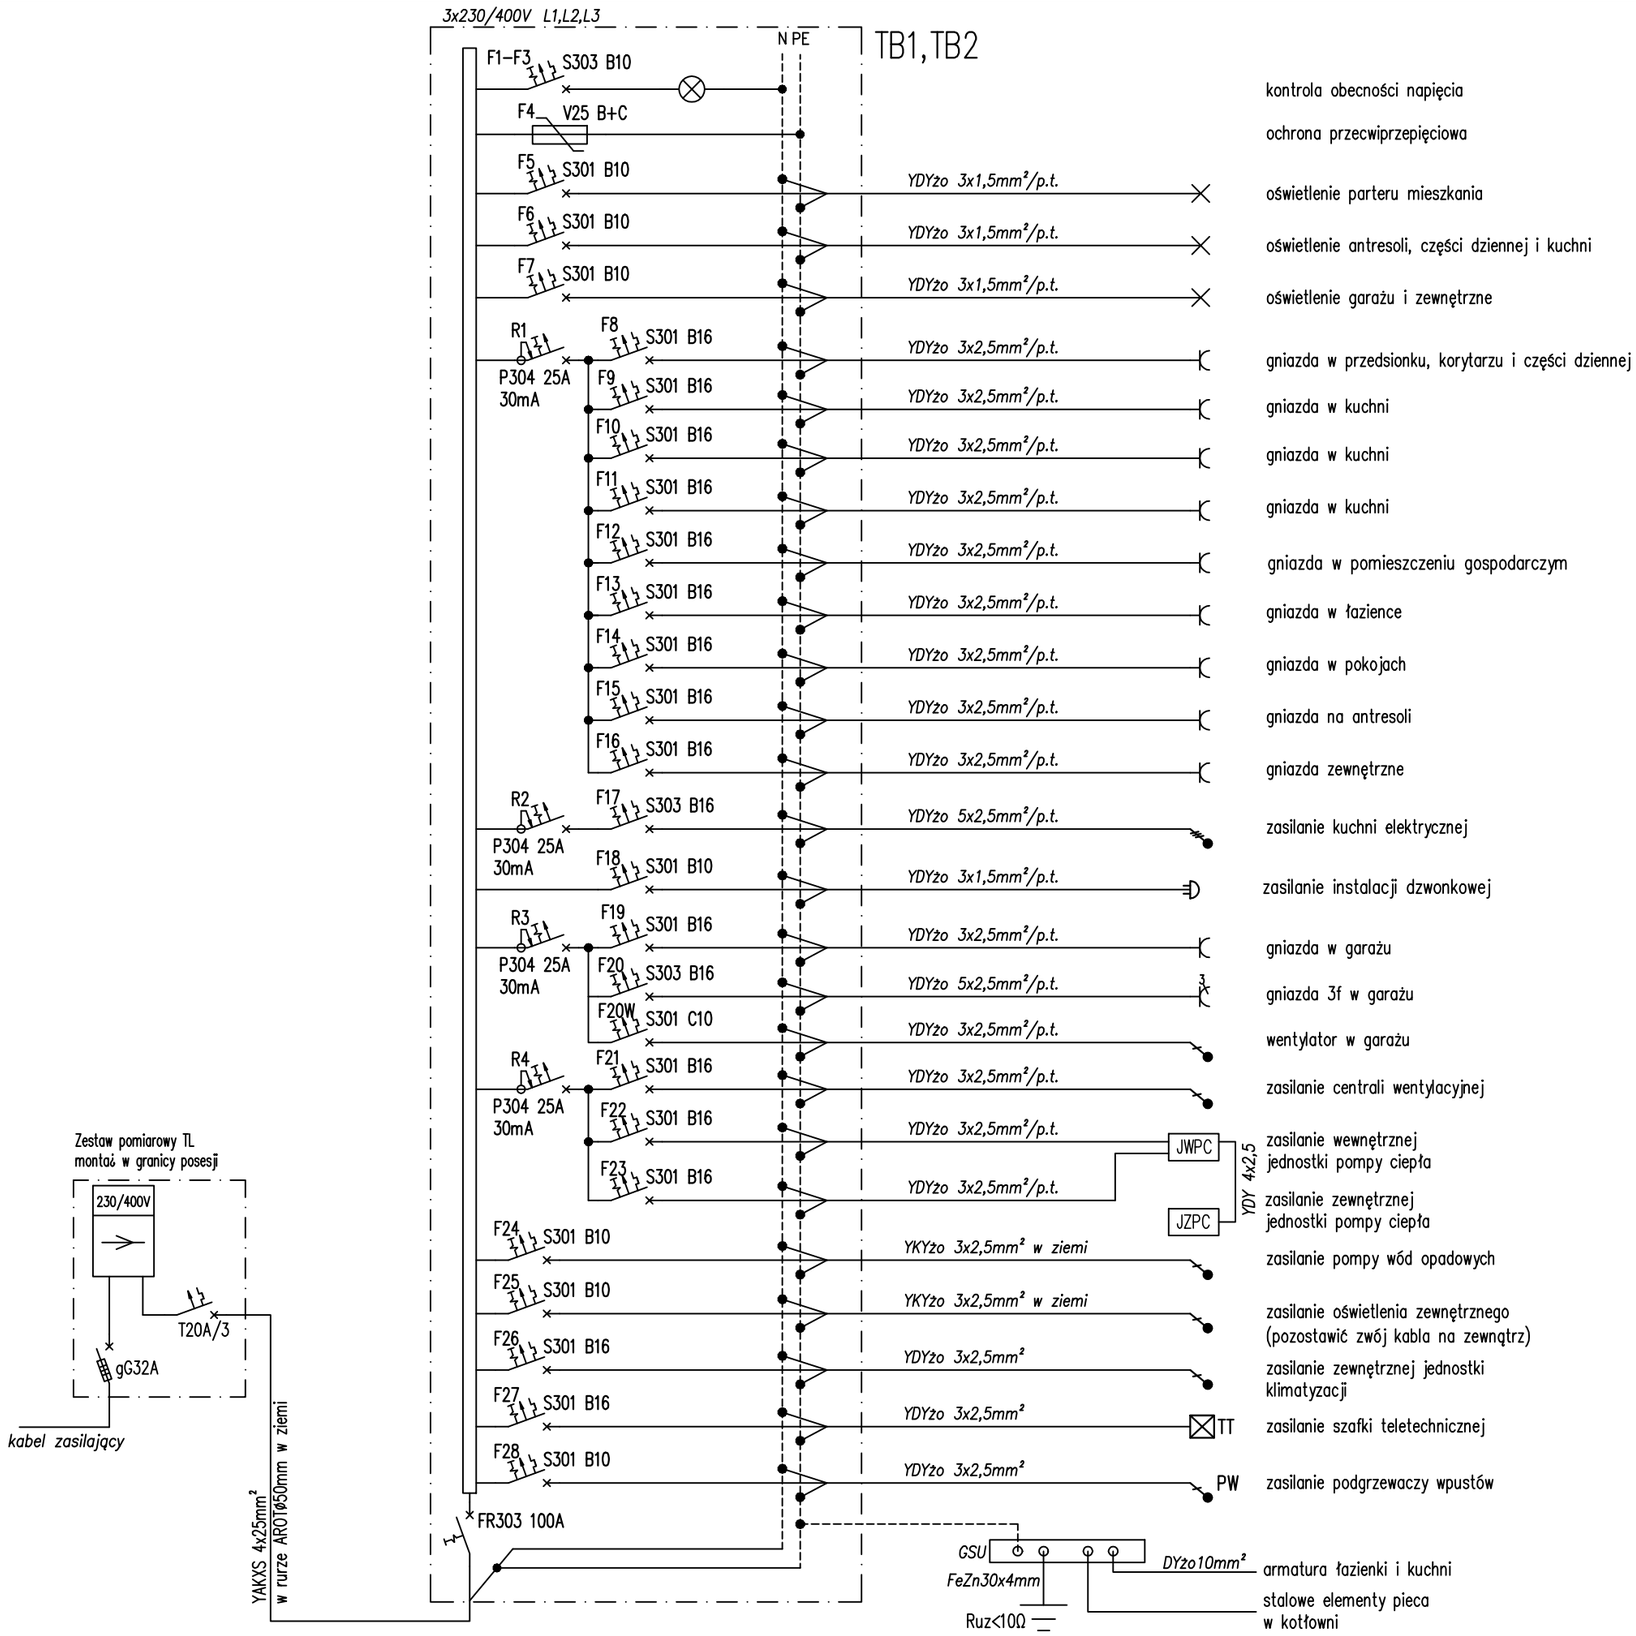



**NAZWA OBIEKTU BUDOWLANEGO**

**BUDOWA 28 BUDYNKÓW MIESZKALNYCH JEDNORODZINNYCH W ZABUDOWIE BLIŹNIACZEJ Z 14 GARAŻAMI ZAMKNIĘTYMI, WBUDOWANYMI ORAZ 14 GARAŻY ZAMKNIĘTYCH, WOLNOSTOJĄCYCH, Z ZAGOSPODAROWANIEM TERENU, SCHODAMI ZEWNĘTRZNYMI, MURAMI OPOROWYMI, ZEWNĘTRZNYMI STANOWISKAMI POSTOJOWYMI, DOJŚCIEM I DOJAZDEM.**

| PROJEKTANT | NR UPRAWNIEŃ |
|---|---|
| PAWEŁ PAWŁOWSKI | SWK/PWOE/0099/12 |

TYTUŁ RYSUNKU

**SCHEMAT INSTALACJI ELEKTRYCZNEJ - TB1, TB2. BUDYNEK B I C**

| ELEMENT PROJEKTU | NUMER RYSUNKU |
|---|---|
| PROJEKT TECHNICZNY | E13 |
| BRANŻA: ELEKTRYCZNA | |
| DATA: 01.2023 | SKALA: 1:100 |