


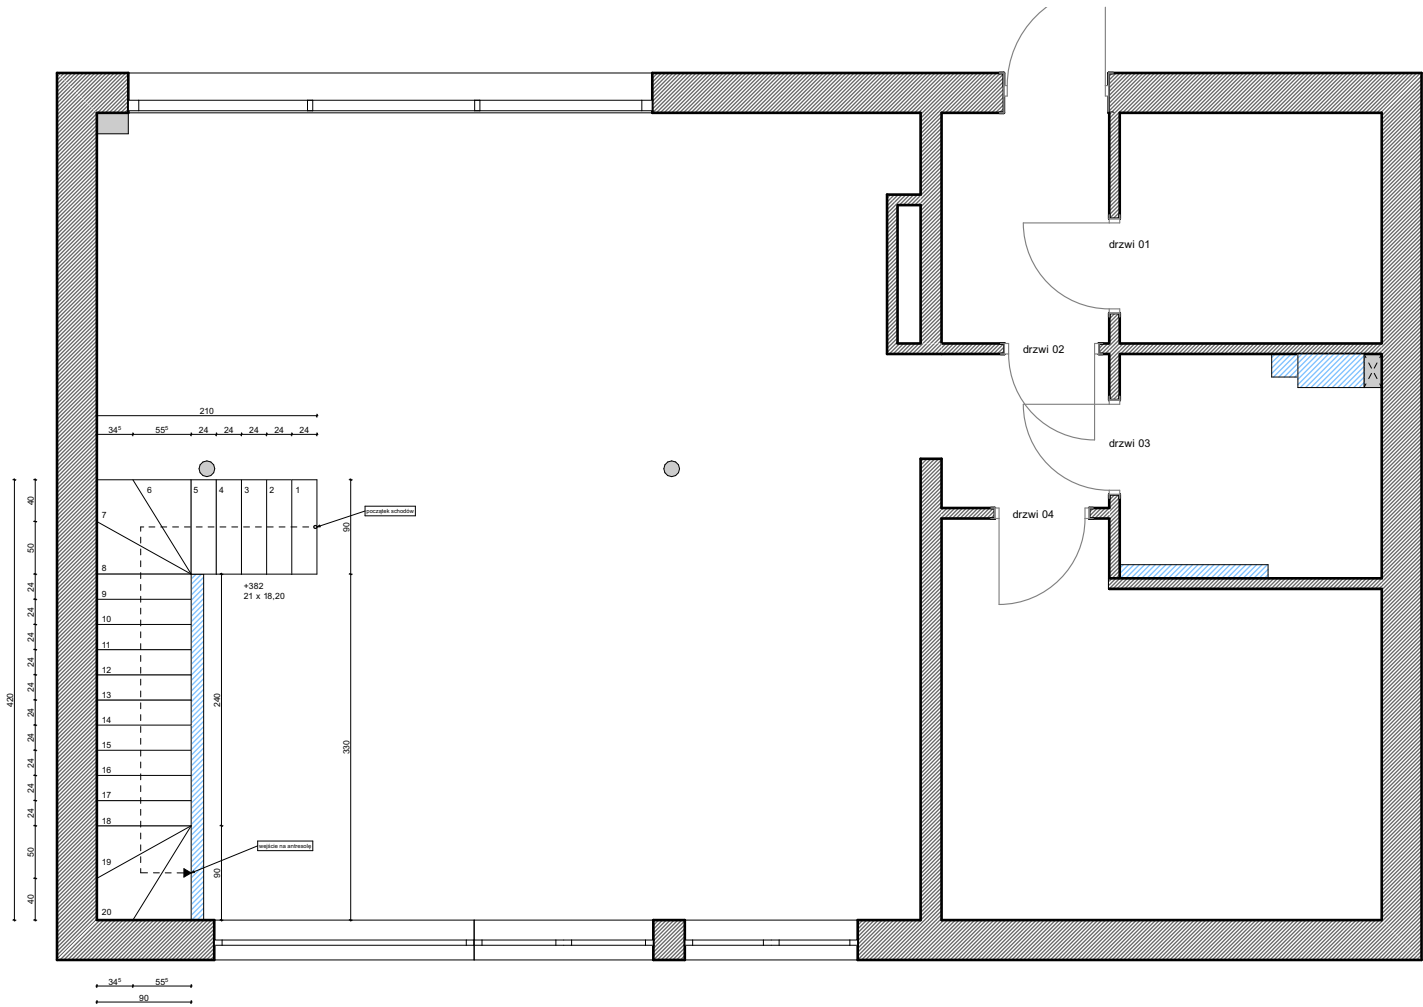

SPECYFIKACJA:

RÓŻNICA POZIOMÓW: 382 CM
PROJEKTOWANA LICZBA PODNIESIEŃ: 21 SZT.
WYSOKOŚĆ PODNIESIENIA: OK. 18,20 CM
OSTATECZNĄ GEOMETRIĘ SCHODÓW ZWERYFIKOWAĆ PRZEZ WYKONAWCĘ / KONSTRUKTORA

założenia projektowe:


- Wysokość od poziomu wykonanej posadzki parteru do poziomu wykonanej posadzki antresoli: 382 cm.
- Początek biegu schodów znajduje się w środkowej części pomieszczenia; wejście na antresolę przy oknie.
- Liczba stopni, wysokość podstopnic i głębokość stopni należy dostosować do ostatecznej długości biegu i zweryfikować przez wykonawcę schodów / konstruktora.
- Dolne stopnie projektowane jako kubikowa zabudowa meblowa, zintegrowana wizualnie ze schodami, z frontami meblowymi.
- Pod biegiem schodów przewidziana nisza / otwór w zabudowie przeznaczony na legowisko dla dużego psa. Lokalizację i wielkość otworu dostosować do przebiegu konstrukcji schodów oraz wymaganej wysokości użytkowej niszy.
- Stopnie wykonane drewnem / materiałem drewnopodobnym zgodnie z projektem materiałowym.
- Od strony ściany przewidziana poręcz ścienna, docelowo możliwość wykonania jako pochwytyt wpuszczony w płaszczyznę ściany.
- Na poziomie antresoli przewidziana pełna ściana pełniąca funkcję balustrady, h pełna wysokość pomieszczenia.
- Konstrukcja schodów: stalowa, niezależna od ściany zewnętrznej budynku.
- Schody nie mogą być konstrukcyjnie mocowane ani podwieszane do ściany zewnętrznej budynku.
- Podparcie / mocowanie konstrukcji przewidzieć do elementów konstrukcyjnych przygotowanych i ukrytych w zabudowie z płyt g-k oraz do elementów konstrukcyjnych budynku w miejscach dopuszczonych przez konstruktora.
- Projekt konstrukcyjny, dobór profilu stalowych, sposób kotwienia, połączenia oraz wymiarowanie konstrukcji po stronie konstruktora / wykonawcy schodów.
- Wszystkie wymiary należy zweryfikować na budowie przed wykonaniem konstrukcji i zabudowy stolarskiej

zabudowa g-k

ściana g-k wysokość h=110 cm

dodatkowy strop

DETALE STOPNIA I PORĘCZY:

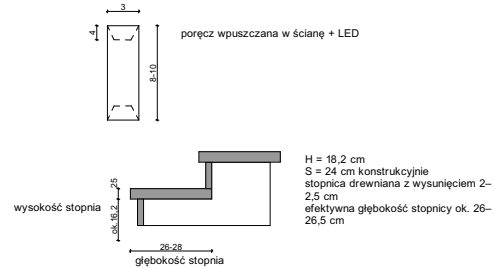

INWESTYCJA:	mieszkanie EKR	
PRACOWNIA:	ANNA KRZAK STUDIO	
INWESTORKA:	Ewa i Kuba Różyczcy	
NAZWA RYSUNKU:		
OPRACOWANIE:	ANNA KRZAK	
DATA:	SKALA:	NR RYS.:

WSZYSTKIE WYMIARY PODANE OD POZIOMU GOTOWEJ PODŁOGI
UWAGA! WSZYSTKIE WYMIARY DO WERYFIKACJI NA BUDOWIE