


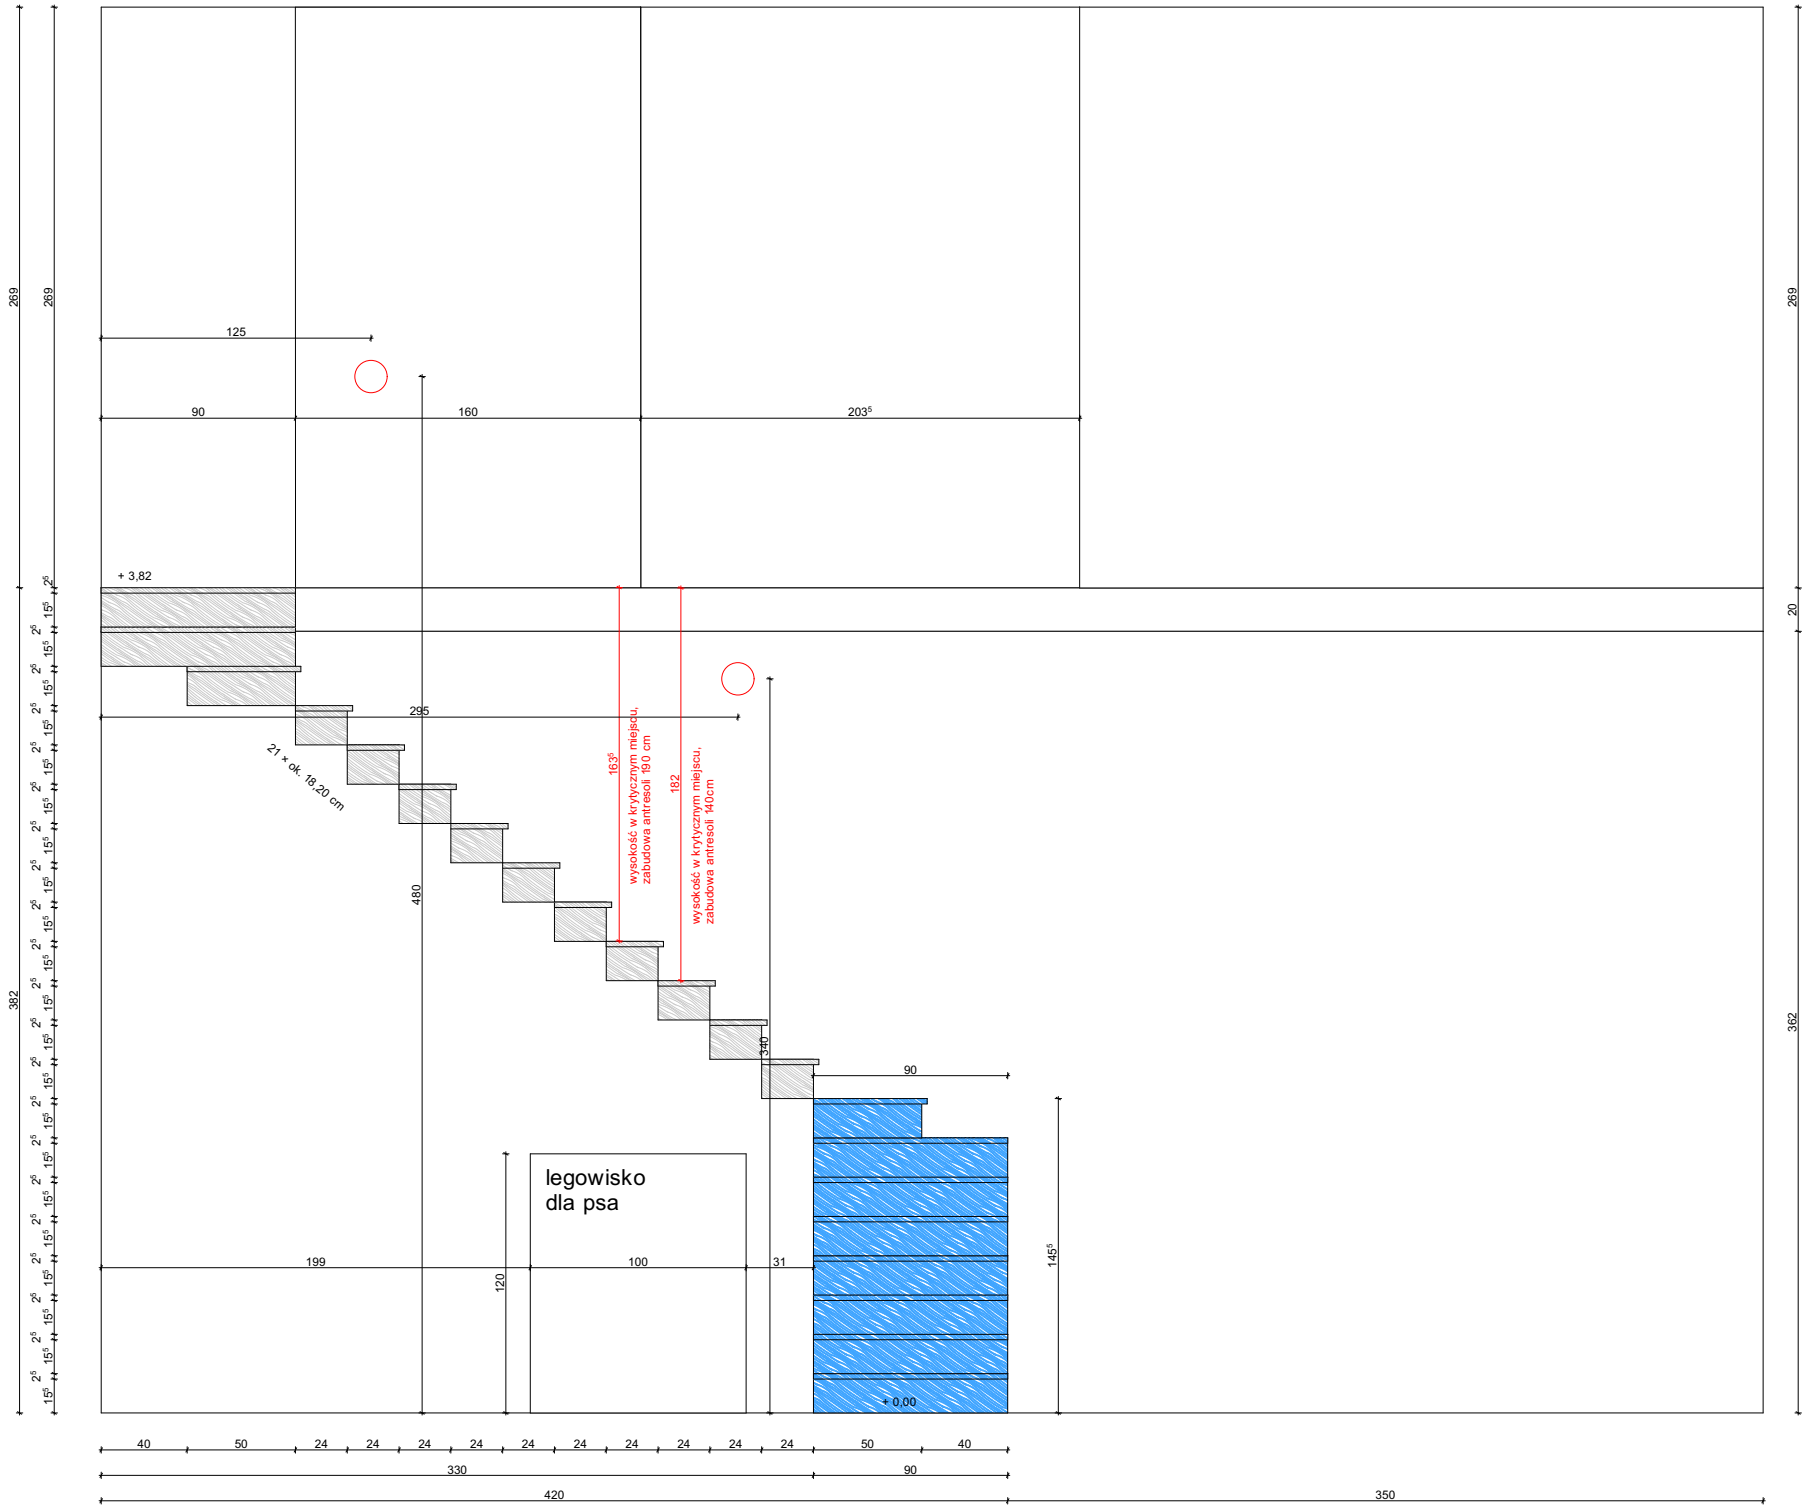

SPECYFIKACJA:

±0,00 — gotowa posadzka parteru,
+3,82 — gotowa posadzka antresoli,
21 podniesień x ok. 18,20 cm,
głębokość konstrukcyjna stopnia 24 cm,
stopnica drewniana z wysunięciem 2–2,5 cm,
efektywna głębokość ok. 26–26,5 cm,
ściana pełna G-K do sufitu,
pochwyt wpuszczany w ścianę + LED,
konstrukcja stalowa niezależna od ściany zewnętrznej,
dolne stopnie jako zabudowa meblowa, zaznaczone na niebiesko
nisza dla psa, do weryfikacji czy jej ostateczny wymiar zależy od konstrukcji schodów
konstrukcja stalowa samonośna / niezależna od ściany zewnętrznej;
profile, kotwienie i połączenia wg projektu konstruktora/wykonawcy schodów

wszystkie wymiary do weryfikacji na budowie

INWESTYCJA:	mieszkanie EKR	
PRACOWNIA:	ANNA KRZAK STUDIO	
INWESTORKA:	Ewa i Kuba Różyczcy	
NAZWA RYSUNKU:		
OPRACOWANIE:	ANNA KRZAK	
DATA:	SKALA:	NR RYS.:

WSZYSTKIE WYMIARY PODANE OD POZIOMU GOTOWEJ PODŁOGI
UWAGA! WSZYSTKIE WYMIARY DO WERYFIKACJI NA BUDOWIE